


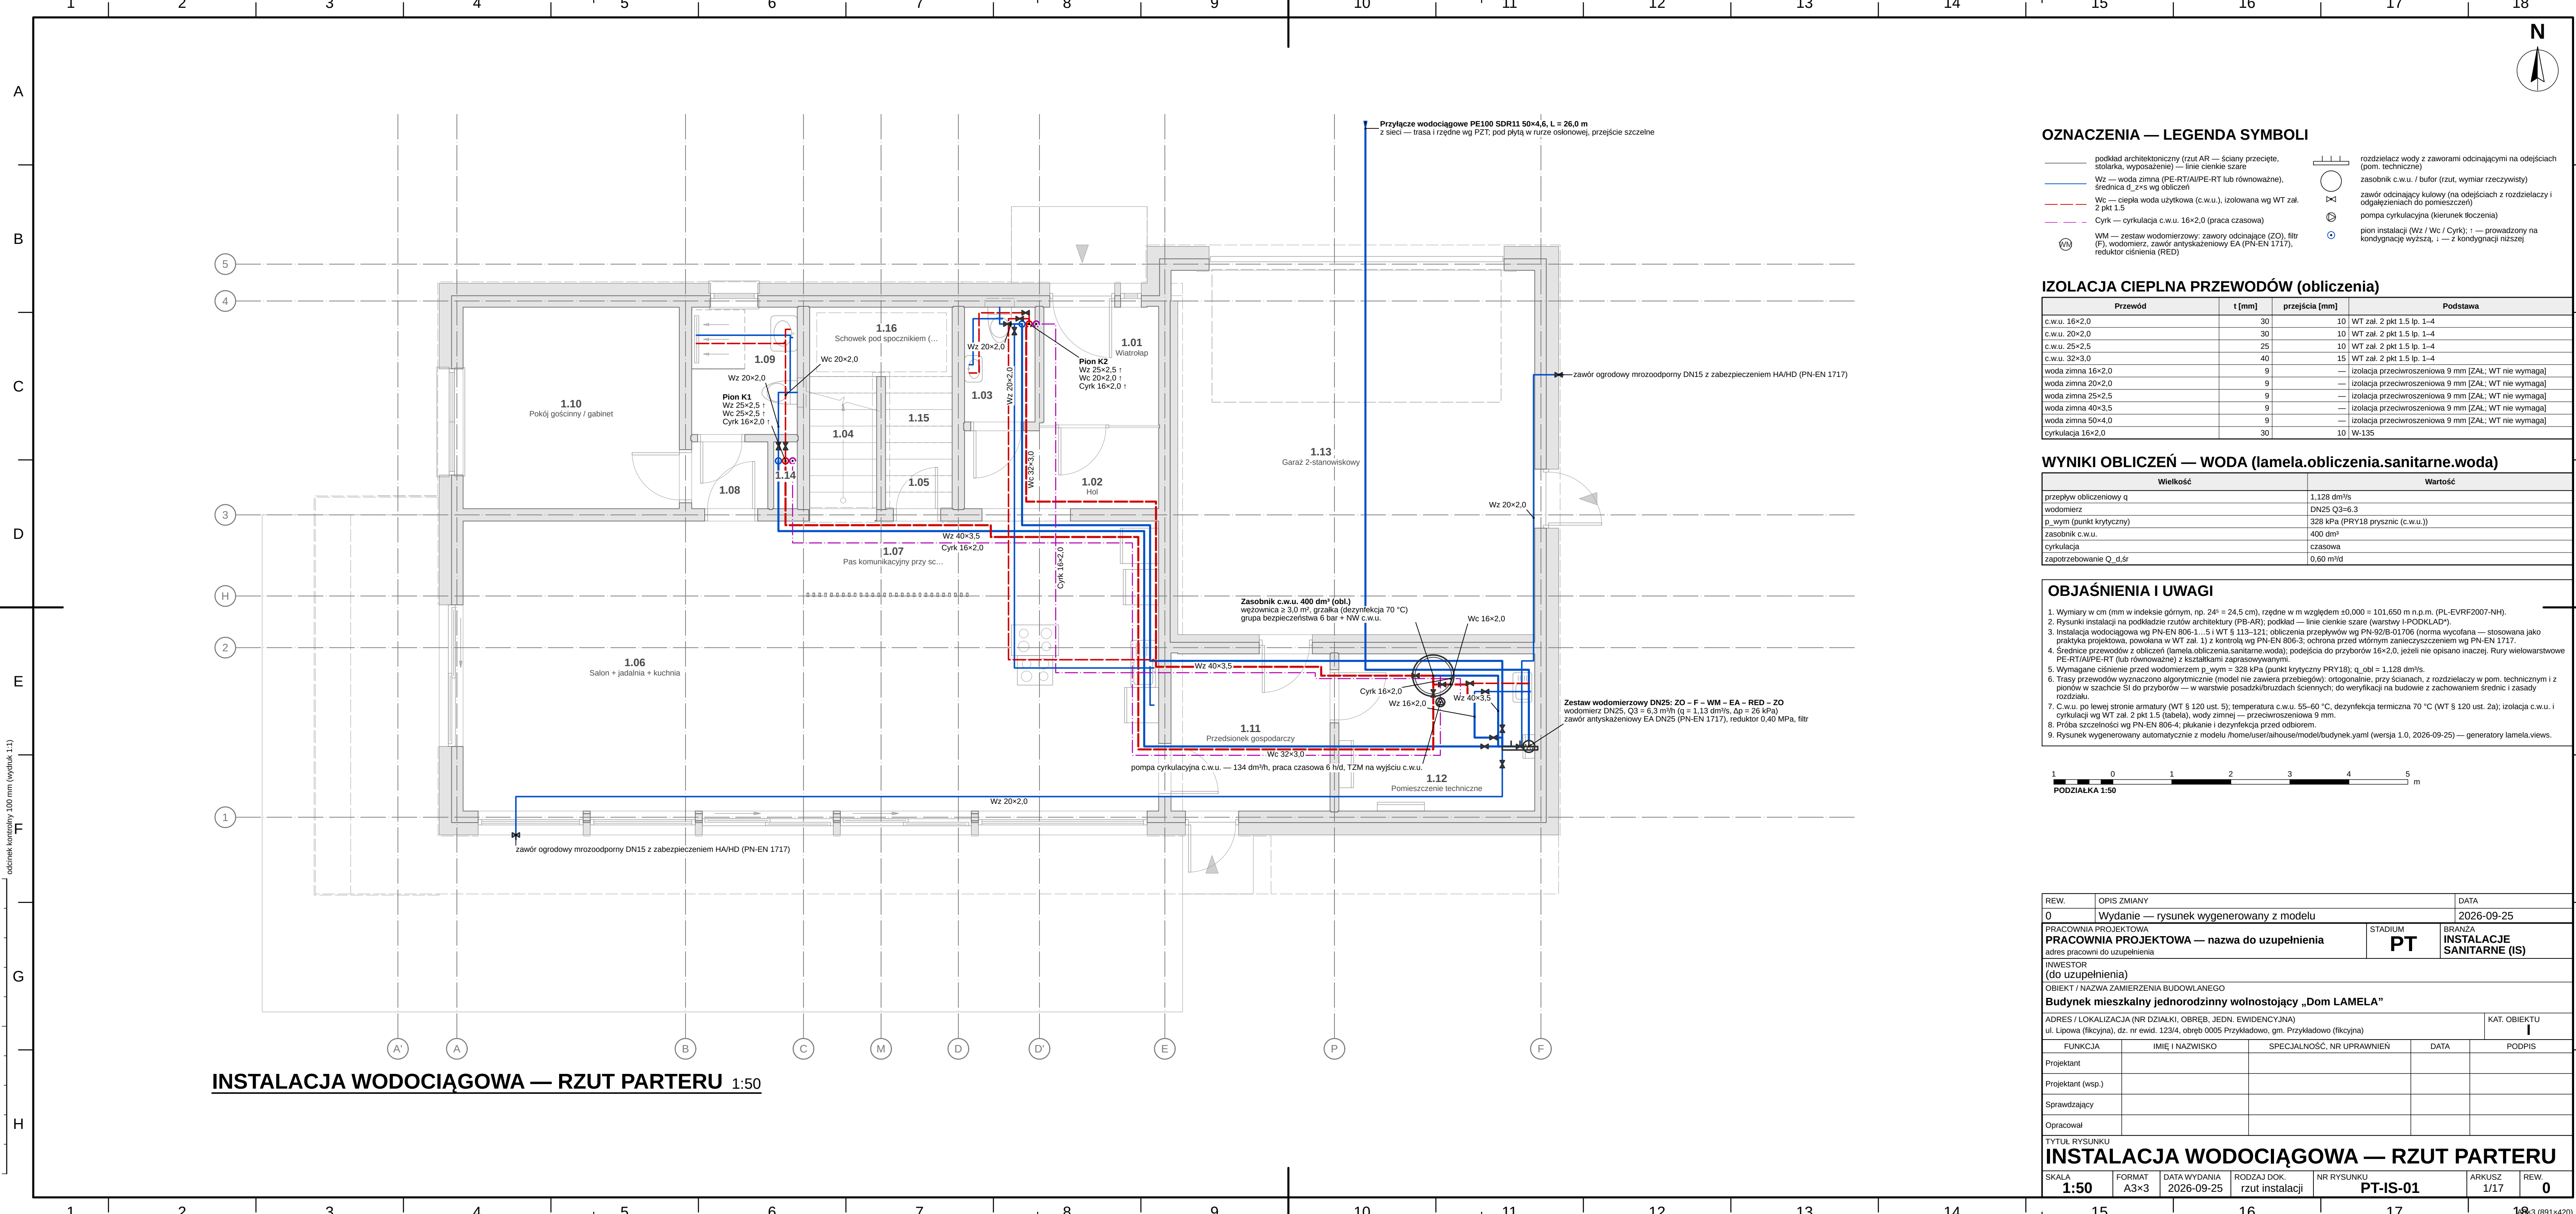

INSTALACJA WODOCIĄGOWA — RZUT PARTERU 1:50

OZNACZENIA — LEGENDA SYMBOLI

	podkład architektoniczny (rzut AR — ściany przecięte, stolarka, wyposażenie) — linie cienkie szare		rozdzielacz wody z zaworami odcinającymi na odcieczach (pom. techniczne)
	Wz — woda zimna (PE-RT/Al/PE-RT lub równoważne), średnica d_z x s wg obliczeń		zasobnik c.w.u. / bufor (rzut, wymiar rzeczywisty)
	Wc — ciepła woda użytkowa (c.w.u.), izolowana wg WT zał. 2 pkt 1.5		zawór odcinający kulowy (na odcieczach z rozdzielaczy i odgałęzieniach do pomieszczeń)
	Cyrk — cyrkulacja c.w.u. 16x2,0 (praca czasowa)		zawór odcinający kulowy (na odcieczach z rozdzielaczy i odgałęzieniach do pomieszczeń)
	WM — zestaw wodomierzowy: zawory odcinające (ZO), filtr (F), wodomierz, zawór antyskażeniowy EA (PN-EN 1717), reduktor ciśnienia (RED)		pompa cyrkulacyjna (kierunek tłoczenia)
			pion instalacji (Wz / Wc / Cyrk); 1 — prowadzony na kondygnację wyższą, i — z kondygnacji niższej

IZOLACJA CIEPLNA PRZEWODÓW (obliczenia)


Przewód	t [mm]	przejścia [mm]	Podstawa
c.w.u. 16x2,0	30	10	WT zał. 2 pkt 1.5 lp. 1–4
c.w.u. 20x2,0	30	10	WT zał. 2 pkt 1.5 lp. 1–4
c.w.u. 25x2,5	25	10	WT zał. 2 pkt 1.5 lp. 1–4
c.w.u. 32x3,0	40	15	WT zał. 2 pkt 1.5 lp. 1–4
woda zimna 16x2,0	9	—	izolacja przeciwwoszeniowa 9 mm [ZAL; WT nie wymaga]
woda zimna 20x2,0	9	—	izolacja przeciwwoszeniowa 9 mm [ZAL; WT nie wymaga]
woda zimna 25x2,5	9	—	izolacja przeciwwoszeniowa 9 mm [ZAL; WT nie wymaga]
woda zimna 40x3,5	9	—	izolacja przeciwwoszeniowa 9 mm [ZAL; WT nie wymaga]
woda zimna 50x4,0	9	—	izolacja przeciwwoszeniowa 9 mm [ZAL; WT nie wymaga]
cyrkulacja 16x2,0	30	10	W-135

WYNIKI OBLICZEŃ — WODA (lamela.obliczenia.sanitarne.woda)

Wielkość	Wartość
przepływ obliczeniowy q	1,128 dm³/s
wodomierz	DN25 Q3=6.3
p_wym (punkt krytyczny)	328 kPa (PRY18 przysic (c.w.u.))
zasobnik c.w.u.	400 dm³
cyrkulacja	czasowa
zapotrzebowanie Q_d,śr	0,60 m³/d

OBJAŚNIENIA I UWAGI

- Wymiary w cm (mm w indeksie górnym, np. 24^o = 24,5 cm), rzędne w m względem ±0.000 = 101.650 m n.p.m. (PL-EVRF2007-NH).
- Rysunki instalacji na podkładzie rzutów architektury (PB-AR); podkład — linie cienkie szare (warstwy I-PODKŁAD).
- Instalacja wodociągowa wg PN-EN 806-1...5 i WT § 113–121; obliczenia przepływów wg PN-92/B-01.706 (norma wycofana — stosowana jako praktyka projektowa, powołana w WT zał. 1) z kontrolą wg PN-EN 806-3; ochrona przed wtórnym zanieczyszczeniem wg PN-EN 1717.
- Średnice przewodów z obliczeń (lamela.obliczenia.sanitarne.woda); podejścia do przyborów 16x2,0, jeżeli nie opisano inaczej. Rury wielowarstwowe PE-RT/Al/PE-RT (lub równoważne) z kształtkami zaprasowywanymi.
- Wymagane ciśnienie przed wodomierzem p_wym = 328 kPa (punkt krytyczny PRY18); q_obl = 1,128 dm³/s.
- Trasy przewodów wyznaczone algorytmicznie (model nie zawiera przebiegów): ortogonalnie, przy ścianach, z rozdzielaczem w pom. technicznym i z pionów w szachcie SI do przyborów — w warstwie posadzki/bruzdach ściennych; do weryfikacji na budowie z zachowaniem średnic i zasady rozdziálu.
- C.w.u. po lewej stronie armatury (WT § 120 ust. 5); temperatura c.w.u. 55–60 °C, dezynfekcja termiczna 70 °C (WT § 120 ust. 2a); izolacja c.w.u. i cyrkulacji wg WT zał. 2 pkt 1.5 (tabela), wody zimne — przeciwwoszeniowa 9 mm.
- Próba szczelności wg PN-EN 806-4; płukanie i dezynfekcja przed odbiorem.
- Rysunek wygenerowany automatycznie z modelu /home/user/aihouse/model/budynek.yaml (wersja 1.0, 2026-09-25) — generatory lamela.views.

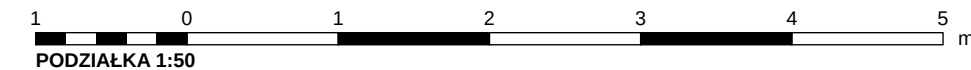

REW.	OPIS ZMIANY	DATA
0	Wydanie — rysunek wygenerowany z modelu	2026-09-25
PRACOWNIA PROJEKTOWA	PRACOWNIA PROJEKTOWA — nazwa do uzupełnienia	STADIUM
adres pracowni do uzupełnienia	PT	BRANŻA
INWESTOR	(do uzupełnienia)	INSTALACJE
OBIEKT / NAZWA ZAMIERZENIA BUDOWLANEGO	Budynek mieszkalny jednorodzinny wolnostojący „Dom LAMELA”	SANITARNE (IS)
ADRES / LOKALIZACJA (NR DZIAŁKI, OBRĘB, JEDN. EWIDENCYJNA)	ul. Lipowa (fikcyjna), dz. nr ewid. 123/4, obręb 0005 Przykładowo, gm. Przykładowo (fikcyjna)	KAT. OBIEKTU
FUNKCJA	IMIĘ I NAZWISKO	SPECJALNOŚĆ, NR UPRAWNIEN
Projektant		DATA
Projektant (wsp.)		PODPIS
Sprawdzający		
Opracował		
TYTUŁ RYSUNKU	INSTALACJA WODOCIĄGOWA — RZUT PARTERU	
SKALA	1:50	FORMAT
A3x3	DATA WYDANIA	2026-09-25
RODZAJ DOK.	rzut instalacji	NR RYSUNKU
PT-IS-01	ARKUSZ	1/17
REW.	0	