


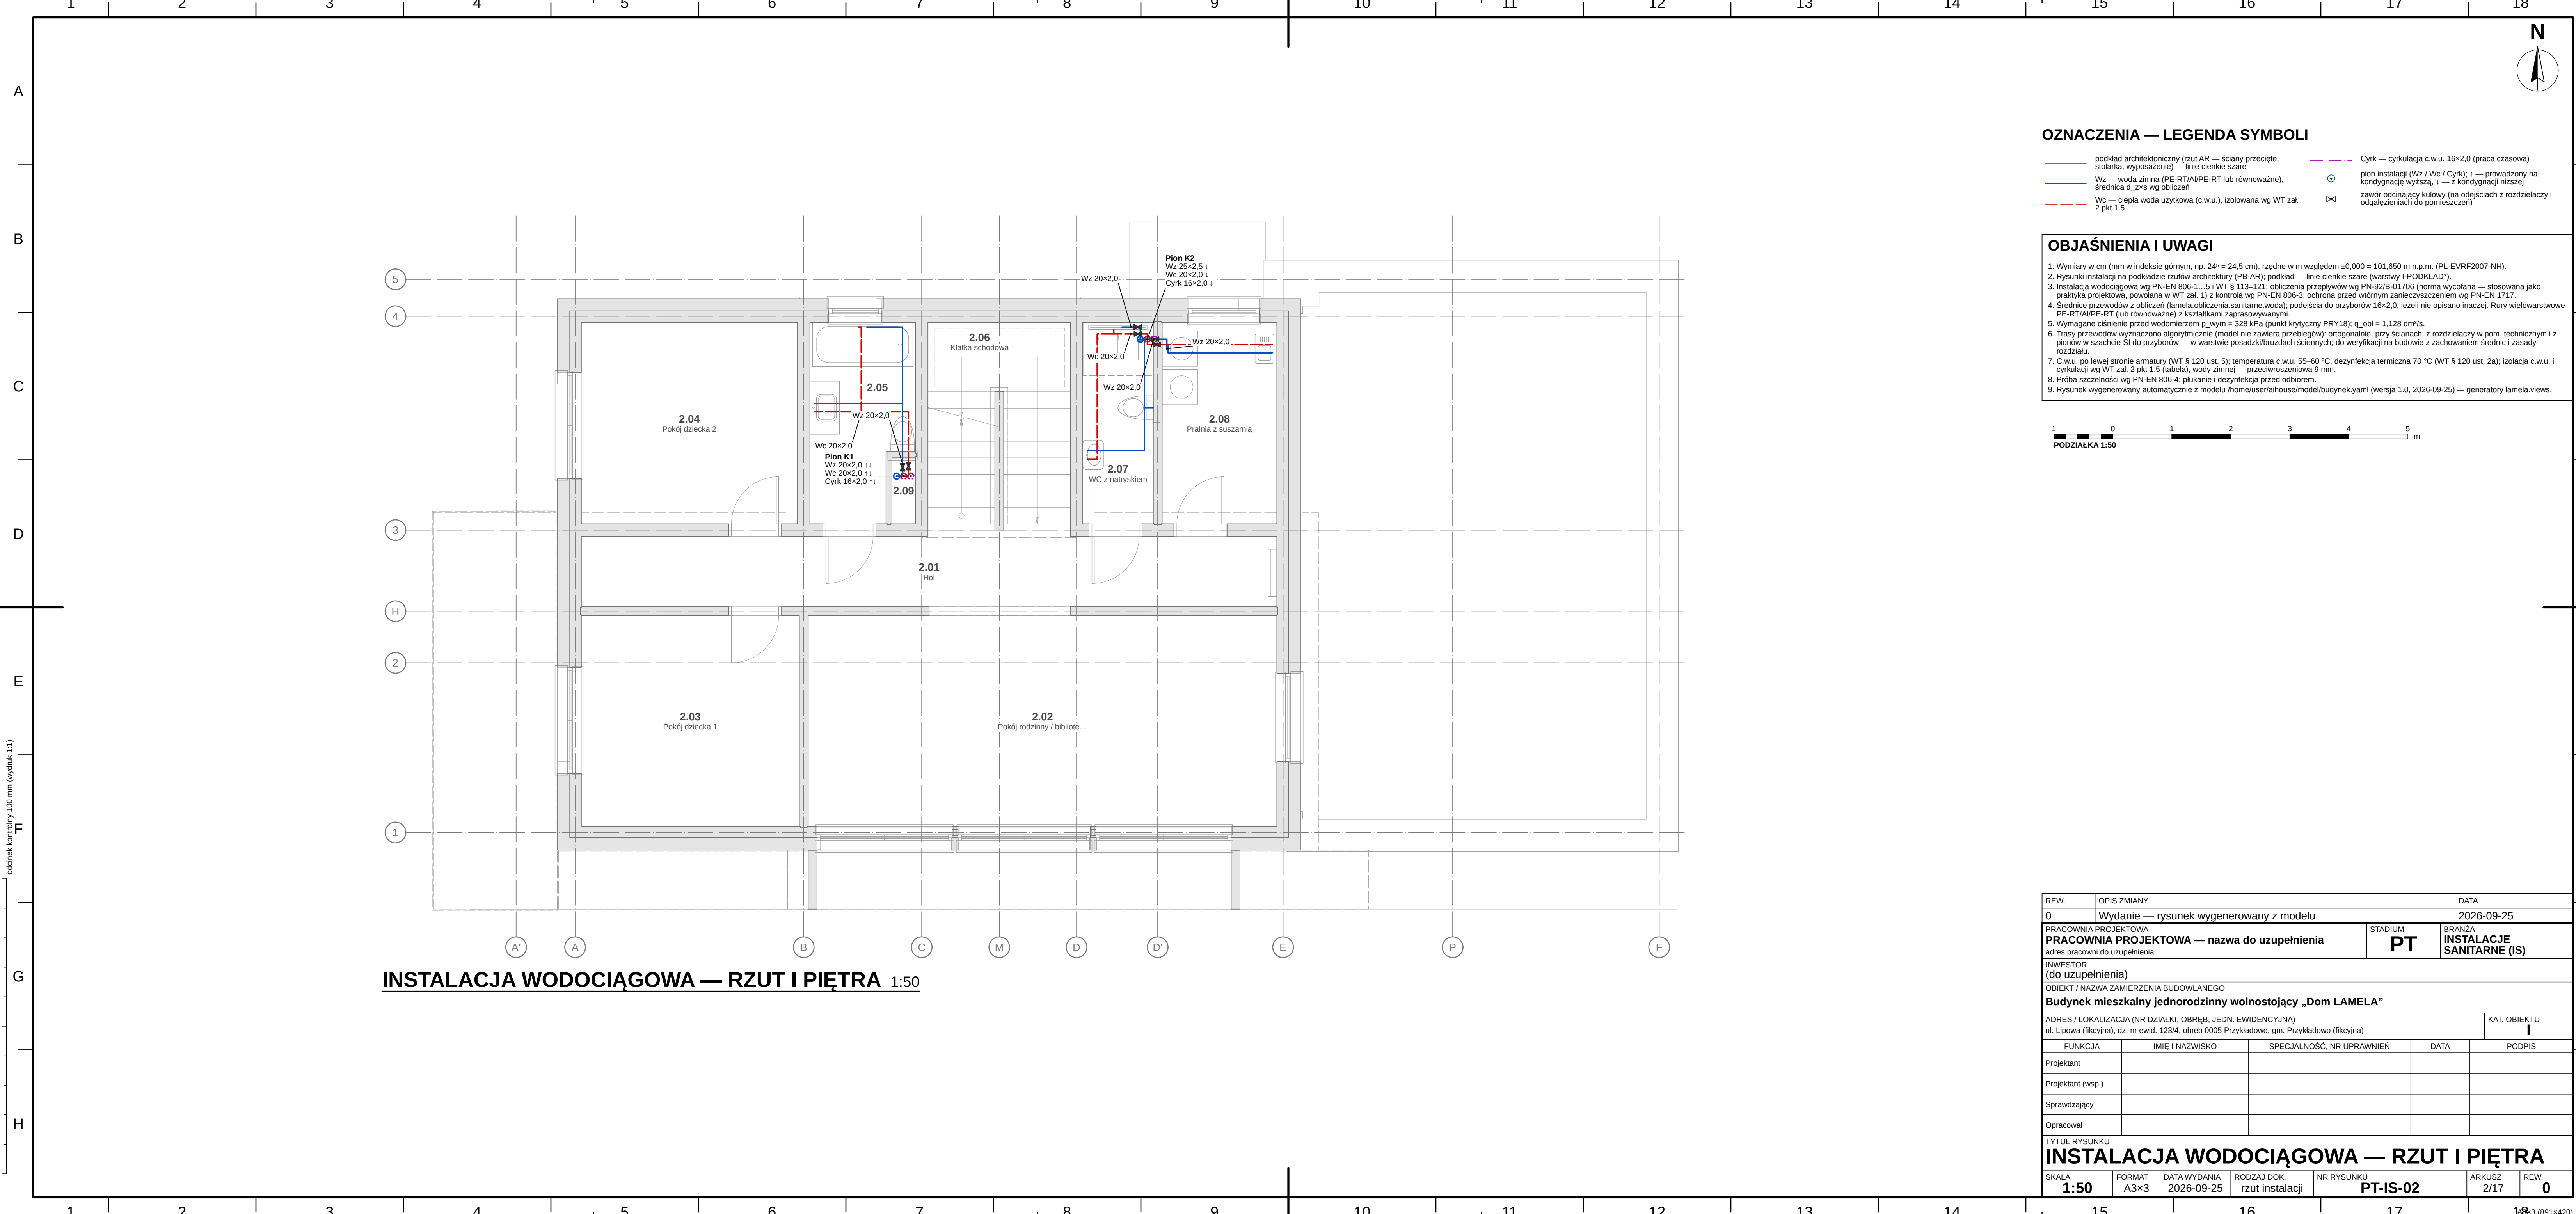

INSTALACJA WODOCIĄGOWA — RZUT I PIĘTRA 1:50

OZNACZENIA — LEGENDA SYMBOLI

- podkład architektoniczny (rzut AR — ściany przecięte, stolarka, wyposażenie) — linie cienkie szare
- Wz — woda zimna (PE-RT/Al/PE-RT lub równoważne), średnica d_z x s wg obliczeń
- Wc — ciepła woda użytkowa (c.w.u.), izolowana wg WT zał. 2 pkt 1.5
- Cyrk — cyrkulacja c.w.u. 16x2.0 (praca czasowa)
- ⊙ pion instalacji (Wz / Wc / Cyrk); 1 — prowadzony na kondygnację wyższą, i — z kondygnacji niższej
- ⋈ zawór odcinający kulowy (na odciskach z rozdzielaczy i odgałęzieniach do pomieszczeń)

OBJAŚNIENIA I UWAGI

- Wymiary w cm (mm w indeksie górnym, np. 24^ø = 24,5 cm), rzędne w m względem ±0,000 = 101,650 m n.p.m. (PL-EVRF2007-NH).
- Rysunki instalacji na podkładzie rzutów architektury (PB-AR); podkład — linie cienkie szare (warstwy I-PODKŁAD).
- Instalacja wodociągowa wg PN-EN 806-1...5 i WT § 113–121; obliczenia przepływów wg PN-92/B-01706 (norma wycofana — stosowana jako praktyka projektowa, powołana w WT zał. 1) z kontrolą wg PN-EN 806-3; ochrona przed wtórnym zanieczyszczeniem wg PN-EN 1717.
- Średnice przewodów z obliczeń (lamela obliczenia sanitarne woda); podejścia do przyborów 16x2.0, jeżeli nie opisano inaczej. Rury wielowarstwowe PE-RT/Al/PE-RT (lub równoważne) z kształtkami zaprasowywanymi.
- Wymagane ciśnienie przed wodomierzem p_wym = 328 kPa (punkt krytyczny PRY18); q_obl = 1,128 dm³/s.
- Trasy przewodów wyznaczono algorytmicznie (model nie zawiera przebiegów); ortogonalnie, przy ścianach, z rozdzielaczy w pom. technicznym i z pionów w szachcie SI do przyborów — w warstwie posadzki/bruzdach ściennych; do weryfikacji na budowie z zachowaniem średnic i zasady rozdziaku.
- C.w.u. po lewej stronie armatury (WT § 120 ust. 5); temperatura c.w.u. 55–60 °C, dezynfekcja termiczna 70 °C (WT § 120 ust. 2a); izolacja c.w.u. i cyrkulacji wg WT zał. 2 pkt 1.5 (tabela), wody zimnej — przeciwwrośnościowa 9 mm.
- Próba szczelności wg PN-EN 806-4; płukanie i dezynfekcja przed odbiorem.
- Rysunek wygenerowany automatycznie z modelu /home/user/aihouse/model/budynek.yaml (wersja 1.0, 2026-09-25) — generatory lamela.views.

1 0 1 2 3 4 5 m
PODZIAŁKA 1:50

REW.	OPIS ZMIANY			DATA	
0	Wydanie — rysunek wygenerowany z modelu			2026-09-25	
PRACOWNIA PROJEKTOWA PRACOWNIA PROJEKTOWA — nazwa do uzupełnienia adres pracowni do uzupełnienia			STADIUM PT	BRANŻA INSTALACJE SANITARNE (IS)	
INWESTOR (do uzupełnienia)					
OBIEKT / NAZWA ZAMIERZENIA BUDOWLANEGO					
Budynek mieszkalny jednorodzinny wolnostojący „Dom LAMELA”					
ADRES / LOKALIZACJA (NR DZIAŁKI, OBREB, JEDN. EWIDENCYJNA) ul. Lipowa (fikcyjna), dz. nr ewid. 123/4, obręb 0005 Przykładowo, gm. Przykładowo (fikcyjna)					KAT. OBIEKTU I
FUNKCJA	IMIĘ I NAZWISKO		SPECJALNOŚĆ, NR UPRAWNIENI	DATA	PODPIS
Projektant					
Projektant (wsp.)					
Sprawdzający					
Opracował					
TYTUŁ RYSUNKU					
INSTALACJA WODOCIĄGOWA — RZUT I PIĘTRA					
SKALA 1:50	FORMAT A3x3	DATA WYDANIA 2026-09-25	RODZAJ DOK. rzut instalacji	NR RYSUNKU PT-IS-02	ARKUSZ 2/17
					REW. 0