



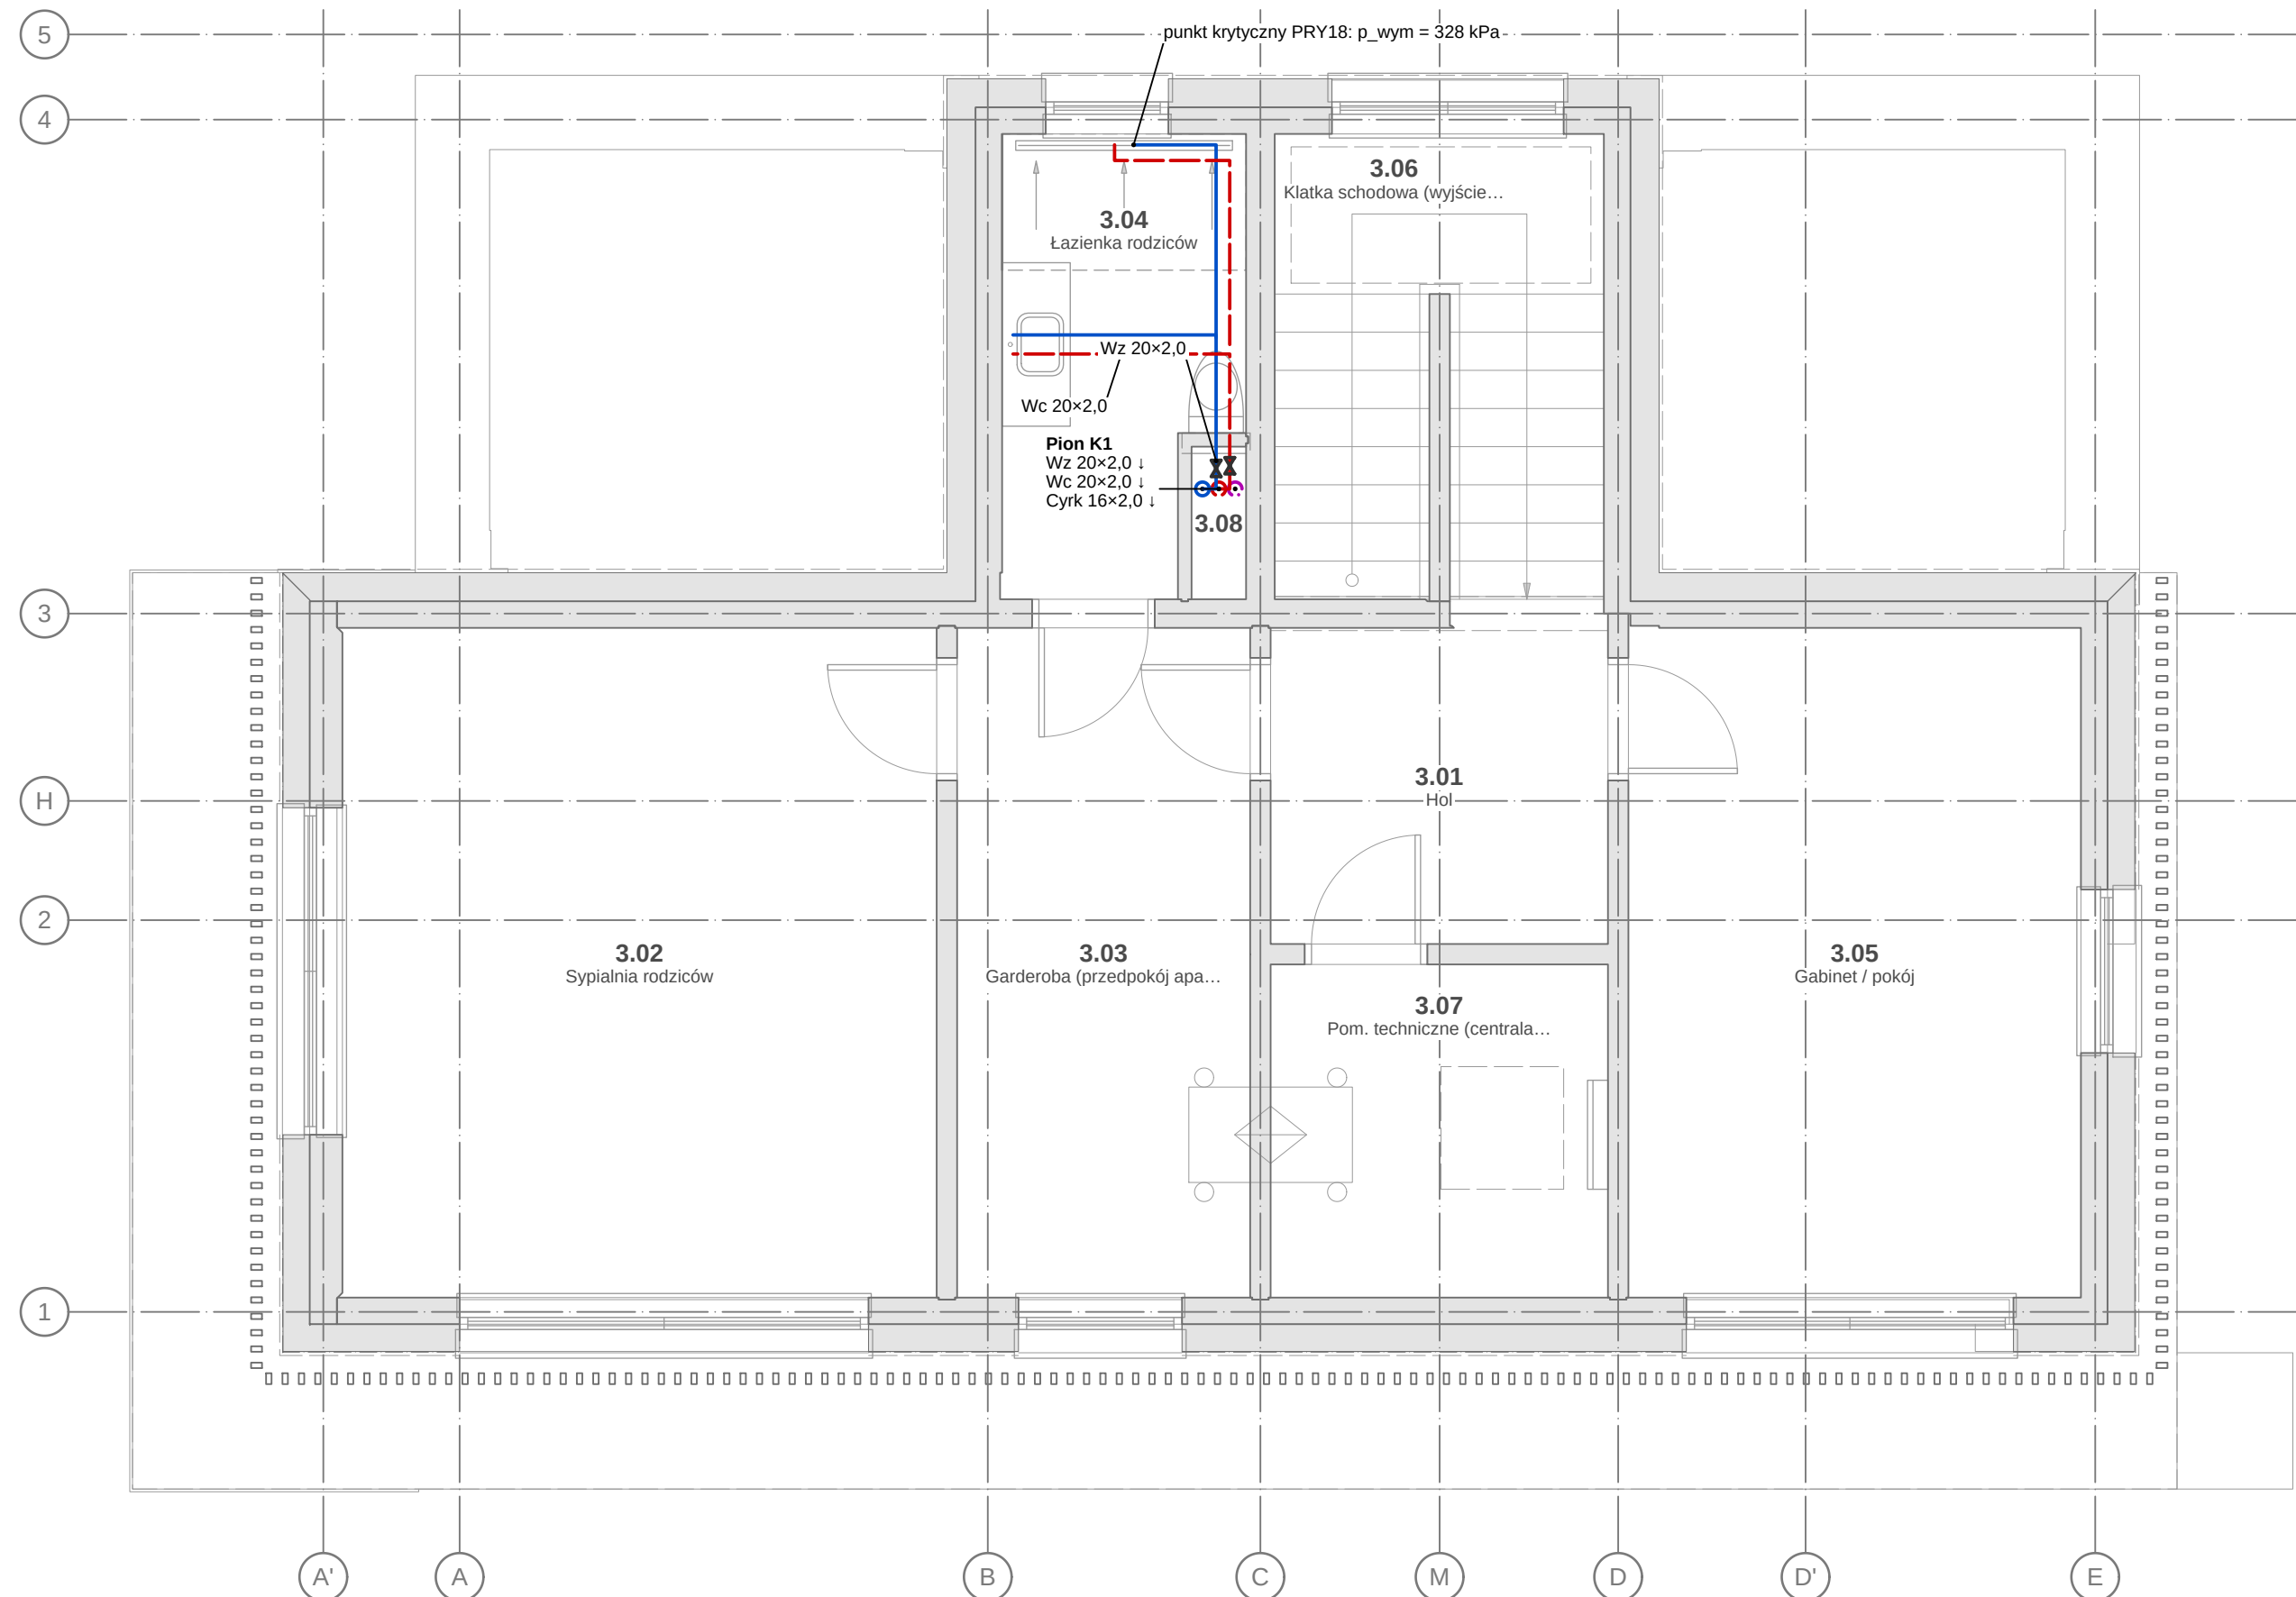

INSTALACJA WODOCIĄGOWA — RZUT II PIĘTRA 1:50

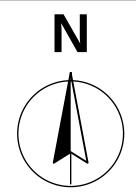


OZNACZENIA — LEGENDA SYMBOLI

-----	podłak architektoniczny (rzut AR) – ściany przecięcie, stolarka, wyposażenie) – linie cienie szare	-----	Cyrk – cyrkulacja c.w.u. 16x20 (praca czasowa)
-----	Wz – woda zimna (PE-RT/AlPE-RT lub równoważne), średnica d _z wg obliczeń	-----	pion instalacji (Wz / Wc / Iry) – prowadzony na kondygnację wyższą, z / w kondygnacji niższej
-----	Wz – ciepła woda użytkowa (c.w.u.), izolowana wg WT zał. 2 pkt 1.5	-----	zawór odcinający kulowy (na odcięciach z rozdzielaczy i odgórników do pomieszczeń)

OBJAŚNIENIA I UWAGI

- Wymiary w cm (mm w niektórych górnym, np. 24" = 24,5 cm), rzekąd w m względem 0+000 = 101,650 m np.m. (PL-EVRF2007-NH).
- Rysunki instalacji na podkładzie rzutu architektury (PB-AR); rzekąd – linie cieniarskie szare (warstwy I+PODKŁAD).
- Instalacja wodociągowa wg PN-EN 806-1. 5 IT wg 113–112; obciążenia przepływów wg PN-92/B-01706 (norma wycofana – stosowana jako praktyka projektowa, powołana w WT 1. 2) i kontrola wg PN-806-3; ochrona przed wymorzeniem zanieczyszczeniem wg PN-91/17. 4.
- Ścieki przewodów – obciążenia (faktora obciążenia) wg PN-91/17. 4; podjęcia do przyborów 16/20, jeżeli nie opisano inaczej. Rury wielowarstwowe PE-RTA/PE-RT lub (równoważne) z kształtkami zaprasowywanymi.
- Wymagane ciśnienie przed wodomierzem $p_{wm} = 328 \text{ kPa}$ (punkt krytyczny PRY18); $q_{bl} = 1,128 \text{ dm}^3/\text{s}$.
- Trasy przewodów wyznaczono algorytmicznie (model nie zawiera przebiegów); ortogonalnie, przy szcianach, z rozdzielaczami w pom. technicznym i z pionów w szachcie S1 do przyborów – w warstwie posadzki/burzących ściennych; do weryfikacji na budowie z zachowaniem średni i czasami rozdzielu.
- C.w. w lewej stronie armatury WT § 120 ust. 5); temperatura c.w. 55–60 °C, definitywna temperatura 70 °C (WT § 120 ust. 2a); izolacja c.w.u. i cyrkulacji wg WT 2. 2 pkt 15 (tabela), wody zimnej – przewieszczeniowa 9 mm.
- Próba szczelności wg PN-EN 806-4; pukanie i defektyzacja przed odbiorem.
- Rysunek wygenerowany automatycznie z modelu `home/user/ahouse/home/model/budynek.yaml` (wersja 1.0, 2020-09-25) – generatory lamela views.

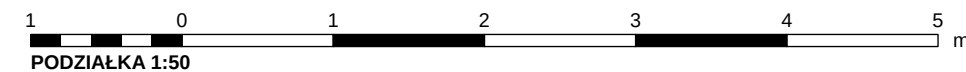

REW.	OPIS ZMIANY				DATA
0	Wydanie — rysunek wygenerowany z modelu				2026-09-25
PRACOWNIA PROJEKTOWA PRACOWNIA PROJEKTOWA — nazwa do uzupełnienia adres pracowni do uzupełnienia			STADIUM PT	BRANŻA INSTALACJE SANITARNE (IS)	
INWESTOR (do uzupełnienia)					
OBIEKT / NAZWA ZAMIERZENIA BUDOWLANEGO					
Budynek mieszkalny jednorodzinny wolnostojący „Dom LAMELA”					
ADRES / LOKALIZACJA (NR DZIAŁKI, OBRĘB, JEDN. EWIDENCYJNA) ul. Lipowa (fikcyjna), dz. nr ewid. 123/4, obręb 0005 Przykładowo, gm. Przykładowo (fikcyjna)					KAT. OBIEKTU I
FUNKCJA	IMIĘ I NAZWISKO		SPECJALNOŚĆ, NR UPRAWNIENI	DATA	PODPIS
Projektant					
Projektant (wsp.)					
Sprawdzający					
Opracował					
TYTUŁ RYSUNKU					
INSTALACJA WODOCIĄGOWA — RZUT II PIĘTRA					
SKALA 1:50	FORMAT A3×3	DATA WYDANIA 2026-09-25	RODZAJ DOK. rzut instalacji	NR RYSUNKU PT-IS-03	ARKUSZ 3/17
					REW. 0