


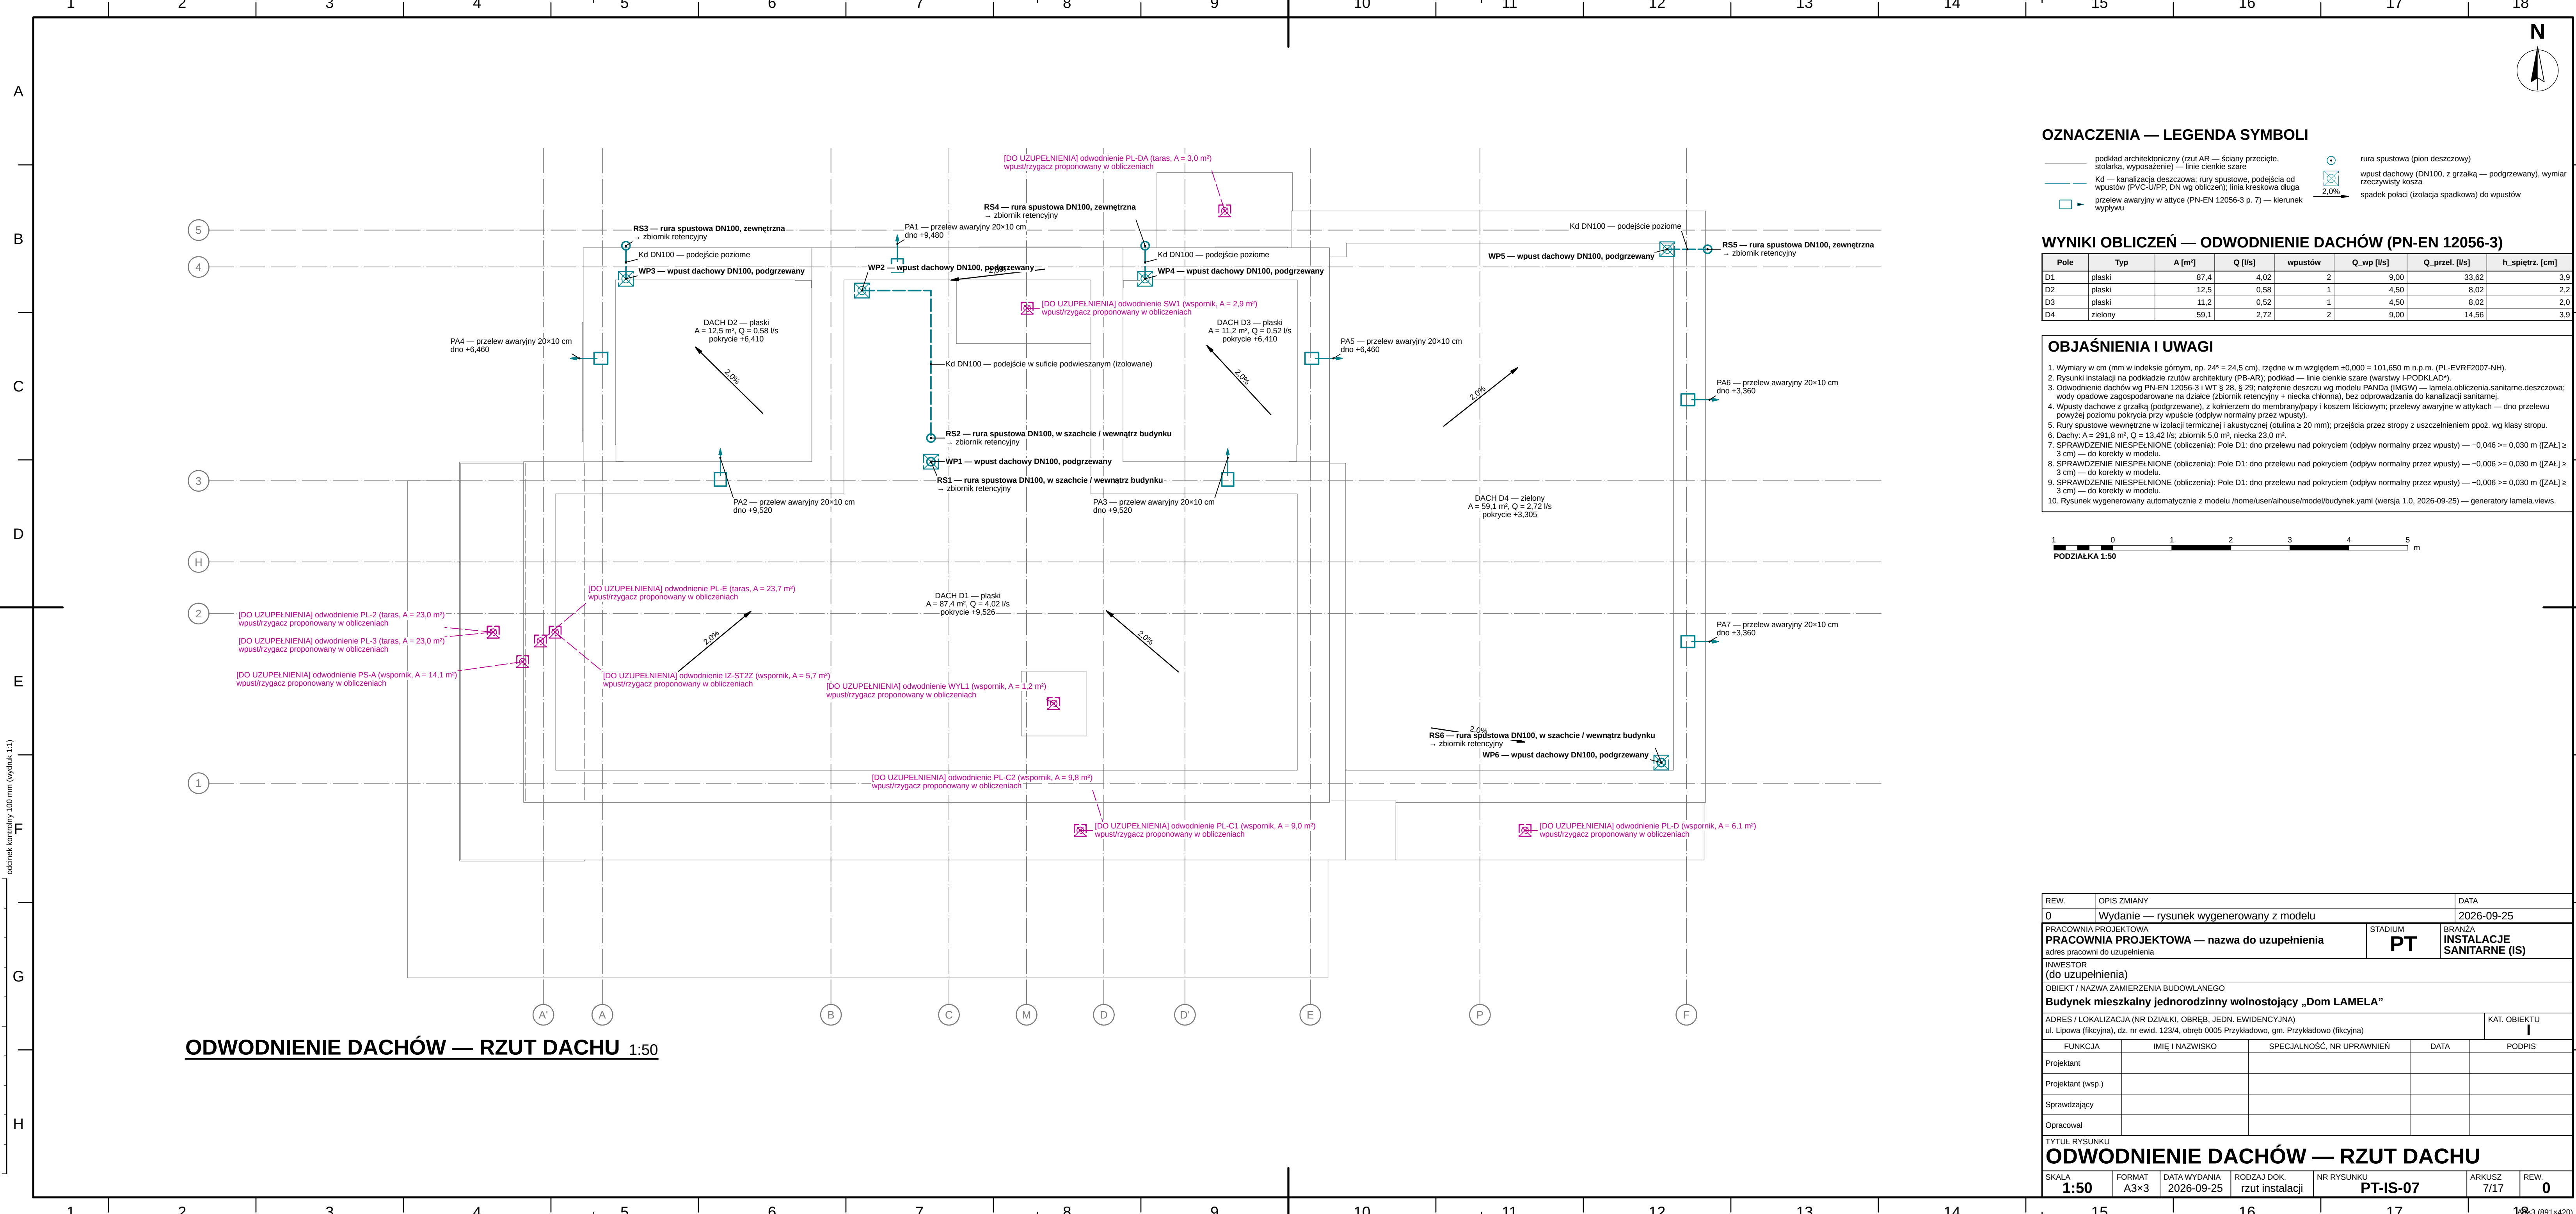

OZNACZENIA — LEGENDA SYMBOLI


	podkład architektoniczny (rzut AR — ściany przecięte, stolarka, wyposażenie) — linie cienkie szare		rura spustowa (pion deszczowy)
	Kd — kanalizacja deszczowa: rury spustowe, podejścia od wpustów (PVC-U/PP, DN wg obliczeń), linia kreskowa długa		wpust dachowy (DN100, z grzałką — podgrzewany), wymiar rzeczywisty kosza
	przelew awaryjny w attyce (PN-EN 12056-3 p. 7) — kierunek wypływu		spadek połaci (izolacja spadkowa) do wpustów

WYNIKI OBLICZEŃ — ODWODNIENIE DACHÓW (PN-EN 12056-3)

Pole	Typ	A [m²]	Q [l/s]	wpustów	Q_wp [l/s]	Q_przel. [l/s]	h_spiętrz. [cm]
D1	plaski	87,4	4,02	2	9,00	33,62	3,9
D2	plaski	12,5	0,58	1	4,50	8,02	2,2
D3	plaski	11,2	0,52	1	4,50	8,02	2,0
D4	zielony	59,1	2,72	2	9,00	14,56	3,9

OBJAŚNIENIA I UWAGI

- Wymiary w cm (mm w indeksie górnym, np. 24⁴ = 24,5 cm), rzędne w m względem ±0,000 = 101,650 m n.p.m. (PL-EVRF2007-NH).
- Rysunki instalacji na podkładzie rzutów architektury (PB-AR); podkład — linie cienkie szare (warstwy I-PODKLAD).
- Odwodnienie dachów wg PN-EN 12056-3 i WT § 28, § 29; natężenie deszczu wg modelu PANDA (IMGW) — lamela, obliczenia sanitarne, deszczowa; wody opadowe zagospodarowane na działce (zbiornik retencyjny + niecka chłonna), bez odprowadzania do kanalizacji sanitarnej.
- Wpusty dachowe z grzałką (podgrzewane), z kółkiem do membrany/papy i koszem liściowym; przelewy awaryjne w attykach — dno przelewu powyżej poziomu pokrycia przy wpuszczeniu (odpływ normalny przez wpusty).
- Rury spustowe wewnętrzne w izolacji termicznej i akustycznej (otulina ≥ 20 mm); przejścia przez stropy z uszczelnieniem ppoż. wg klasy stropu.
- Dachy: A = 291,8 m², Q = 13,42 l/s; zbiornik 5,0 m³, niecka 23,0 m³.
- SPRAWDZENIE NIESPEŁNIONE (obliczenia): Pole D1: dno przelewu nad pokryciem (odpływ normalny przez wpusty) — -0,046 >= 0,030 m ([ZAL] ≥ 3 cm) — do korekty w modelu.
- SPRAWDZENIE NIESPEŁNIONE (obliczenia): Pole D1: dno przelewu nad pokryciem (odpływ normalny przez wpusty) — -0,006 >= 0,030 m ([ZAL] ≥ 3 cm) — do korekty w modelu.
- SPRAWDZENIE NIESPEŁNIONE (obliczenia): Pole D1: dno przelewu nad pokryciem (odpływ normalny przez wpusty) — -0,006 >= 0,030 m ([ZAL] ≥ 3 cm) — do korekty w modelu.
- Rysunek wygenerowany automatycznie z modelu /home/user/aihouse/model/budynek.yaml (wersja 1.0, 2026-09-25) — generatory lamela.views.

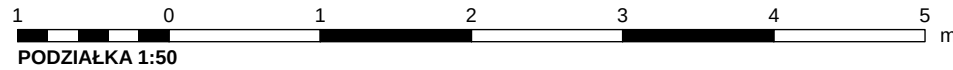

REW.	OPIS ZMIANY	DATA
0	Wydanie — rysunek wygenerowany z modelu	2026-09-25
PRACOWNIA PROJEKTOWA	PRACOWNIA PROJEKTOWA — nazwa do uzupełnienia	STADIUM PT
adres pracowni do uzupełnienia	BRANZA INSTALACJE SANITARNE (IS)	
INWESTOR (do uzupełnienia)	OBIEKT / NAZWA ZAMIERZENIA BUDOWLANEGO Budynek mieszkalny jednorodzinny wolnostojący „Dom LAMELA”	
ADRES / LOKALIZACJA (NR DZIAŁKI, OBRĘB, JEDN. EWIDENCYJNA) ul. Lipowa (fikcyjna), dz. nr ewid. 123/4, obręb 0005 Przykładowo, gm. Przykładowo (fikcyjna)	KAT. OBIEKTU I	
FUNKCJA	IMIĘ I NAZWISKO	SPECJALNOŚĆ, NR UPRAWNIEN
Projektant		DATA
Projektant (wsp.)		PODPIS
Sprawdzający		
Opracował		
TYTUŁ RYSUNKU	ODWODNIENIE DACHÓW — RZUT DACHU	
SKALA 1:50	FORMAT A3×3	DATA WYDANIA 2026-09-25
RODZAJ DOK. rzut instalacji	NR RYSUNKU PT-IS-07	ARKUSZ 7/17
		REW. 0