


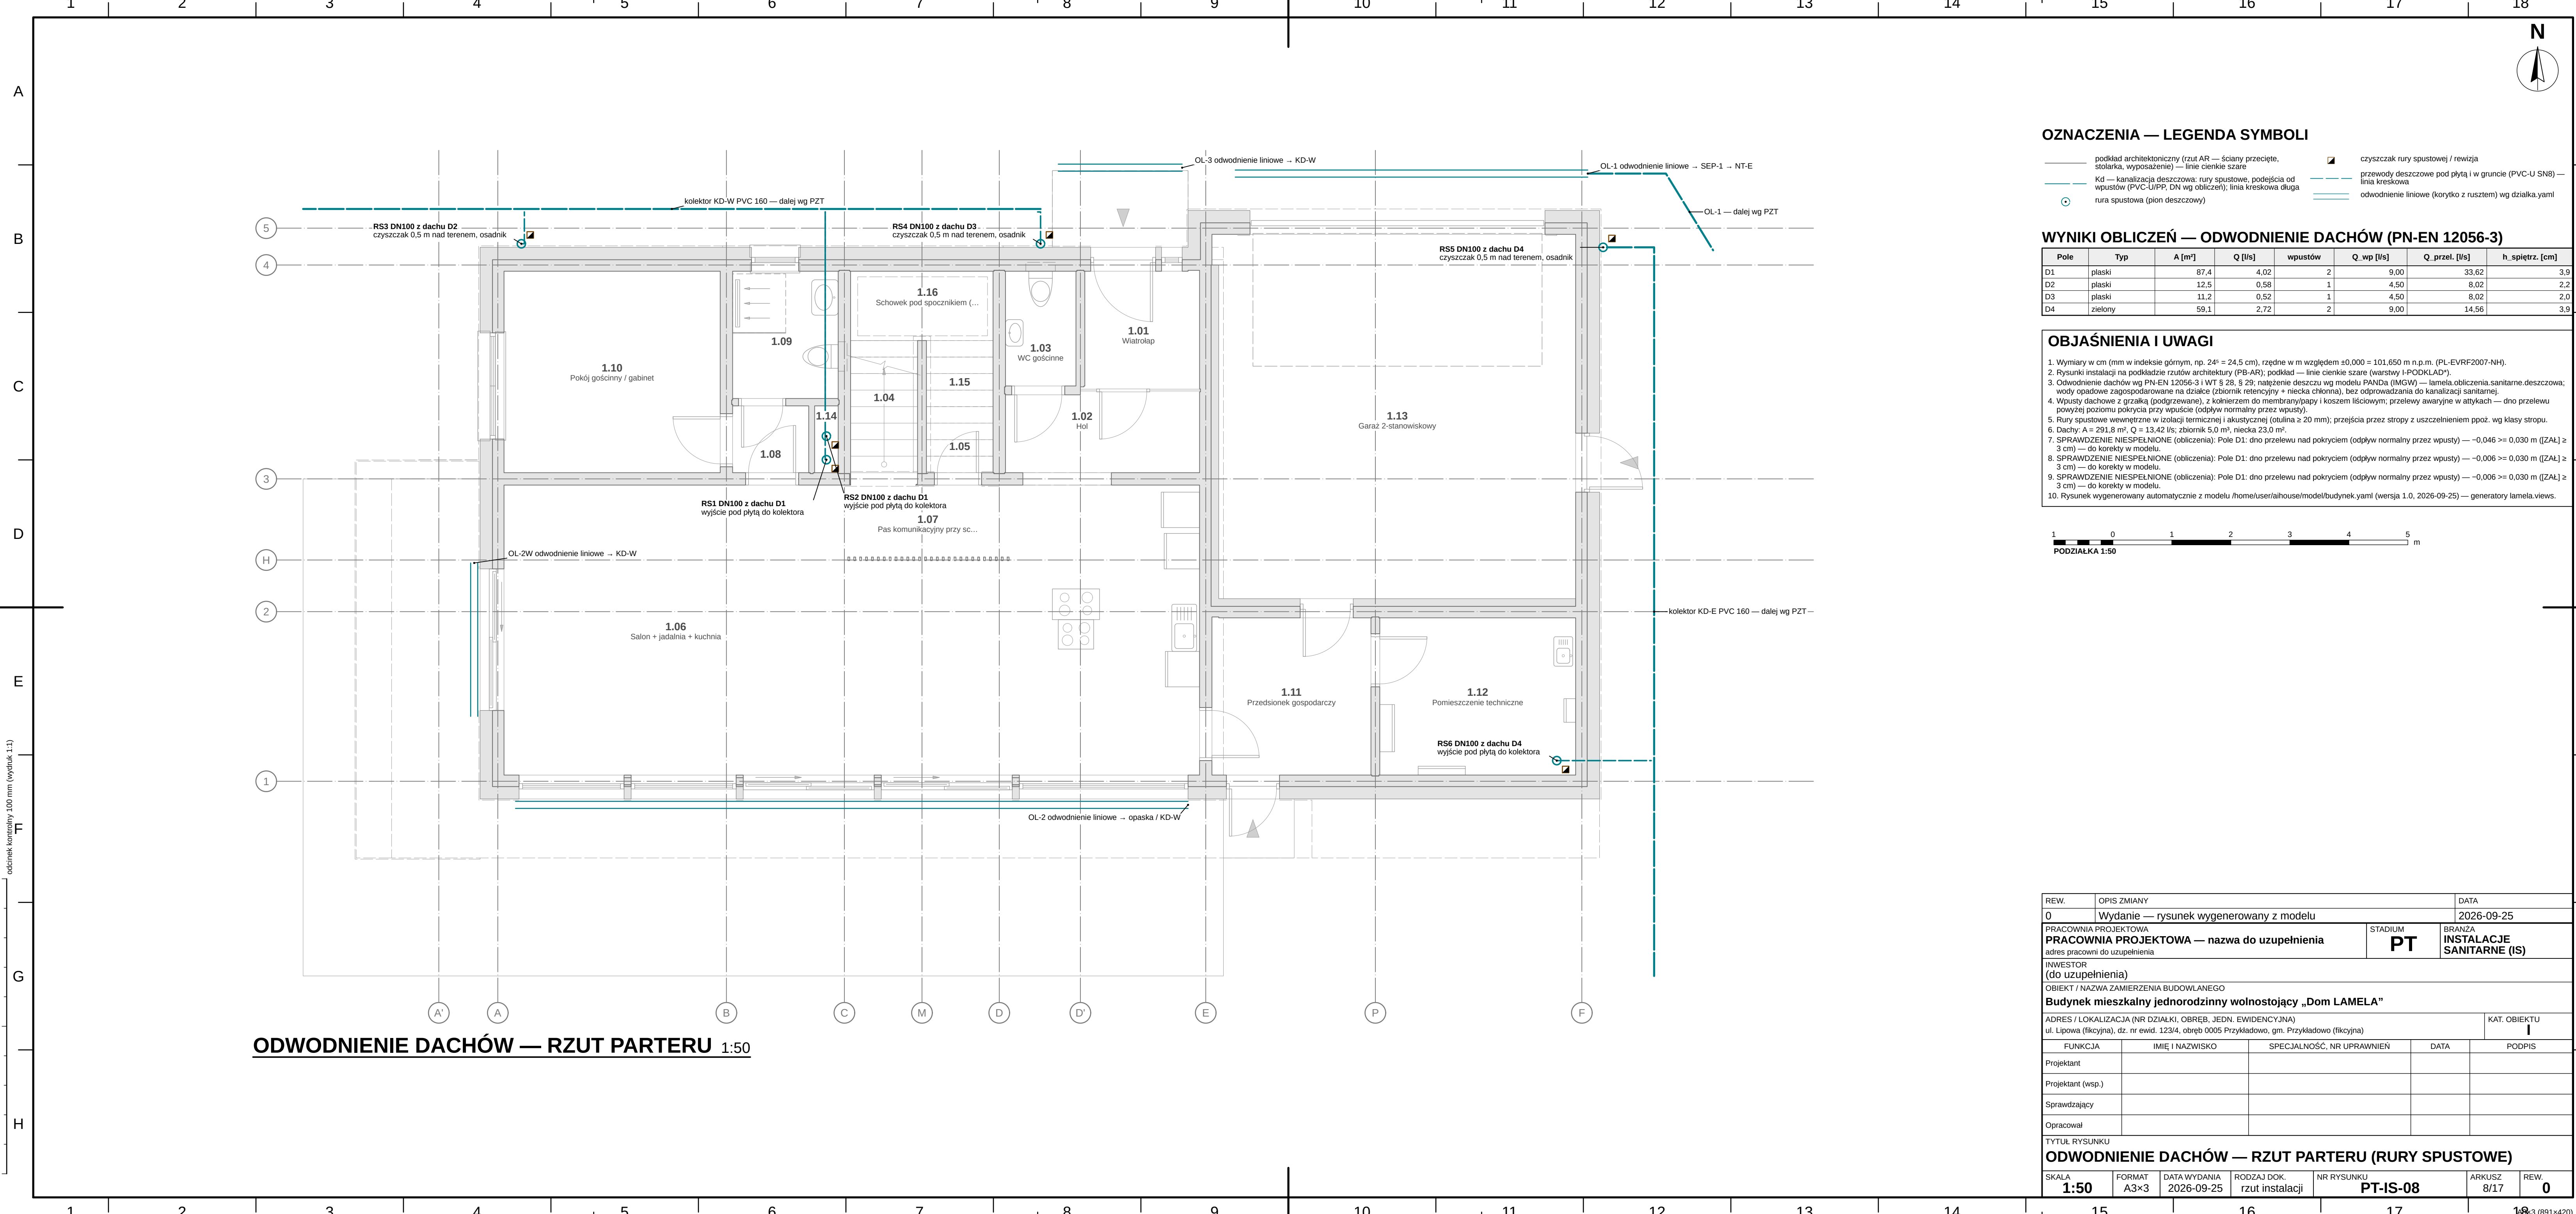

ODWODNIENIE DACHÓW — RZUT PARTERU 1:50

OZNACZENIA — LEGENDA SYMBOLI


	podkład architektoniczny (rzut AR — ściany przecięte, stolarka, wyposażenie) — linie cienie szare		czyszczak rury spustowej / rewizja
	Kd — kanalizacja deszczowa: rury spustowe, podejścia od wpustów (PVC-U/PP, DN wg obliczeń); linia kreskowa długa		przewody deszczowe pod płytą i w gruncie (PVC-U SN8) — linia kreskowa
	rura spustowa (pion deszczowy)		odwodnienie liniowe (korytko z rusztem) wg działka.yaml

WYNIKI OBLICZEŃ — ODWODNIENIE DACHÓW (PN-EN 12056-3)

Pole	Typ	A [m²]	Q [l/s]	wpustów	Q_wp [l/s]	Q_przel. [l/s]	h_spiętrz. [cm]
D1	plaski	87,4	4,02	2	9,00	33,62	3,9
D2	plaski	12,5	0,58	1	4,50	8,02	2,2
D3	plaski	11,2	0,52	1	4,50	8,02	2,0
D4	zielony	59,1	2,72	2	9,00	14,56	3,9

OBJAŚNIENIA I UWAGI

- Wymiary w cm (mm w indeksie górnym, np. 24^a = 24,5 cm), rzędne w m względem ±0,000 = 101,650 m n.p.m. (PL-EVRF2007-NH).
- Rysunki instalacji na podkładzie rzutów architektury (PB-AR); podkład — linie cienie szare (warstwy I-PODKŁAD).
- Odwodnienie dachów wg PN-EN 12056-3 i WT § 28, § 29; natężenie deszczu wg modelu PANDA (IMGW) — lamela obliczenia sanitarne deszczowa; wody opadowe zagospodarowane na działce (zbiornik retencyjny + niecka chłonna), bez odprowadzania do kanalizacji sanitarnej.
- Wpusty dachowe z grzałką (podgrzewane), z kolnierzem do membrany/papy i koszem liściowym; przelewy awaryjne w attykach — dno przelewu powyżej poziomu pokrycia przy wpuscie (odpływ normalny przez wpusty).
- Rury spustowe wewnętrzne w izolacji termicznej i akustycznej (ciutlina ≥ 20 mm); przejścia przez stropy z uszczelnieniem ppoż. wg klasy stropu.
- Dachy: A = 291,8 m², Q = 13,42 l/s; zbiornik 5,0 m³, niecka 23,0 m³.
- SPRAWDZENIE NIESPEŁNIONE (obliczenia): Pole D1: dno przelewu nad pokryciem (odpływ normalny przez wpusty) — -0,046 >= 0,030 m ([ZAL] ≥ 3 cm) — do korekty w modelu.
- SPRAWDZENIE NIESPEŁNIONE (obliczenia): Pole D1: dno przelewu nad pokryciem (odpływ normalny przez wpusty) — -0,006 >= 0,030 m ([ZAL] ≥ 3 cm) — do korekty w modelu.
- SPRAWDZENIE NIESPEŁNIONE (obliczenia): Pole D1: dno przelewu nad pokryciem (odpływ normalny przez wpusty) — -0,006 >= 0,030 m ([ZAL] ≥ 3 cm) — do korekty w modelu.
- Rysunek wygenerowany automatycznie z modelu /home/user/aihouse/model/budynek.yaml (wersja 1.0, 2026-09-25) — generatory lamela.views.

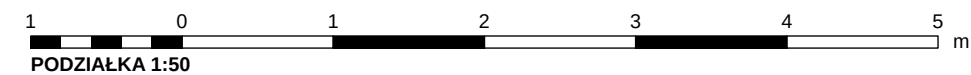

REW.	OPIS ZMIANY			DATA	
0	Wydanie — rysunek wygenerowany z modelu			2026-09-25	
PRACOWNIA PROJEKTOWA				STADIUM PT	BRANŻA INSTALACJE SANITARNE (IS)
PRACOWNIA PROJEKTOWA — nazwa do uzupełnienia					
adres pracowni do uzupełnienia					
INWESTOR (do uzupełnienia)					
OBIEKT / NAZWA ZAMIERZENIA BUDOWLANEGO					
Budynek mieszkalny jednorodzinny wolnostojący „Dom LAMELA”					
ADRES / LOKALIZACJA (NR DZIAŁKI, OBRĘB, JEDN. EWIDENCYJNA)					KAT. OBIEKTU I
ul. Lipowa (fikcyjna), dz. nr ewid. 123/4, obręb 0005 Przykładowo, gm. Przykładowo (fikcyjna)					
FUNKCJA	IMIĘ I NAZWISKO	SPECJALNOŚĆ, NR UPRAWNIEN		DATA	PODPIS
Projektant					
Projektant (wsp.)					
Sprawdzający					
Opracował					
TYTUŁ RYSUNKU					
ODWODNIENIE DACHÓW — RZUT PARTERU (RURY SPUSTOWE)					
SKALA	FORMAT	DATA WYDANIA	RODZAJ DOK.	NR RYSUNKU	ARKUSZ
1:50	A3×3	2026-09-25	rzut instalacji	PT-IS-08	8/17
					REW.
					0