


PRZEKRÓJ B-B 1:50

wysokość budynku wg § 6 WT: H = 9,79 m
9/79³

odcinek kantabiny 100 mm (wydruk 1:1)

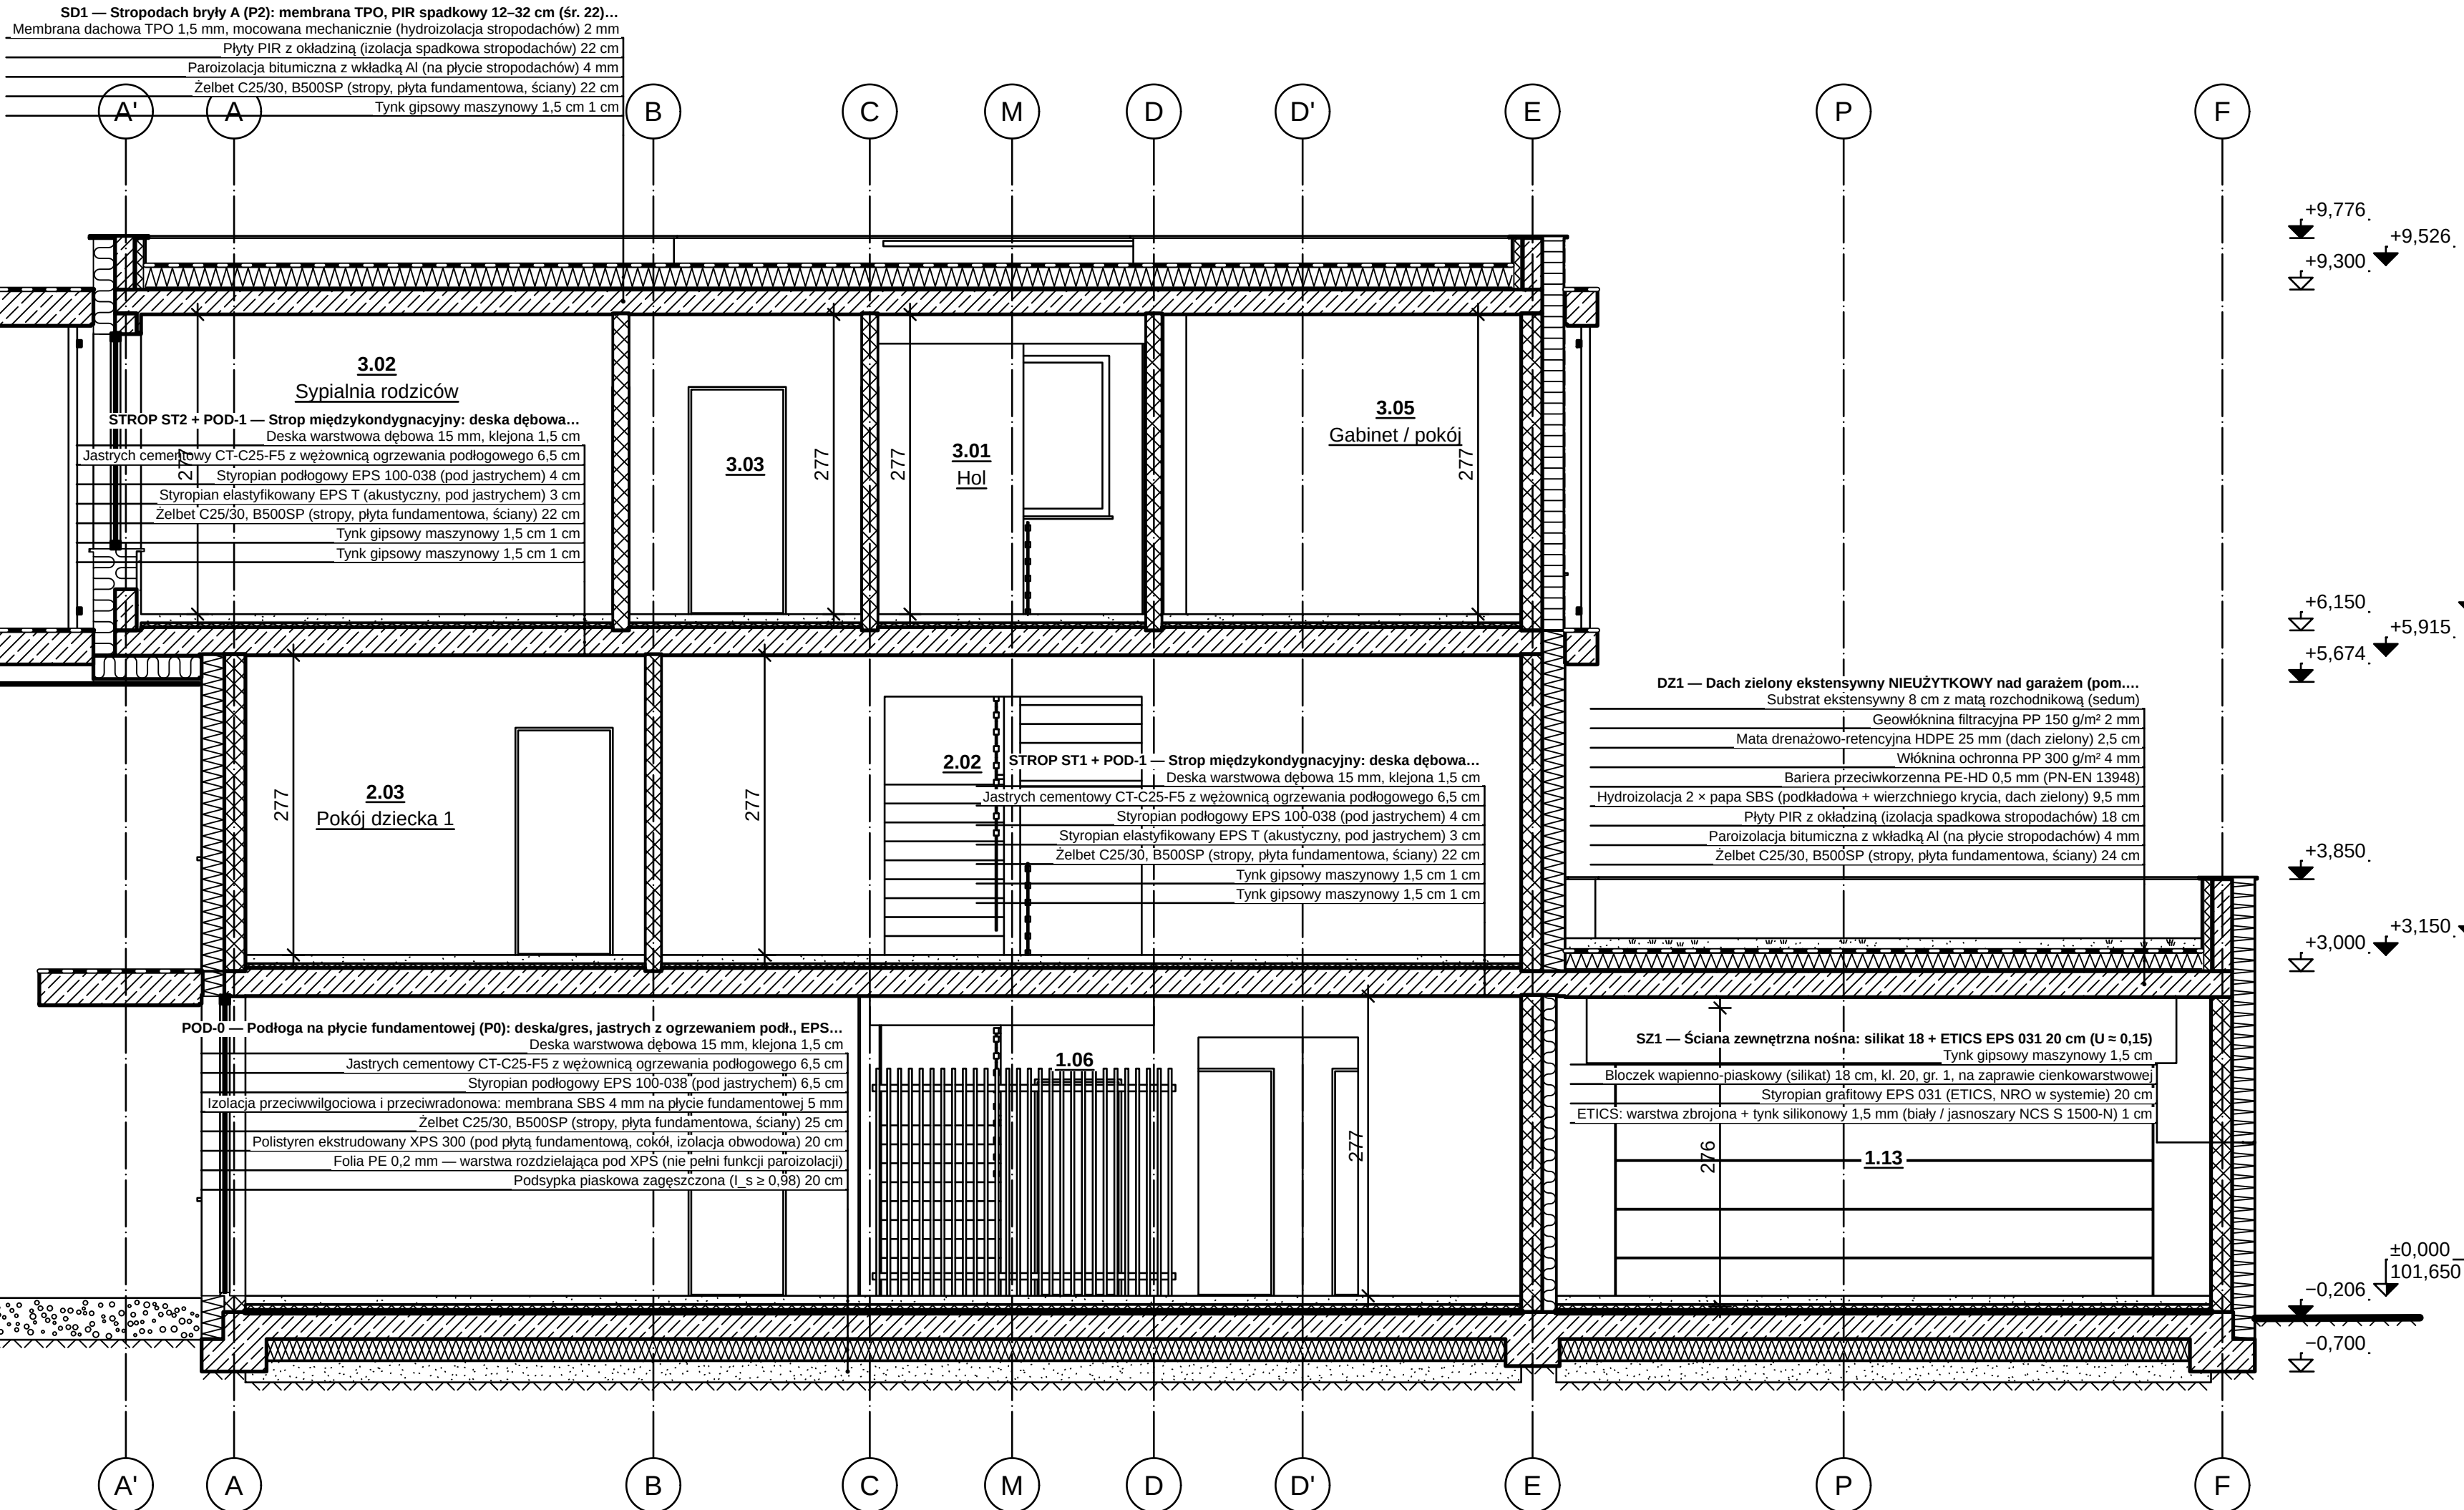


OZNACZENIA MATERIAŁÓW (PN-B-01030 + przyjęte)

	grunt rodzimy		Membrana fasadowa wiatroizolacyjna UV-stabilna, czarna (sd = 0,02 m)
	Substrat ekstensywny 8 cm z matą rozchodnikową (sedum)		Błoczek wapienno-piaskowy 12 cm, kl. 15 (ścianki działowe, licowy w kładce); Błoczek wapienno-piaskowy (silikat) 18 cm, kl. 20, gr. 1, na zaprawie cienkowarstwowej — krętka ułożona 45°/135°
	Welna mineralna 035 (szkielet, docieplenia, ściana dom-garaż); Welna mineralna fasadowa (elewacja wentylowana bryły A, A1) — meander „UUU”		Paroizolacja bitumiczna z wkładką Al (na płycie stropodachów) — linia kreskowa cienka 3/1 po ciepłej stronie
	Płyty PIR z okładziną (izolacja spadkowa stropodachów) — zygzak z okładzinami		Podsypka piaskowa zagęszczona (l_s ≥ 0,98)
	Izolacja przeciwwilgociowa i przeciwdrań: membrana SBS 4 mm na płycie fundamentowej — linia bardzo gruba		Płyta gipsowo-kartonowa 12,5 mm (GKB / GKBI w łazienkach); Podosufłoka zewnętrzna: płyta włóknocementowa 12 mm na ruszcie, RAL 7016
	Membrana dachowa TPO 1,5 mm, mocowana mechanicznie (hydroizolacja stropodachów); Hydroizolacja 2 x papa SBS (podkładowa + wierzchniego krycia, dach zielony) — pas czarno-biały		Obróbki blacharskie (blacha powlekana); Stalarka — profile aluminiowe, antracyt; Stal malowana proszkowo (balustrady, rygle) — zaczerpnienie
	Styropian grafitowy EPS 031 (ETICS, NRO w systemie); Styropian podłogowy EPS 100-038 (pod jastrychem); Styropian elastyczny EPS T (akustyczny, pod jastrychem) — zygzak „VVV”		Żelbet C25/30, B500SP (stropy, płyta fundamentowa, ściany); Żelbet C30/37 XC4/XF1 (krawędzie płyt wysuniętych, atyki, belki) — 45° na przemian ciągłe i przerywane
	Polistyren ekstrudowany XPS 300 (pod płytą fundamentową, cokół, izolacja obwodowa) — zygzak podwójny		Podbudowa nawierzchni (kruszywo)
	Jasnych cementowych CT-C25-F5 z węzownicą ogrzewania podłogowego — kropki		

OBJAŚNIENIA I UWAGI

- Wymiary w cm (mm w indeksie górnym, np. 24⁶ = 24,5 cm), rzędne w m względem ±0,000 = 101,650 m n.p.m. (PL-EVRF2007-NH).
- Rzędne: trójkąt zaczerpiony — poziom wykończenia, niezaczerpiony — konstrukcji, w pokoiwie zaczerpiony — poziom ±0,000 z rzędną bezwzględną (PN-B-01025).
- Wysokość budynku wg § 6 WT: od terenu przy najniższym wejściu (-0,267) do wierzchu stropodachu D1 (+9,526) — H = 9,79 m (bez atyki).
- Opisy warstw: kod i nazwa przegrody z modelu, materiały i grubości wg modelu (od góry / od lewej).
- Opisy warstw pominięte na rysunku (brak miejsca w podziale 1:50): STROP ST22 + POD-1, OK1 — układ warstw wg zestawienia przegród w części opisowej / przekroju 1:50.
- Rysunek wygenerowany automatycznie z modelu /home/user/aihouse/model/budynek.yaml (wersja 1.0, 2026-09-25) — generatory lamela.views.

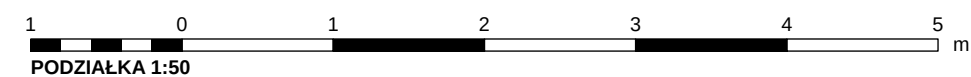

REW.	OPIS ZMIANY	DATA
0	Wydanie — rysunek wygenerowany z modelu	2026-09-25
PRACOWNIA PROJEKTOWA PRACOWNIA PROJEKTOWA — nazwa do uzupełnienia		STADIUM PB
adres pracowni do uzupełnienia		BRANZA ARCHITEKTURA (AR)
INWESTOR (do uzupełnienia)		
OBIEKT / NAZWA ZAMIERZENIA BUDOWLANEGO Budynek mieszkalny jednorodzinny wolnostojący „Dom LAMELA”		
ADRES / LOKALIZACJA (NR DZIAŁKI, OBRĘB, JEDN. EWIDENCYJNA) ul. Lipowa (fikcyjna), dz. nr ewid. 123/4, obręb 0005 Przykładowo, gm. Przykładowo (fikcyjna)		KAT. OBIEKTU I
FUNKCJA	IMIĘ I NAZWISKO	SPECJALNOŚĆ, NR UPRAWNIENI
Projektant		DATA
Projektant (wsp.)		PODPIS
Sprawdzający		
Opracował		
TYTUŁ RYSUNKU		

PRZEKRÓJ B-B

SKALA	FORMAT	DATA WYDANIA	RODZAJ DOK.	NR RYSUNKU	ARKUSZ	REW.
1:50	A3x3	2026-09-25	przekrój	PB-AR-06	6/10	0