
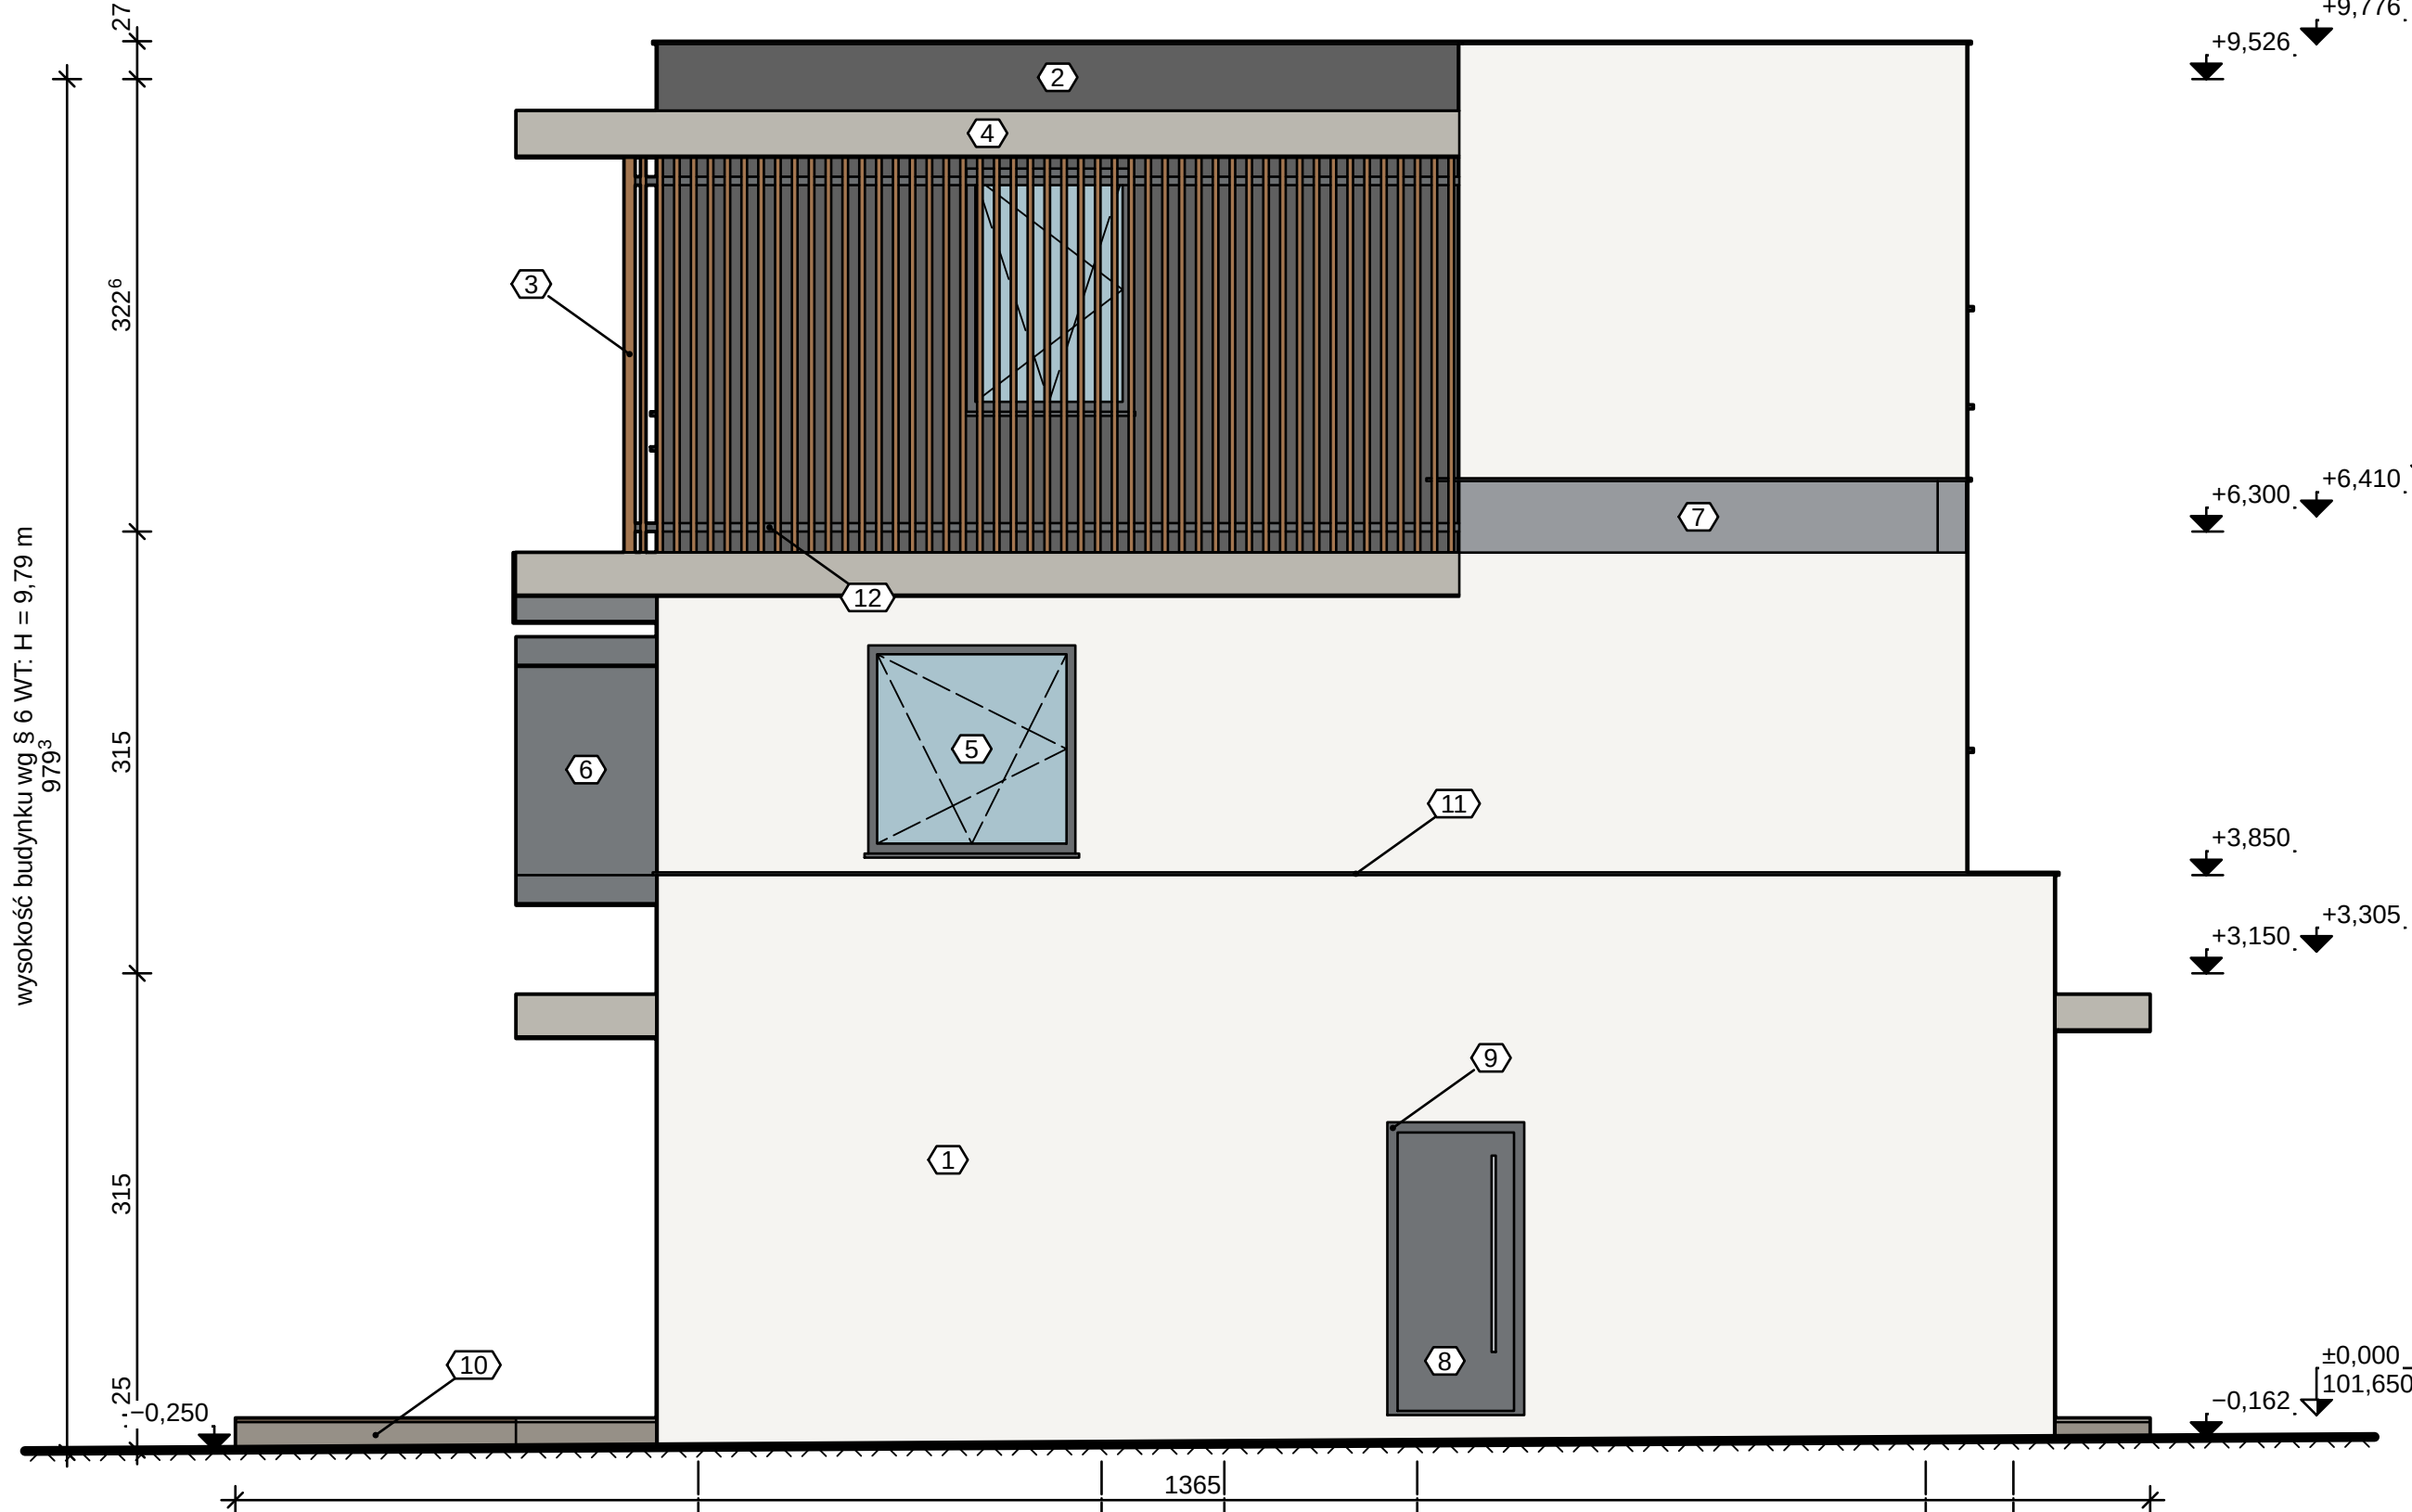
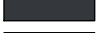
 


 


ELEWACJA WSCHODNIA 1:50

KOLORYSTYKA I MATERIAŁY ELEWACJI		
1		ETICS: warstwa zbrojona + tynk silikonowy 1,5 mm (biały) / jasnoszary NCS S 1500-N [TYNK_SIL] #f5f4f0
2		Membrana fasadowa wiatroizolacyjna UV-stabilna, czarna (sd ≈ 0,02 m) [MEMB_WIATR] #1d1d1d
3		Lamele elewacyjne 40×80 mm, drewno termoolesion (klasa 1 trwałości), olejowane [DREWNO_TERMO] #9b6b41
4		Żelbet C30/37 XC4/XF1 (krawędzie płyt wysuniętych, attyki, belki) [ZB_C30] #b4b1a9
5		Szkło (szyby zespolone) [SZKLO] #a9c3cd
6		Rama boksu C: ruszt stalowy ocynkowany w okładzinie z blachy aluminiowej RAL 7016 (pusta w środku) [RAMA_C] #3b4044
7		Styropian grafitowy EPS 031 (ETICS, NRO w systemie) [EPS031] #8f9296
8		Drzwi zewnętrzne, płycina aluminiowa [DRZWI_ZEWNI] #34383c
9		Stolarka — profile aluminiowe, antracyt [RAMA_ALU] #2b2f33
10		Podbudowa nawierzchni (kruszywo) [NAW_PODBUDOWA] #8d877d
11		Obróbki blacharskie (blacha powlekana) [OBRÓBKA_BLACH] #3b3f43
12		Stal malowana proszkowo (balustrady, rygle) [STAL_BAL] #2c3034

OBJAŚNIENIA I UWAGI

1. Wymiary w mm (mm w indeksie górnym, np. 24° = 24,5 cm), rzędne w m względem $\pm 0,000 = 101,650$ m n.p.m. (PL-EVRF2007-NH).
2. Rzędne: trójkąt zaczerpiony — poziom wykończenia, niezaczerpiony — konstrukcji, w połowie zaczerpiony — poziom $\pm 0,000$ z rzędną bezwzględną (PN-B-01025).
3. Wysokość budynku wg § 6 WT: od terenu przy najniższym położonym wejściu ($-0,267$) do wierzchu stropodachu D1 ($+9,526$) — $H = 9,79$ m (bez attyk).
4. Kolorystyka orientacyjna wg kolorów materiałów w modelu (od potwierdzenia wzornikiem RAL/NCs).
5. Rysunek wygenerowany automatycznie z modelu `/home/user/aihouse/model/budynek.yaml` (wersja 1.0, 2026-09-25) — generatory lamela.views.

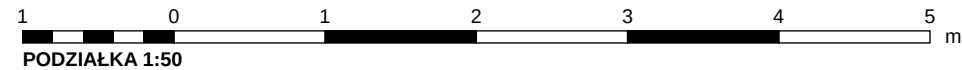

REW.	OPIS ZMIANY	DATA				
0	Wydanie — rysunek wygenerowany z modelu		2026-09-25			
PRACOWNIA PROJEKTOWA PRACOWNIA PROJEKTOWA — nazwa do uzupełnienia adres pracowni do uzupełnienia		STADIUM PB	BRANŻA ARCHITEKTURA (AR)			
INWESTOR (do uzupełnienia)						
OBIEKT / NAZWA ZAMIERZENIA BUDOWLANEGO Budynek mieszkalny jednorodzinny wolnostojący „Dom LAMELA”						
ADRES / LOKALIZACJA (NR DZIAŁKI, OBRĘB, JEDN. EWIDENCYJNA) ul. Lipowa (fikcyjna), dz. nr ewid. 123/4, obręb 0005 Przykładowo, gm. Przykładowo (fikcyjna)			KAT. OBIEKTU I			
FUNKCJA	IMIĘ I NAZWISKO	SPECJALNOŚĆ, NR UPRAWNIENI	DATA	PODPIS		
Projektant						
Projektant (wsp.)						
Sprawdzający						
Opracował						
TYTUŁ RYSUNKU ELEWACJA WSCHODNIA						
SKALA 1:50	FORMAT A2	DATA WYDANIA 2026-09-25	RODZAJ DOK. elewacja	NR RYSUNKU PB-AR-09	ARKUSZ 9/10	REW. 0