

A

B

C

D

E

F

G

H

J

K

L

M

N

P

Q


R

ZESTAWIENIE STALI


Poz.	Ø [mm]	Kształt ISO 3766, wymiary [cm]	Długość [cm]	Liczba [szt.]	Elem.	Ø8 [m]	Ø12 [m]	Ø14 [m]
1	14	21: a=25 b=536 c=25	581	3	B6			17.43
2	12	21: a=25 b=536 c=25	582	2	B6		11.64	
3	8	51: a=15 b=35	116	22	B6	25.52		
4	14	21: a=25 b=568 c=25	613	2	B7			12.26
5	12	21: a=25 b=568 c=25	614	2	B7		12.28	
6	8	51: a=20 b=80	216	16	B7	34.56		
7	12	21: a=25 b=286 c=25	332	18	B8		59.76	
8	8	51: a=20 b=45	146	78	B8	113.88		
9	12	21: a=25 b=243 c=25	289	4	N16		11.56	
10	8	51: a=13 b=49	140	8	N16	11.20		
Długość całkowita [m]						185.2	95.2	29.7
Masa jednostkowa [kg/m]						0.395	0.888	1.208
Masa [kg]						73.1	84.6	35.9
RAZEM stal B500SP [kg]								193.5

B6, B7: beton C30/37, XC1, otulina strzemiem c_nom = 25 mm (tabl. 4.4N + NA).
B8, B9, B10, N16: beton C25/30, XC1, otulina strzemiem c_nom = 25 mm (tabl. 4.4N + NA).

B7 — 25×85 cm, C30/37 (poz. 5.16)

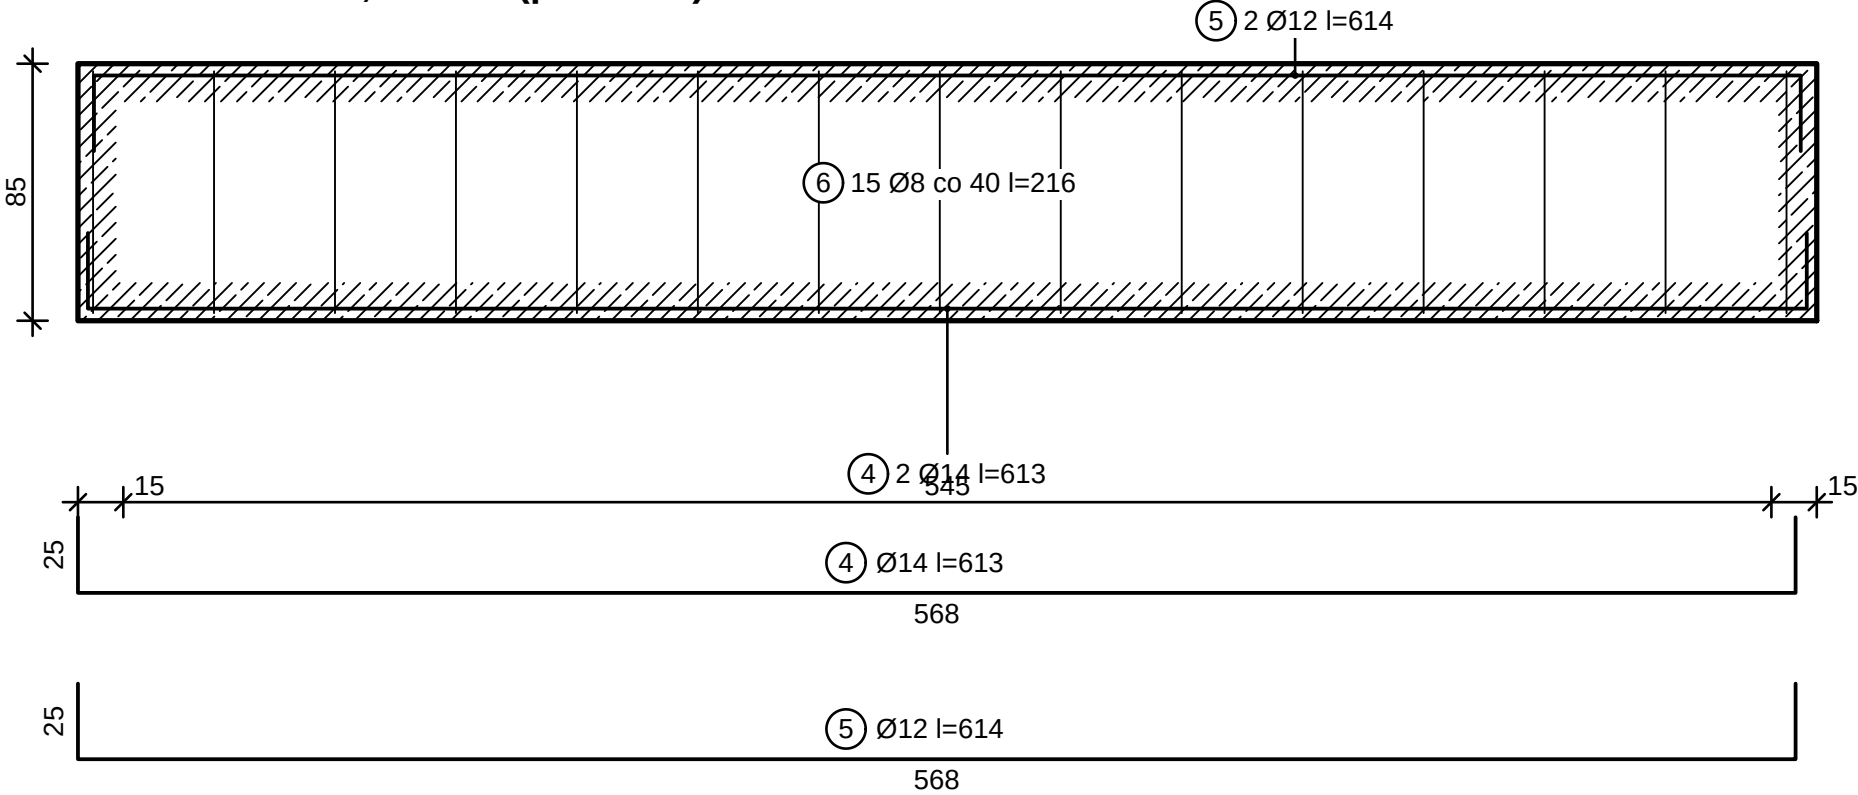


A-A

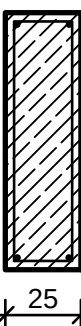

OBJAŚNIENIA I UWAGI

- Wymiary w cm (mm w indeksie górnym, np. 24^o = 24,5 cm), rzędne w m względem ±0,000 = 101,650 m n.p.m. (PL-EVRF2007-NH).
- Belki: preły dolne i górne z odcięciami 90° w strefach podporowych (zakotwienie ≥ l_{bd} od lica podpory — PN-EN 1992-1-1 § 2.1.4), strzemięna zamknięte z hakami 135° (§ 5.1, rys. 8.5), pierwsze strzemie 5 cm od lica podpory; rozstaw wg obliczeń (§ 6.2.3), s ≤ min(0,15·d, 400 mm) (§ 9.6.4).
- Przekrój A-A — w środku rozpiętości; długości prętów l — długości rozwinięcia (wymiary zewnętrzne, odliczenie gięcia wg PN-EN ISO 3766).
- Betonowanie: beton wg PN-EN 206+A2 i PN-B-06265 (klasa, ekspozycja, D_{max} 16 mm, konsystencja S3); pielęgnacja ≥ 7 dni (klasa pielęgnacji 2 — PN-EN 13670 p. 8.5); przerwy robocze wyłącznie w miejscach uzgodnionych z projektantem.
- Rozszalowanie i usunięcie podpór: płyty i belki po uzyskaniu ≥ 70 % f_{ck} (PN-EN 13670 p. 5.6 i 8.5), wsporniki — nie wcześniej niż po 28 dniach i po wykonaniu elementów doczających zaplecze; podpory wtórne do 28 dni.
- Rysunek wygenerowany automatycznie z modelu model/budynki.yam (wersja 1.0, 2026-09-25) — generatory lamela.views.


B6 — 20×40 cm, C30/37 (poz. 5.1)

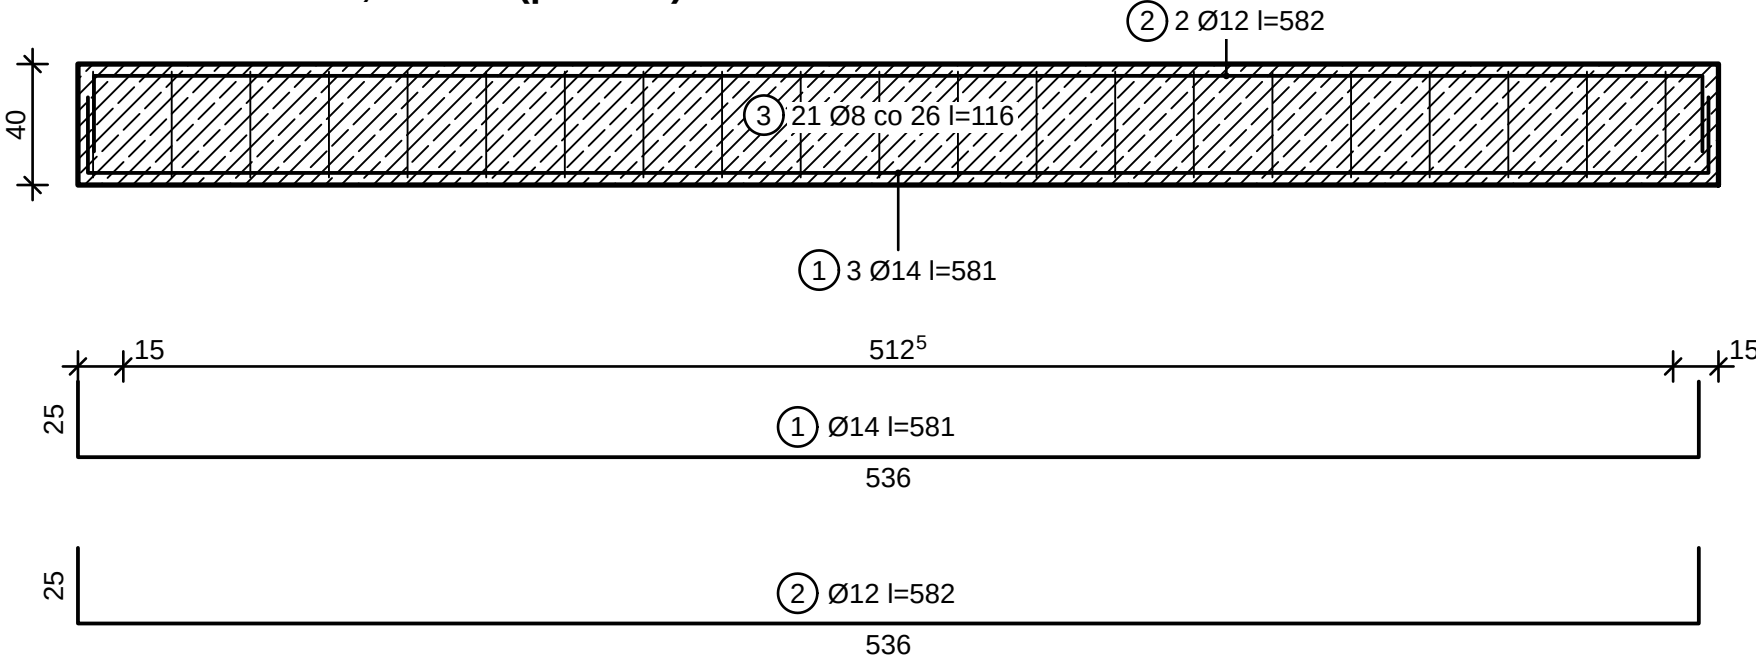


A-A




N16 — 18×54 cm, C25/30 (poz. 5.13)

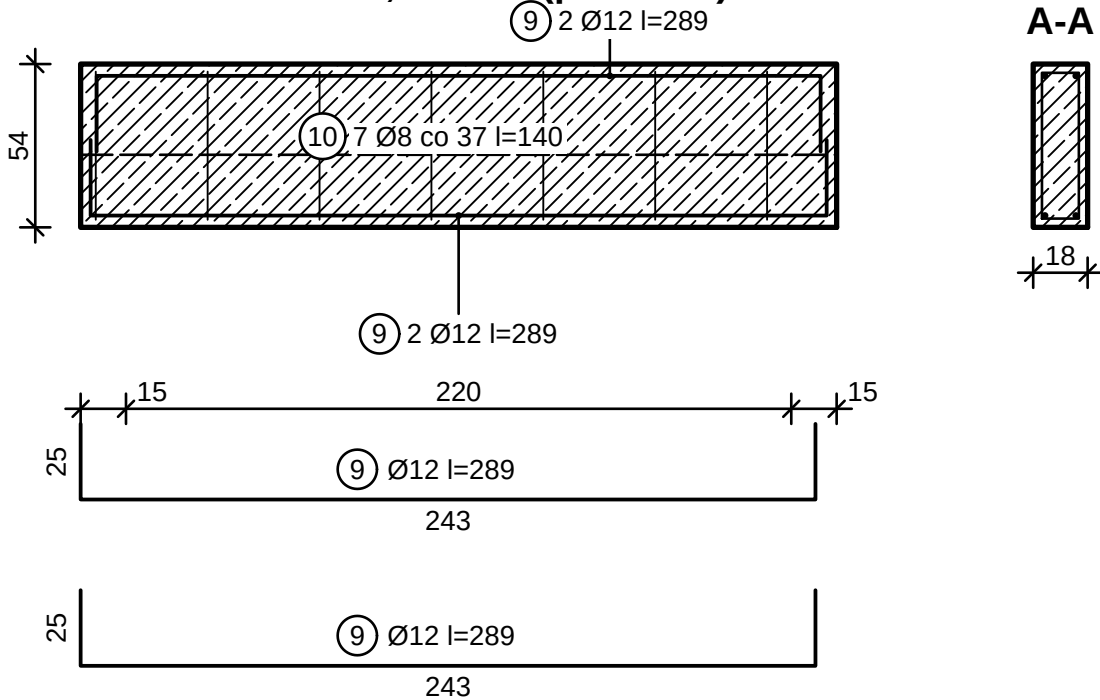


A-A

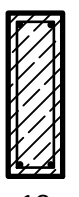


B8 — 25×50 cm, C25/30 (poz. 5.17)

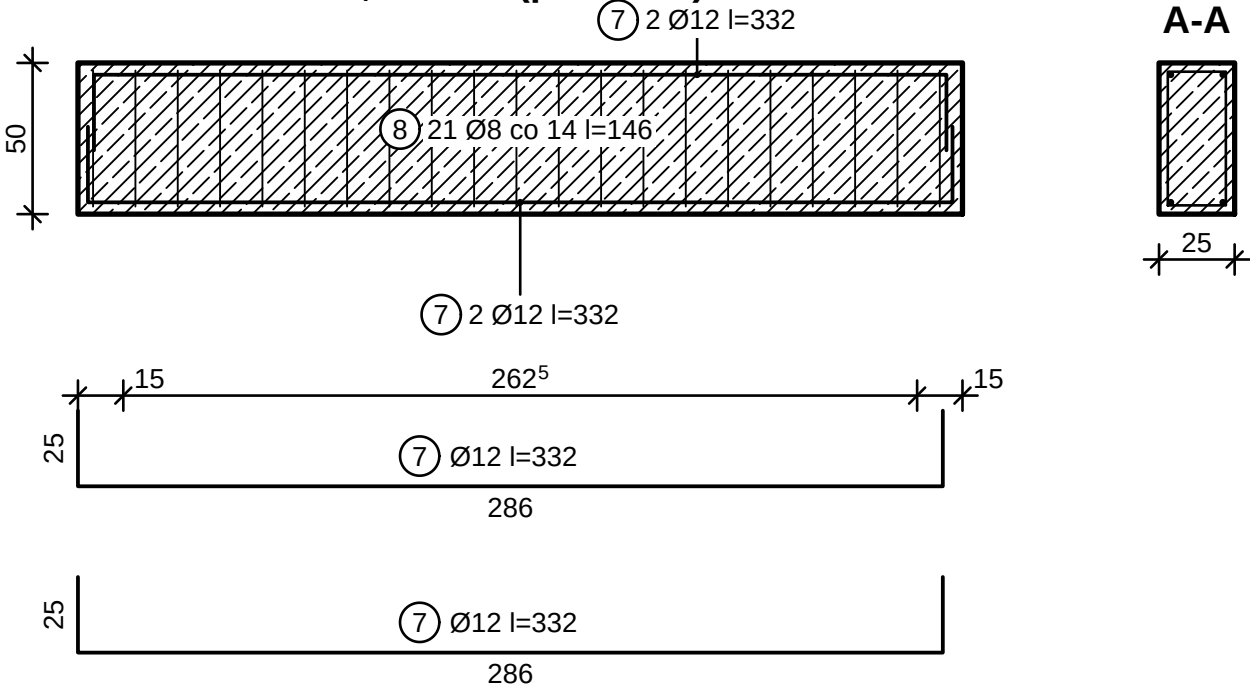


A-A

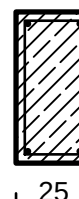


B9 — 25×50 cm, C25/30 (poz. 5.12)

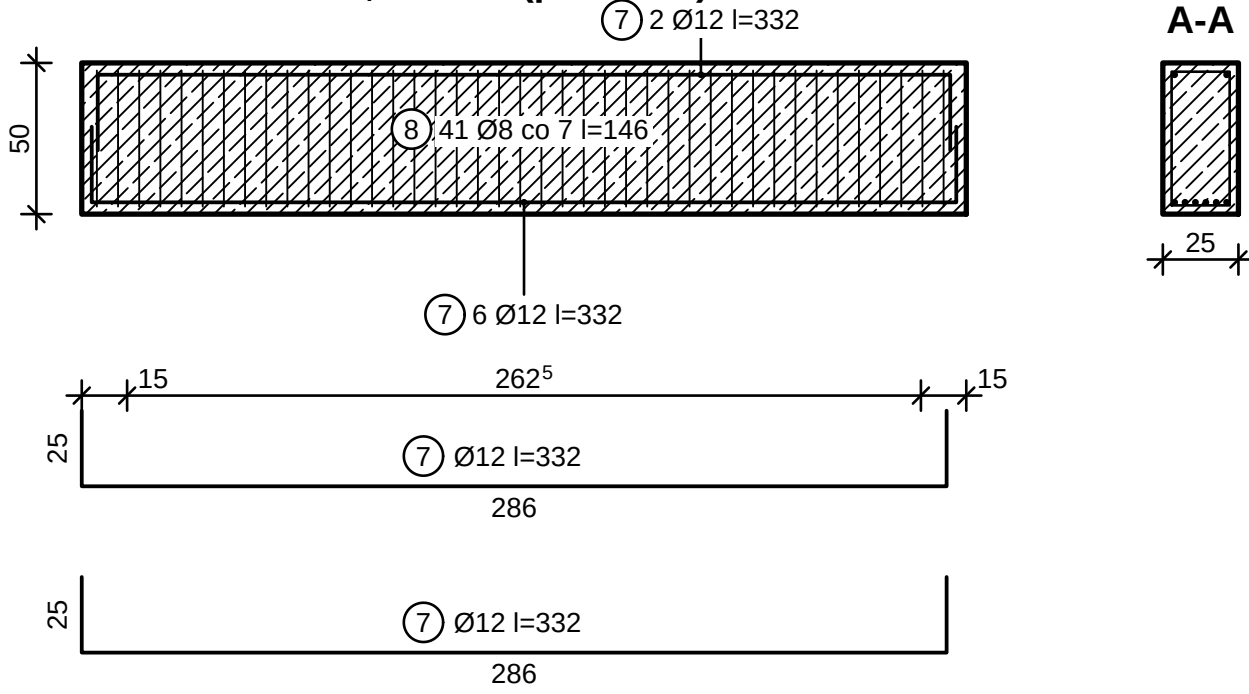



A-A

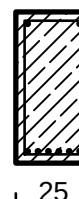


B10 — 25×50 cm, C25/30 (poz. 5.2)

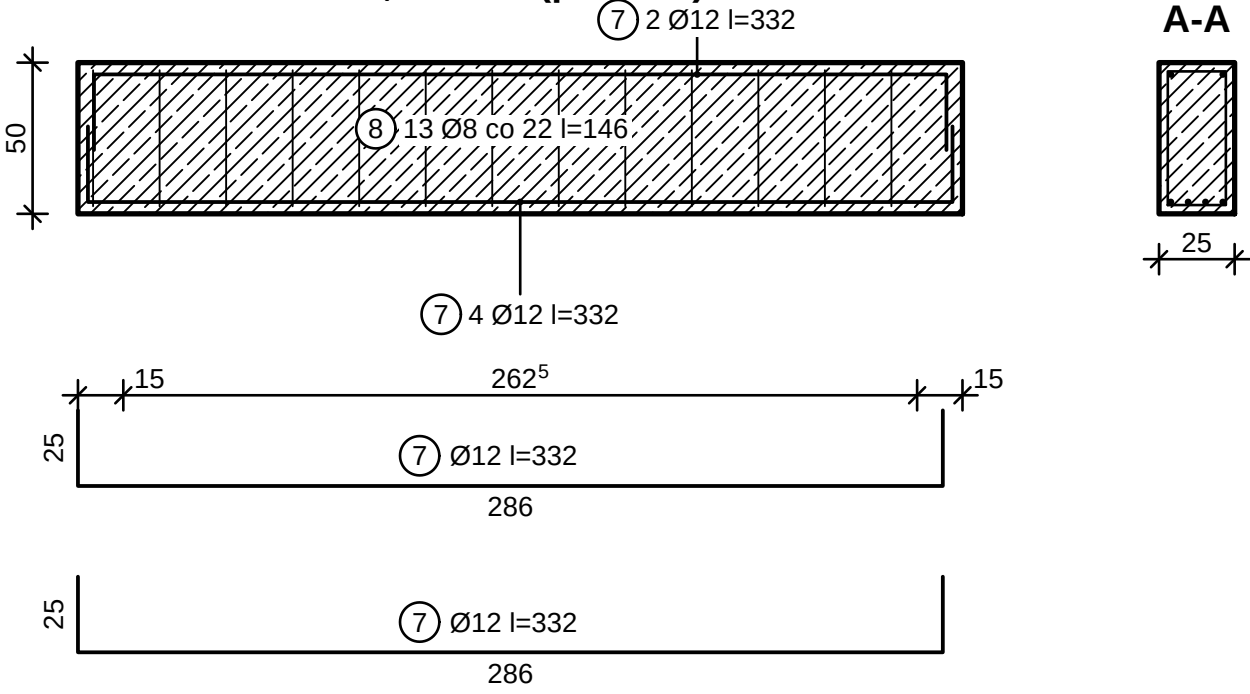

A-A

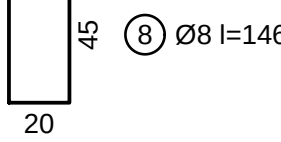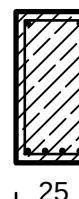

ZBROJENIE BELEK B6, B7, B8, B9, B10, N16 1:25

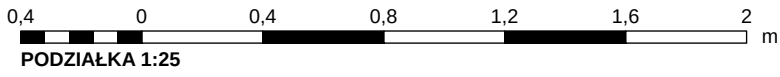

REW.	OPIS ZMIANY	DATA				
0	Wydanie — rysunek wygenerowany z modelu	2026-09-25				
PRACOWNIA PROJEKTOWA		STADIUM	BRANŻA			
PRACOWNIA PROJEKTOWA — nazwa do uzupełnienia		PT	KONSTRUKCJA (BO)			
adres pracowni do uzupełnienia						
INWESTOR						
(do uzupełnienia)						
OBIEKT / NAZWA ZAMIERZENIA BUDOWLANEGO						
Budynek mieszkalny jednorodzinny wolnostojący „Dom LAMELA”						
ADRES / LOKALIZACJA (NR DZIAŁKI, OBRĘB, JEDN. EWIDENCYJNA)			KAT. OBIEKTU			
ul. Lipowa (fikcyjna), dz. nr ewid. 123/4, obręb 0005 Przykładowo, gm. Przykładowo (fikcyjna)			I			
FUNKCJA	IMIĘ I NAZWISKO	SPECJALNOŚĆ, NR UPRAWNIEN	DATA	PODPIS		
Projektant						
Projektant (wsp.)						
Sprawdzający						
Opracował						
TYTUŁ RYSUNKU						
ZBROJENIE BELEK (2)						
SKALA	FORMAT	DATA WYDANIA	RODZAJ DOK.	NR RYSUNKU	ARKUSZ	REW.
1:25	500×841	2026-09-25	rysunek zbrojenia	PT-BO-21	21/26	0