


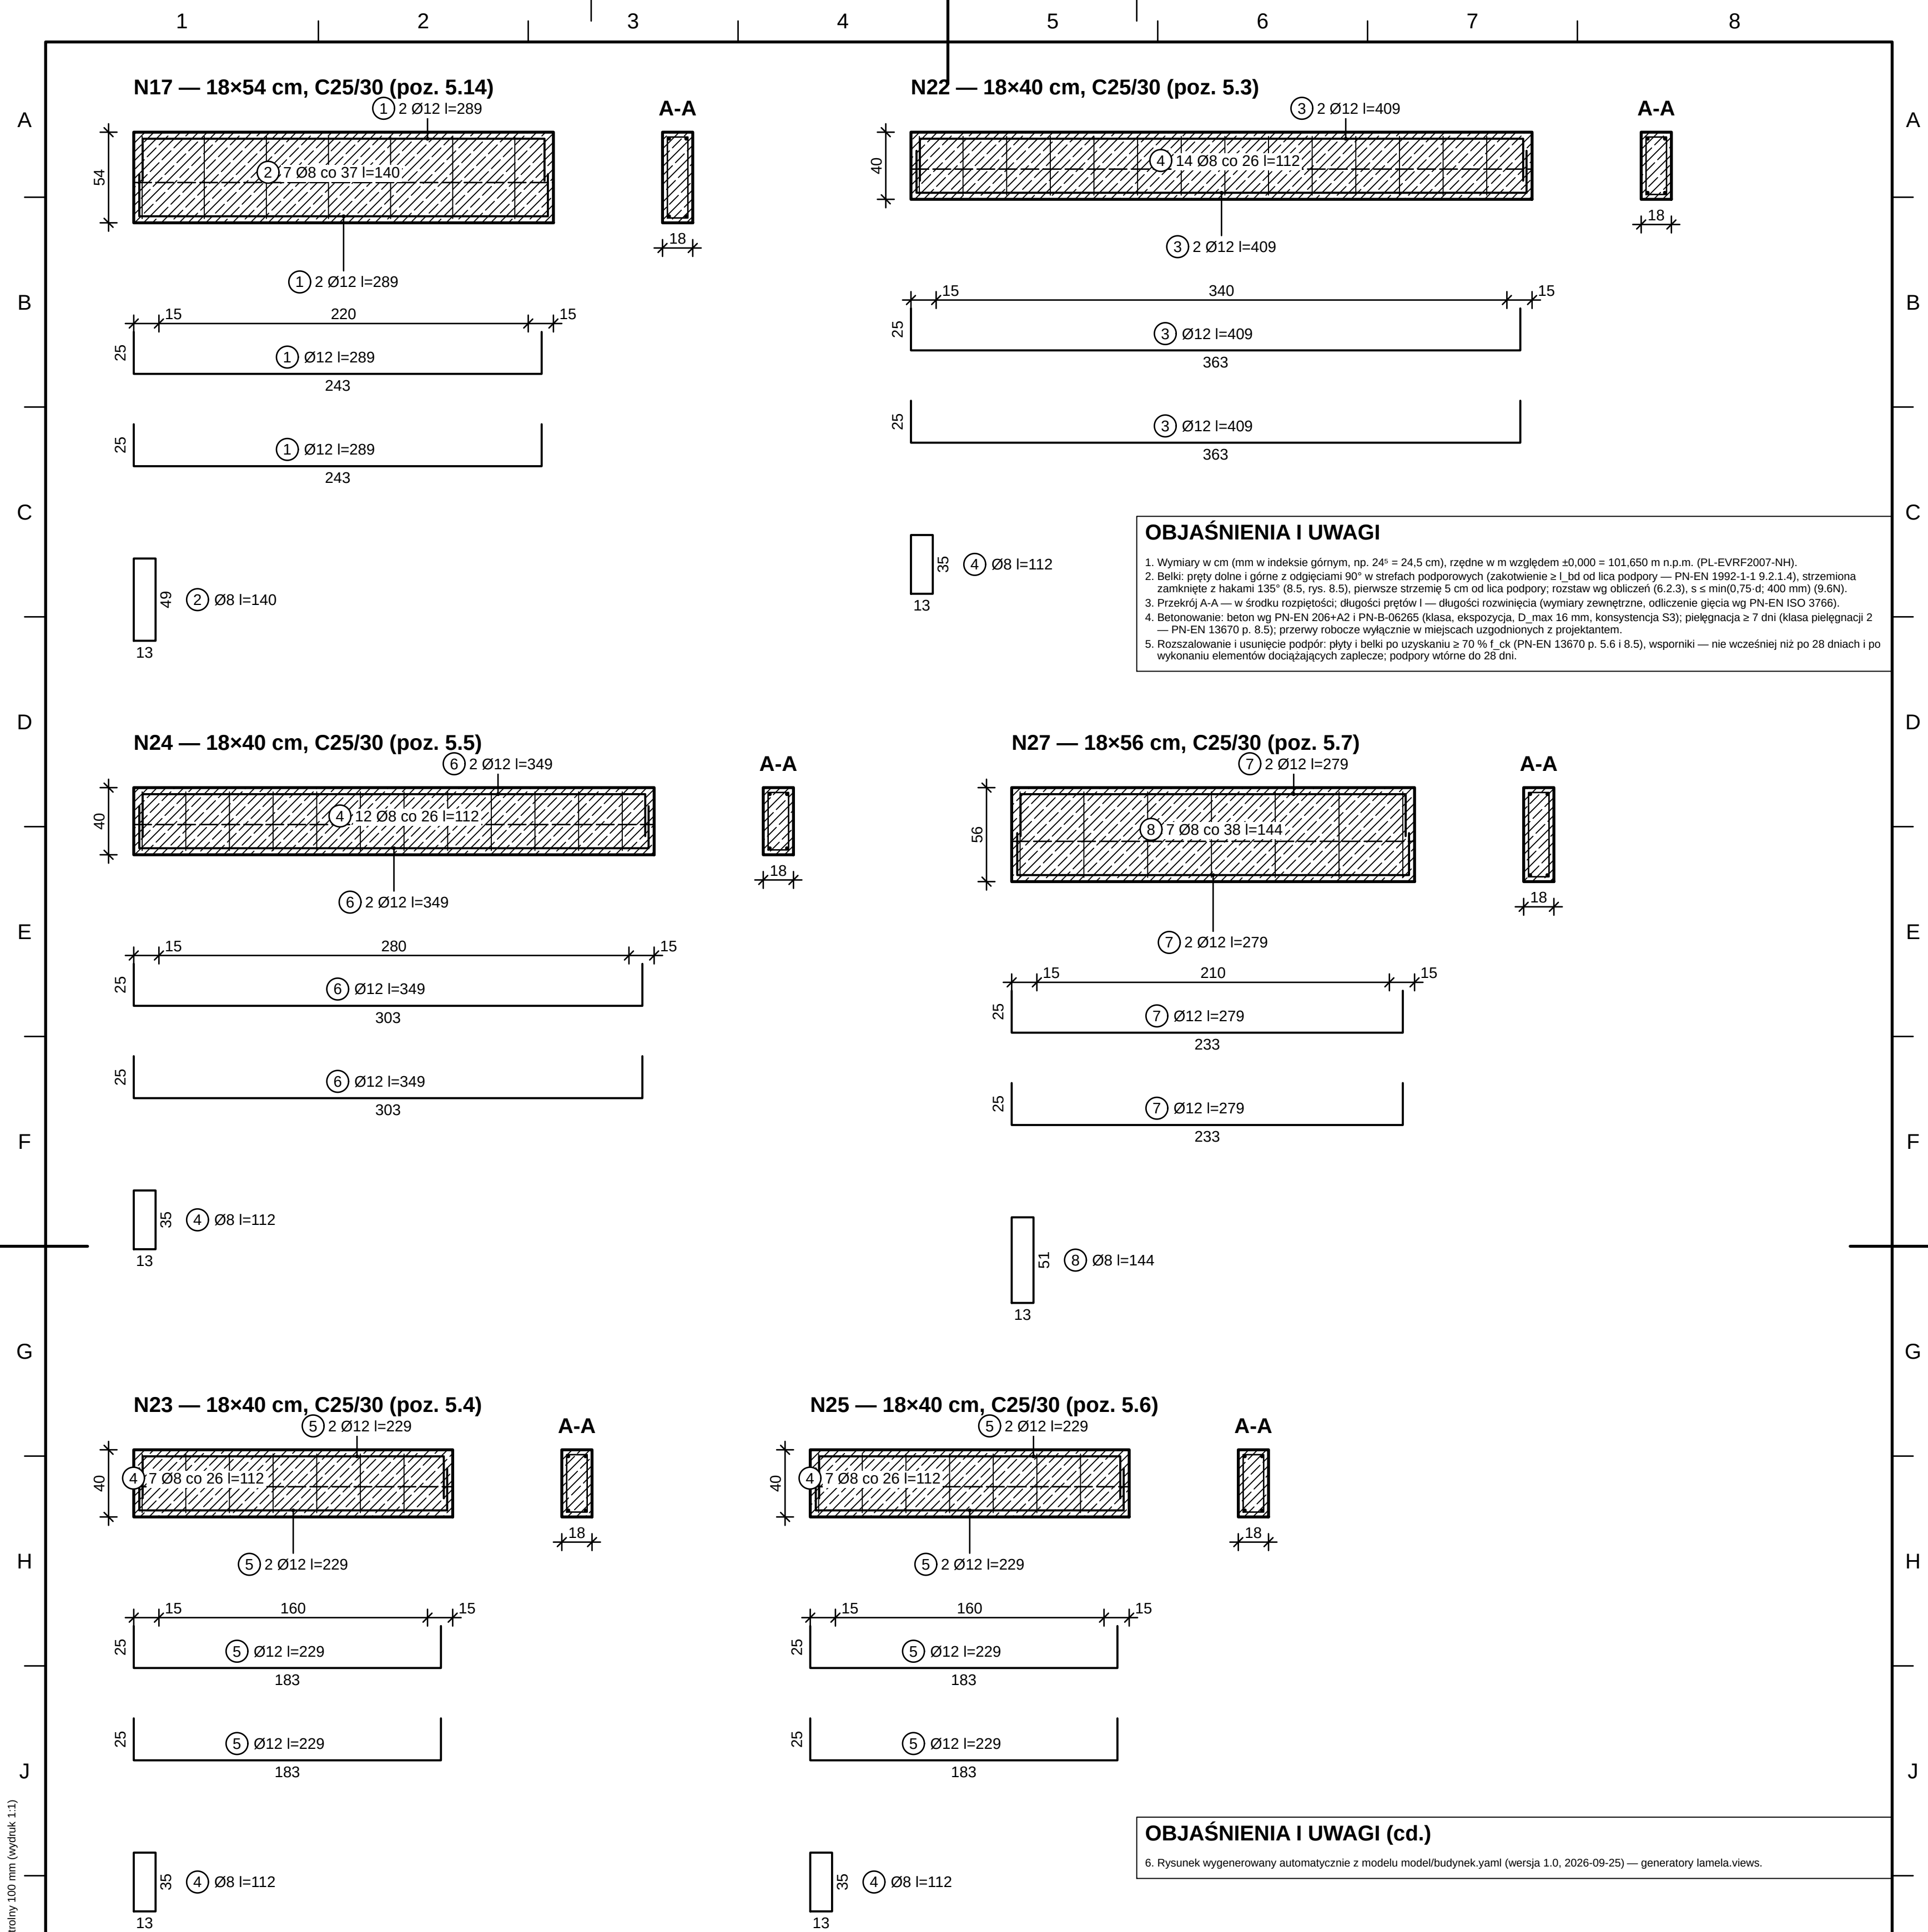

ZBROJENIE BELEK N17, N22, N23, N24, N25, N27 1:25

ZESTAWIENIE STALI

Poz.	Ø [mm]	Kształt ISO 3766, wymiary [cm]	Dłg. [cm]	Liczba [szt.]	Elem.	Ø8 [m]	Ø12 [m]
1	12	 21: a=25 b=243 c=25	289	4	N17		11,56
2	8	 51: a=13 b=49	140	8	N17	11,20	
3	12	 21: a=25 b=363 c=25	409	4	N22		16,36
4	8	 51: a=13 b=35	112	44	N22	49,28	
5	12	 21: a=25 b=183 c=25	229	8	N23		18,32
6	12	 21: a=25 b=303 c=25	349	4	N24		13,96
7	12	 21: a=25 b=233 c=25	279	4	N27		11,16
8	8	 51: a=13 b=51	144	8	N27	11,52	
		Długość całkowita [m]				72,0	71,4
		Masa jednostkowa [kg/m]				0,395	0,888
		Masa [kg]				28,4	63,4
		RAZEM stal B500SP [kg]					91,8


N17, N22, N23, N24, N25, N27: beton C25/30, XC1, otulina strzemion $c_{nom} = 25 \text{ mm}$ (tabl. 4.4N + NA).

OBJAŚNIENIA I UWAGI

1. Wymiary w mm (mm w indeksie górnym, np. 24 × 24,5 cm), rzędne w mm względem $\sigma_{0,000} = 101,650$ mm n.p.m. (PL-EVRF2007-NH).
2. Belki: przety dołki i górne z ugięciem 90° w strefach podporowych (zakotwienie ≥ 1 lub dla podłogi – PN-EN 1992-1-1 9.2.1.4), strzemiona zamknięte z hakami 13/5 (8,5; rys. 8.5), pierwsze strzemie 5 cm od podporów; rozstaw w obliczeniach (6,2,3), $s \leq \min(0,75; d; 400$ mm) (9.6.6).
3. Przekrój A-A – w środku rozpiętości; długości przętów I – długości rozwinęcia (wymiary zewnętrzne, odliczenie gięgi); odległość między przętami – PN-EN ISO 3761.
4. Betonowanie: beton wg PN-EN 206+A2 i PN-B-06265 (klasa, ekspozycja, $D_{\max}$ 16 mm, konsystencja S3); pielęgnacja ≥ 7 dni (klasa pielęgnacji 2 – PN-EN 13670 p. 8.5); przerwy robót wyłączenie w miejscach uzgodnionych z projektantem.
5. Rozszalowanie i usunięcie podpor: płyty i belki po uzyskaniu $\geq 70\%$ f_{ck} (PN-EN 13670 p. 5.6 i 8.5), wsporniki – nie wcześniej niż po 28 dniach i po wykonaniu elementów dociągających zaplecze; podporów wórnó do 28 dni.

OBJAŚNIENIA I UWAGI (cd.)

6. Rysunek wygenerowany automatycznie z modelu model/budynek.yaml (wersja 1.0, 2026-09-25) — generatory lamela.views

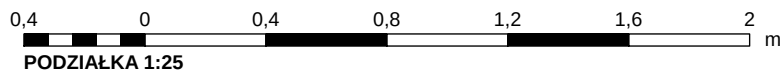

REW.	OPIS ZMIANY	DATA				
0	Wydanie — rysunek wygenerowany z modelu	2026-09-25				
PRACOWNIA PROJEKTOWA PRACOWNIA PROJEKTOWA — nazwa do uzupełnienia adres pracowni do uzupełnienia		STADIUM PT	BRANŻA KONSTRUKCJA (BO)			
INWESTOR (do uzupełnienia)						
OBIEKT / NAZWA ZAMIERZENIA BUDOWLANEGO Budynek mieszkalny jednorodzinny wolnostojący „Dom LAMELA”						
ADRES / LOKALIZACJA (NR DZIAŁKI, OBRĘB, JEDN. EWIDENCYJNA) ul. Lipowa (fikcyjna), dz. nr ewid. 123/4, obręb 0005 Przykładowo, gm. Przykładowo (fikcyjna)			KAT. OBIEKTU I			
FUNKCJA	IMIĘ I NAZWISKO	SPECJALNOŚĆ, NR UPRAWNIENIĆ	DATA	PODPIS		
Projektant						
Projektant (wsp.)						
Sprawdzający						
Opracował						
TYTUŁ RYSUNKU ZBROJENIE BELEK (3)						
SKALA 1:25	FORMAT 470x594	DATA WYDANIA 2026-09-25	RODZAJ DOK. rysunek zbrojenia	NR RYSUNKU PT-BO-22	ARKUSZ 22/26	REW. 0