


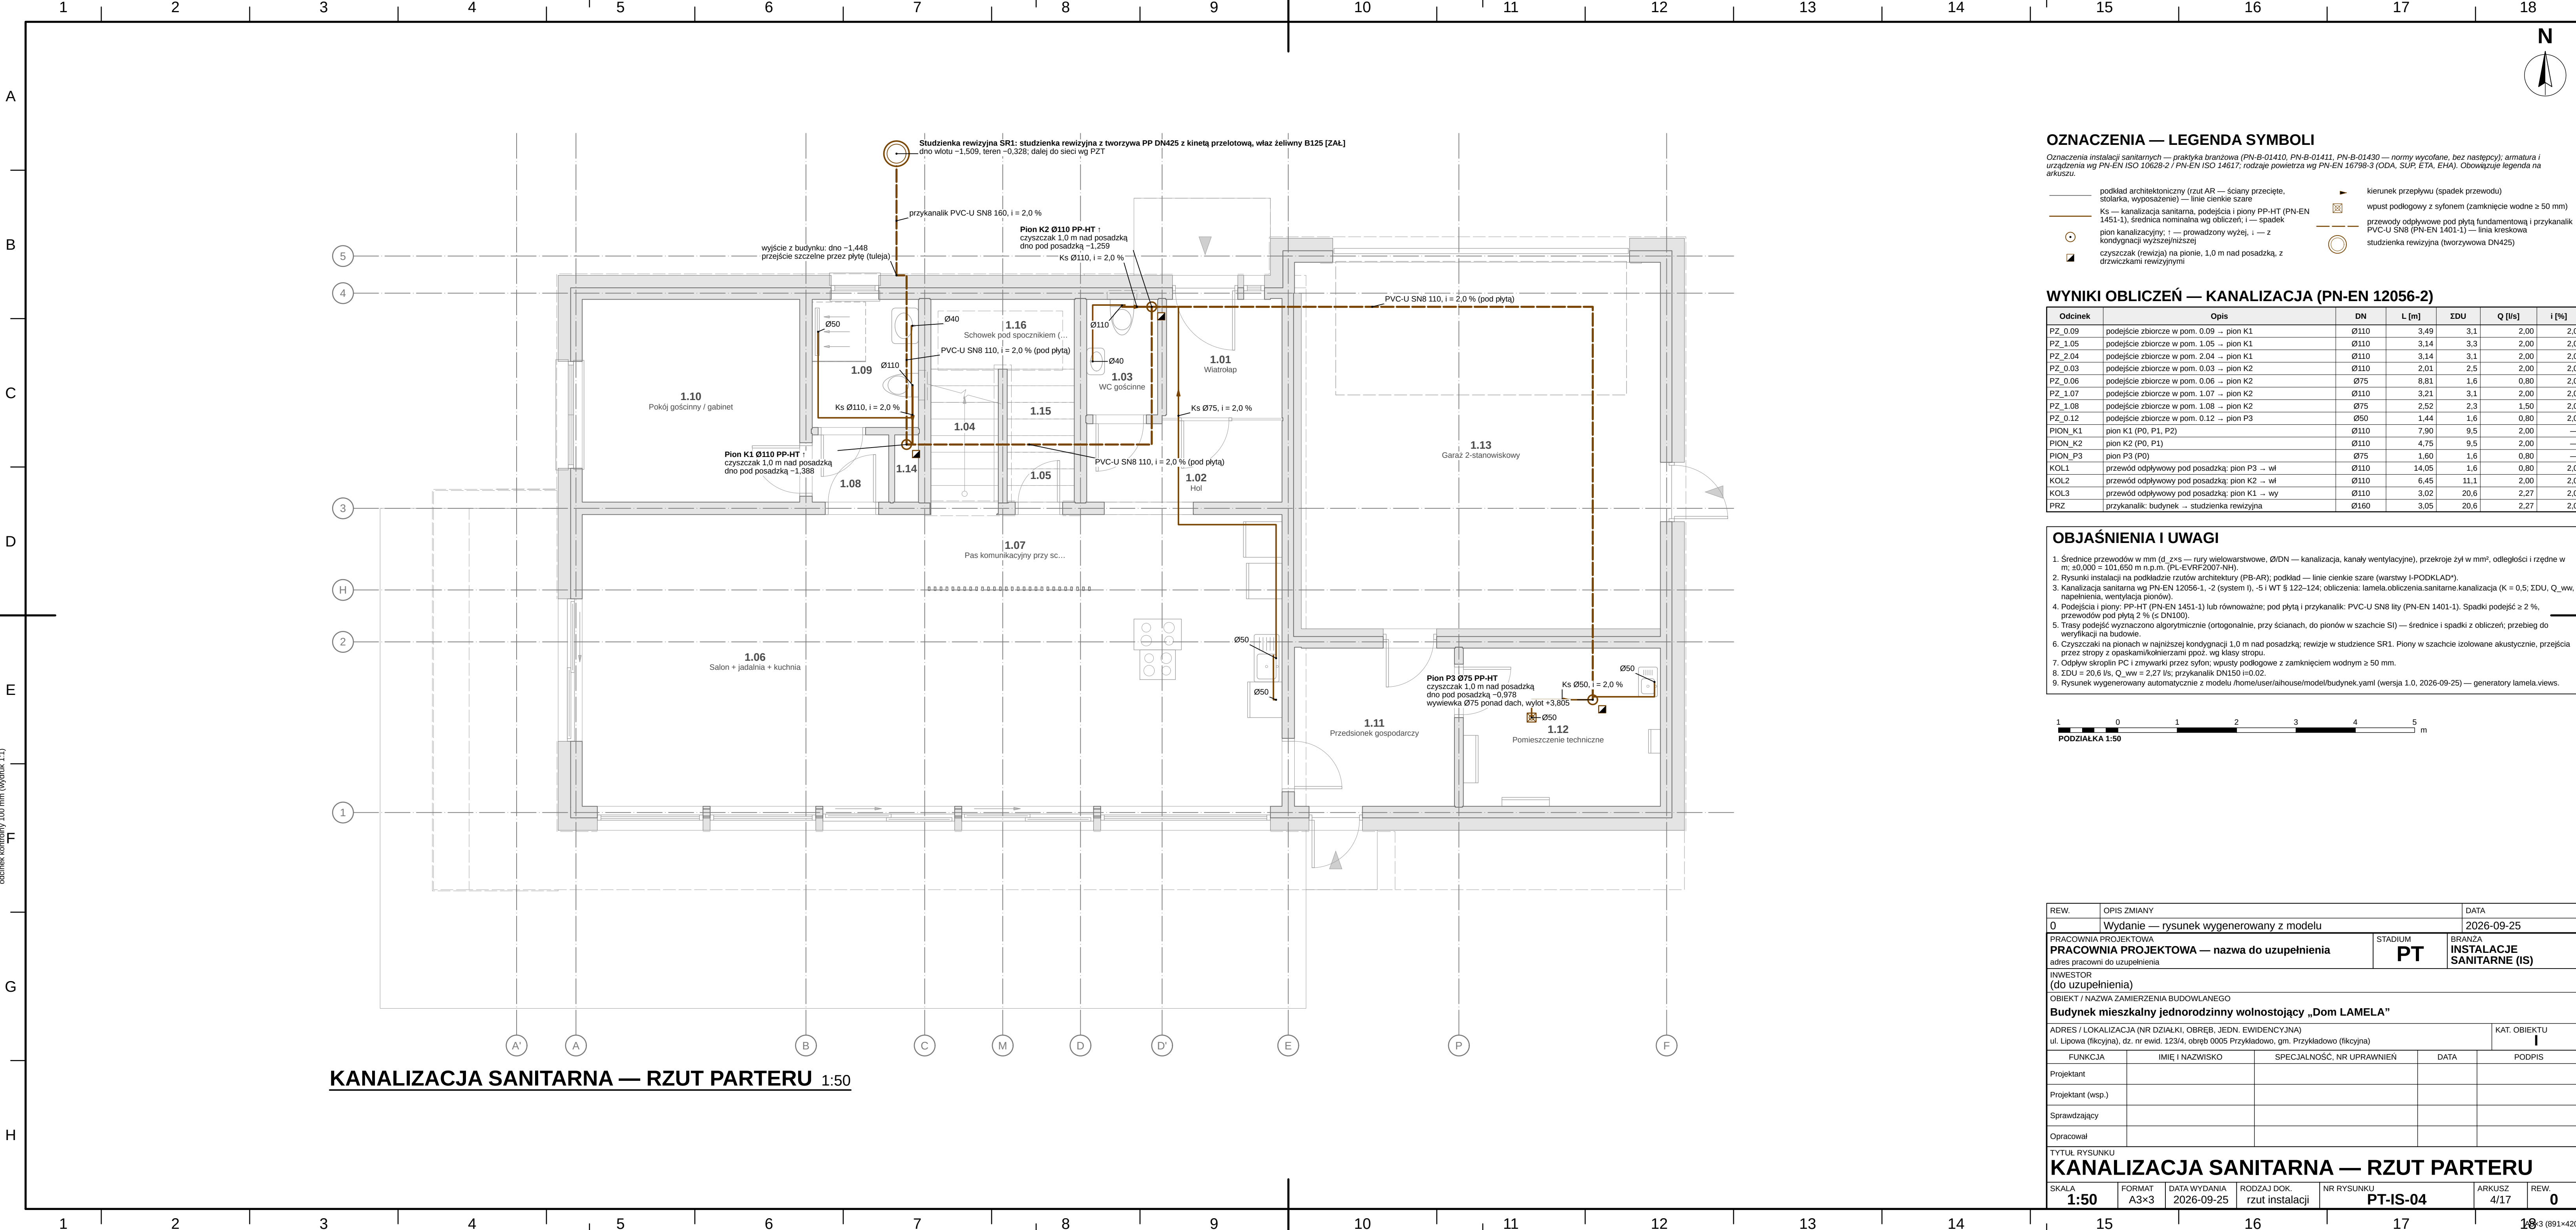

### OZNACZENIA — LEGENDA SYMBOLI

Oznaczenia instalacji sanitarnych — praktyka branżowa (PN-B-01410, PN-B-01411, PN-B-01430 — normy wycofane, bez następcy); amatura i urządzenia wg PN-EN ISO 10628-2 / PN-EN ISO 14617; rodzaje powłoki wg PN-EN 16798-3 (ODA, SUP, ETA, EHA). Obowiązuje legenda na arkuszu.

|   |   |   |                                                                                                   |
|---|---|---|---------------------------------------------------------------------------------------------------|
| — | podkład architektoniczny (rzut AR — ściany przecięte, stolarka, wyposażenie) — linie cienkie szare             | ➔ | kierunek przepływu (spadek przewodu)                                                              |
| — | Ks — kanalizacja sanitarna, podejścia i piony PP-HT (PN-EN 1451-1), średnica nominalna wg obliczeń; i — spadek | ⊠ | wpust podłogowy z syfonem (zamknięcie wodne ≥ 50 mm)                                              |
| ⊙ | pion kanalizacyjny; 1 — prowadzony wyżej, i — z kondygnacji wyższej/niższej                                    | — | przewody odpływowe pod płytą fundamentową i przykanalik PVC-U SN8 (PN-EN 1401-1) — linia kreskowa |
| ■ | czyszczak (rewizja) na pionie, 1,0 m nad posadzką, z drzwiczkami rewizyjnymi                                   | ○ | studzienka rewizyjna (tworzywowa DN425)                                                           |

### WYNIKI OBLICZEŃ — KANALIZACJA (PN-EN 12056-2)

| Odcinek | Opis                                         | DN   | L [m] | ΣDU  | Q [l/s] | i [%] |
|---------|----------------------------------------------|------|-------|------|---------|-------|
| PZ_0.09 | podejście zbiorcze w pom. 0.09 → pion K1     | Ø110 | 3,49  | 3,1  | 2,00    | 2,0   |
| PZ_1.05 | podejście zbiorcze w pom. 1.05 → pion K1     | Ø110 | 3,14  | 3,3  | 2,00    | 2,0   |
| PZ_2.04 | podejście zbiorcze w pom. 2.04 → pion K1     | Ø110 | 3,14  | 3,1  | 2,00    | 2,0   |
| PZ_0.03 | podejście zbiorcze w pom. 0.03 → pion K2     | Ø110 | 2,01  | 2,5  | 2,00    | 2,0   |
| PZ_0.06 | podejście zbiorcze w pom. 0.06 → pion K2     | Ø75  | 8,81  | 1,6  | 0,80    | 2,0   |
| PZ_1.07 | podejście zbiorcze w pom. 1.07 → pion K2     | Ø110 | 3,21  | 3,1  | 2,00    | 2,0   |
| PZ_1.08 | podejście zbiorcze w pom. 1.08 → pion K2     | Ø75  | 2,52  | 2,3  | 1,50    | 2,0   |
| PZ_0.12 | podejście zbiorcze w pom. 0.12 → pion P3     | Ø50  | 1,44  | 1,6  | 0,80    | 2,0   |
| PION_K1 | pion K1 (P0, P1, P2)                         | Ø110 | 7,90  | 9,5  | 2,00    | —     |
| PION_K2 | pion K2 (P0, P1)                             | Ø110 | 4,75  | 9,5  | 2,00    | —     |
| PION_P3 | pion P3 (P0)                                 | Ø75  | 1,60  | 1,6  | 0,80    | —     |
| KOL1    | przewód odpływowy pod posadzką; pion P3 → wł | Ø110 | 14,05 | 1,6  | 0,80    | 2,0   |
| KOL2    | przewód odpływowy pod posadzką; pion K2 → wł | Ø110 | 6,45  | 11,1 | 2,00    | 2,0   |
| KOL3    | przewód odpływowy pod posadzką; pion K1 → wy | Ø110 | 3,02  | 20,6 | 2,27    | 2,0   |
| PRZ     | przykanalik: budynek → studzienka rewizyjna  | Ø160 | 3,05  | 20,6 | 2,27    | 2,0   |

### OBJAŚNIENIA I UWAGI

- Średnice przewodów w mm (d, z×s — rury wielowarstwowe, Ø/DN — kanalizacja, kanały wentylacyjne), przekroje żył w mm², odległości i rzędne w m; ±0,000 = 101,650 m n.p.m. (PL-EVRF2007-AH).
- Rysunki instalacji na podkładzie rzutów architektury (PB-AR); podkład — linie cienkie szare (warstwy I-PODKŁAD).
- Kanalizacja sanitarna wg PN-EN 12056-1, -2 (system I), -5 i WT § 122–124; obliczenia: lamela, obliczenia sanitarne, kanalizacja (K = 0,5; ΣDU, Q<sub>ww</sub>, napelnienia, wentylacja pionów).
- Podejścia i piony: PP-HT (PN-EN 1451-1) lub równoważne; pod płytą i przykanalik: PVC-U SN8 lity (PN-EN 1401-1). Spadki podejść ≥ 2 ‰, przewodów pod płytą 2 ‰ (≤ DN100).
- Trasy podejść wyznaczone algorytmicznie (ortogonalnie, przy ścianach, do pionów w szachcie SI) — średnice i spadki z obliczeń; przebieg do weryfikacji na budowie.
- Czyszczaki na pionach w najniższej kondygnacji 1,0 m nad posadzką; rewizje w studzienkach SR1. Piony w szachcie izolowane akustycznie, przejścia przez stropy z opaskami/kolierzami ppoz. wg klasy stropu.
- Odpływ skroplin PC-1 zmywarki przez syfon; wpusty podłogowe z zamknięciem wodnym ≥ 50 mm.
- ΣDU = 20,6 l/s, Q<sub>ww</sub> = 2,27 l/s; przykanalik DN150 i=0,02.
- Rysunek wygenerowany automatycznie z modelu /home/user/aihouse/model/budynek.yaml (wersja 1.0, 2026-09-25) — generatory lamela.views.

1 0 1 2 3 4 5 m  
PODZIAŁKA 1:50

|   |                |                                         |                                |                                        |                   |           |
|---|----------------|-----------------------------------------|--------------------------------|----------------------------------------|-------------------|-----------|
| REW.   |                | OPIS ZMIANY                             |                                | DATA                                   |                   |           |
| 0   |                | Wydanie — rysunek wygenerowany z modelu |                                | 2026-09-25                             |                   |           |
| PRACOWNIA PROJEKTOWA<br>PRACOWNIA PROJEKTOWA — nazwa do uzupełnienia                                                                                        |                |                                         | STADIUM<br>PT                  | BRANŻA<br>INSTALACJE<br>SANITARNE (IS) |                   |           |
| adres pracowni do uzupełnienia   |                |                                         |                                |                                        |                   |           |
| INWESTOR<br>(do uzupełnienia)   |                |                                         |                                |                                        |                   |           |
| OBIEKT / NAZWA ZAMIERZENIA BUDOWLANEGO<br>Budynek mieszkalny jednorodzinny wolnostojący „Dom LAMELA”                                                        |                |                                         |                                |                                        |                   |           |
| ADRES / LOKALIZACJA (NR DZIAŁKI, OBRĘB, JEDN. EWIDENCYJNA)<br>ul. Lipowa (fikcyjna), dz. nr ewid. 123/4, obręb 0005 Przykładowo, gm. Przykładowo (fikcyjna) |                |                                         |                                |                                        | KAT. OBIEKTU<br>I |           |
| FUNKCJA   |                | IMIĘ I NAZWISKO                         |                                | SPECJALNOŚĆ, NR UPRAWNIENI             | DATA              | PODPIS    |
| Projektant   |                |                                         |                                |                                        |                   |           |
| Projektant (wsp.)   |                |                                         |                                |                                        |                   |           |
| Sprawdzający   |                |                                         |                                |                                        |                   |           |
| Opracował   |                |                                         |                                |                                        |                   |           |
| TYTUŁ RYSUNKU<br>KANALIZACJA SANITARNA — RZUT PARTERU   |                |                                         |                                |                                        |                   |           |
| SKALA<br>1:50   | FORMAT<br>A3×3 | DATA WYDANIA<br>2026-09-25              | RODZAJ DOK.<br>rzut instalacji | NR RYSUNKU<br>PT-IS-04                 | ARKUSZ<br>4/17    | REW.<br>0 |