


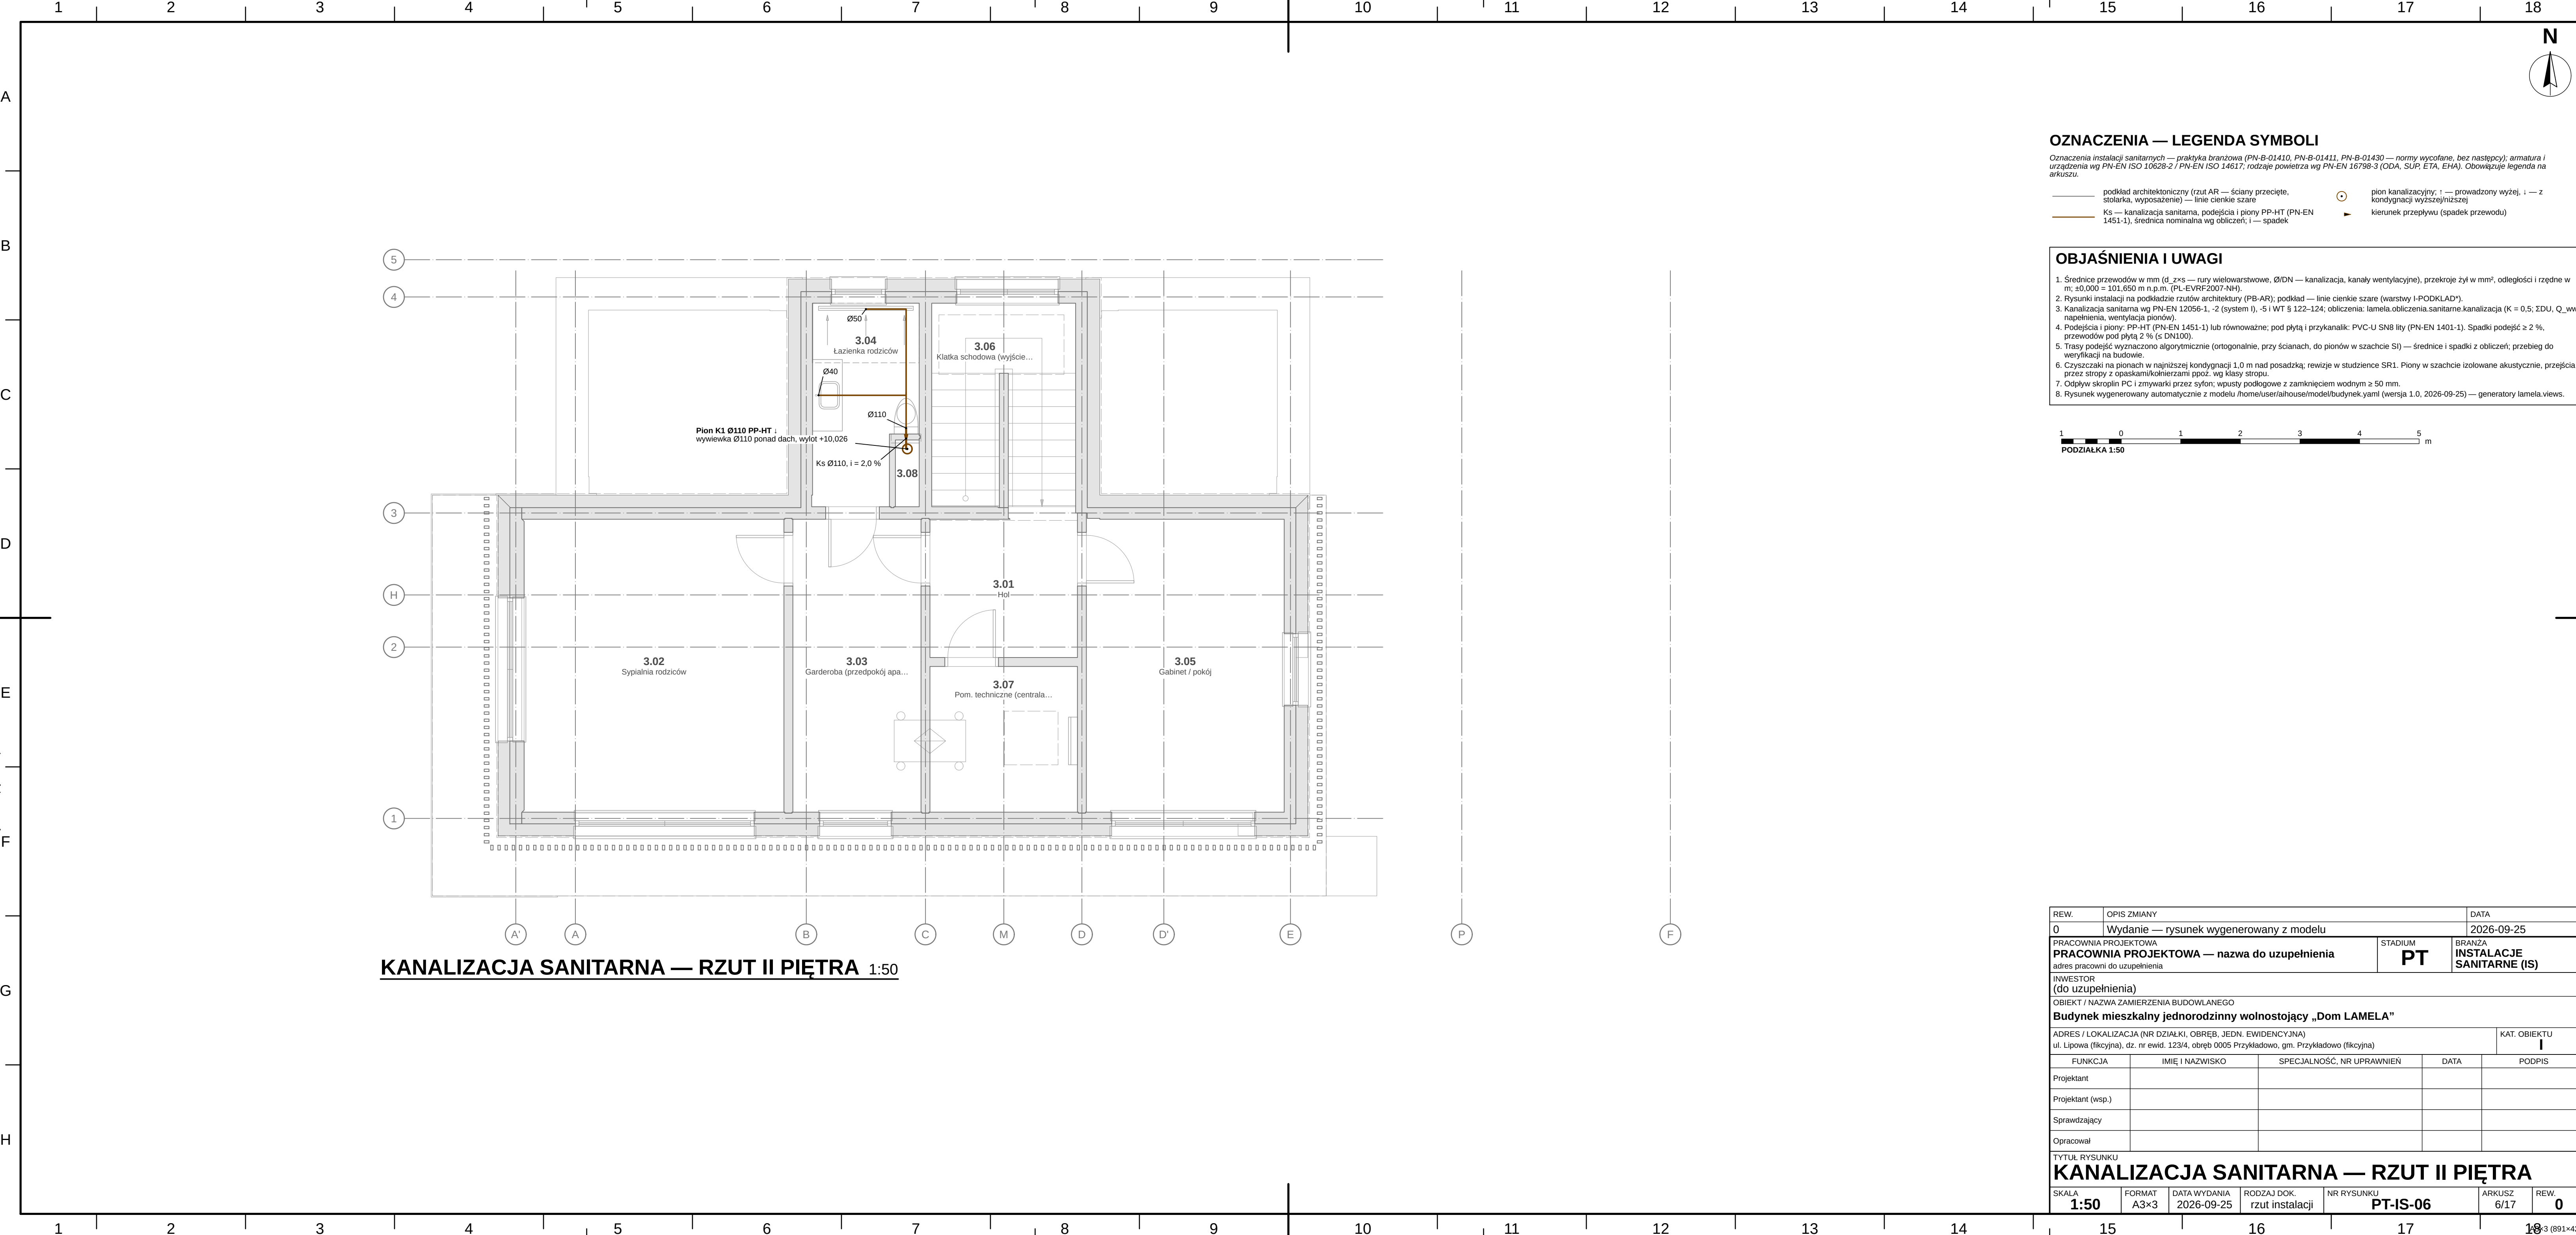


OZNACZENIA — LEGENDA SYMBOLI

Oznaczenia instalacji sanitarnych — praktyka branżowa (PN-B-01410, PN-B-01411, PN-B-01430 — normy wycofane, bez następcy); armatura i urządzenia wg PN-EN ISO 10628-2 / PN-EN ISO 14617; rodzaje powietrza wg PN-EN 16798-3 (ODA, SUP, ETA, EHA). Obowiązuje legenda na arkuszu.

- podkład architektoniczny (rzut AR — ściany przecięte, stolarka, wyposażenie) — linie cienkie szare
- pion kanalizacyjny; ↑ — prowadzony wyżej, ↓ — z kondygnacji wyższej/niższej
- Ks — kanalizacja sanitarna, podejścia i piony PP-HT (PN-EN 1451-1), średnica nominalna wg obliczeń; i — spadek
- kierunek przepływu (spadek przewodu)

OBJAŚNIENIA I UWAGI

- Średnice przewodów w mm (d_z×s — rury wielowarstwowe, Ø/DN — kanalizacja, kanały wentylacyjne), przekroje żył w mm², odległości i rzędne w m; ±0,000 = 101,650 m n.p.m. (PL-EVRF2007-NH).
- Rysunki instalacji na podkładzie rzutów architektury (PB-AR); podkład — linie cienkie szare (warstwy I-PODKŁAD*).
- Kanalizacja sanitarna wg PN-EN 12056-1, -2 (system I), -5 i WT § 122-124; obliczenia: lamela.obliczenia.sanitarna.kanalizacja (K = 0,5; ΣDU, Q_{ww}, napełnienia, wentylacja pionów).
- Podejścia i piony: PP-HT (PN-EN 1451-1) lub równoważne; pod płytą i przykanalik: PVC-U SN8 lity (PN-EN 1401-1). Spadki podejść ≥ 2 ‰, przewodów pod płytą 2 ‰ (≤ DN100).
- Trasy podejść wyznaczone algorytmicznie (ortogonalnie, przy ścianach, do pionów w szachcie SI) — średnice i spadki z obliczeń; przebieg do weryfikacji na budowie.
- Czyszczaki na pionach w najniższej kondygnacji 1,0 m nad posadzką; rewizje w studzience SR1. Piony w szachcie izolowane akustycznie, przejścia przez stropy z opaskami/kolierzami ppóz. wg klasy stropu.
- Odływ skroplin PC i zmywarki przez syfon; wpusty podłogowe z zamknięciem wodnym ≥ 50 mm.
- Rysunek wygenerowany automatycznie z modelu /home/user/ai/house/model/budynek.yaml (wersja 1.0, 2026-09-25) — generatory lamela.views.

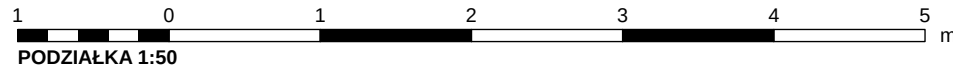

REW.		OPIS ZMIANY		DATA	
0		Wydanie — rysunek wygenerowany z modelu		2026-09-25	
PRACOWNIA PROJEKTOWA PRACOWNIA PROJEKTOWA — nazwa do uzupełnienia adres pracowni do uzupełnienia				STADIUM PT	BRANŻA INSTALACJE SANITARNE (IS)
INWESTOR (do uzupełnienia)					
OBIEKT / NAZWA ZAMIERZENIA BUDOWLANEGO Budynek mieszkalny jednorodzinny wolnostojący „Dom LAMELA”					
ADRES / LOKALIZACJA (NR DZIAŁKI, OBRĘB, JEDN. EWIDENCYJNA) ul. Lipowa (fikcyjna), dz. nr ewid. 123/4, obręb 0005 Przykładowo, gm. Przykładowo (fikcyjna)					KAT. OBIEKTU I
FUNKCJA	IMIĘ I NAZWISKO		SPECJALNOŚĆ, NR UPRAWNIEN	DATA	PODPIS
Projektant					
Projektant (wsp.)					
Sprawdzający					
Opracował					
TYTUŁ RYSUNKU KANALIZACJA SANITARNA — RZUT II PIĘTRA					
SKALA 1:50	FORMAT A3×3	DATA WYDANIA 2026-09-25	RODZAJ DOK. rzut instalacji	NR RYSUNKU PT-IS-06	ARKUSZ 6/17
					REW. 0