


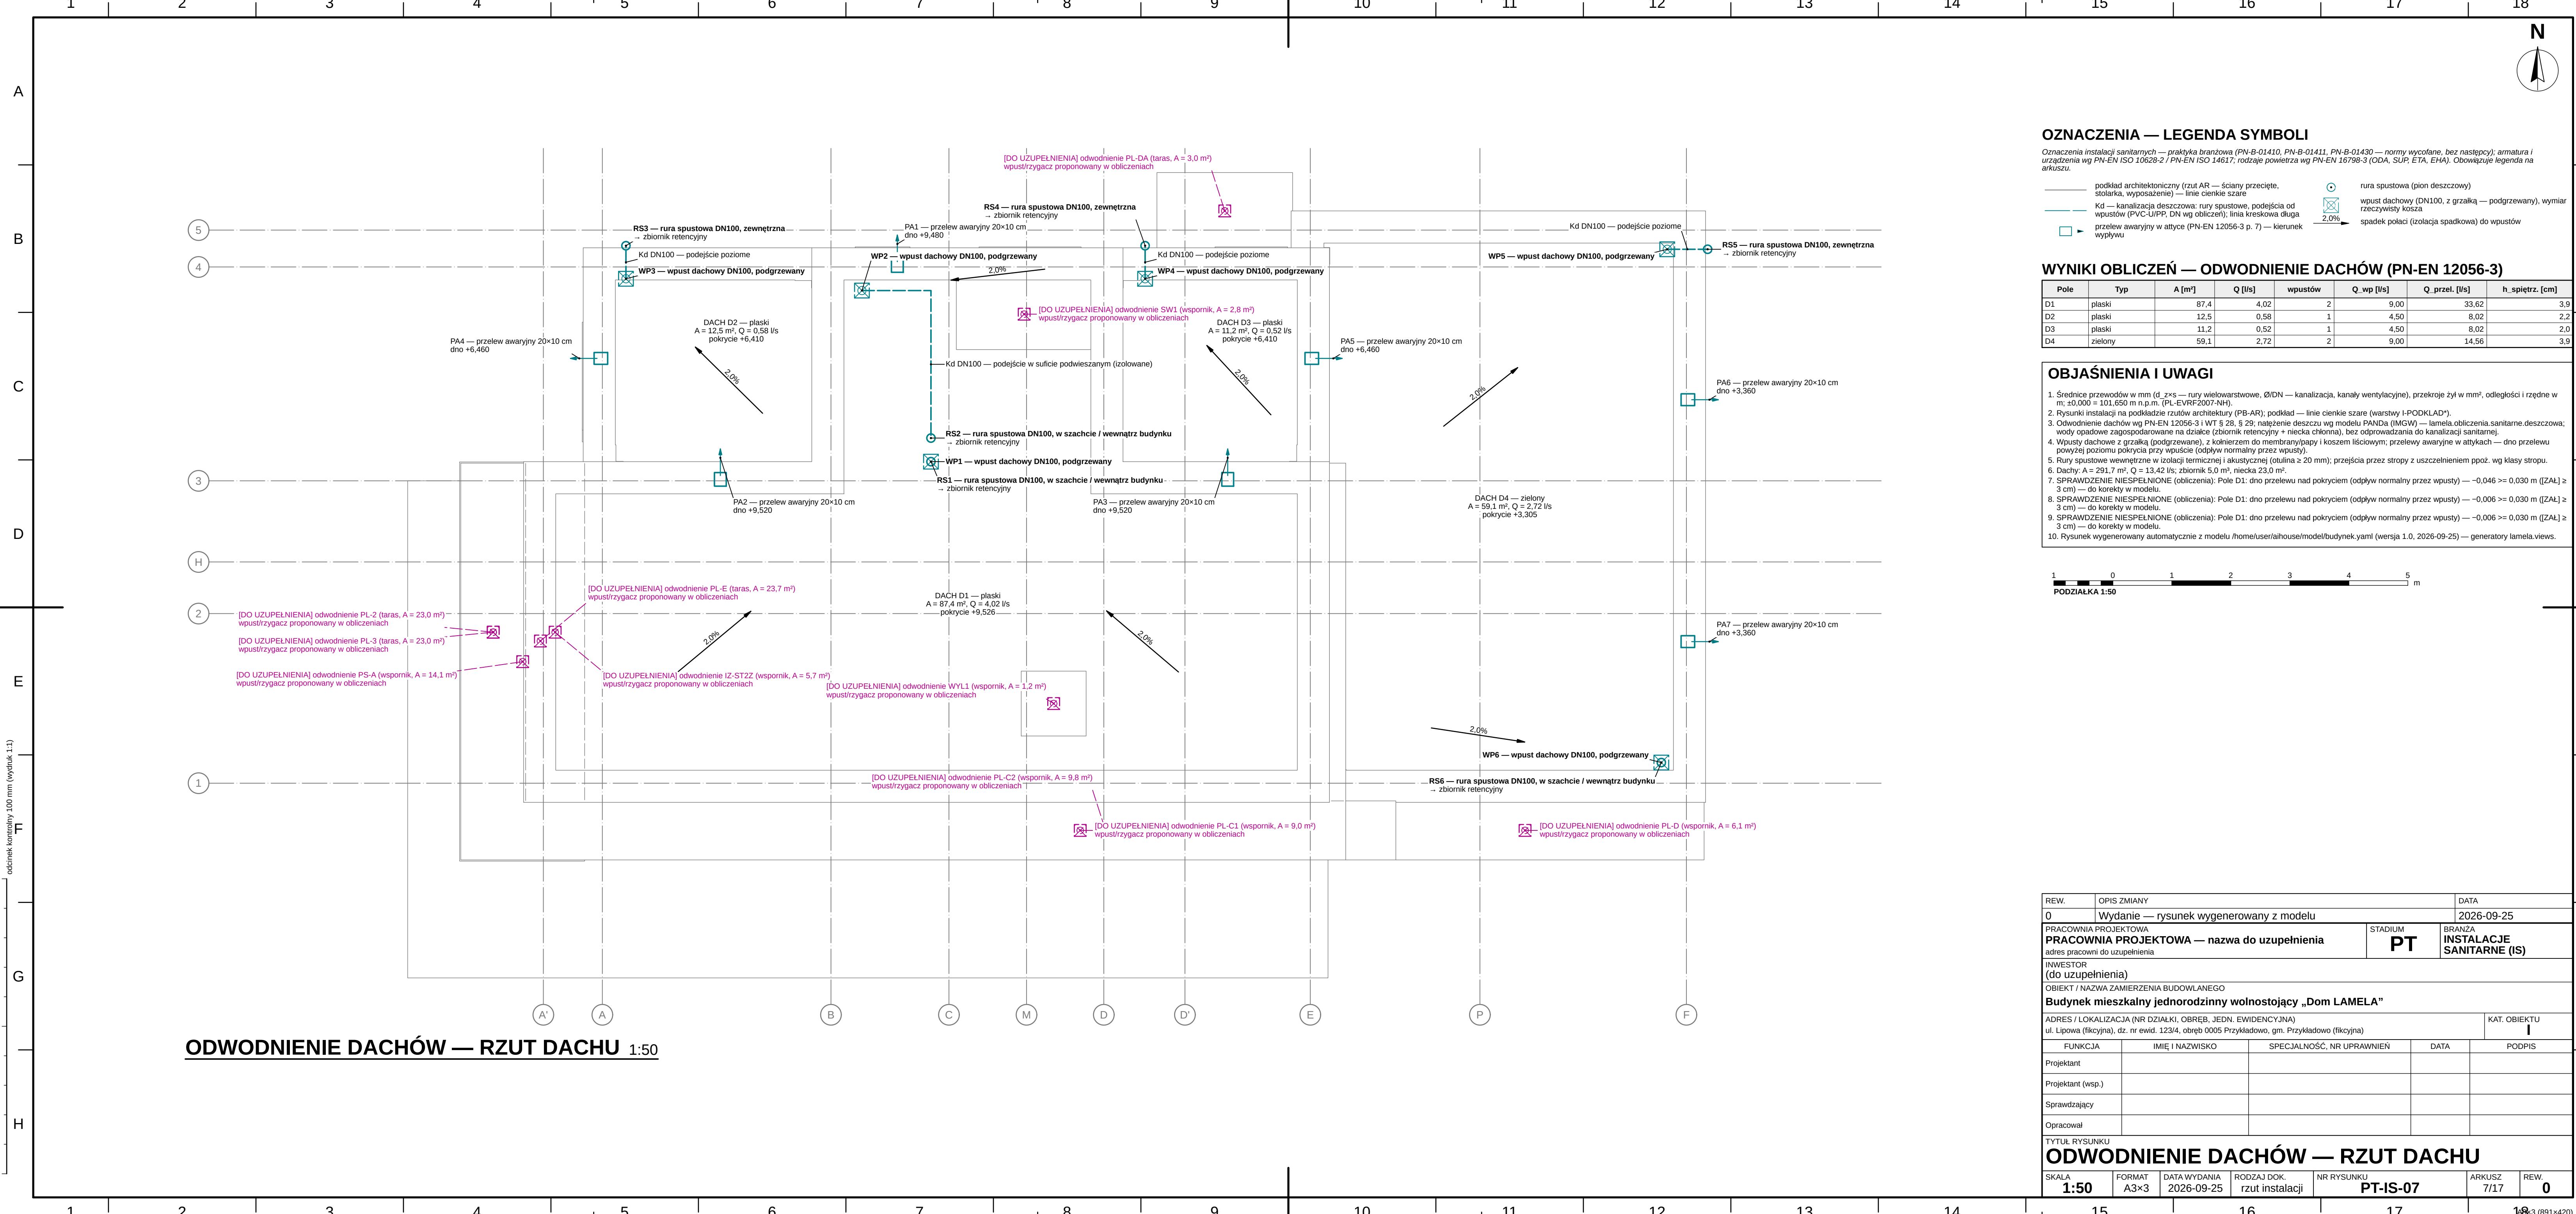

ODWODNIENIE DACHÓW — RZUT DACHU 1:50

OZNACZENIA — LEGENDA SYMBOLI

Oznaczenia instalacji sanitarnych — praktyka branżowa (PN-B-01410, PN-B-01411, PN-B-01430 — normy wycofane, bez następcy); armatura i urządzenia wg PN-EN ISO 10628-2 / PN-EN ISO 14617; rodzaje powietrza wg PN-EN 16798-3 (ODA, SUP, ETA, EHA). Obowiązuje legenda na arkuszu.


|  |   |  |                                                                           |
|--|---|--|---------------------------------------------------------------------------|
|  | podkład architektoniczny (rzut AR) — ściany przecięte, stolarka, wyposażenie) — linie cienkie szare              |  | rura spustowa (pion deszczowy)                                            |
|  | Kd — kanalizacja deszczowa: rury spustowe, podejścia od wpustów (PVC-U/PP, DN wg obliczeń); linia kreskowa długa |  | wpust dachowy (DN100, z grzałką — podgrzewany), wymiar rzeczywisty kossza |
|  | przelew awaryjny w attyce (PN-EN 12056-3 p. 7) — kierunek wypływu                                                |  | spadek połaci (izolacja spadkową) do wpustów                              |

WYNIKI OBLICZEŃ — ODWODNIENIE DACHÓW (PN-EN 12056-3)

| Pole | Typ     | A [m²] | Q [l/s] | wpustów | Q_wp [l/s] | Q_przel. [l/s] | h_spiętrz. [cm] |
|------|---------|--------|---------|---------|------------|----------------|-----------------|
| D1   | plaski  | 87,4   | 4,02    | 2       | 9,00       | 33,62          | 3,9             |
| D2   | plaski  | 12,5   | 0,58    | 1       | 4,50       | 8,02           | 2,2             |
| D3   | plaski  | 11,2   | 0,52    | 1       | 4,50       | 8,02           | 2,0             |
| D4   | zielony | 59,1   | 2,72    | 2       | 9,00       | 14,56          | 3,9             |

OBJAŚNIENIA I UWAGI

- Średnice przewodów w mm (d, z×s — rury wielowarstwowe, Ø/DN — kanalizacja, kanały wentylacyjne), przekroje żył w mm², odległości i rzędne w m; ±0,000 = 101,650 m n.p.m. (PL-EVRF2007-NH).
- Rysunki instalacji na podkładzie rzutów architektury (PB-AR); podkład — linie cienkie szare (warstwy I-PODKŁAD).
- Odwodnienie dachów wg PN-EN 12056-3 i WT 8 28, § 29; natężenie deszczu wg modelu PANDA (IMGW) — lamela.obliczenia.sanitarne.deszczowa; wody opadowe zagospodarowane na działce (zbiornik retencyjny + niecka chłonna), bez odprowadzania do kanalizacji sanitarnej.
- Wpusty dachowe z grzałką (podgrzewane), z kółkiem do membrany/papy i koszem liściowym; przelewy awaryjne w attykach — dno przelewu powyżej poziomu pokrycia przy wpuście (odpływ normalny przez wpusty).
- Rury spustowe wewnętrzne w izolacji termicznej i akustycznej (otulina ≥ 20 mm); przejścia przez stropy z uszczelnieniem ppoż. wg klasy stropu.
- Dachy: A = 291,7 m², Q = 13,42 l/s; zbiornik 5,0 m³, niecka 23,0 m².
- SPRAWDZENIE NIESPEŁNIONE (obliczenia): Pole D1: dno przelewu nad pokryciem (odpływ normalny przez wpusty) — -0,046 >= 0,030 m ([ZAL] ≥ 3 cm) — do korekty w modelu.
- SPRAWDZENIE NIESPEŁNIONE (obliczenia): Pole D1: dno przelewu nad pokryciem (odpływ normalny przez wpusty) — -0,006 >= 0,030 m ([ZAL] ≥ 3 cm) — do korekty w modelu.
- SPRAWDZENIE NIESPEŁNIONE (obliczenia): Pole D1: dno przelewu nad pokryciem (odpływ normalny przez wpusty) — -0,006 >= 0,030 m ([ZAL] ≥ 3 cm) — do korekty w modelu.
- Rysunek wygenerowany automatycznie z modelu /home/user/ai/house/model/budynek.yaml (wersja 1.0, 2026-09-25) — generatory lamela.views.

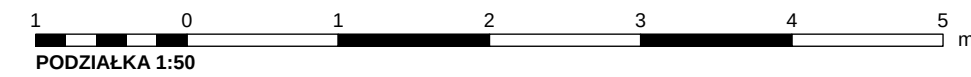

|   |                                         |                                     |
|---|-----------------------------------------|-------------------------------------|
| REW.   | OPIS ZMIANY                             | DATA                                |
| 0   | Wydanie — rysunek wygenerowany z modelu | 2026-09-25                          |
| PRACOWNIA PROJEKTOWA<br>PRACOWNIA PROJEKTOWA — nazwa do uzupełnienia                                                                                        | STADIUM<br>PT                           | BRANŻA<br>INSTALACJE SANITARNE (IS) |
| adres pracowni do uzupełnienia   |                                         |                                     |
| INWESTOR<br>(do uzupełnienia)   |                                         |                                     |
| OBIEKT / NAZWA ZAMIERZENIA BUDOWLANEGO<br>Budynek mieszkalny jednorodzinny wolnostojący „Dom LAMELA”                                                        |                                         |                                     |
| ADRES / LOKALIZACJA (NR DZIAŁKI, OBRĘB, JEDN. EWIDENCYJNA)<br>ul. Lipowa (fikcyjna), dz. nr ewid. 123/4, obręb 0005 Przykładowo, gm. Przykładowo (fikcyjna) | KAT. OBIEKTU<br>I                       |                                     |
| FUNKCJA   | IMIĘ I NAZWISKO                         | SPECJALNOŚĆ, NR UPRAWNIEN           |
| Projektant   |                                         | DATA                                |
| Projektant (wsp.)   |                                         | PODPIS                              |
| Sprawdzający   |                                         |                                     |
| Opracował   |                                         |                                     |
| TYTUŁ RYSUNKU<br>ODWODNIENIE DACHÓW — RZUT DACHU   |                                         |                                     |
| SKALA<br>1:50   | FORMAT<br>A3×3                          | DATA WYDANIA<br>2026-09-25          |
| RODZAJ DOK.<br>rzut instalacji   | NR RYSUNKU<br>PT-IS-07                  | ARKUSZ<br>7/17                      |
| REW.<br>0   |                                         |                                     |