


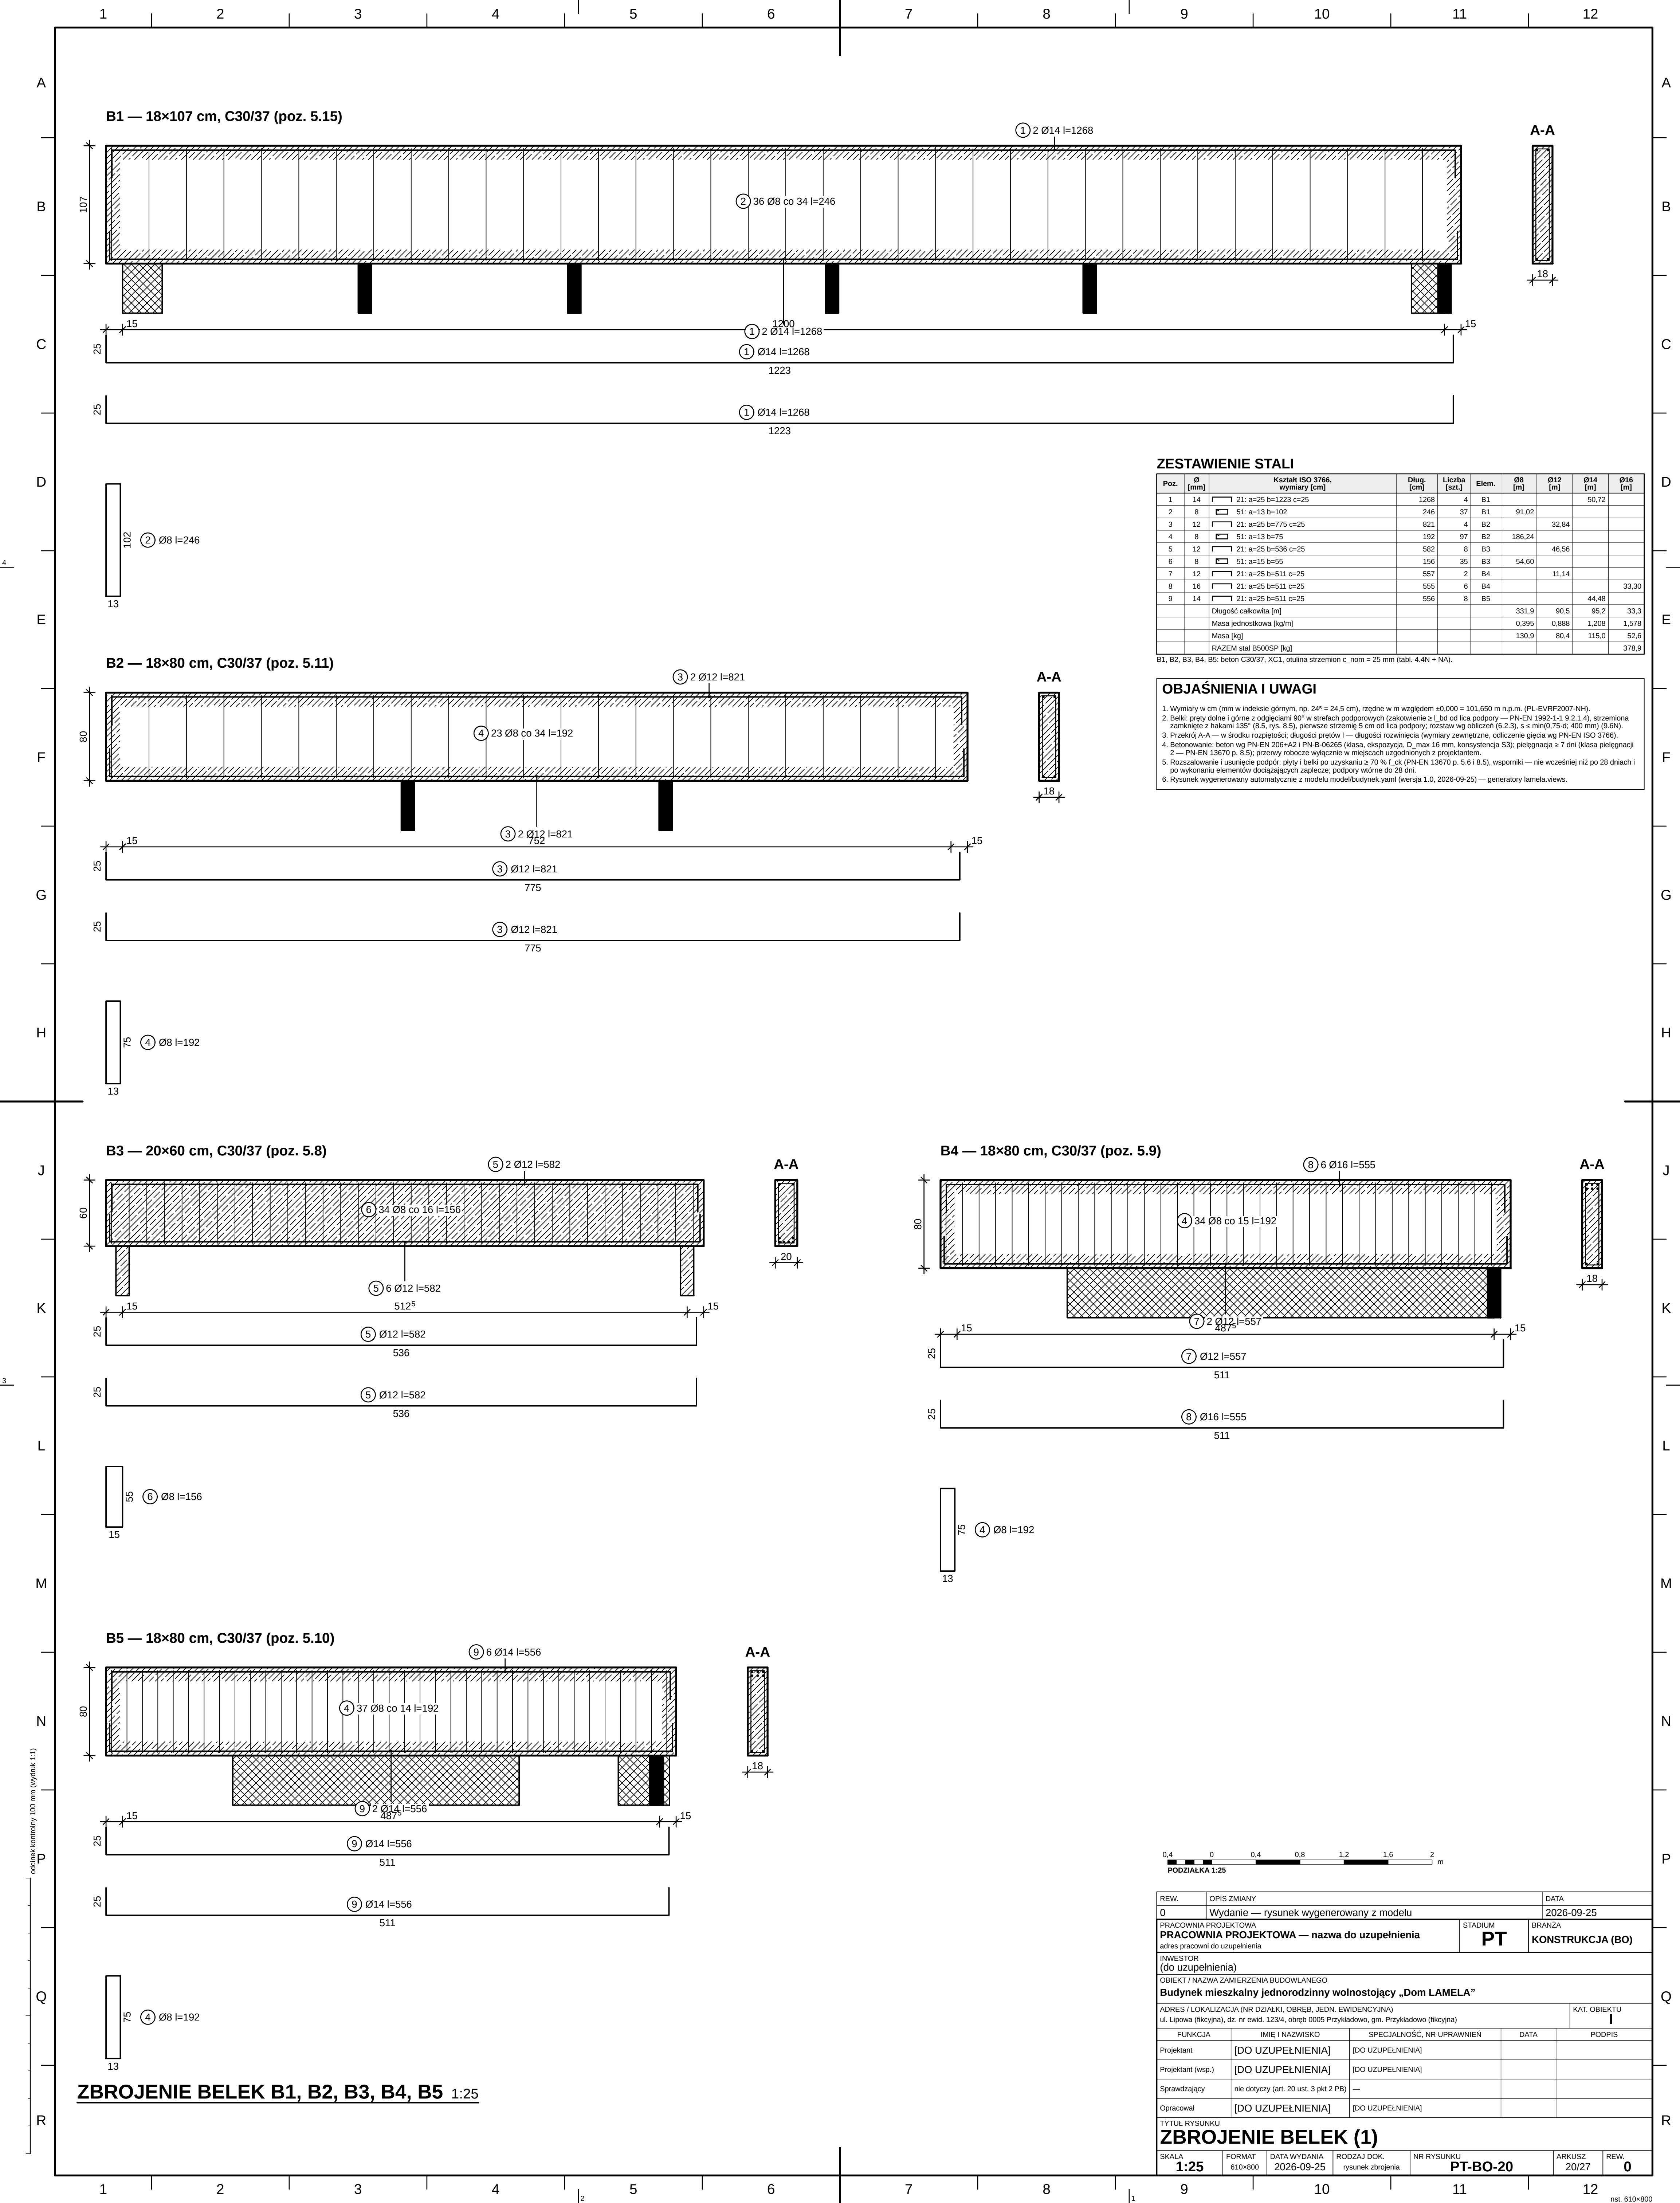

Poz.	Ø [mm]	Kształt ISO 3766, wymiar [cm]	Dług. [cm]	Liczba [szt.]	Elem.	Ø8 [m]	Ø12 [m]	Ø14 [m]	Ø16 [m]
1	14	 21: a=25 b=1223 c=25	1268	4	B1			50,72	
2	8	 51: a=13 b=102	246	37	B1	91,02			
3	12	 21: a=26 b=775 c=25	1221	4	B2		32,84		
4	8	 51: a=13 b=75	192	97	B2	186,24			
5	12	 21: a=25 b=536 c=25	582	8	B3		46,56		
6	8	 51: a=15 b=55	156	35	B3	54,60			
7	12	 21: a=25 b=511 c=25	557	2	B4		11,14		
8	16	 21: a=25 b=511 c=25	555	6	B4				33,30
9	14	 21: a=25 b=511 c=25	556	8	B5			44,48	
Długość całkowita [m]						331,9	90,5	95,2	33,3
Masa jednostkowa [kg/m]						0,395	0,888	1,208	1,578
Masa [kg]						130,9	80,4	115,0	52,6
RAZEM stal B500SP [kg]									378,9

B1, B2, B3, B4, B5: beton C30/37, XC1, otulina strzemion c nom = 25 mm (tabl. 4.4N + NA)

OBJAŚNIENIA I UWAGI

- [illegible]