



SCH1 bieg 1, SCH2 bieg 1 — płyta h = 18 cm, C25/30 (poz. 4.1, 4.2)

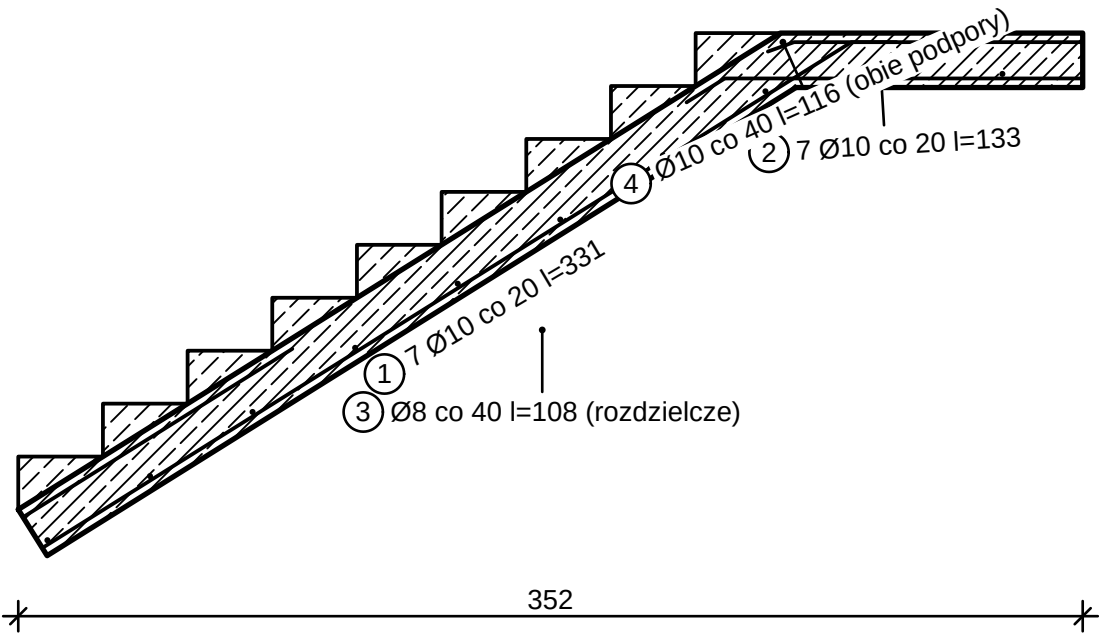

SCH1 bieg 2, SCH2 bieg 2 — płyta h = 18 cm, C25/30 (poz. 4.1, 4.2)

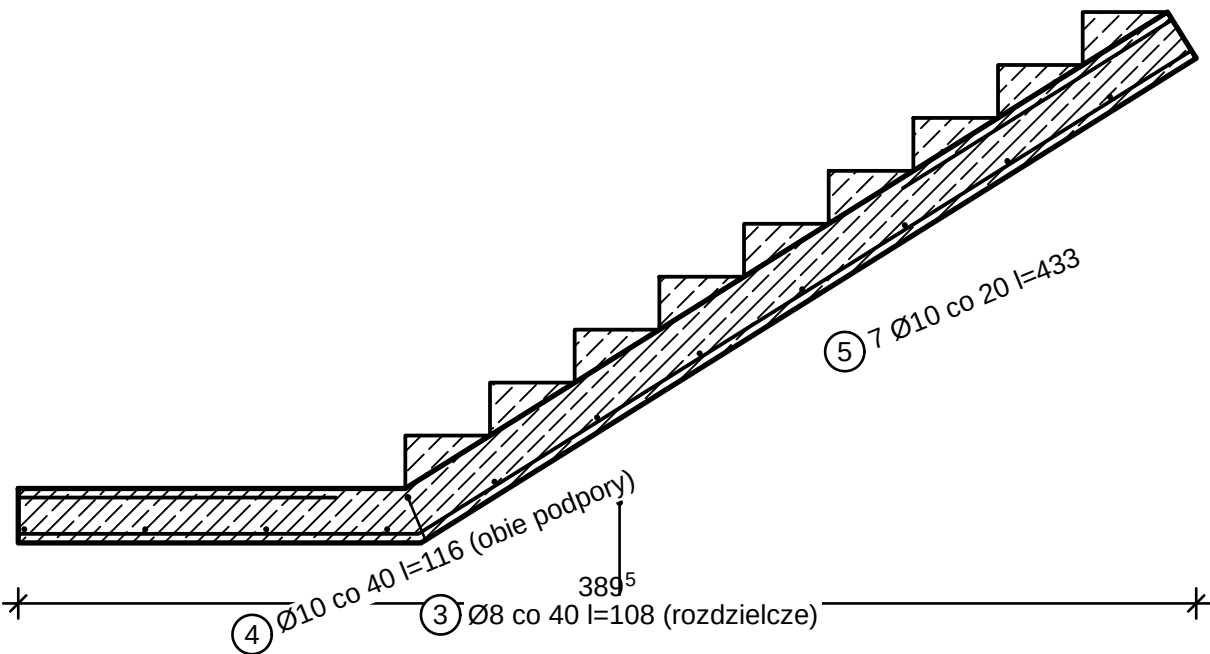

ZBROJENIE SCHODÓW 1:25


ZESTAWIENIE STALI — SCHODY

Poz.	Ø [mm]	Kształt ISO 3766, wymiary [cm]	Dług. [cm]	Liczba [szt.]	Elem.	Ø8 [m]	Ø10 [m]
1	10	26: a=316 b=15	331	14	SCH1/1		46,34
2	10	26: a=15 b=118	133	14	SCH1/1		18,62
3	8	00: a=108	108	34	SCH1/1	36,72	
4	10	11: a=105 b=13	116	24	SCH1/1		27,84
5	10	26: a=132 b=301	433	14	SCH1/2		60,62
		Długość całkowita [m]				36,7	153,4
		Masa jednostkowa [kg/m]				0,395	0,617
		Masa [kg]				14,5	94,6
		RAZEM stal B500SP [kg]					109,1

Beton C25/30, klasa ekspozycji XC1, c_nom = 25 mm; stal B500SP.

OBJAŚNIENIA I UWAGI

- Wymiary w cm (mm w indeksie górnym, np. 24⁵ = 24,5 cm), rzędne w m względem ±0,000 = 101,650 m n.p.m. (PL-EVRF2007-NH).
- Płyty biegów i spoczników monolityczne. Załamanie z narożem wklęsłym od strony rozciąganej (bieg → spocznik górny): pręty dolne NIE są prowadzone po narożu (wypadkowa sił w przecie odpaja otulinę) — dwa pręty proste krzyżujące się, każdy przedłużony za załamanie do krawędzi przeciwległej (strefa ściskana) i zakotwiony tam łącznie ≥ l_{bd} (PN-EN 1992-1-1 8.4.3–8.4.4; zasada jak dla naroży z momentem otwierającym — zał. J.2.3, informacyjny). Załamanie z narożem wypukłym od strony rozciąganej (spocznik dolny → bieg) — pręt odgięty (trzępień wg tabl. 8.1N). Pręty górne przy podporach na 0,25·L (9.3.1.2(2)); stopnie wg projektu architektury.
- Biegi identyczne geometrycznie i obliczeniowo przedstawiono jednym rysunkiem (lista w tytule); liczby sztuk w zestawieniu — łącznie.
- Betonowanie: beton wg PN-EN 206+A2 i PN-B-06265 (klasa, ekspozycja, D_{max} 16 mm, konsystencja S3); pielęgnacja ≥ 7 dni (klasa pielęgnacji 2 — PN-EN 13670 p. 8.5); przerwy robocze wyłącznie w miejscach uzgodnionych z projektantem.
- Rozszalowanie i usunięcie podpór: płyty i belki po uzyskaniu ≥ 70 % f_{ck} (PN-EN 13670 p. 5.6 i 8.5), wsporniki — nie wcześniej niż po 28 dniach i po wykonaniu elementów dociążających zaplecze; podpory wtórne do 28 dni.
- Rysunek wygenerowany automatycznie z modelu model/budynek.yaml (wersja 1.0, 2026-09-25) — generatory lamela.views.

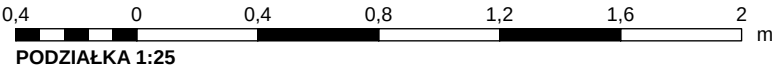

REW.	OPIS ZMIANY			DATA	
0	Wydanie — rysunek wygenerowany z modelu			2026-09-25	
PRACOWNIA PROJEKTOWA PRACOWNIA PROJEKTOWA — nazwa do uzupełnienia adres pracowni do uzupełnienia			STADIUM PT	BRANŻA KONSTRUKCJA (BO)	
INWESTOR (do uzupełnienia)					
OBIEKT / NAZWA ZAMIERZENIA BUDOWLANEGO Budynek mieszkalny jednorodzinny wolnostojący „Dom LAMELA”					
ADRES / LOKALIZACJA (NR DZIAŁKI, OBRĘB, JEDN. EWIDENCYJNA) ul. Lipowa (fikcyjna), dz. nr ewid. 123/4, obręb 0005 Przykładowo, gm. Przykładowo (fikcyjna)				KAT. OBIEKTU I	
FUNKCJA	IMIĘ I NAZWISKO	SPECJALNOŚĆ, NR UPRAWNIENI	DATA	PODPIS	
Projektant	[DO UZUPEŁNIENIA]	[DO UZUPEŁNIENIA]			
Projektant (wsp.)	[DO UZUPEŁNIENIA]	[DO UZUPEŁNIENIA]			
Sprawdzający	nie dotyczy (art. 20 ust. 3 pkt 2 PB)	—			
Opracował	[DO UZUPEŁNIENIA]	[DO UZUPEŁNIENIA]			
TYTUŁ RYSUNKU ZBROJENIE SCHODÓW					
SKALA 1:25	FORMAT 400×297	DATA WYDANIA 2026-09-25	RODZAJ DOK. rysunek zbrojenia	NR RYSUNKU PT-BO-26	ARKUSZ 26/27
					REW. 0