



odcinek kontroli 100 mm (wydruk 1:1)


ZBROJENIE SŁUPÓW ŻELBETOWYCH W MURZE 1:25

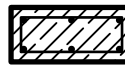


A-A

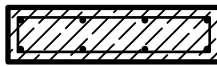

A-A

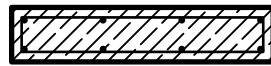


A-A

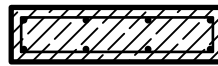


A-A



A-A

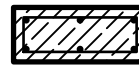

A-A

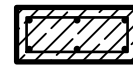

A-A

OBJAŚNIENIA I UWAGI

- Wymiary w cm (mm w indeksie górnym, np. 24⁵ = 24,5 cm), rzędne w m względem ±0,000 = 101,650 m n.p.m. (PL-EVRF2007-NH).
- Słupy żelbetowe w murze (trzpienie) w węzłach obciążeń skupionych — wymiarowanie: obliczenia statyczne, poz. 8 (ściskanie mimośrodowe z efektami II rzędu — metoda nominalnej krzywizny, PN-EN 1992-1-1 5.8.8).
- Strzemiona zagęszczone (0,6-s) na długości z większego wymiaru przekroju przy głowicy i podstawie (9.5.3(4)); pręty podłużne w narożach strzemion (9.5.3(6)).
- Słupy o tym samym przekroju, zbrojeniu i wysokości — jeden rysunek (lista w tytule); liczby sztuk w zestawieniu łącznie.
- Rysunek wygenerowany automatycznie z modelu model/budynek.yaml (wersja 1.0, 2026-09-25) — generatory lamela.views.


OZNACZENIA NA RYSUNKU

- pręt podłużny (widok), linia gruba — z zakładem/zakotwieniem poza obrysem słupa
- ③ numer pozycji pręta (zestawienie stali)
- — — przekrój A-A: strzemię (linia), pręty podłużne (punkty)

ZESTAWIENIE STALI — SŁUPY ŻB

Poz.	Ø [mm]	Kształt ISO 3766, wymiary [cm]	Dług. [cm]	Liczba [szt.]	Elem.	Ø6 [m]	Ø12 [m]
1	12	00: a=353	353	54	SL9		190,62
2	6	51: a=34 b=12	106	125	SL9	132,50	
3	6	51: a=64 b=12	166	126	SL13	209,16	
4	12	00: a=325	325	30	SL16		97,50
5	6	51: a=80 b=12	198	68	SL16	134,64	
6	6	51: a=24 b=12	86	22	SL19	18,92	
7	6	51: a=38 b=12	114	28	SL20	31,92	
8	12	00: a=268	268	6	SL21		16,08
Długość całkowita [m]						527,1	304,2
Masa jednostkowa [kg/m]						0,222	0,888
Masa [kg]						117,0	270,1
RAZEM stal B500SP [kg]							387,1

Beton C30/37, XC1, c_{nom} = 30 mm; stal B500SP. Trzpienie betonowane po wymurowaniu ścian (strzemia muru, kotwy stalowe co 2 warstwy) lub w szalunku przed murowaniem; pręty podłużne ciągłe przez wieniec/belkę (zakład l₀ ≥ 50φ), zakotwione w pogrubieniu płyty fundamentowej (l₀ bd).

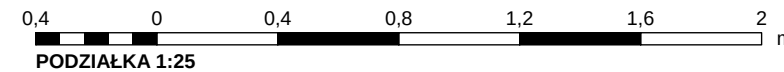

REW.	OPIS ZMIANY			DATA	
0	Wydanie — rysunek wygenerowany z modelu			2026-09-25	
PRACOWNIA PROJEKTOWA PRACOWNIA PROJEKTOWA — nazwa do uzupełnienia adres pracowni do uzupełnienia			STADIUM PT	BRANŻA KONSTRUKCJA (BO)	
INWESTOR (do uzupełnienia)					
OBIEKT / NAZWA ZAMIERZENIA BUDOWLANEGO Budynek mieszkalny jednorodzinny wolnostojący „Dom LAMELA”					
ADRES / LOKALIZACJA (NR DZIAŁKI, OBRĘB, JEDN. EWIDENCYJNA) ul. Lipowa (fikcyjna), dz. nr ewid. 123/4, obręb 0005 Przykładowo, gm. Przykładowo (fikcyjna)				KAT. OBIEKTU I	
FUNKCJA	IMIĘ I NAZWISKO	SPECJALNOŚĆ, NR UPRAWNIEŃ		DATA	PODPIS
Projektant	[DO UZUPEŁNIENIA]	[DO UZUPEŁNIENIA]			
Projektant (wsp.)	[DO UZUPEŁNIENIA]	[DO UZUPEŁNIENIA]			
Sprawdzający	nie dotyczy (art. 20 ust. 3 pkt 2 PB)	—			
Opracował	[DO UZUPEŁNIENIA]	[DO UZUPEŁNIENIA]			
TYTUŁ RYSUNKU ZBROJENIE SŁUPÓW ŻELBETOWYCH W MURZE					
SKALA 1:25	FORMAT 870×297	DATA WYDANIA 2026-09-25	RODZAJ DOK. rysunek zbrojenia	NR RYSUNKU PT-BO-27	ARKUSZ 27/27
					REW. 0