


RZUT II PIĘTRA 1:50

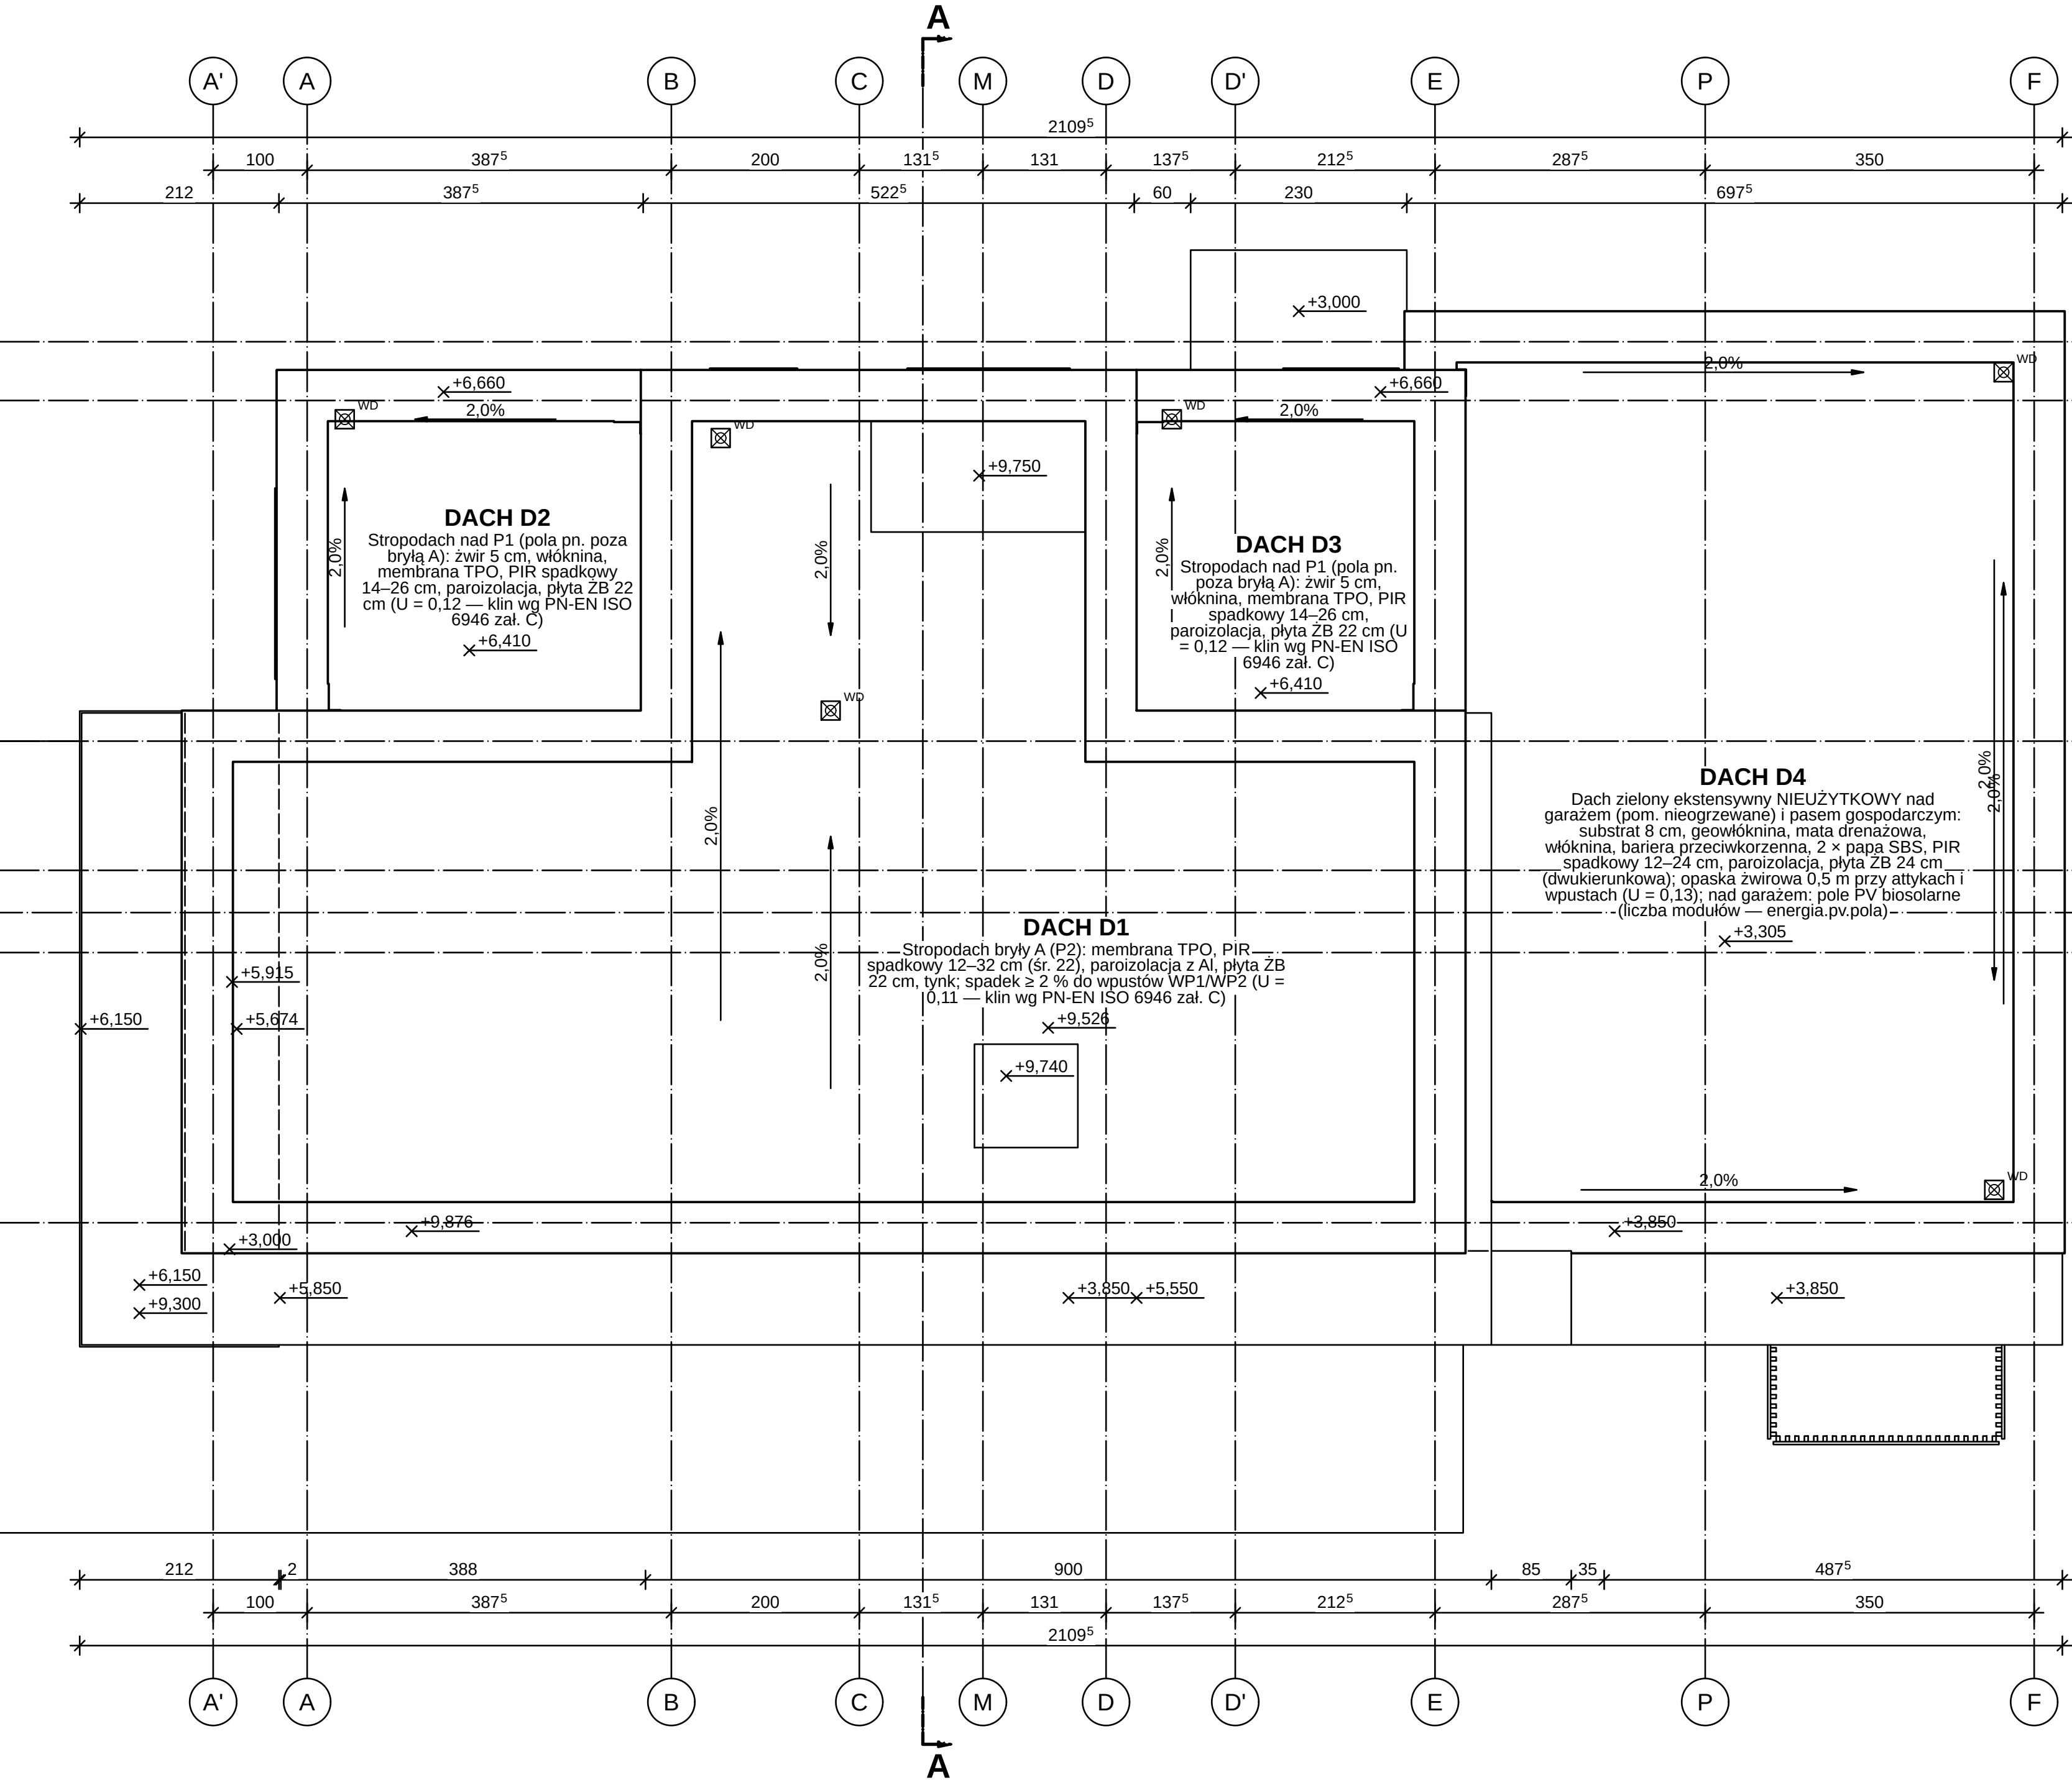

RZUT DACHU 1:50

OZNACZENIA MATERIAŁÓW (PN-B-01030 + przyjęte)

	Włna mineralna 035 (szkielet, docieplenia, ściana dom-garaz); Włna mineralna: fasadowa (elewacja wentylowana bryły A, A1) — meander, UUU
	Błoczek wapniowo-piaskowy 12 cm, kl. 15 (ścianki działowe, bocowy w klatce); Błoczek wapniowo-piaskowy (silikat) 18 cm, kl. 20, gr. 1, na zaprawie cienkowarstwowej — kralka ukośna 45°/135°
	Styropian grafityowy EPS 031 (ETICS, NRO w systemie) — zygtrak, VVV
	Membrana tefasadowa wiatrozolacyjna UV-stabilna, czarna (sd = 0,02 m)

OBJAŚNIENIA I UWAGI

- Wymiary w cm (mm w indeksie górnym, np. 24° = 24,5 cm), rzędne w m względem ±0,000 = 101,650 m n.p.m. (PL-EVRF2007-NH).
- Rzuty: płaszczyzna cięcia +1,10 m nad posadzką kondygnacji. Linia kreślowa — elementy nad płaszczyzną cięcia (obryszy płyt i wsporników, brył wyższych kondygnacji, otwory w stropie nad, belki); linia cienka — elementy poniżej (widok).
- Otwory: licznik — szerokość, mianownik — wysokość w świetle muru, w nawiasie wysokość parapetu; symbol stolarki wg zestawienia stolarki.
- Numeracja pomieszczeń wg PN-B-01025 / PN-EN ISO 4157-2: <nr> kondygnacji (parter = 1) <nr>; identyfikator w modelu: <kond> <nr> (parter = 0).
- Drzwi: strona otwierania (lewo/prawo) wg modelu — patrz: od strony, w którą otwiera się skrzydło.
- Rysunek projektu technicznego (RPB § 24 pkt 1) wykonany z tego samego stanu modelu co rysunki PB-AR-xx projektu architektoniczno-budowlanego (tom I); stan modelu: SHA-256 42ac7a811873 (budynek, działka, instalacje, wyposażenie).
- Układ warstw przegrod, stolarki, wykończenia, odprowadzenie — części opisane PT-1 AR, wepły — detale PT-AR-D.
- Rysunek wygenerowany automatycznie z modelu modelbudynek.yaml (wersja 1.0, 2025-09-25) — generatory lamela.views.

1 0 1 2 3 4 5 m
PODZIAŁKA 1:50

ZESTAWIENIE POMIESZCZEŃ

Nr	Nazwa pomieszczenia	Posadzka	Kat.	Wys. [m]	Pow. [m²]
3.02	Sypialnia rodziców	Deska warstwowa dębowa 15 mm, klejona	podst.	2,77	21,43
3.05	Gabinet / pokój gościnny okazjonalny	Deska warstwowa dębowa 15 mm, klejona	podst.	2,77	16,25
3.03	Garderoba (przedpokój apartamentu)	Deska warstwowa dębowa 15 mm, klejona	pomoc.	2,77	10,49
3.07	Pom. techniczne (centrala rekuperacyjna, wylaz na dach)	Płyty gresowe 60x120 na kleju CZ2E \$1 techn.		2,77	5,90
3.01	Hol	Deska warstwowa dębowa 15 mm, klejona	ruchu	2,77	5,74
3.04	Łazienka rodziców	Płytki gresowe 60x120 na kleju CZ2E \$1 techn.		2,77	5,51
3.06	Szacht instalacyjny SI		techn.	2,77	0,45
3.08	Klatka schodowa (wyjście z biegu 2, pustka)	Deska warstwowa dębowa 15 mm, klejona	ruchu	2,77	0,24
RAZEM powierzchnia netto					66,01
w tym podstawowa + pomocnicza					53,67

REW.	OPIS ZMIANY	DATA
0	Wydanie — rysunek wygenerowany z modelu	2026-09-25
PRACOWNIA PROJEKTOWA ul. Lipowa (fikcyjna), dz. nr ewid. 123/4, obręb 0005 Przykładowo, gm. Przykładowo (fikcyjna)		STADIUM PT
PRACOWNIA PROJEKTOWA — nazwa do uzupełnienia		BRANŻA ARCHITEKTURA (AR)
INWESTOR (do uzupełnienia)		
OBIEKT / NAZWA ZAMIERZENIA BUDOWLANEGO Budynek mieszkalny jednorodzinny wolnostojący „Dom LAMELA”		
ADRES / LOKALIZACJA (NR DZIAŁKI, OBRĘB, JEDN. EWIDENCYJNA)		KAT. OBIEKTU I
FUNKCJA		
Projektant	[DO UZUPEŁNIENIA]	[DO UZUPEŁNIENIA]
Projektant (wsp.)	[DO UZUPEŁNIENIA]	[DO UZUPEŁNIENIA]
Sprawdzający	nie dotyczy (art. 20 ust. 3 pkt 2 PB)	—
Opracował	[DO UZUPEŁNIENIA]	[DO UZUPEŁNIENIA]
TYTUŁ RYSUNKU RZUT II PIĘTRA I RZUT DACHU		
SKALA 1:50	FORMAT 590x891	DATA WYDANIA 2026-09-25
RODZAJ DOK. RZUT	NR RYSUNKU PT-AR-03	ARKUSZ 3/5
REW.	0	