



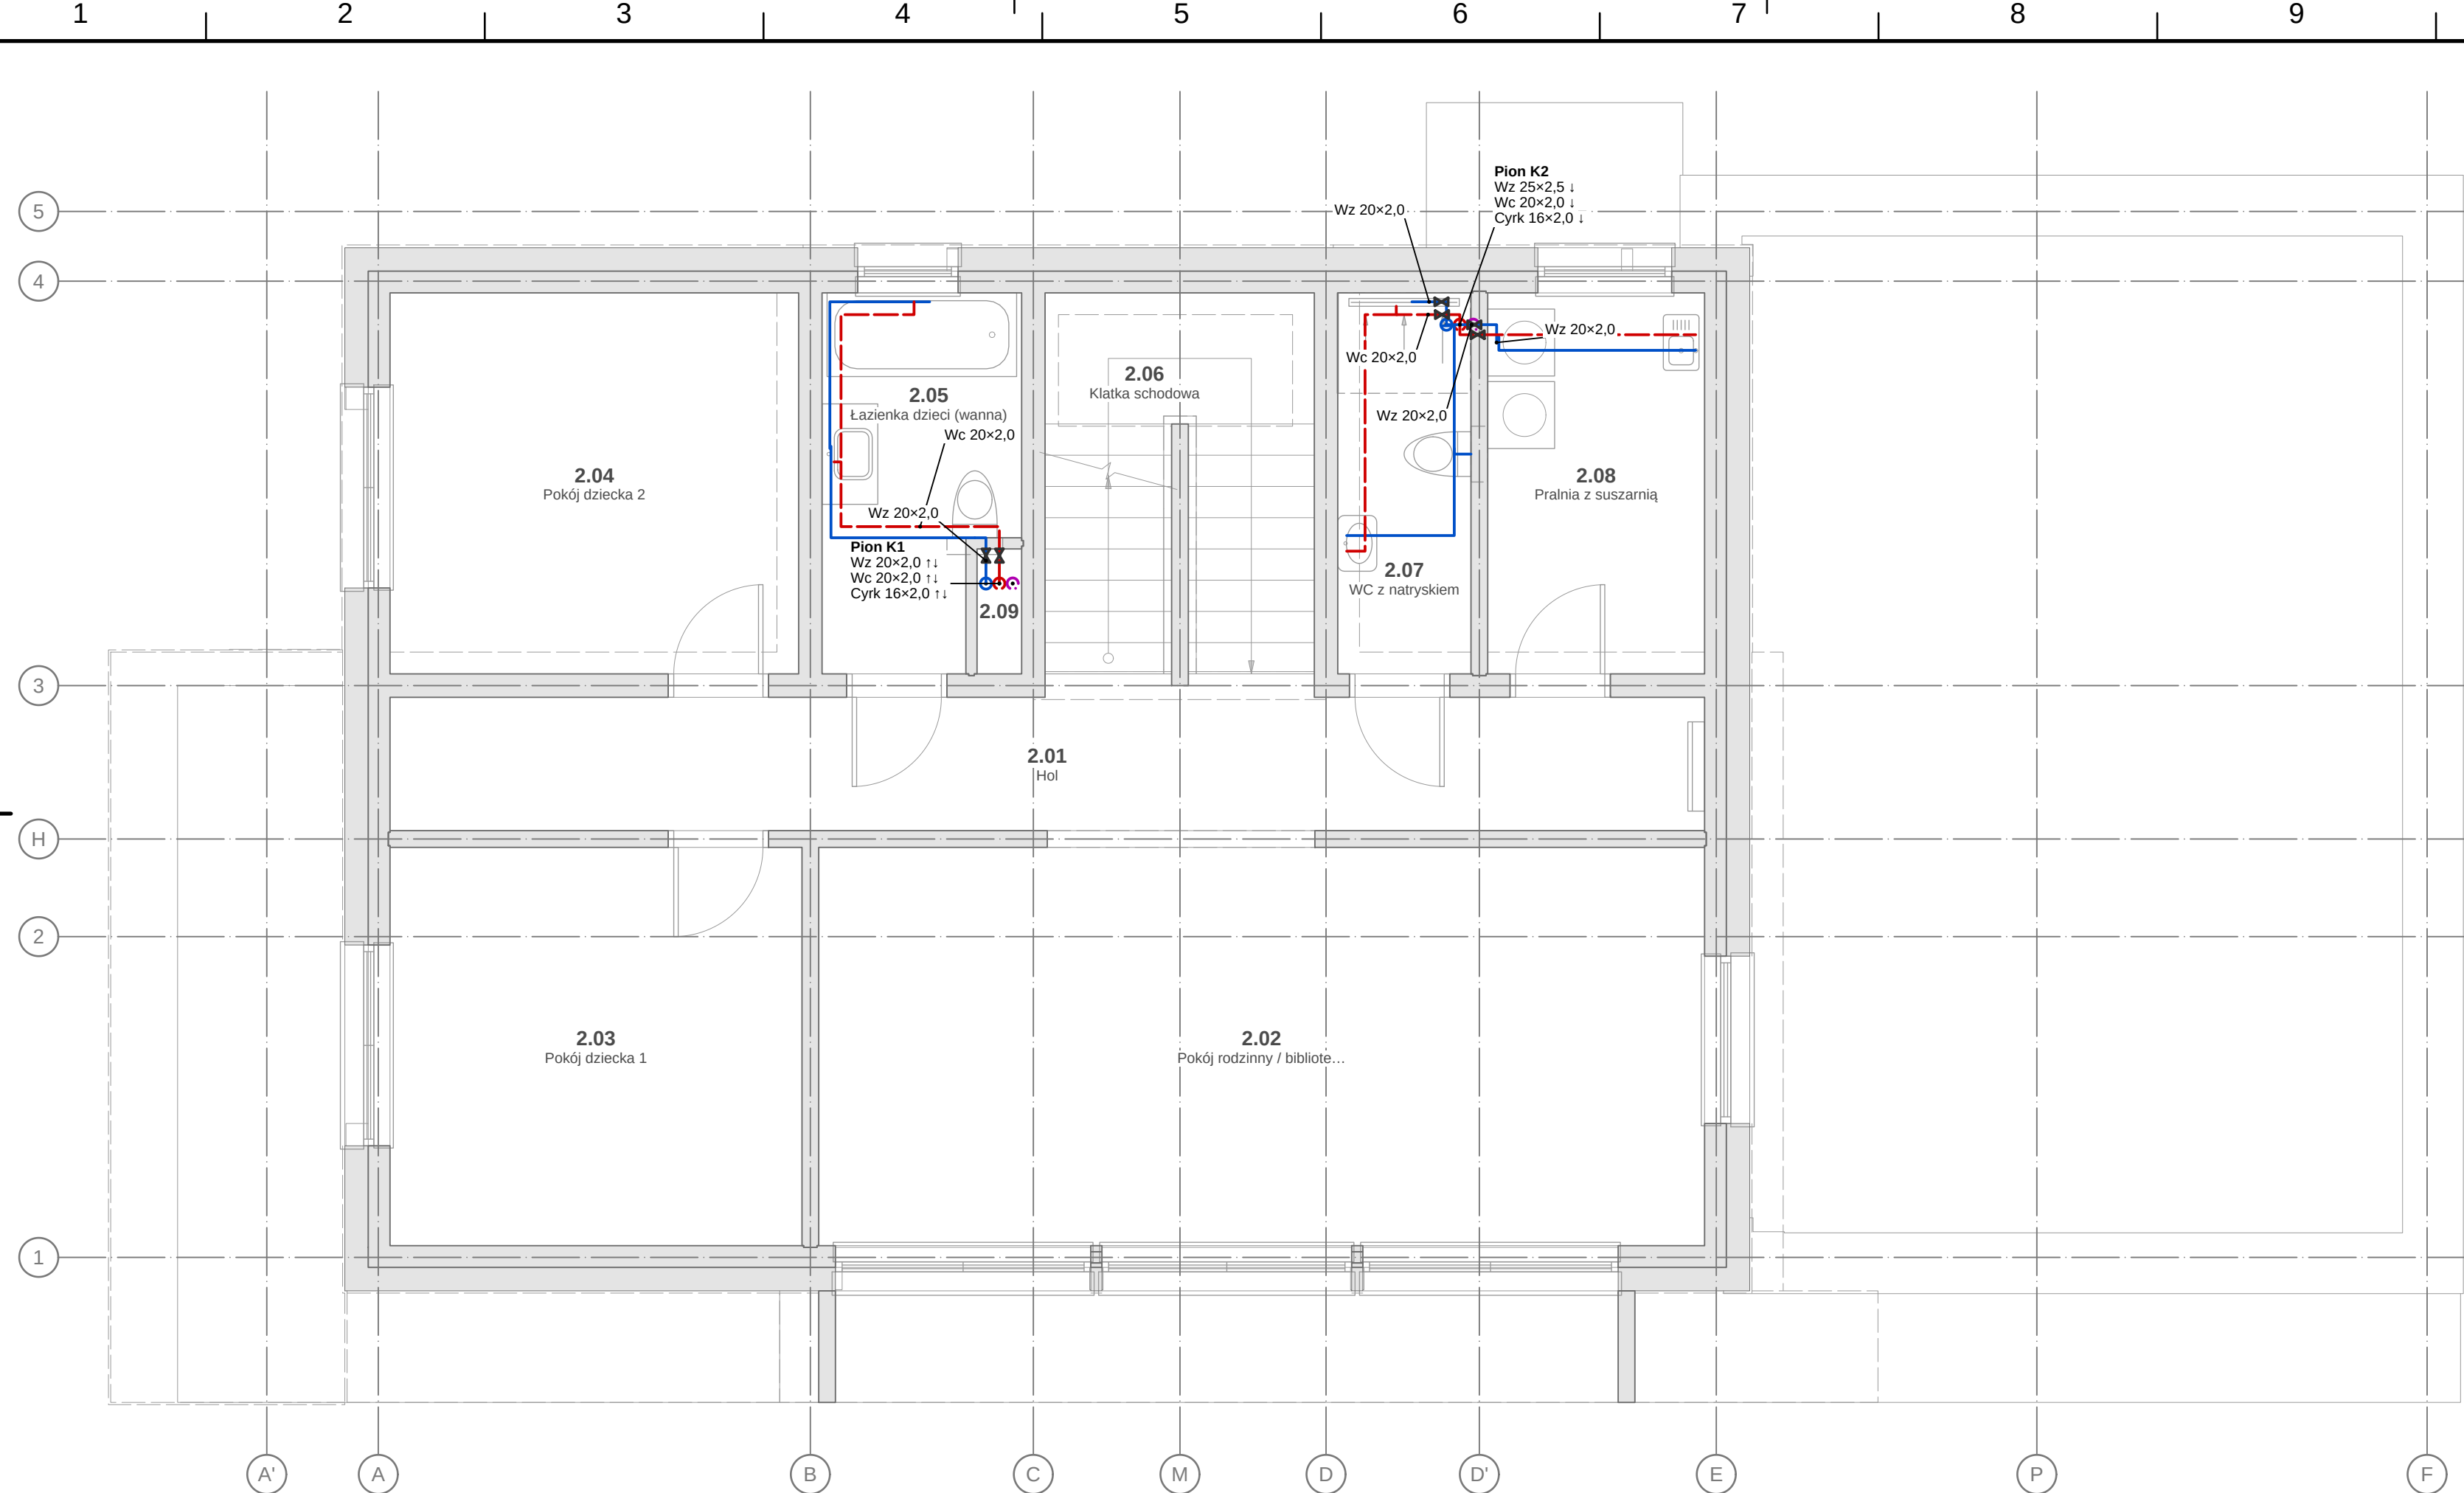

INSTALACJA WODOCIĄGOWA — RZUT I PIĘTRA 1:50

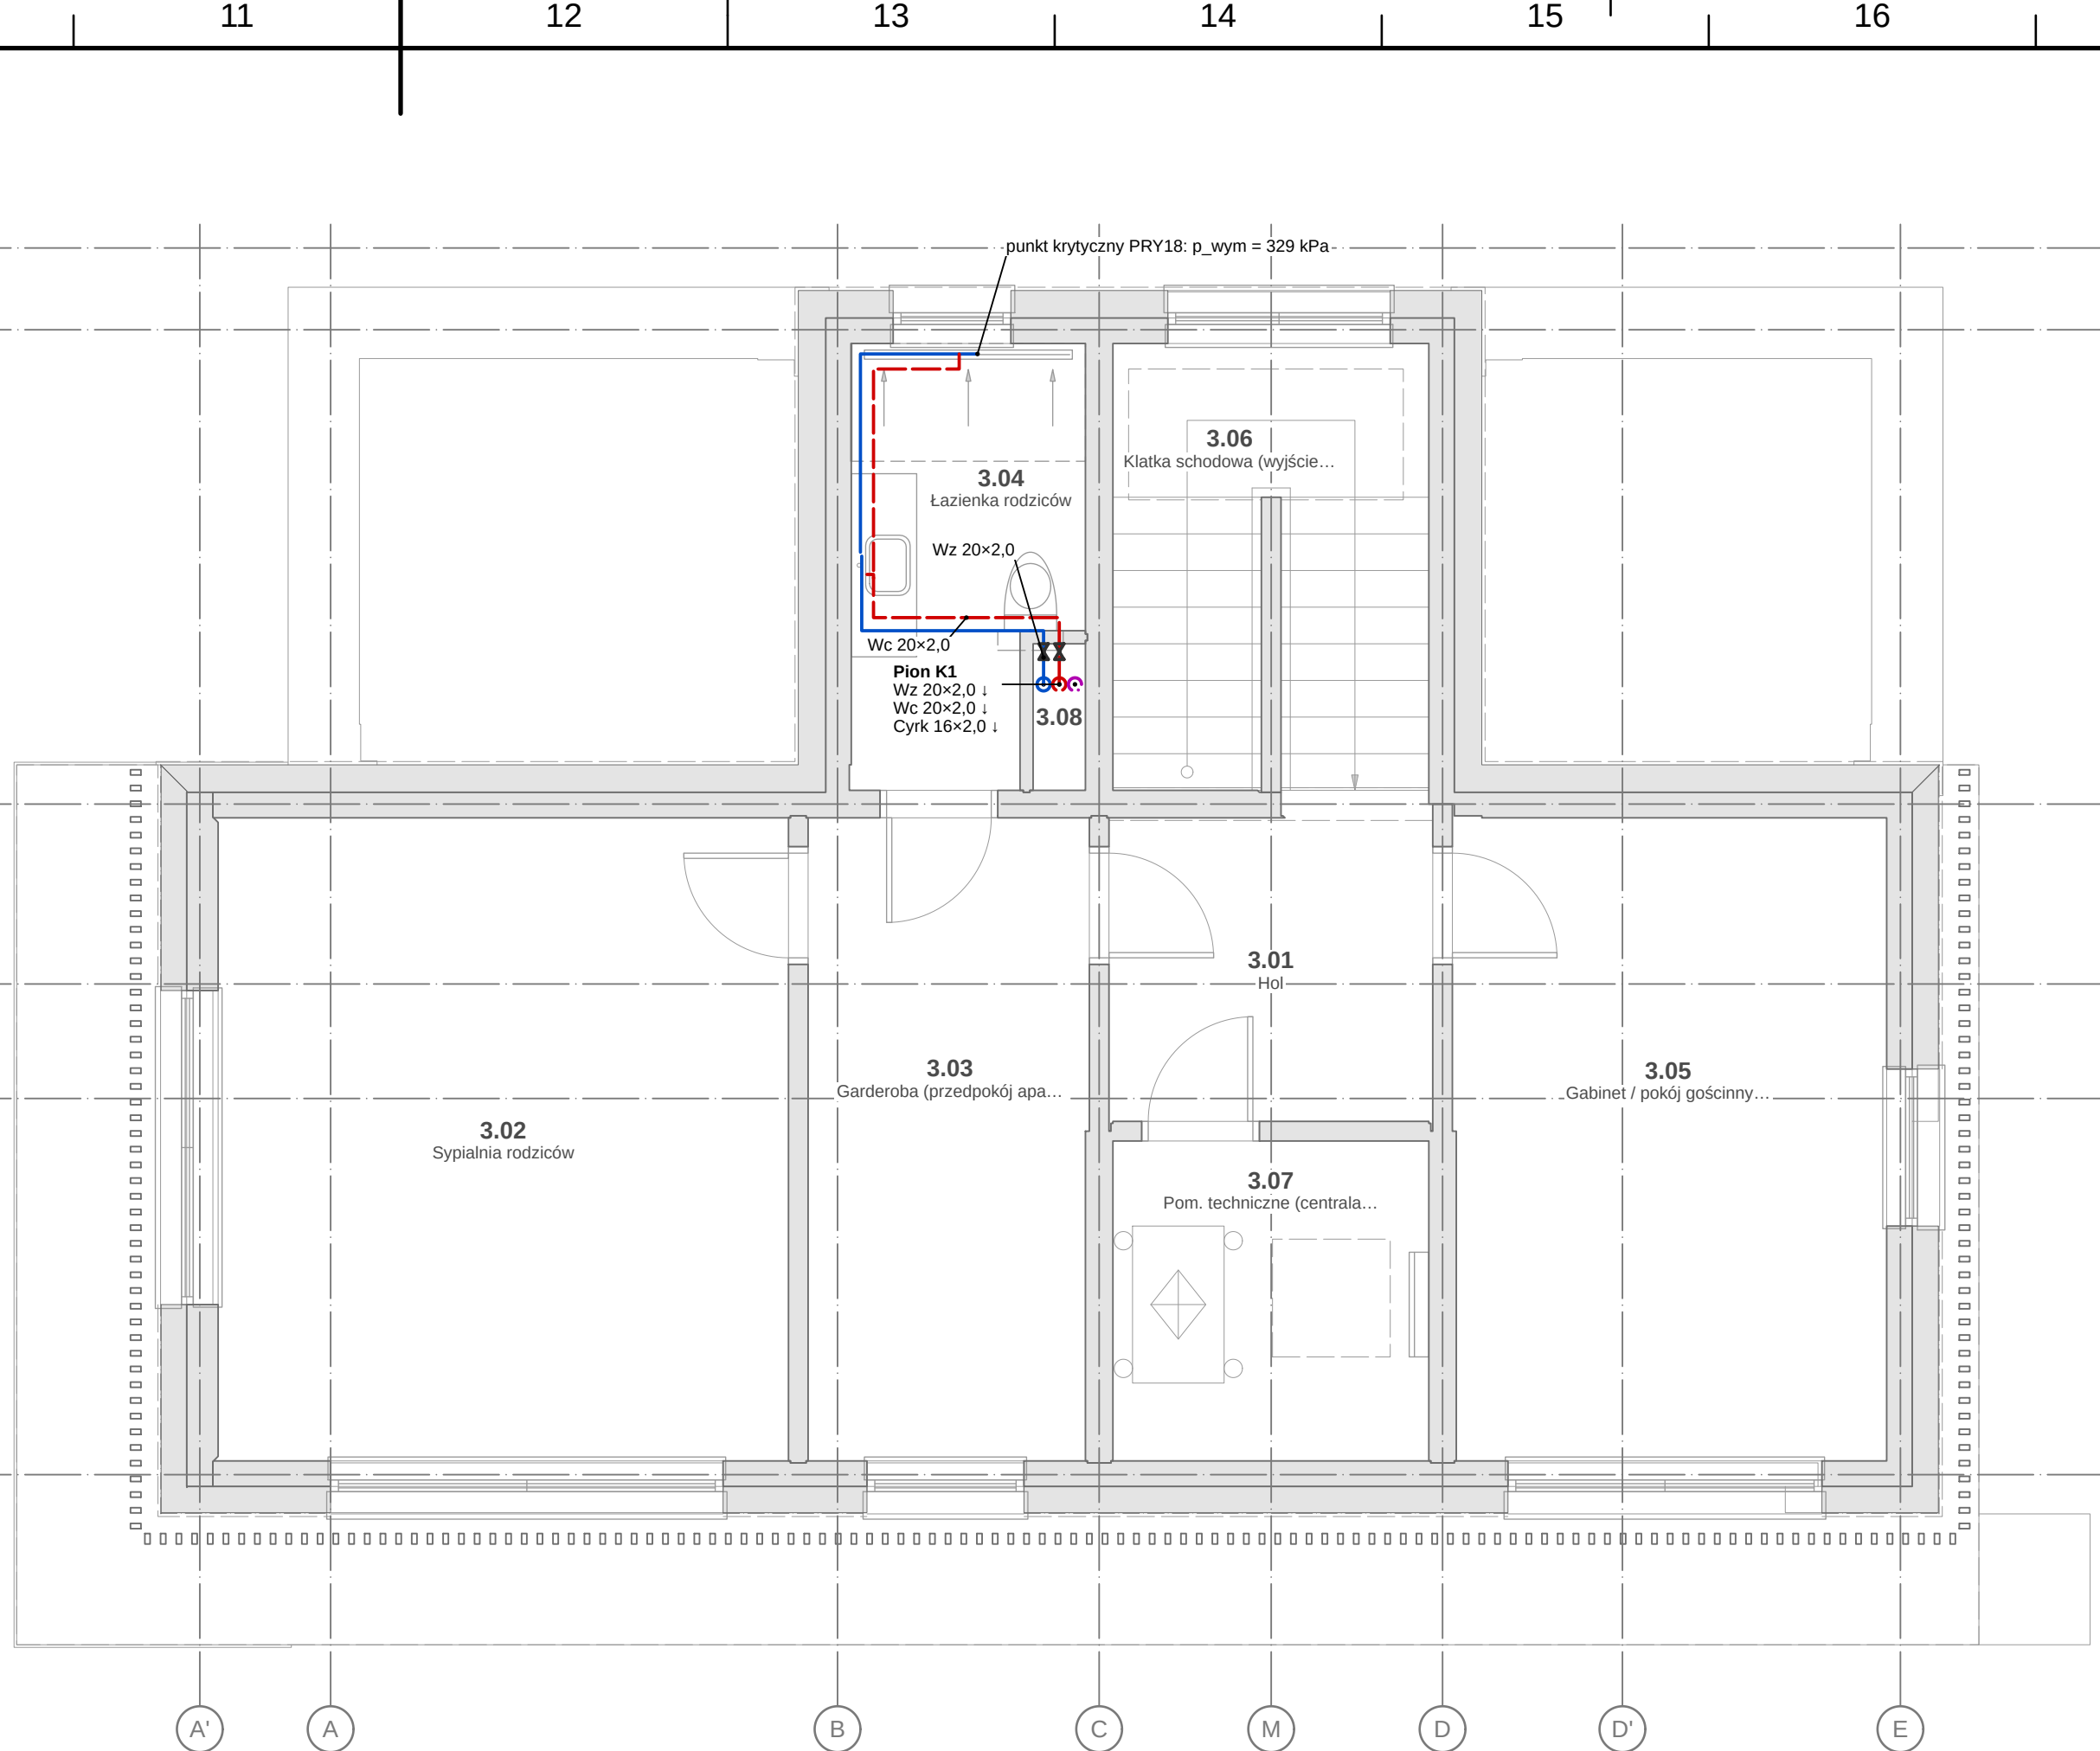

INSTALACJA WODOCIĄGOWA — RZUT II PIĘTRA 1:50

OZNACZENIA — LEGENDA SYMBOLI


Oznaczenia instalacji sanitarnych — praktyka branżowa (PN-B-01410, PN-B-01411, PN-B-01430 — normy wycofane, bez następcy); armatura i urządzenia wg PN-EN ISO 10628-2 / PN-EN ISO 14617; rodzaje powietrza wg PN-EN 16798-3 (ODA, SUP, ETA, EHA). Obowiązuje legenda na arkuszu.

—	podkład architektoniczny (rzut AR — ściany przecięte, stolarka, wyposażenie) — linie cienkie szare	—	Cyrk — cyrkulacja c.w.u. 16×2,0 (praca czasowa)
—	Wz — woda zimna (PE-RT/Al/PE-RT lub równoważne), średnica d _z ×s wg obliczeń	⊙	pion instalacji (Wz / Wc / Cyrk); ⊕ — prowadzony na kondygnację wyższą, ⊖ — z kondygnacji niższej
—	Wc — ciepła woda użytkowa (c.w.u.), izolowana wg WT zał. 2 pkt 1.5	⌞	zawór odcinający kulowy (na odgałęziach z rozdzielaczy i odgałęzieniach do pomieszczeń)

OBJAŚNIENIA I UWAGI

- Średnice przewodów w mm (d_z×s — rury wielowarstwowe, Ø/DN — kanalizacja, kanały wentylacyjne), przekroje żył w mm², odległości i rzędne w m; ±0,000 = 101,650 m n.p.m. (PL-EVRF2007-NH).
- Rysunki instalacji na podkładzie rzutów architektury (PB-AR); podkład — linie cienkie szare (warstwy I-PODKŁAD*).
- Instalacja wodociągowa wg PN-EN 806-1...5 i WT § 113-121; obliczenia przepływów wg PN-92B-01706 (norma wycofana — stosowana jako praktyka projektowa, powołana w WT zał. 1) z kontrolą wg PN-EN 806-3; ochrona przed wtórnym zanieczyszczeniem wg PN-EN 1717.
- Średnice przewodów z obliczeń (lamela, obliczenia, sanitarne, woda); podejścia do przyborów 16×2,0, jeżeli nie opisano inaczej. Rury wielowarstwowe PE-RT/Al/PE-RT (lub równoważne) z kształtkami zaprasowywanymi.
- Wymagane ciśnienie przed wodomierzem p_{wym} = 329 kPa (punkt krytyczny PRY18); q_{obl} = 1,128 dm³/s.
- Trasy przewodów wyznaczone algorytmicznie (model nie zawiera przebiegów); ortogonalnie, przy ścianach, z rozdzielaczy w pom. technicznym i z pionów w szachcie SI do przyborów — w warstwie posadzkibruzdach ściennych; do weryfikacji na budowie z zachowaniem średnic i zasady rozdzielu.
- C.w.u. po lewej stronie armatury (WT § 120 ust. 5); temperatura c.w.u. 55–60 °C, dezynfekcja termiczna 70 °C (WT § 120 ust. 2a); izolacja c.w.u. i cyrkulacji wg WT zał. 2 pkt 1.5 (tabela), wody zimnej — przeciwzrośnięcia 9 mm.
- Próba szczelności wg PN-EN 806-4; płukanie i dezynfekcja przed odbiorem.
- Rysunek wygenerowany automatycznie z modelu model/budynki.yaml (wersja 1.0, 2026-09-25) — generatory lamela.views.

1 0 1 2 3 4 5 m
PODZIAŁKA 1:50

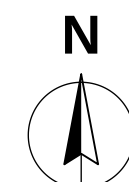

REW.	OPIS ZMIANY			DATA		
0	Wydanie — rysunek wygenerowany z modelu			2026-09-25		
PRACOWNIA PROJEKTOWA PRACOWNIA PROJEKTOWA — nazwa do uzupełnienia				STADIUM PT	BRANŻA INSTALACJE SANITARNE (IS)	
INWESTOR (do uzupełnienia)						
OBJEKT / NAZWA ZAMIERZENIA BUDOWLANEGO Budynek mieszkalny jednorodzinny wolnostojący „Dom LAMELA”						
ADRES / LOKALIZACJA (NR DZIAŁKI, OBRĘB, JEDN. EWIDENCYJNA) ul. Lipowa (fikcyjna), dz. nr ewid. 123/4, obręb 0005 Przykładowo, gm. Przykładowo (fikcyjna)					KAT. OBIEKTU I	
FUNKCJA	IMIĘ I NAZWISKO		SPECJALNOŚĆ, NR UPRAWNIIEŃ		DATA	PODPIS
Projektant	[DO UZUPEŁNIENIA]		[DO UZUPEŁNIENIA]			
Projektant (wsp.)	[DO UZUPEŁNIENIA]		[DO UZUPEŁNIENIA]			
Sprawdzający	nie dotyczy (art. 20 ust. 3 pkt 2 PB)		—			
Opracował	[DO UZUPEŁNIENIA]		[DO UZUPEŁNIENIA]			
TYTUŁ RYSUNKU INSTALACJA WODOCIĄGOWA — RZUTY I PIĘTRA I II PIĘTRA						
SKALA 1:50	FORMAT 1130x297	DATA WYDANIA 2026-09-25	RODZAJ DOK. rzut instalacji	NR RYSUNKU PT-IS-02	ARKUSZ 2/11	REW.