
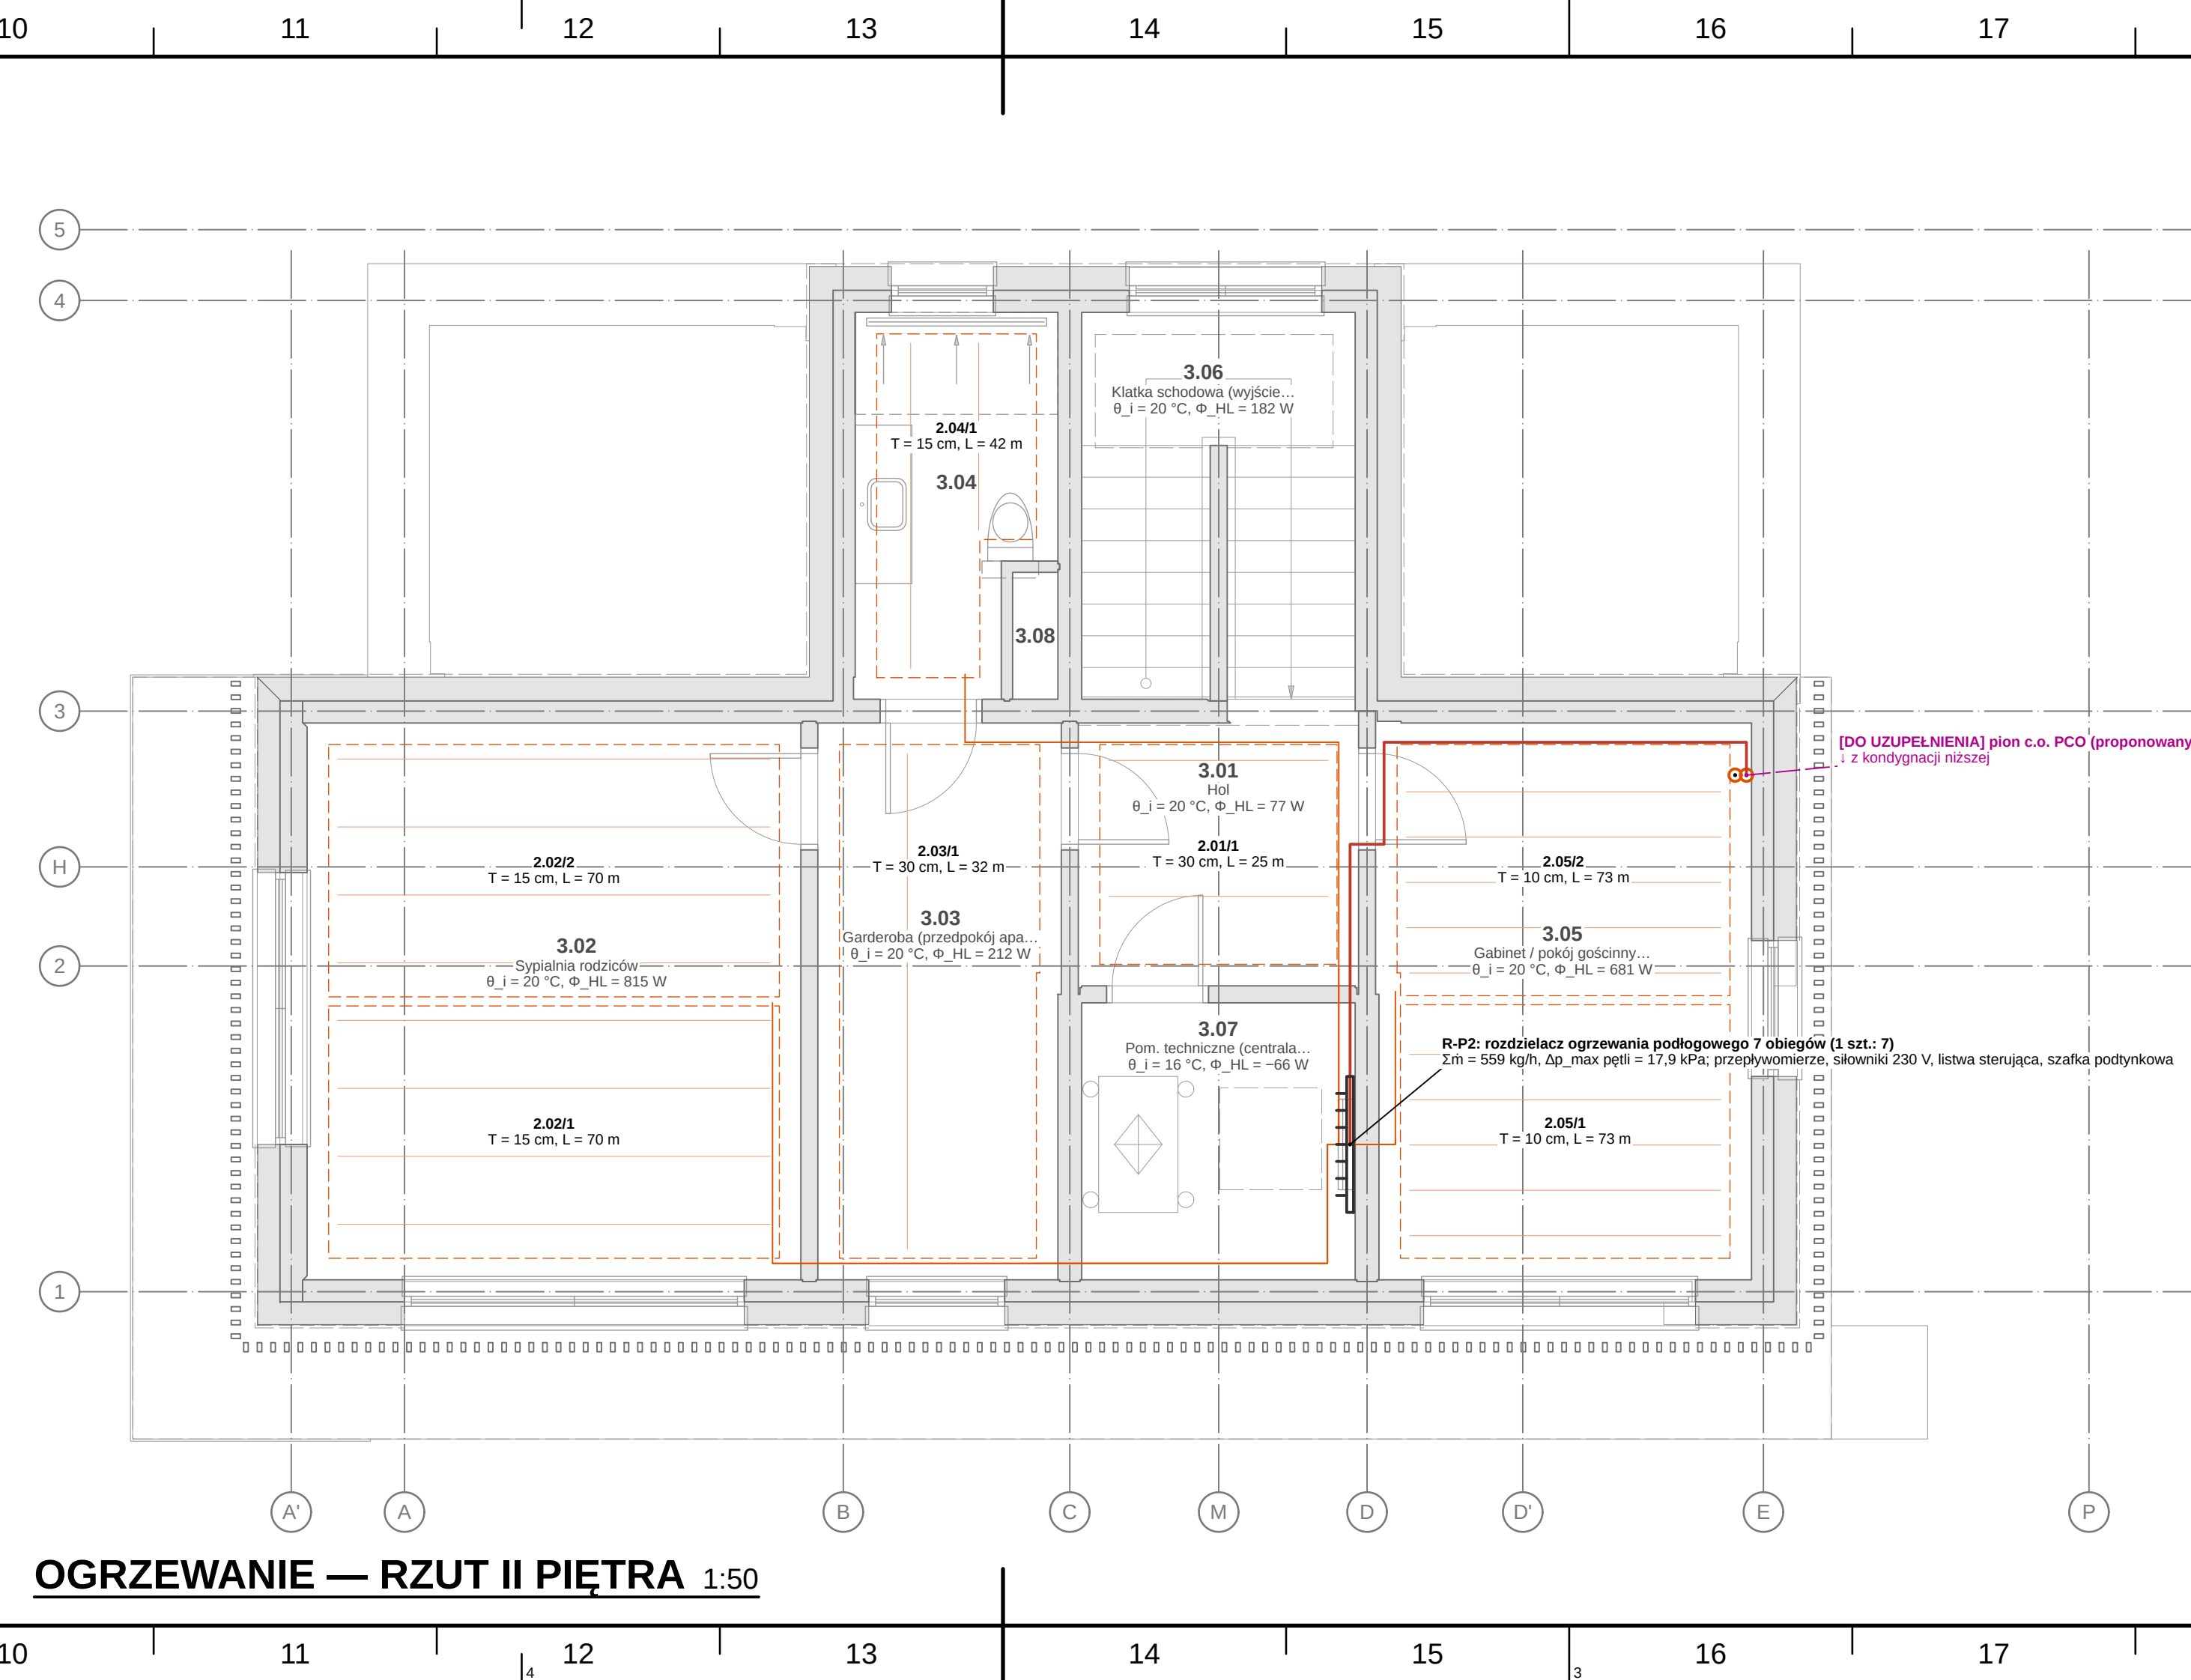


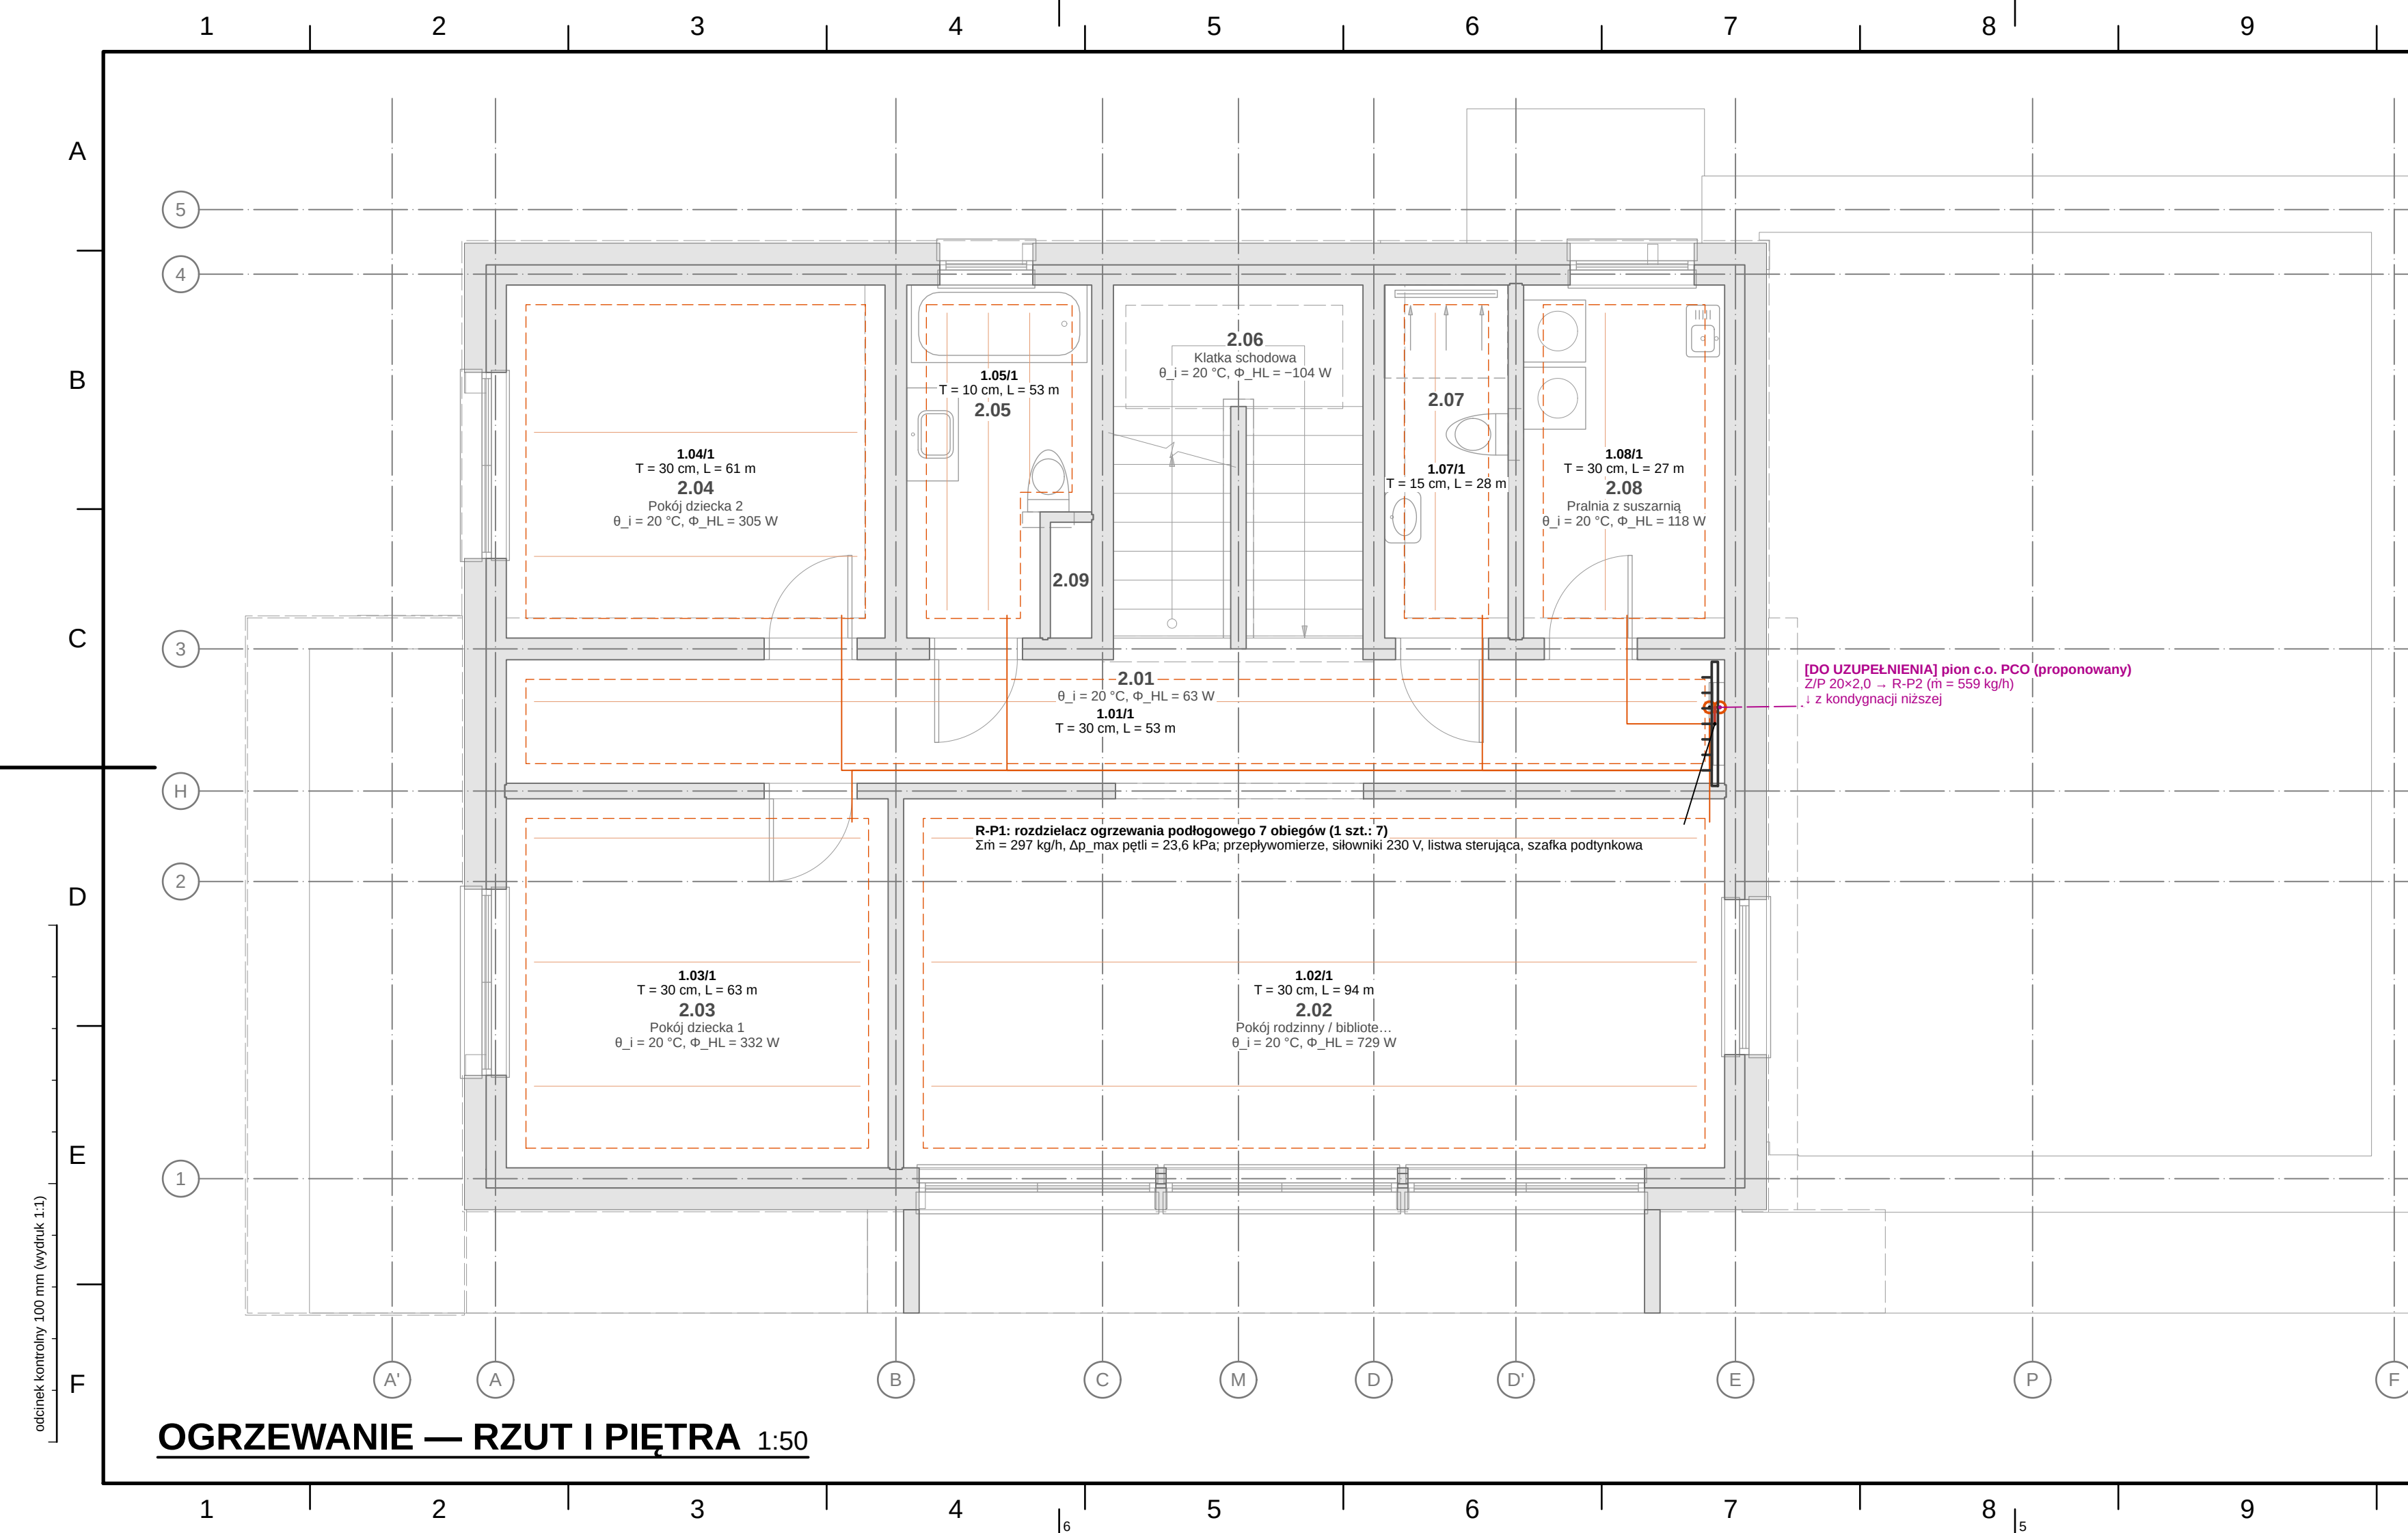

OZNACZENIA — LEGENDA SYMBOLI

Oznaczenia instalacji sanitarnych — praktyka branżowa (PN-B-01410, PN-B-01411, PN-B-01430 — normy wycofane, bez następcy); armatura urządzenia wg PN-EN ISO 10628-2 / PN-EN ISO 14617; rodzaje powietrza wg PN-EN 16798-3 (ODA, SUP, ÉTA, EHA). Obowiązuje legenda na arkuszu.

podkład architektoniczny (rzut AR — ściany przecięte,
stolarka, wyposażenie) — linie cienkie szare

przylązca petli ogrzewania podłogowego (zasilanie/powrót
PE, X(A/B/E, Y 16x2, prowadzący), żarówka do rozdzielacza)

pion c.o. (zasilanie/powrót rozdzielacza)

R — rozdzielacz ogrzewania podłogowego z przepływomierzami i siłownikami

Z/P — przewody zasilania i powrotu c.o. (PC → bufor → rozdzielacze), piony c.o.

strefa pętli ogrzewania podłogowego <pm.>/<nr>; T —
rozstaw rur, L — długość pętli (z obliczeń PN-EN 1264);
meander symboliczny (co 4 rozstawy)

PĘTLE OGRZEWANIA PODŁOGOWEGO — P1 (PN-EN 1264)

Petla	T [cm]	L [m]	m [kg/h]	Δp [kPa]
1.01/1	30	52.6	4	5.1
1.02/1	30	94.1	124	23.6
1.03/1	30	63.1	52	6.9
1.04/1	30	61.3	44	6.6
1.05/1	10	53.3	33	6.0
1.07/1	15	27.6	31	5.5
1.08/1	30	26.6	8	5.1

PĘTLE OGRZEWANIA PODŁOGOWEGO — P2 (PN-EN 1264

Peta	T [cm]	L [m]	m [kg/h]	Δp [kPa]
2.01/1	30	24.7	6	5.1
2.02/1	15	69.5	120	17.9
2.02/2	15	69.5	120	17.9
2.03/1	30	31.8	63	7.0
2.04/1	15	41.6	49	6.2
2.05/1	10	72.7	101	15.1
2.05/2	10	72.7	101	15.1

