


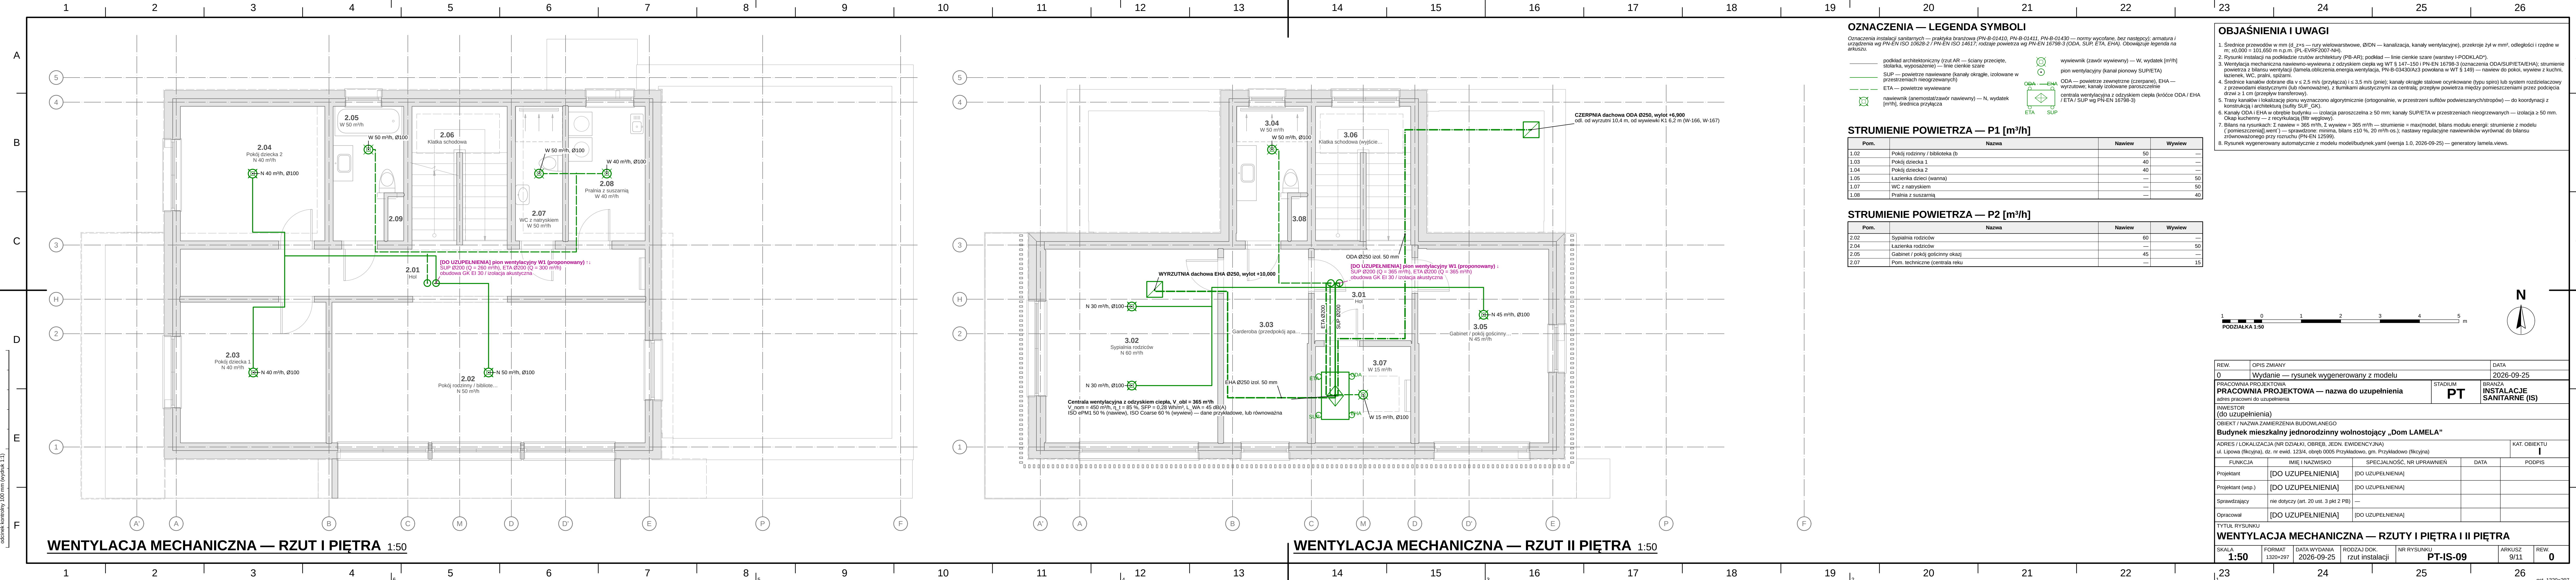

WENTYLACJA MECHANICZNA — RZUT I PIĘTRA 1:50

WENTYLACJA MECHANICZNA — RZUT II PIĘTRA 1:50

OZNACZENIA — LEGENDA SYMBOLI

Oznaczenia instalacji sanitarnych — praktyka branżowa (PN-B-01410, PN-B-01411, PN-B-01430 — normy wycofane, bez następcy); armatura i urządzenia wg PN-EN ISO 10628-2 / PN-EN ISO 14617; rodzaje powietrza wg PN-EN 16798-3 (ODA, SUP, ETA, EHA). Obowiązuje legenda na arkuszu.

- podkład architektoniczny (rzut AR — ściany przecięte, stolarka, wyposażenie) — linie cienie szare
- SUP — powietrze nawiewane (kanały okrągłe, izolowane w przestrzeniach nieogrzewanych)
- ETA — powietrze wywiewane
- nawiewnik (anemostat/zawór nawiewny) — N, wydatek [m³/h, średnica przyłącza]
- wywiewnik (zawór wywiewny) — W, wydatek [m³/h] pion wentylacyjny (kanał pionowy SUP/ETA)
- ODA — powietrze zewnętrzne (czerpane), EHA — wyrzutowe; kanały izolowane paroszczelnie
- centrala wentylacyjna z odzyskiem ciepła (króćce ODA / EHA / ETA / SUP wg PN-EN 16798-3)

STRUMIENIE POWIETRZA — P1 [m³/h]

Pom.	Nazwa	Nawiew	Wywiew
1.02	Pokój rodzinny / biblioteka (b)	50	—
1.03	Pokój dziecka 1	40	—
1.04	Pokój dziecka 2	40	—
1.05	Łazienka dzieci (wanna)	—	50
1.07	WC z natryskiem	—	50
1.08	Pralnia z suszarnią	—	40

STRUMIENIE POWIETRZA — P2 [m³/h]

Pom.	Nazwa	Nawiew	Wywiew
2.02	Sypialnia rodziców	60	—
2.04	Łazienka rodziców	—	50
2.05	Gabinet / pokój gościnny okazj	45	—
2.07	Pom. techniczne (centrala reku	—	15

OBJAŚNIENIA I UWAGI

- Srednice przewodów w mm (d, z×s — rury wielowarstwowe, Ø/DN — kanalizacja, kanały wentylacyjne), przekroje żył w mm², odległości i rzędne w m: 40,000 ± 101,650 m n.p.m. (PL-EVRF2007-NH).
- Rysunki instalacji na podkładzie rzutów architektury (PB-AR); podkład — linie cienie szare (warstwy I-PODKŁAD*).
- Wentylacja mechaniczna nawiewno-wywiewna z odzyskiem ciepła wg WT § 147–150 i PN-EN 16798-3 (oznaczenia ODA/SUP/ETA/EHA); strumienie powietrza z bilansu wentylacji (lamela.obliczenia.energia.wentylacja, PN-B-03430/Az3 powołana w WT § 149) — nawiew do pokoi, wywiew z kuchni, łazienek, WC, pralni, sypialni.
- Srednice kanałów dobrane dla v ≤ 2.5 m/s (przyłacza) i ≤ 3.5 m/s (pnie); kanały okrągłe stalowe ocynkowane (typu spiro) lub system rozdzielaczy z przewodami elastycznymi (lub równoważne), z tłumikami akustycznymi za centralą; przepływ powietrza między pomieszczeniami przez podcięcie drzwi ≥ 1 cm (przepływ transferowy).
- Trasy kanałów i lokalizację pionu wyznaczono algorytmicznie (ortogonalnie, w przestrzeni sufitów podwieszanych/stropów) — do koordynacji z konstrukcją i architekturą (suffity SUF_GK).
- Kanały ODA i EHA w obrebie budynku — izolacja paroszczelna ≥ 50 mm; kanały SUP/ETA w przestrzeniach nieogrzewanych — izolacja ≥ 50 mm. Okap kuchenny — z recykulacją (filtr węglowy).
- Bilans na rysunkach: Σ nawiew = 365 m³/h; Σ wywiew = 365 m³/h — strumienie = max(model, bilans modulu energii; strumienie z modelu (pomieszczenia[vent]) — sprawdzone: minima, bilans ±10 %, 20 m³/h-os.); nastawy regulacyjne nawiewników wyrównać do bilansu zrównoważonego przy rozruchu (PN-EN 12599).
- Rysunek wygenerowany automatycznie z modelu model/budynki.yamli (wersja 1.0, 2026-09-25) — generatory lamela.views.



REW.	OPIS ZMIANY	DATA
0	Wydanie — rysunek wygenerowany z modelu	2026-09-25
PRACOWNIA PROJEKTOWA PRACOWNIA PROJEKTOWA — nazwa do uzupełnienia		STADIUM PT
adres pracowni do uzupełnienia		BRANZA INSTALACJE SANITARNE (IS)
INWESTOR (do uzupełnienia)		
OBIEKT / NAZWA ZAMIERZENIA BUDOWLANEGO Budynek mieszkalny jednorodzinny wolnostojący „Dom LAMELA”		
ADRES / LOKALIZACJA (NR DZIAŁKI, OBRĘB, JEDN. EWIDENCYJNA) ul. Lipowa (fikcyjna), dz. nr ewid. 123/4, obręb 0005 Przykładowo, gm. Przykładowo (fikcyjna)		KAT. OBIEKTU I
FUNKCJA	IMIĘ I NAZWISKO	SPECJALNOŚĆ, NR UPRAWNIEN
Projektant	[DO UZUPEŁNIENIA]	[DO UZUPEŁNIENIA]
Projektant (wsp.)	[DO UZUPEŁNIENIA]	[DO UZUPEŁNIENIA]
Sprawdzający	nie dotyczy (art. 20 ust. 3 pkt 2 PB)	—
Opracował	[DO UZUPEŁNIENIA]	[DO UZUPEŁNIENIA]
TYTUŁ RYSUNKU WENTYLACJA MECHANICZNA — RZUTY I PIĘTRA I II PIĘTRA		
SKALA 1:50	FORMAT 1320×297	DATA WYDANIA 2026-09-25
RODZAJ DOK. rzut instalacji	NR RYSUNKU PT-IS-09	ARKUSZ 9/11
REW. 0		