
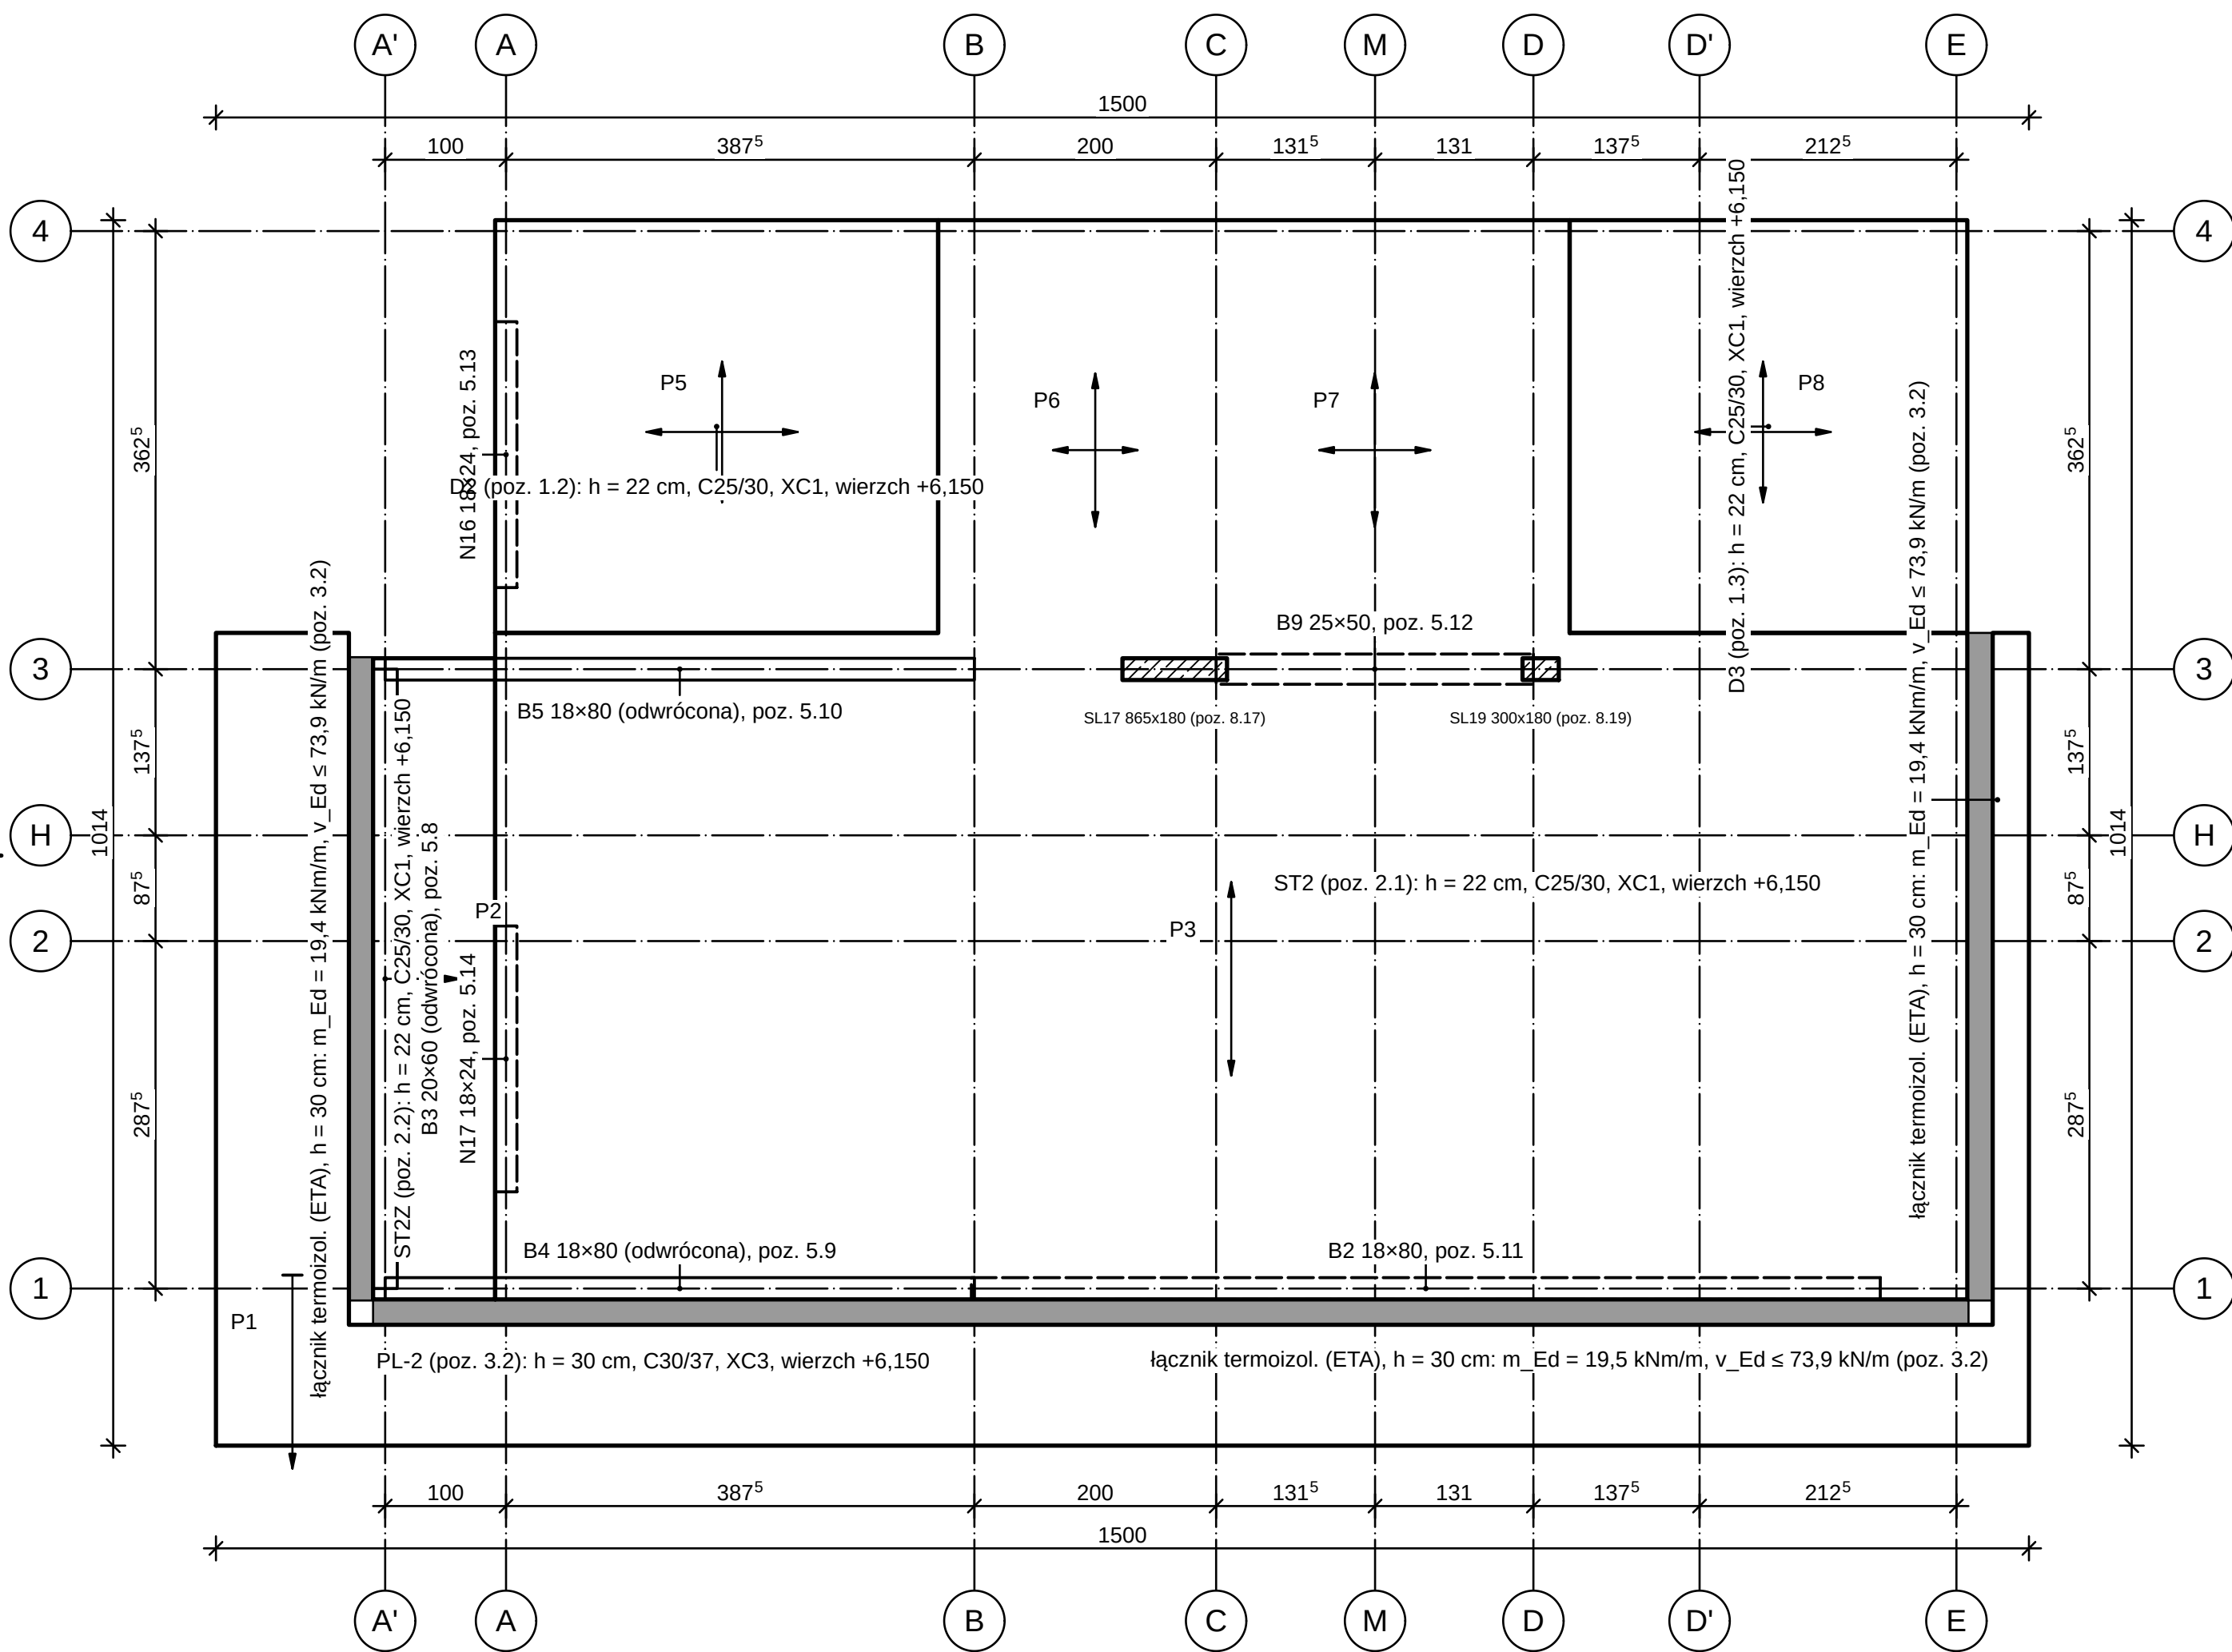


OZNACZENIA NA RYSUNKU

- 
 słup stalowy (przekrój) — pod płytą
 — — — belka / podciąg pod płytą (widok zasłonięty); linia ciągła — belka odwrócona (nad płytą)
 łącznik termooizolacyjny płyty wspornikowej (ETA)
 — kierunek pracy pola (krzyż — płyta krzyżowo zbrojona); P1... — pola obliczeniowe MES
 NA, NB... — typ nadproża (tabela); ściany pod płytą kreskowane wg materiału

OBJAŚNIENIA I UWAGI

1. Wymiary w mm (mm w indeksie górnym, np. 24^s = 24,5 cm), rzędne w m względem $\pm 0,00 \pm 101,650$ m n.p.m. (PL-EVRF2007-NH).
2. PL-2: łączniki termoplastyczne ciagle na całej linii zamocowania — wyrób z Europejską Ocena Techniczną (EAD 050001-00-0301) „Jub równoważny” (np. typ z prejami ze stali nierdzewnej przez izolację gr. 80–120 mm); dobór wg dokumentacji producenta na Ed i v_d E; z obliczeń, z uwzględnieniem uskuo wierzchu płyty, sprawdzenie ugięcia wspornika z podatnością łącznika (W-268, W-272).
3. Płyty monolityczne: ST2 h = 22 cm (C25/30, XCl, c_nom = 25 mm), ST22 h = 22 cm (C25/30, XCl, c_nom = 25 mm), D2 h = 22 cm (C25/30, XCl, c_nom = 25 mm), D3 h = 22 cm (C25/30, XCl, c_nom = 25 mm), PL-2 h = 30 cm (C30/37, XC3, c_nom = 35 mm); wierzch konstrukcji +6,150 (średnio), rzędne elementów wg przekrojów i modelu.
4. Wience (W-ST) ST22, D2, D3, PL-2, poz. 7.2): na wszystkich ścianach nośnych pod płytą, szerokość = grubość muru, wysokość = grubość płyty, 4012 i strzemiemiona 06 co 25 cm, C25/30; zakład $l_0 = 638$ mm (PN-EN 1992-1-1 9.10.2.2, 8.7).
5. Kierunek pracy podłogi wg modelu MES płyty (biblioteka — Wood—Armer); pola P... — numeracja komórek siatki podpór obliczeń (zbrojenie — arkusze zbrojenia dolnego i górnego).
6. Ściany-tarcze: analiza nie wykryła ścian-tarcz na tym poziomie (model tarcza — ściana BZ podparta na < 95 % długości lub pole 'tarcza: true').
7. Rysunek wygenerowany automatycznie z modelu modelu/budynki.yaml (wersja 1.0, 2026-09-25) — generatory lamela.views.

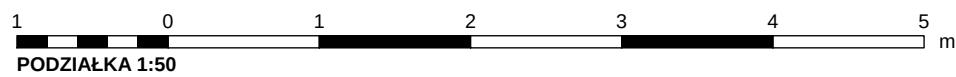

RZUT KONSTRUKCJI — PŁYTY ST2, ST2Z, D2, D3, PL-2 1:50

REV.	OPIS ZMIANY			DATA	
0	Wydanie — rysunek wygenerowany z modelu			2026-09-25	
PRACOWNIA PROJEKTOWA PRACOWNIA PROJEKTOWA — nazwa do uzupełnienia adres pracowni do uzupełnienia			STADIUM PT	BRANŻA KONSTRUKCJA (BO)	
INWESTOR (do uzupełnienia)					
OBIEKT / NAZWA ZAMIERZENIA BUDOWLANEGO Budynek mieszkalny jednorodzinny wolnostojący „Dom LAMELA”					
ADRES / LOKALIZACJA (NR DZIAŁKI, OBRĘB, JEDN. EWIDENCYJNA) ul. Lipowa (fikcyjna), dz. nr ewid. 123/4, obręb 0005 Przykładowo, gm. Przykładowo (fikcyjna)				KAT. OBIEKTU I	
FUNKCJA	IMIĘ I NAZWISKO	SPECJALNOŚĆ, NR UPRAWNIENI		DATA	PODPIS
Projektant	[DO UZUPEŁNIENIA]	[DO UZUPEŁNIENIA]			
Projektant (wsp.)	[DO UZUPEŁNIENIA]	[DO UZUPEŁNIENIA]			
Sprawdzający	nie dotyczy (art. 20 ust. 3 pkt 2 PB)	—			
Opracował	[DO UZUPEŁNIENIA]	[DO UZUPEŁNIENIA]			
TYTUŁ RYSUNKU RZUT KONSTRUKCJI STROPU NAD I PIĘTREM					
SKALA 1:50	FORMAT A2	DATA WYDANIA 2026-09-25	RODZAJ DOK. rzut konstrukcji	NR RYSUNKU PT-BO-07	ARKUSZ 7/27
					REW. 0