


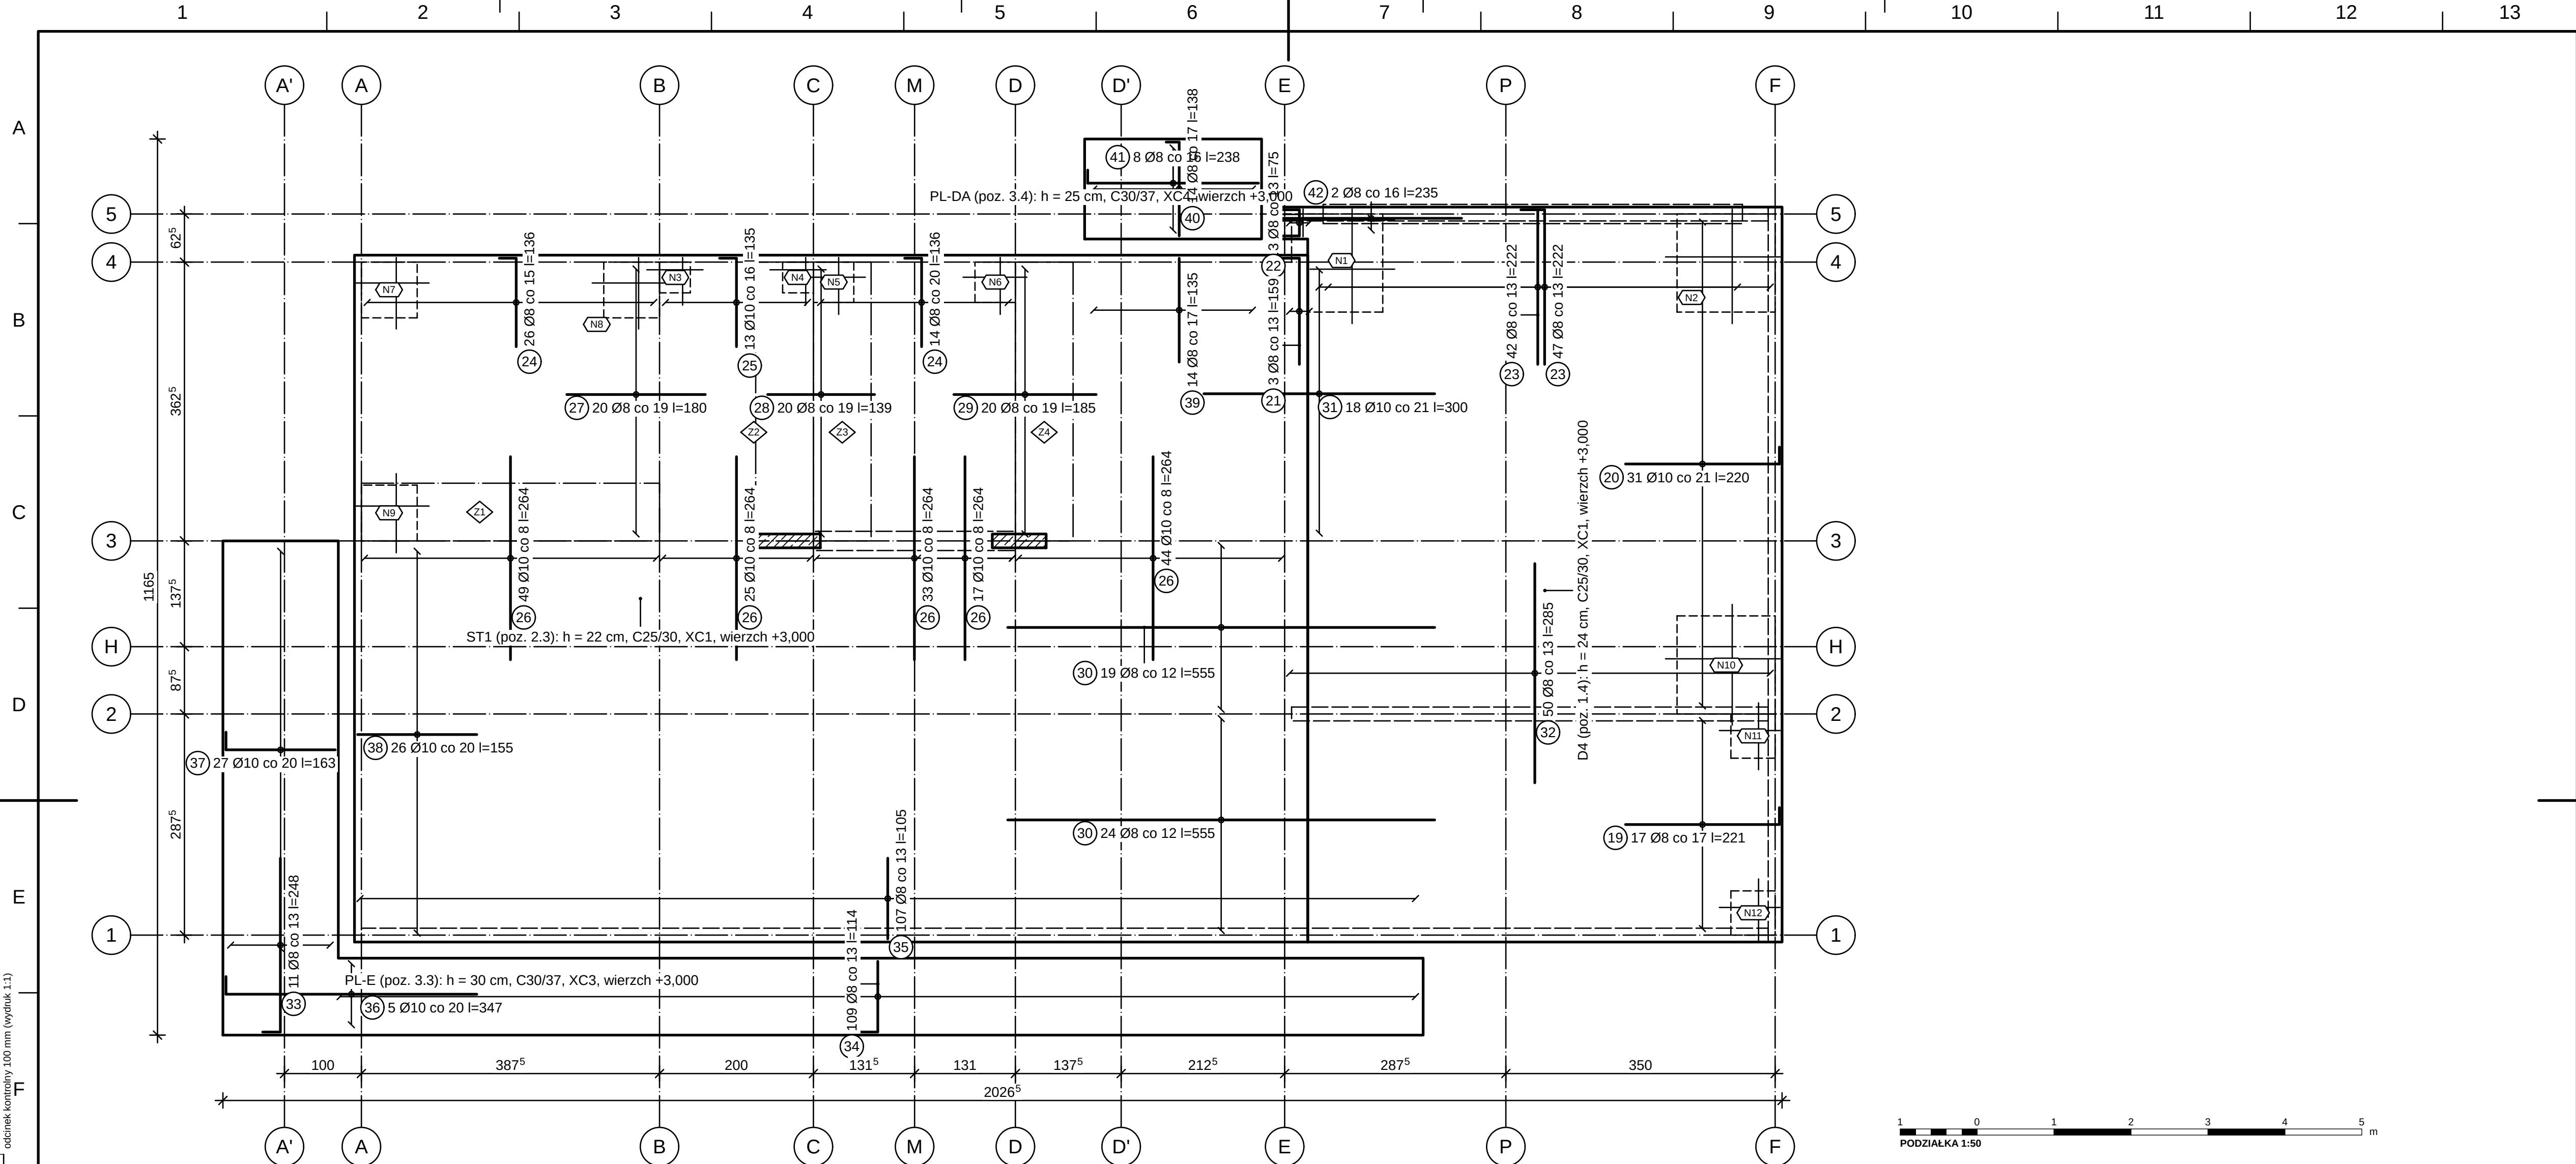


ZBROJENIE GÓRNE PŁYT ST1, D4, PL-E, PL-DA 1:50

OZNACZENIA NA RYSUNKU

- pręt reprezentatywny grupy (warstwa górna), linia gruba
- pręt z odgięciem 90° — odgięcie (ramię) pokazane w płaszczyźnie rysunku
- linia rozkładu prętów grupy (zasięg), kółko — pręt reprezentatywny
- numer pozycji pręta (zestawienie stali)
- strefa zbrojenia narożnego (0,2·l_{min}) — pręty górą i dołem w 2 kierunkach
- ściany / belki / słupy pod płytą (widok zasłonięty)
- łącznik termoz izolacyjny (ETA) — pręty wspornika przez izolację

OBJAŚNIENIA I UWAGI

- Wymiary w cm (mm w indeksie górnym, np. 24° = 24,5 cm), rzędne w m względem ±0,000 = 101,650 m n.p.m. (PL-EVRF2007-NH).
- Zestawienie stali, strefy zbrojenia narożnego/na ścinanie i dozbrojenia — arkusz PT-BO-11.
- Strefy Z... strzemiona zamknięte ø8 obejmujące pręty dolne i górne (kształt 51), rozstaw podłużny wg tabeli, poprzeczny ≤ 1,5d (9.3.2(5)); pierwsze strzemie ≤ 0,5d od lica podpory; V_Ed — reakcja podpory uśredniona na 1,0 m (osobliwość MES płyty na końcach podpór) [ZAL].
- Stal zbrojeniowa B500SP (klasa ciągliwości C, f_{yk} = 500 MPa) wg PN-H-93220:2018-02 / PN-EN 10080; pręty gięte na zimno na trzpieniach ø_m ≥ 4ø (ø ≤ 16 mm) i ≥ 7ø (ø > 16 mm) — PN-EN 1992-1-1 tabl. 8.1N; oznaczenia prętów i kształtów wg PN-EN ISO 3766 (liczba, nr pozycji, Ø, rozstaw [cm], długość rozwinięcia [cm]).
- Opiliny zapewnić podkładkami dystansowymi (rozstaw ≤ 1,0 m, dla siatek górnych — podpórki „kobyłki” ≤ 1,0 m) — PN-EN 13670 p. 6.5; odchyłka wykonawcza Δc_{dev} = 10 mm uwzględniona w c_{nom} (PN-EN 1992-1-1 4.4.1.3 + NA).
- Pręty łącząc na zakład l_a (tabela w stopce zestawienia), styki mijankowo — w jednym przekroju ≤ 50 % prętów; odstęp w świetle prętów ≥ max(ø_p, d_g + 5 mm; 20 mm) — PN-EN 1992-1-1 8.2(2), 8.7.2; pręty dolne w strefie podpory zakotwić ≥ 10ø za licem (9.3.1.2(1) — 9.2.1.5).
- Betonowanie: beton wg PN-EN 206+A2 i PN-B-06265 (klasa, ekspozycja, D_{max} 16 mm, konsystencja S3); pielęgnacja ≥ 7 dni (klasa pielęgnacji 2 — PN-EN 13670 p. 8.5); przerwy robocze wyłącznie w miejscach uzgodnionych z projektantem.
- Rozszalowanie i usunięcie podpór: płyty i belki po uzyskaniu ≥ 70 % f_{ck} (PN-EN 13670 p. 5.6 i 8.5), wsporniki — nie wcześniej niż po 28 dniach i po wykonaniu elementów dociągających zaplecze; podpory wtórne do 28 dni.
- Zbrojenie wynika z obliczeń statycznych (projekt/04_PT_konstrukcja/obliczenia, numeracja pozycji jak na rysunku); kontrola A_{s,prov} ≥ A_{s,req} — raport kontrola_zbrojenia.md. Pozycje z niespełnionymi warunkami nośności (wynik „NIE” w raporcie) wymagają zmian przed wydaniem do realizacji.
- Warstwa górna: pręty nad podporami — 0,3·l przeszła za oś podpory (≥ l_{bd}), przy krawędzi płyty z odgięciem w wiencu (ramię = h – 2c); wsporniki — od krawędzi swobodnej przez łącznik termoz izolacyjny do przęsła zaplecza na max(L_c, l_{bd}) za podporą (PN-EN 1992-1-1 9.3.1.2(2), 9.3.1.4).
- Rysunek wygenerowany automatycznie z modelu model/budynek.yaml (wersja 1.0, 2026-09-25) — generatory lamela.views.

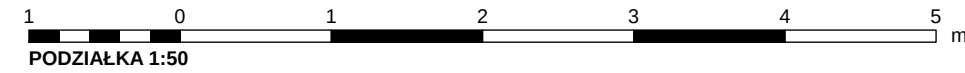

REW.	OPIS ZMIANY			DATA		
0	Wydanie — rysunek wygenerowany z modelu			2026-09-25		
PRACOWNIA PROJEKTOWA PRACOWNIA PROJEKTOWA — nazwa do uzupełnienia adres pracowni do uzupełnienia			STADIUM PT	BRANŻA KONSTRUKCJA (BO)		
INWESTOR (do uzupełnienia)						
OBIEKT / NAZWA ZAMIERZENIA BUDOWLANEGO Budynek mieszkalny jednorodzinny wolnostojący „Dom LAMELA”						
ADRES / LOKALIZACJA (NR DZIAŁKI, OBRĘB, JEDN. EWIDENCYJNA) ul. Lipowa (fikcyjna), dz. nr ewid. 123/4, obręb 0005 Przykładowo, gm. Przykładowo (fikcyjna)				KAT. OBIEKTU I		
FUNKCJA	IMIĘ I NAZWISKO		SPECJALNOŚĆ, NR UPRAWNIENI		DATA	PODPIS
Projektant	[DO UZUPEŁNIENIA]		[DO UZUPEŁNIENIA]			
Projektant (wsp.)	[DO UZUPEŁNIENIA]		[DO UZUPEŁNIENIA]			
Sprawdzający	nie dotyczy (art. 20 ust. 3 pkt 2 PB)		—			
Opracował	[DO UZUPEŁNIENIA]		[DO UZUPEŁNIENIA]			
TYTUŁ RYSUNKU ZBROJENIE GÓRNE STROPU NAD PARTEREM						
SKALA 1:50	FORMAT 690×420	DATA WYDANIA 2026-09-25	RODZAJ DOK. rysunek zbrojenia	NR RYSUNKU PT-BO-10	ARKUSZ 10/27	REW. 0