

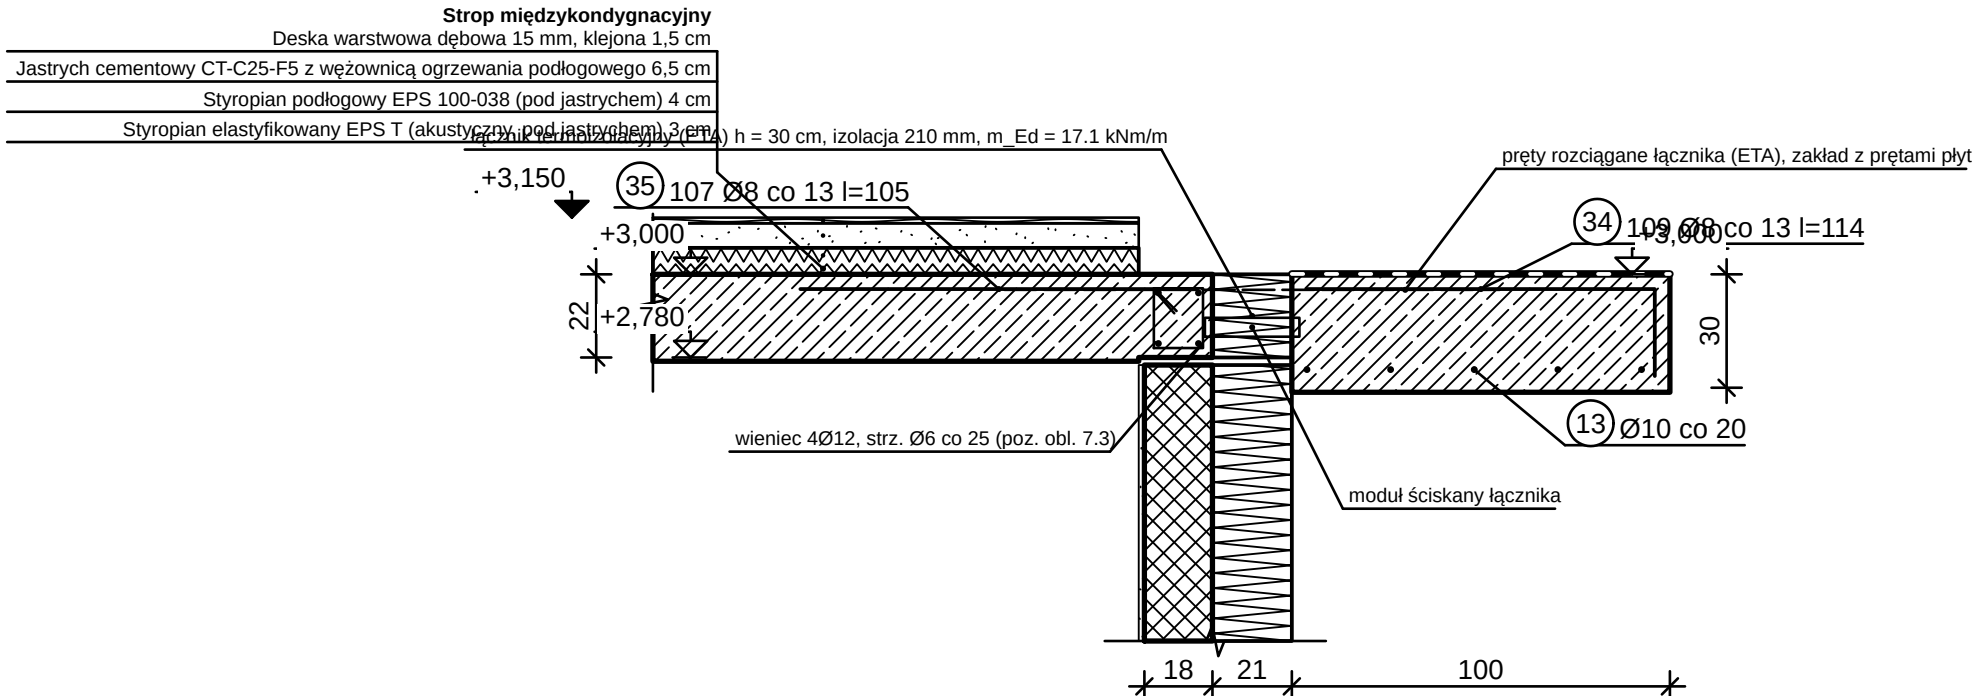


OBJAŚNIENIA I UWAGI


1. Wymiary w cm (mm w indeksie górnym, np. 24<sup>5</sup> = 24,5 cm), rzędne w m względem ±0,000 = 101,650 m n.p.m. (PL-EVRF2007-NH).  
2. Węzły stropów: warstwy wg przegród z modelu; zbrojenie — numery pozycji jak na arkuszach zbrojenia płyt poziomą (warstwa dolna/górna); wieniec wg pozycji obliczeniowej wienców.  
3. Otuliny (c\_nom) — wg klasy ekspozycji elementów (PN-EN 1992-1-1 tabl. 4.4N + NA, Δc\_dev = 10 mm); podkładki dystansowe wg PN-EN 13670.  
4. Stal B500SP (PN-H-93220), beton wg arkuszy zbrojenia; oznaczenia prętów wg PN-EN ISO 3766.  
5. Rysunek wygenerowany automatycznie z modelu model/budynek.yaml (wersja 1.0, 2026-09-25) — generatory lamela.views.

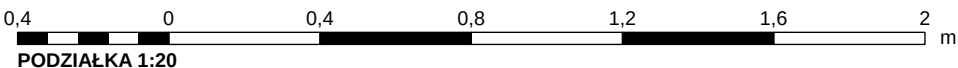

WĘZEL WSPORNIKA PL-E — ŁĄCZNIK TERMOIZOLACYJNY 1:20

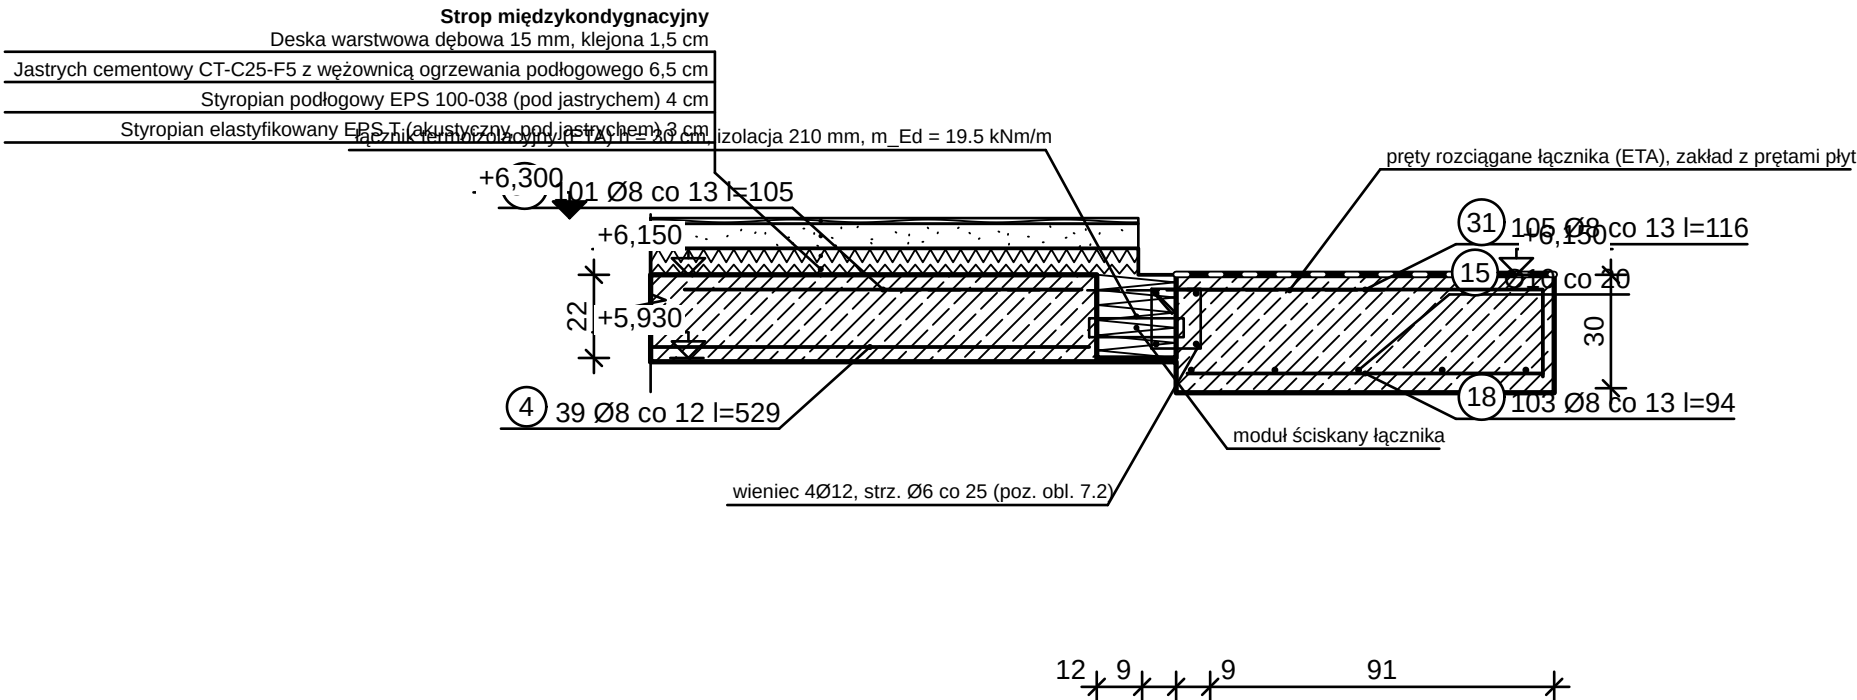

WĘZEL WSPORNIKA PL-2 — ŁĄCZNIK TERMOIZOLACYJNY 1:20

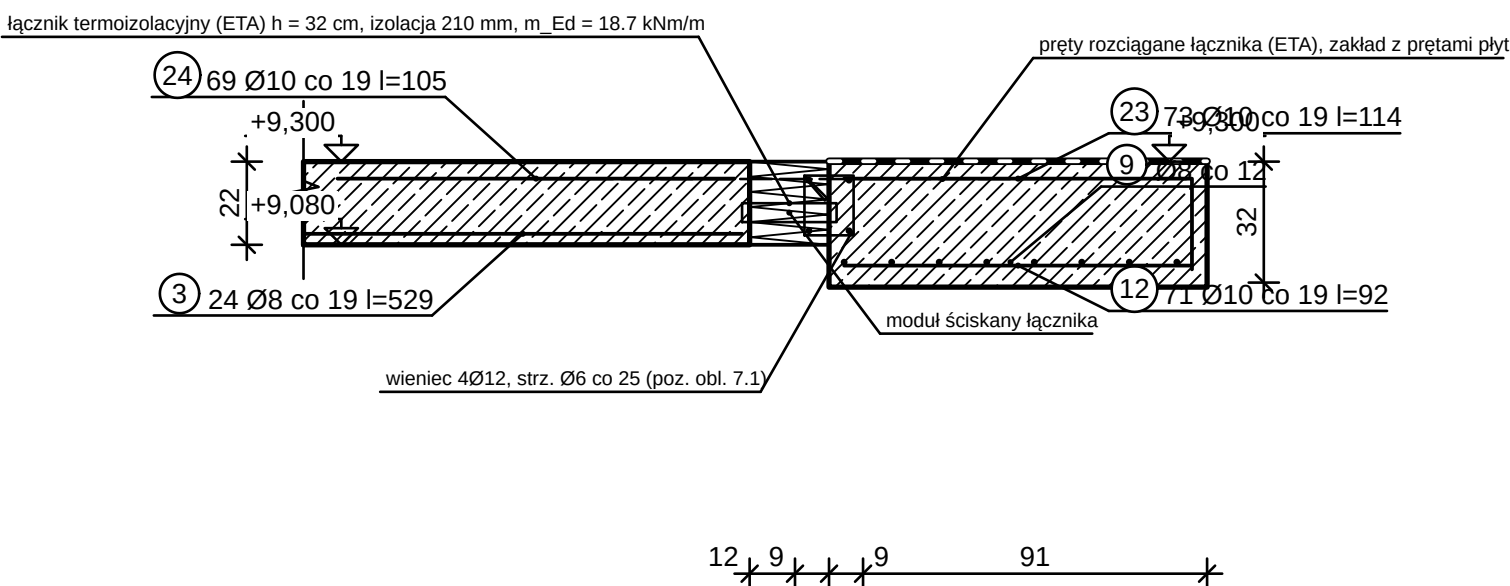

WĘZEL WSPORNIKA PL-3 — ŁĄCZNIK TERMOIZOLACYJNY 1:20

|   |                                         |                            |                                       |                            |                 |
|---|-----------------------------------------|----------------------------|---------------------------------------|----------------------------|-----------------|
| REW.   | OPIS ZMIANY                             |                            |                                       | DATA                       |                 |
| 0   | Wydanie — rysunek wygenerowany z modelu |                            |                                       | 2026-09-25                 |                 |
| PRACOWNIA PROJEKTOWA<br>PRACOWNIA PROJEKTOWA — nazwa do uzupełnienia<br>adres pracowni do uzupełnienia                                                      |                                         |                            | STADIUM<br>PT                         | BRANŻA<br>KONSTRUKCJA (BO) |                 |
| INWESTOR<br>(do uzupełnienia)   |                                         |                            |                                       |                            |                 |
| OBIEKT / NAZWA ZAMIERZENIA BUDOWLANEGO<br>Budynek mieszkalny jednorodzinny wolnostojący „Dom LAMELA”                                                        |                                         |                            |                                       |                            |                 |
| ADRES / LOKALIZACJA (NR DZIAŁKI, OBRĘB, JEDN. EWIDENCYJNA)<br>ul. Lipowa (fikcyjna), dz. nr ewid. 123/4, obręb 0005 Przykładowo, gm. Przykładowo (fikcyjna) |                                         |                            |                                       | KAT. OBIEKTU<br>I          |                 |
| FUNKCJA   | IMIĘ I NAZWISKO                         |                            | SPECJALNOŚĆ, NR UPRAWNIEN             | DATA                       | PODPIS          |
| Projektant   | [DO UZUPEŁNIENIA]                       |                            | [DO UZUPEŁNIENIA]                     |                            |                 |
| Projektant (wsp.)   | [DO UZUPEŁNIENIA]                       |                            | [DO UZUPEŁNIENIA]                     |                            |                 |
| Sprawdzający   | nie dotyczy (art. 20 ust. 3 pkt 2 PB)   |                            | —                                     |                            |                 |
| Opracował   | [DO UZUPEŁNIENIA]                       |                            | [DO UZUPEŁNIENIA]                     |                            |                 |
| TYTUŁ RYSUNKU<br>WĘZŁY WSPORNIKÓW Z ŁĄCZNIKAMI TERMOIZOLACYJNYMI                                                                                            |                                         |                            |                                       |                            |                 |
| SKALA<br>1:20   | FORMAT<br>310×594                       | DATA WYDANIA<br>2026-09-25 | RODZAJ DOK.<br>przekrój konstrukcyjny | NR RYSUNKU<br>PT-BO-18     | ARKUSZ<br>18/27 |
|   |                                         |                            |                                       |                            | REW.<br>0       |