

A

B

C

D

E

F

G

H

J

K

L

M

N

P

Q

R

ZESTAWIENIE STALI

Poz.	Ø [mm]	Kształt ISO 3766, wymiary [cm]	Długość [cm]	Liczba [szt.]	Elem.	Ø8 [m]	Ø12 [m]	Ø14 [m]
1	14	21: a=25 b=536 c=25	581	3	B6			17.43
2	12	21: a=25 b=536 c=25	582	2	B6		11.64	
3	8	51: a=15 b=35	116	22	B6	25.52		
4	14	21: a=25 b=568 c=25	613	2	B7			12.26
5	12	21: a=25 b=568 c=25	614	2	B7		12.28	
6	8	51: a=20 b=80	216	16	B7	34.56		
7	12	21: a=25 b=286 c=25	332	17	B8		56.44	
8	8	51: a=20 b=45	146	73	B8	106.58		
9	12	21: a=25 b=243 c=25	289	4	N16		11.56	
10	8	51: a=13 b=49	140	8	N16	11.20		
Długość całkowita [m]						177.9	91.9	29.7
Masa jednostkowa [kg/m]						0.395	0.888	1.208
Masa [kg]						70.2	81.6	35.9
RAZEM stal B500SP [kg]								187.7

B6, B7: beton C30/37, XC1, otulina strzemiion c_nom = 25 mm (tabl. 4.4N + NA).
B8, B9, B10, N16: beton C25/30, XC1, otulina strzemiion c_nom = 25 mm (tabl. 4.4N + NA).

A

B

C

D

E

F

G

H

J

K

L

M


N

P


Q

R


B7 — 25×85 cm, C30/37 (poz. 5.16)

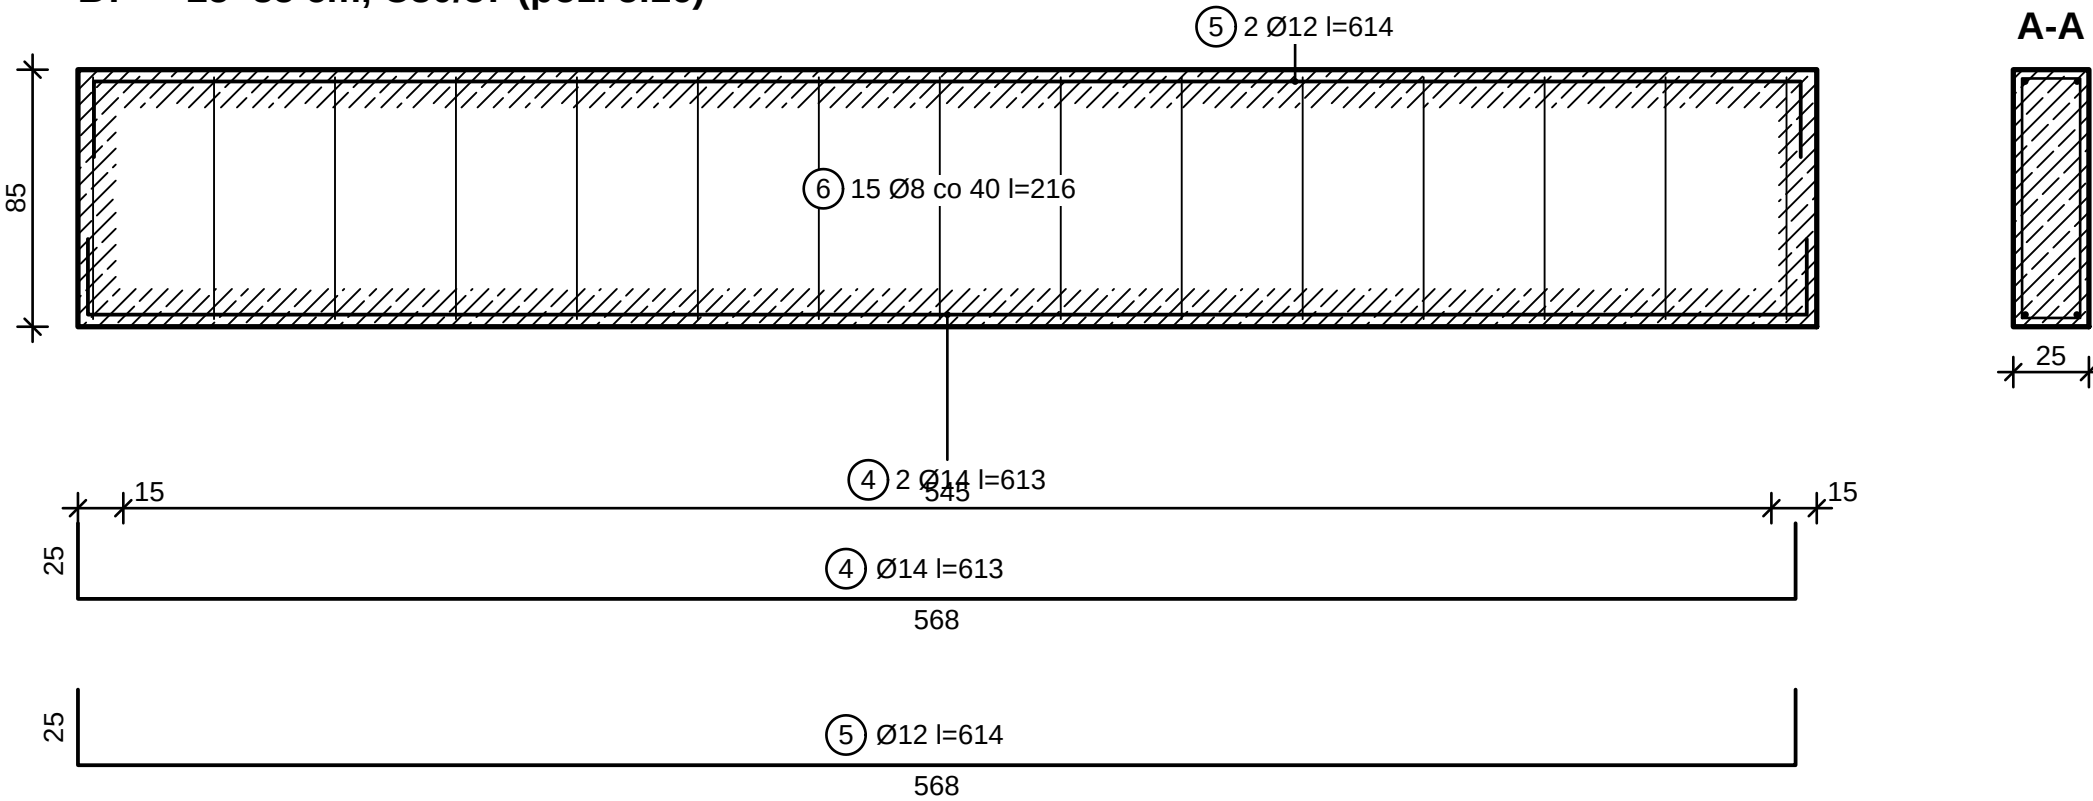


B6 — 20×40 cm, C30/37 (poz. 5.1)

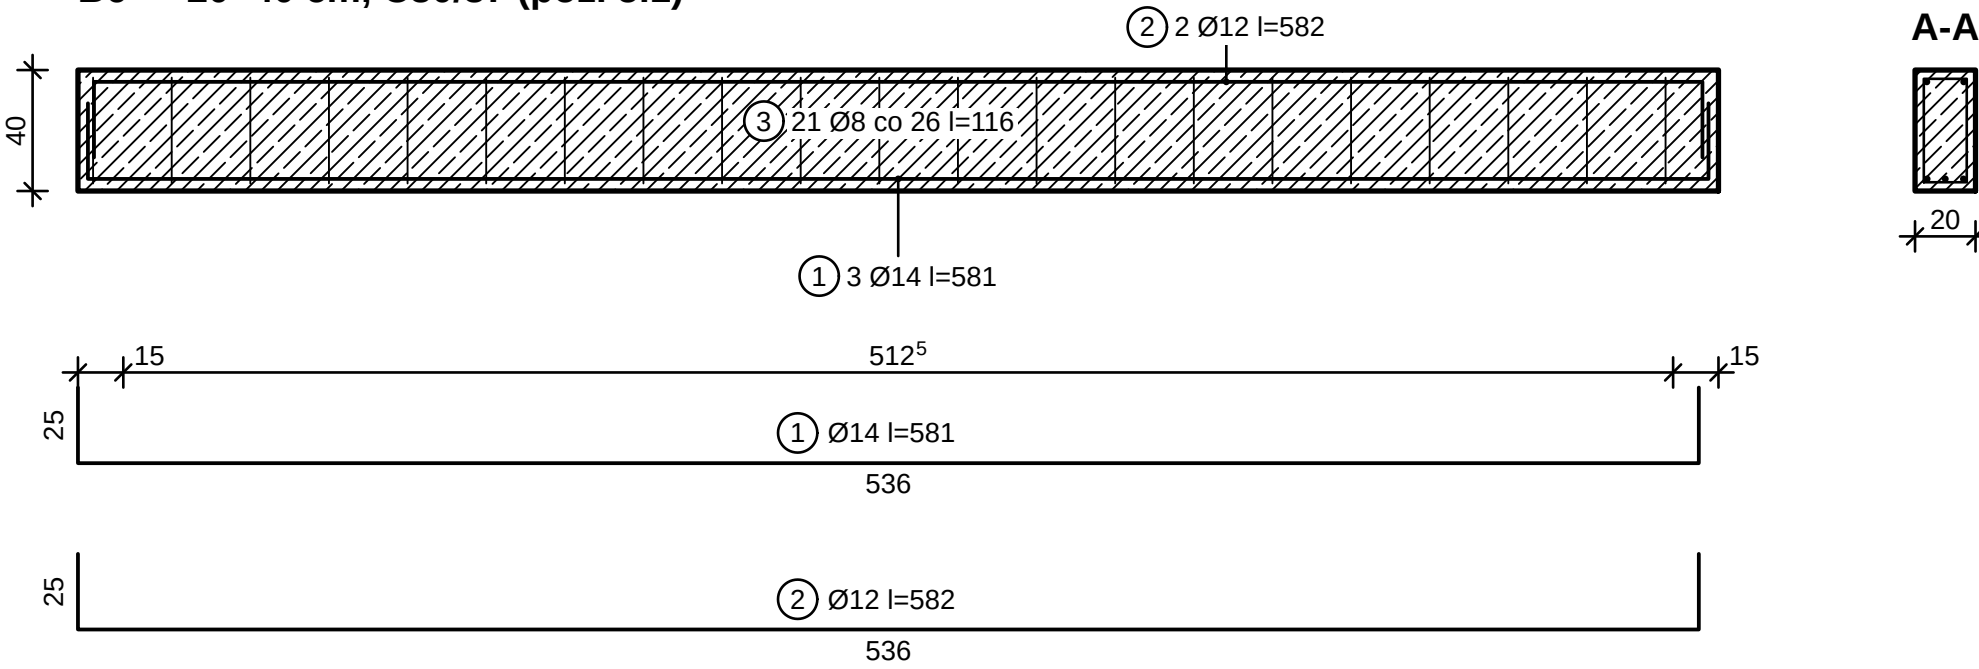


N16 — 18×54 cm, C25/30 (poz. 5.13)

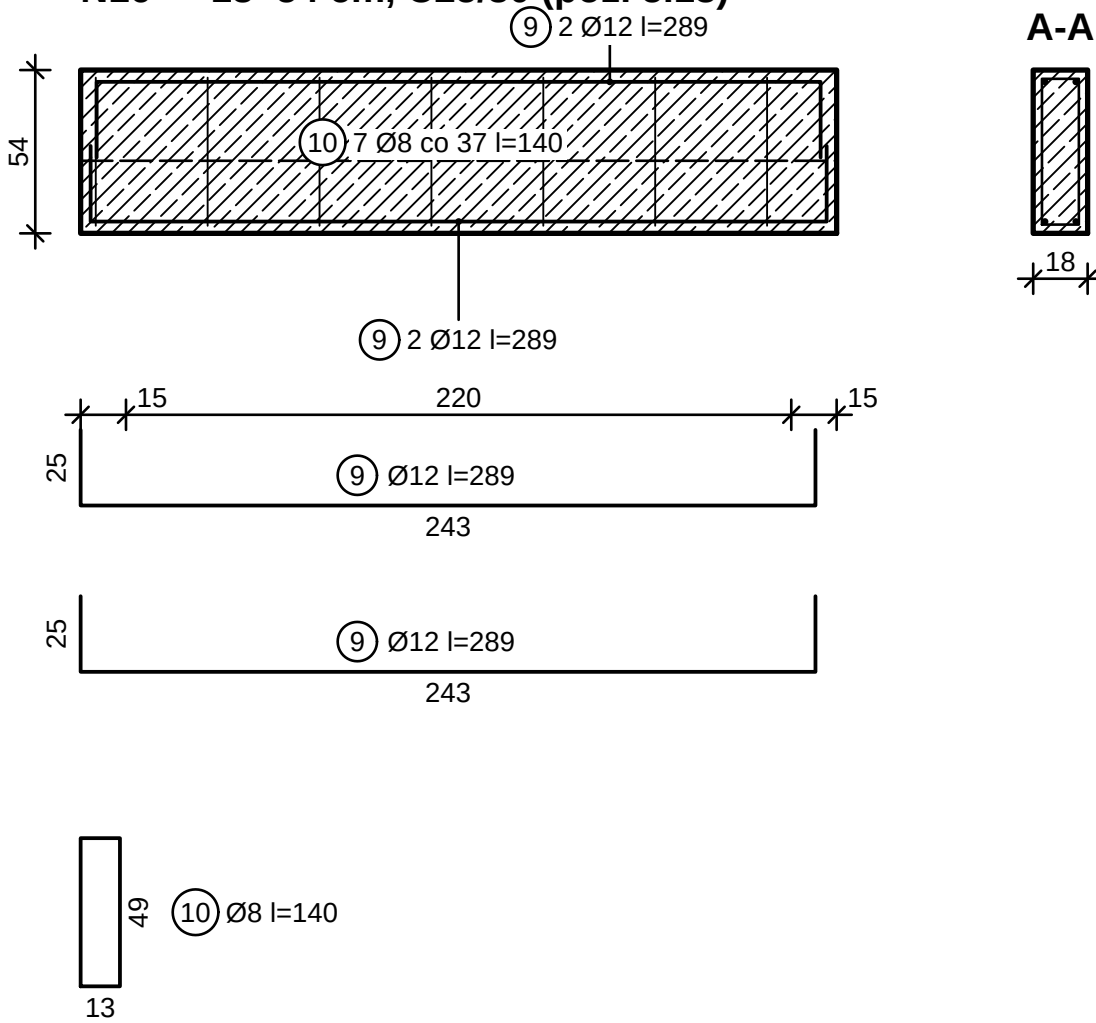


B8 — 25×50 cm, C25/30 (poz. 5.17)

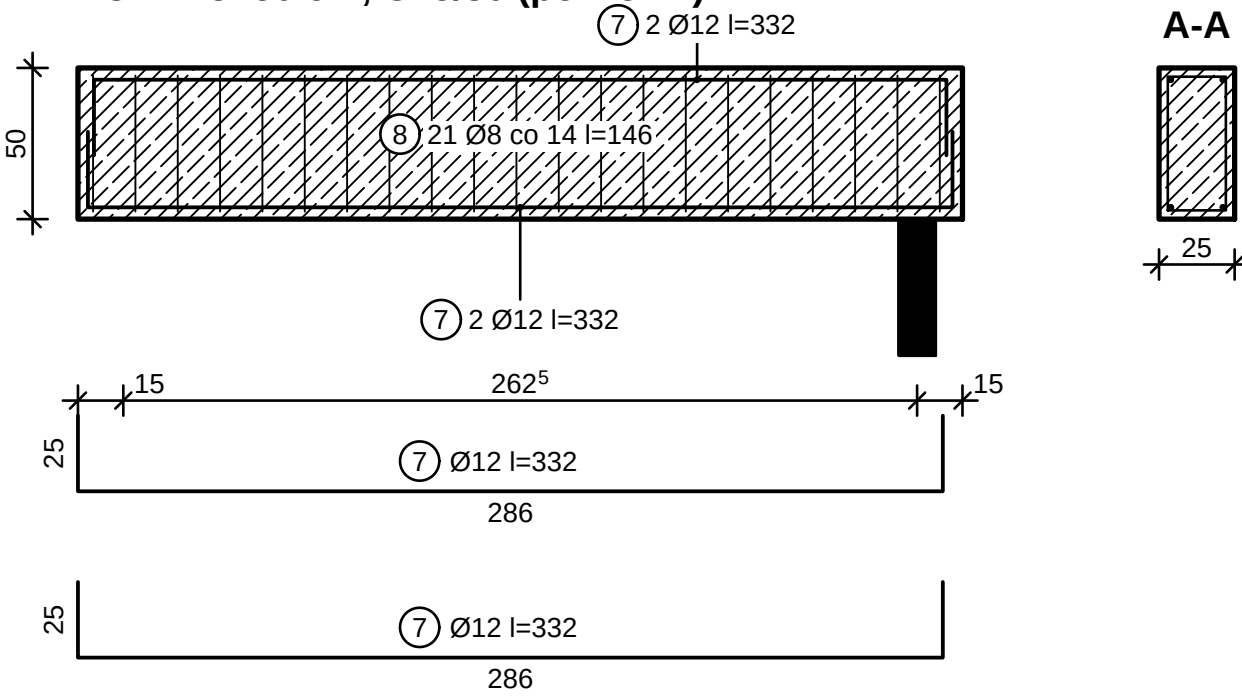


B9 — 25×50 cm, C25/30 (poz. 5.12)

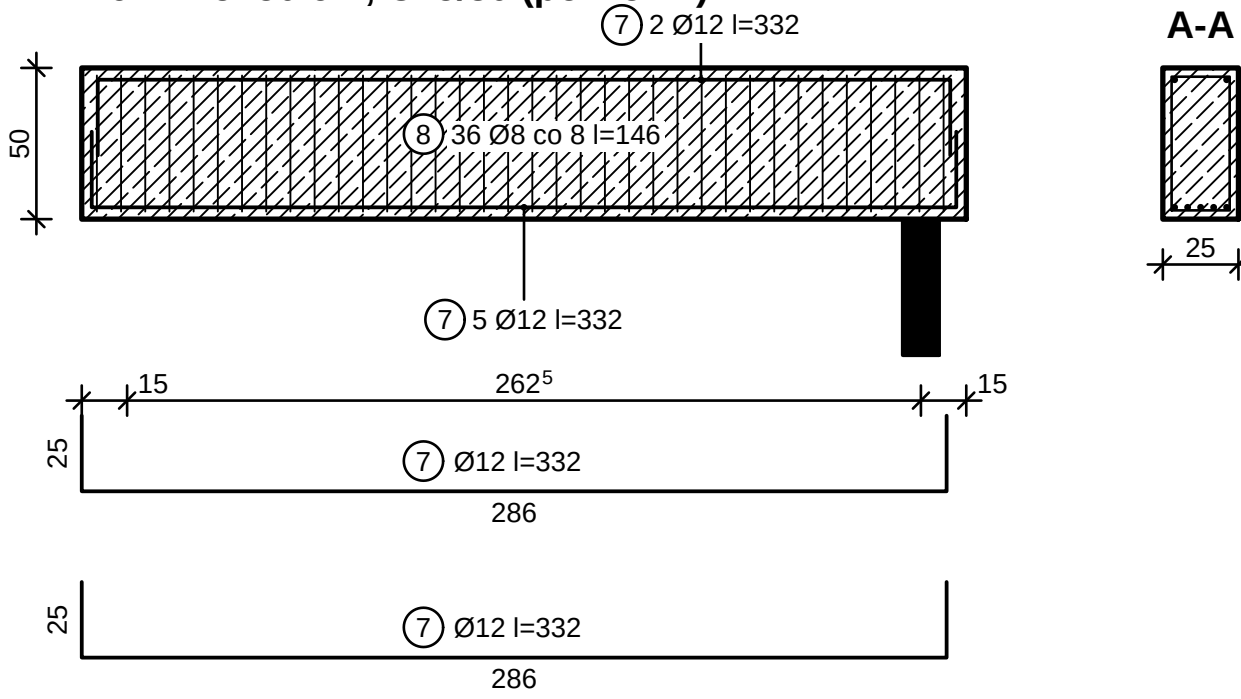

B10 — 25×50 cm, C25/30 (poz. 5.2)

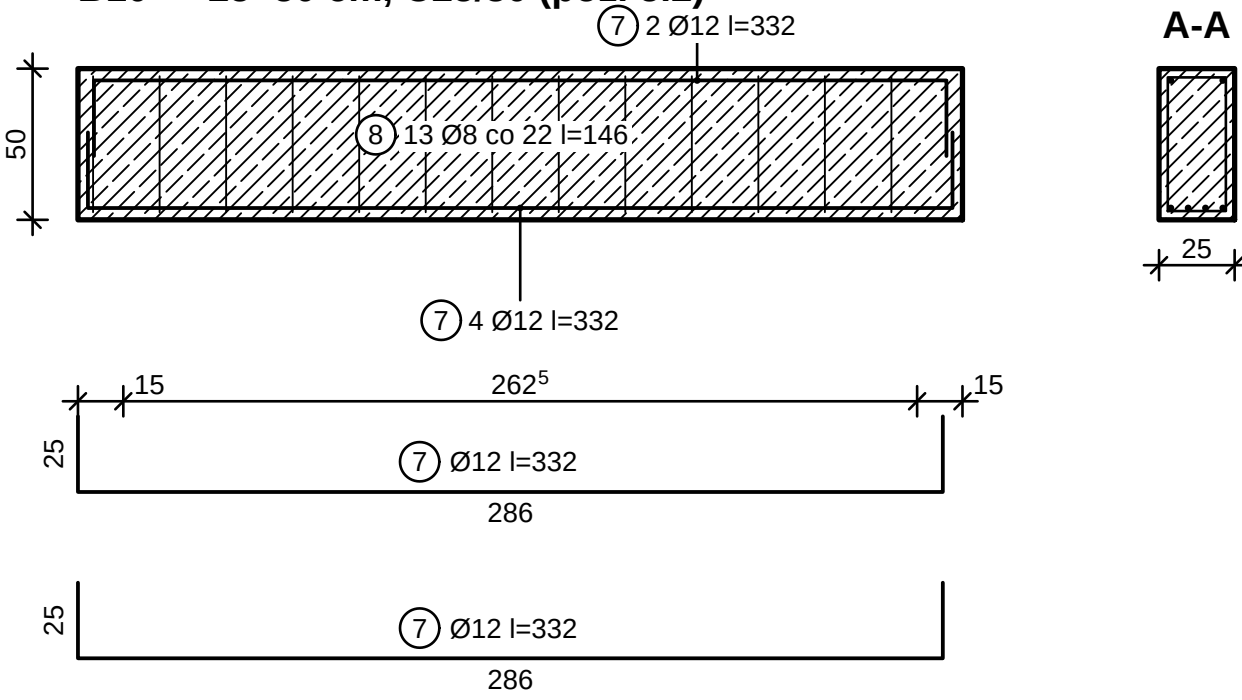

ZBROJENIE BELEK B6, B7, B8, B9, B10, N16 1:25

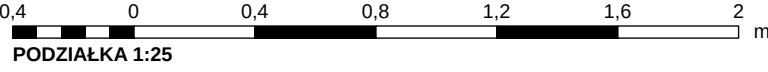

REW.	OPIS ZMIANY	DATA
0	Wydanie — rysunek wygenerowany z modelu	2026-09-25
PRACOWNIA PROJEKTOWA	STADIUM	BRANZA
PRACOWNIA PROJEKTOWA — nazwa do uzupełnienia	PT	KONSTRUKCJA (BO)
adres pracowni do uzupełnienia		
INWESTOR		
(do uzupełnienia)		
OBIEKT / NAZWA ZAMIERZENIA BUDOWLANEGO		
Budynek mieszkalny jednorodzinny wolnostojący „Dom LAMELA”		
ADRES / LOKALIZACJA (NR DZIAŁKI, OBRĘB. JEDN. EWIDENCYJNA)	KAT. OBIEKTU	
ul. Lipowa (fikcyjna), dz. nr ewid. 123/4, obręb 0005 Przykładowo, gm. Przykładowo (fikcyjna)	I	
FUNKCJA	IMIĘ I NAZWISKO	SPECJALNOŚĆ, NR UPRAWNIEN
Projektant	[DO UZUPEŁNIENIA]	[DO UZUPEŁNIENIA]
Projektant (wsp.)	[DO UZUPEŁNIENIA]	[DO UZUPEŁNIENIA]
Sprawdzający	nie dotyczy (art. 20 ust. 3 pkt 2 PB)	—
Opracował	[DO UZUPEŁNIENIA]	[DO UZUPEŁNIENIA]
TYTUŁ RYSUNKU		
ZBROJENIE BELEK (2)		
SKALA	FORMAT	DATA WYDANIA
1:25	500×841	2026-09-25
RODZAJ DOK.	NR RYSUNKU	ARKUSZ
rysunek zbrojenia	PT-BO-21	21/27
	REW.	
	0	