



odcinek kordonu 100 mm (wygląda 1:1)

wysokość budynku wg § 6 WT: H = 9,97 m


ELEWACJA POŁUDNIOWA (OGRODOWA) 1:50

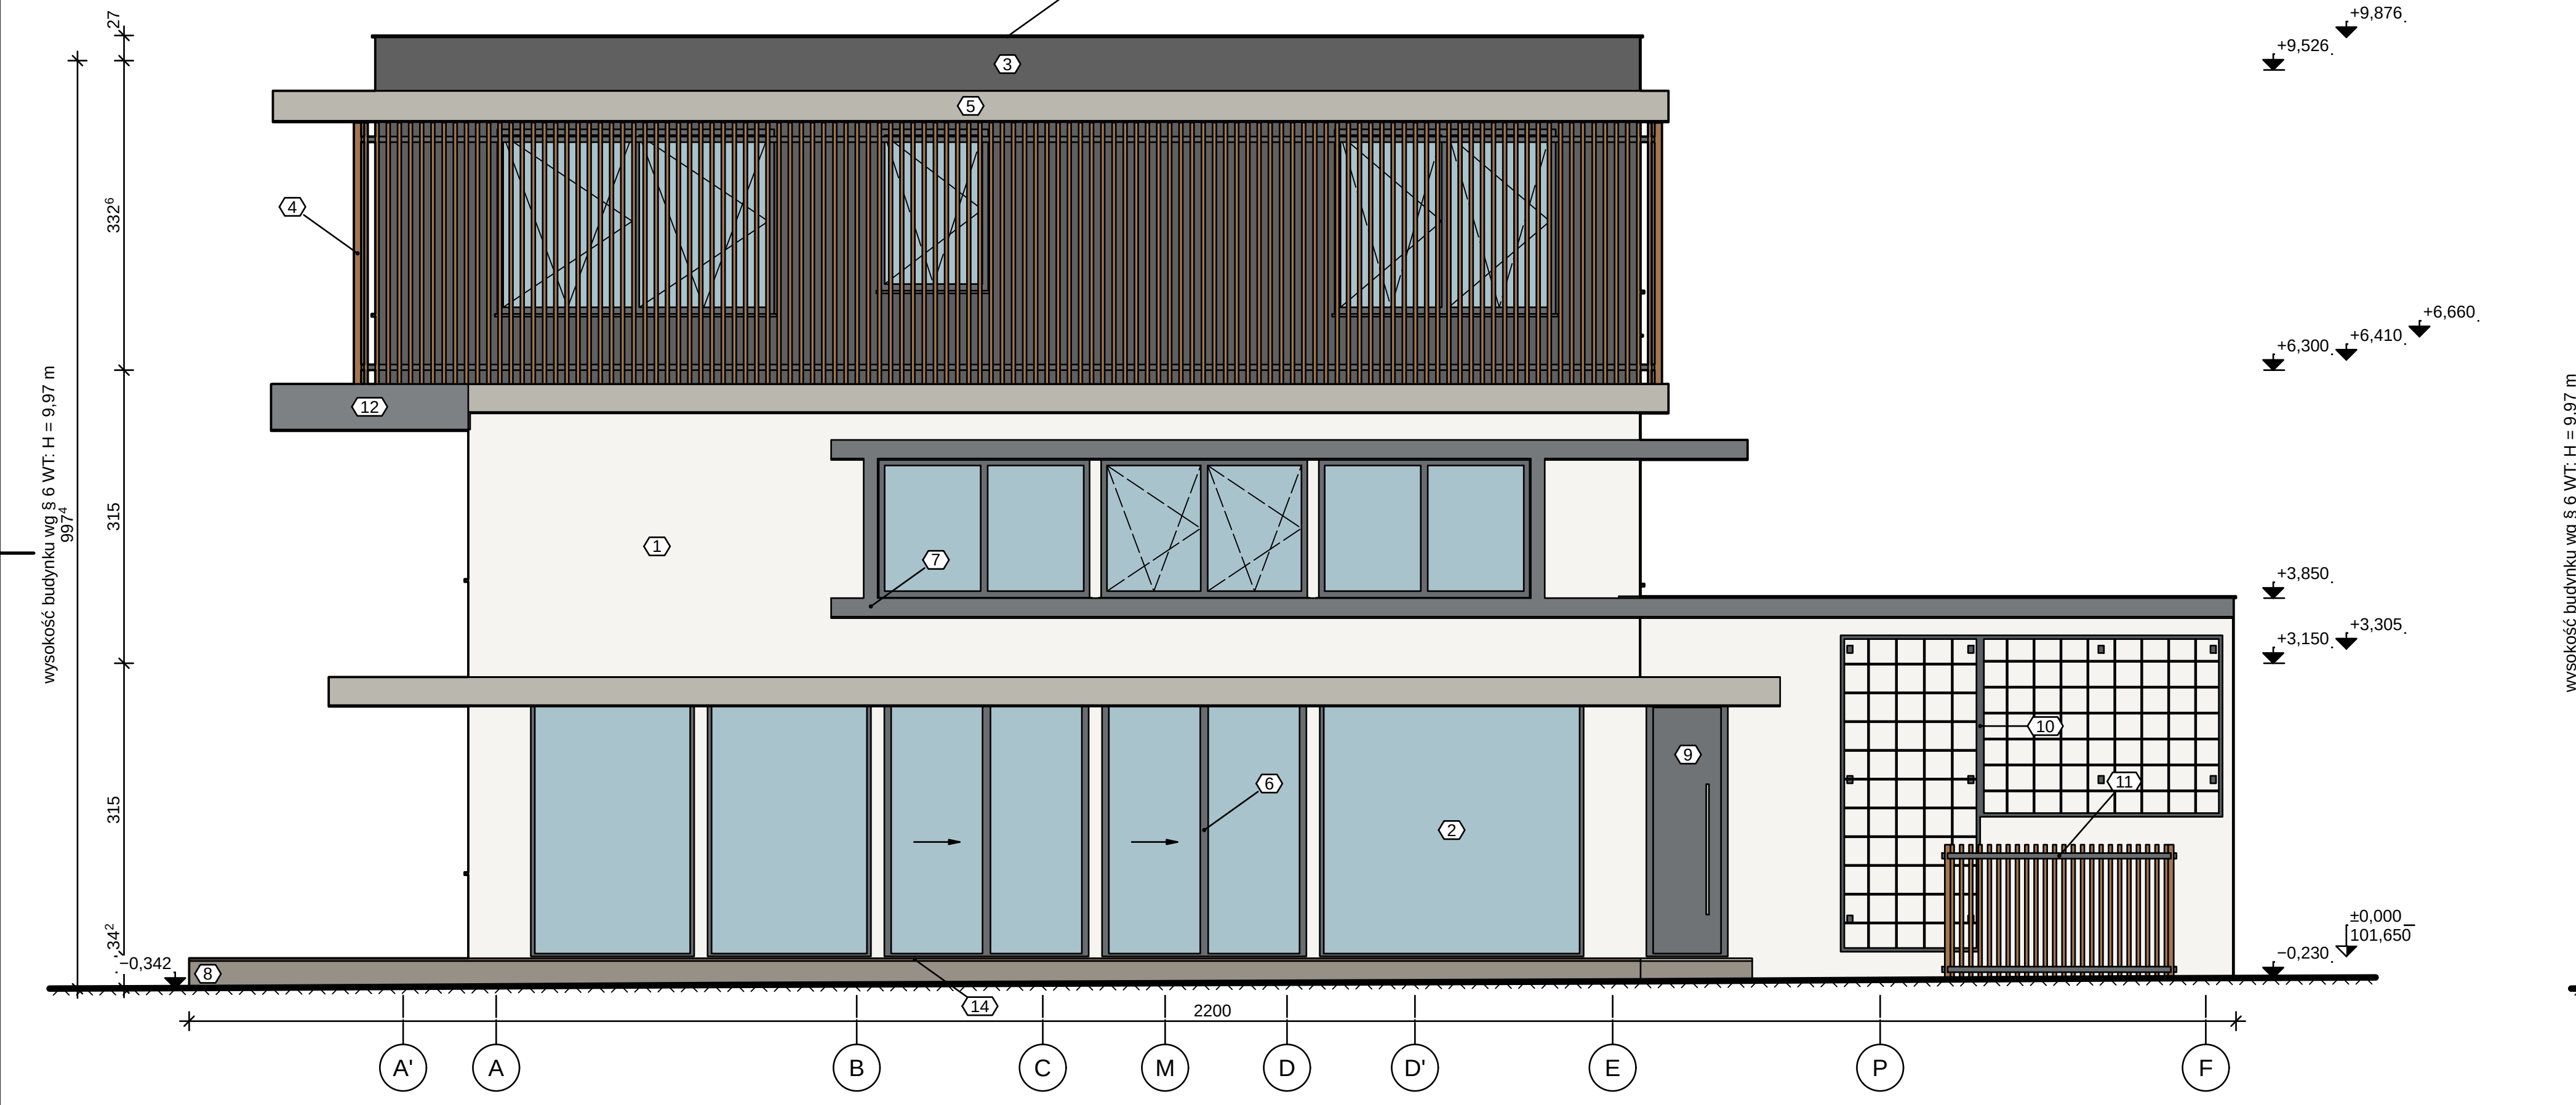


ELEWACJA WSCHODNIA 1:50

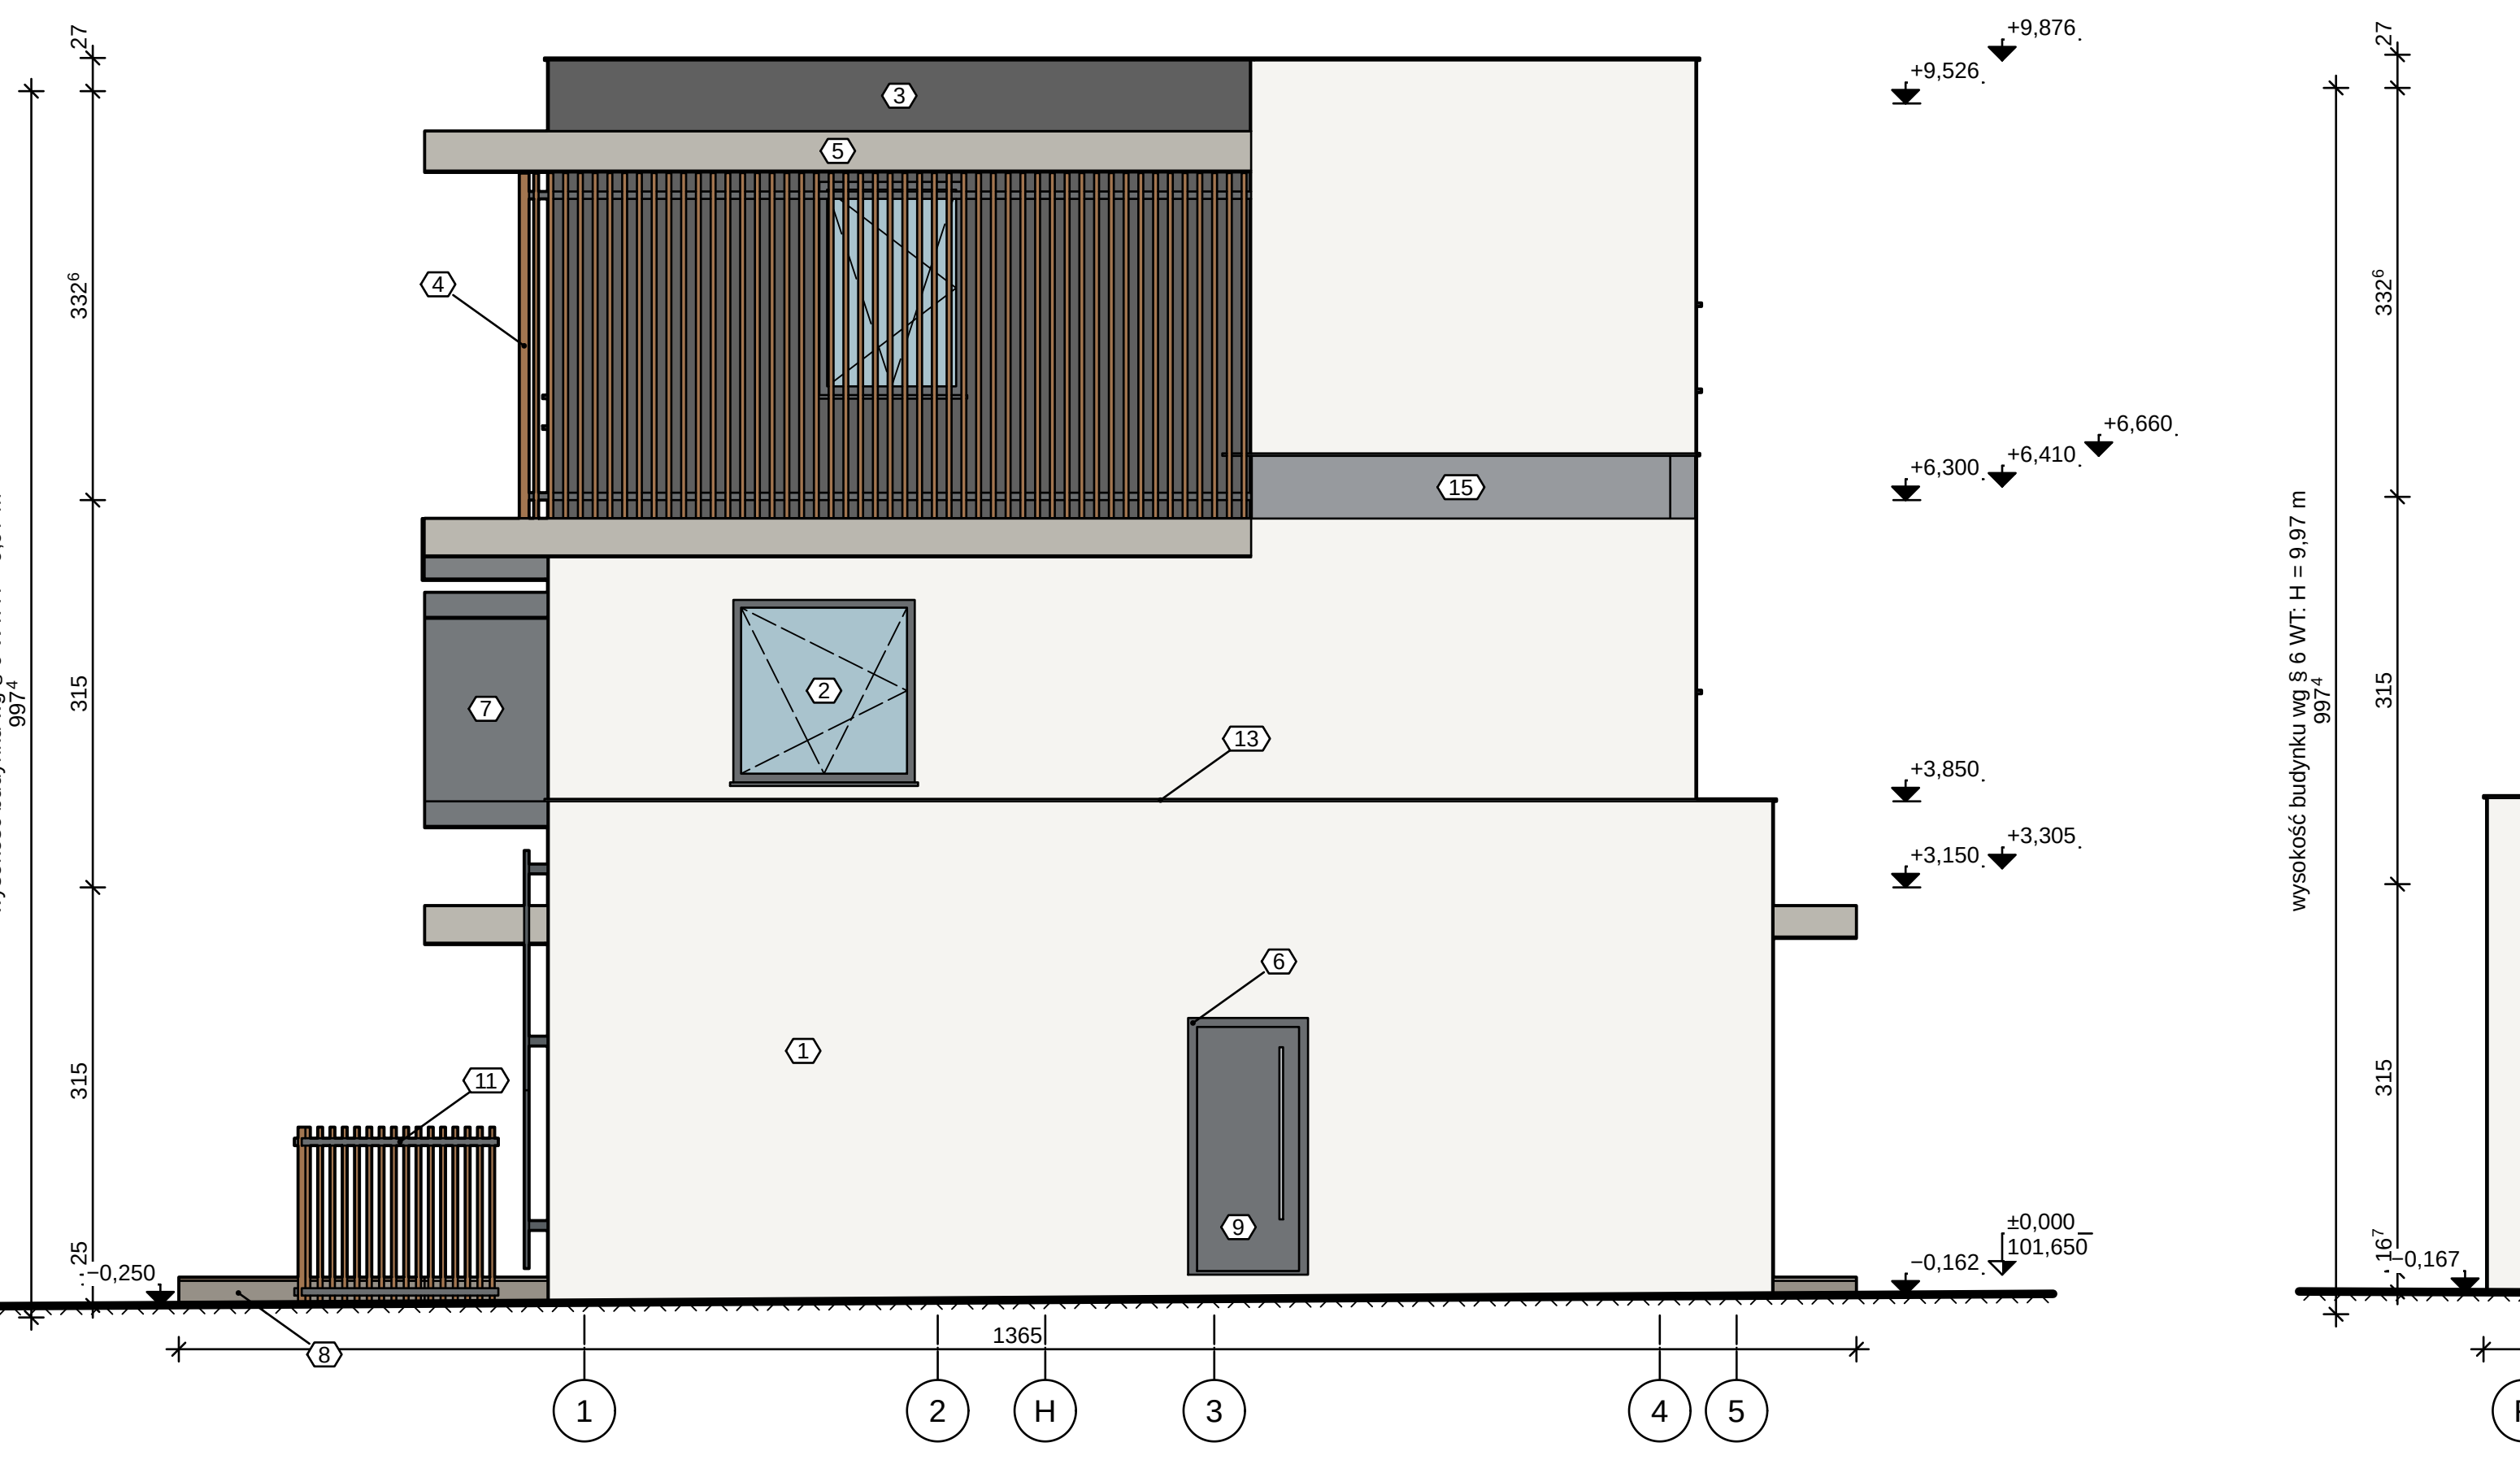

ELEWACJA PÓŁNOCNA (OD ULICY) 1:50

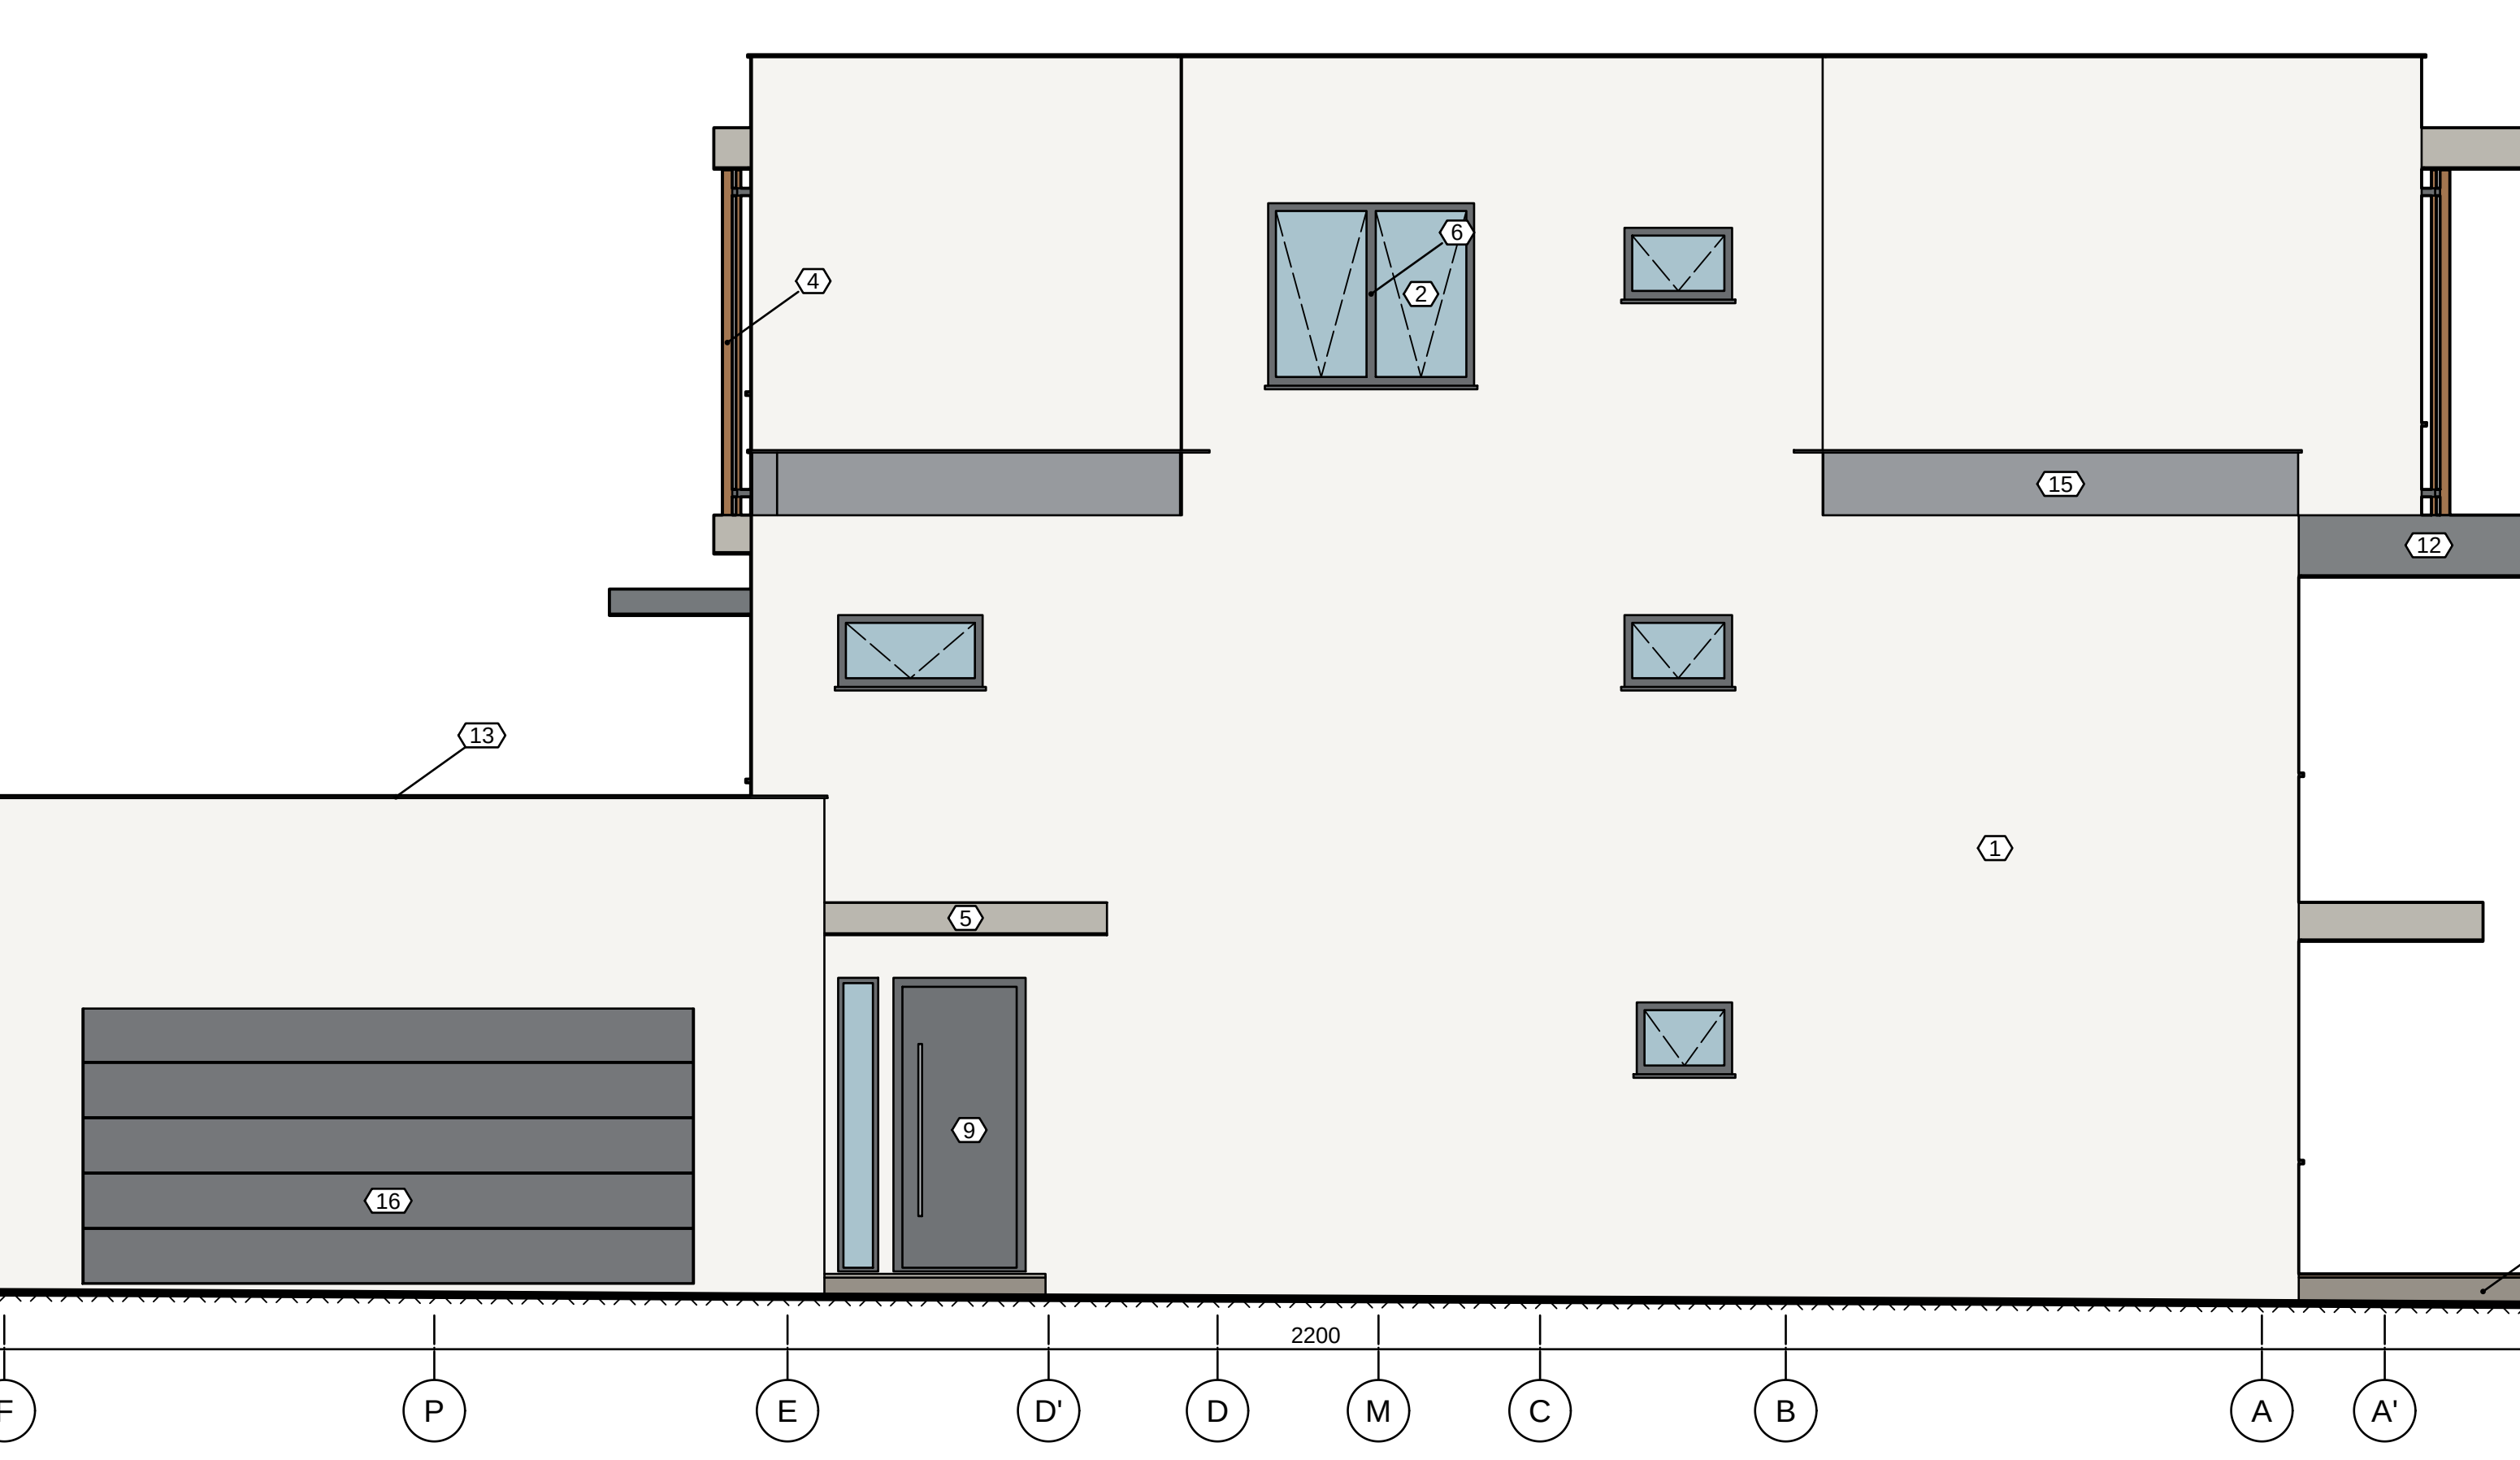

ELEWACJA ZACHODNIA 1:50

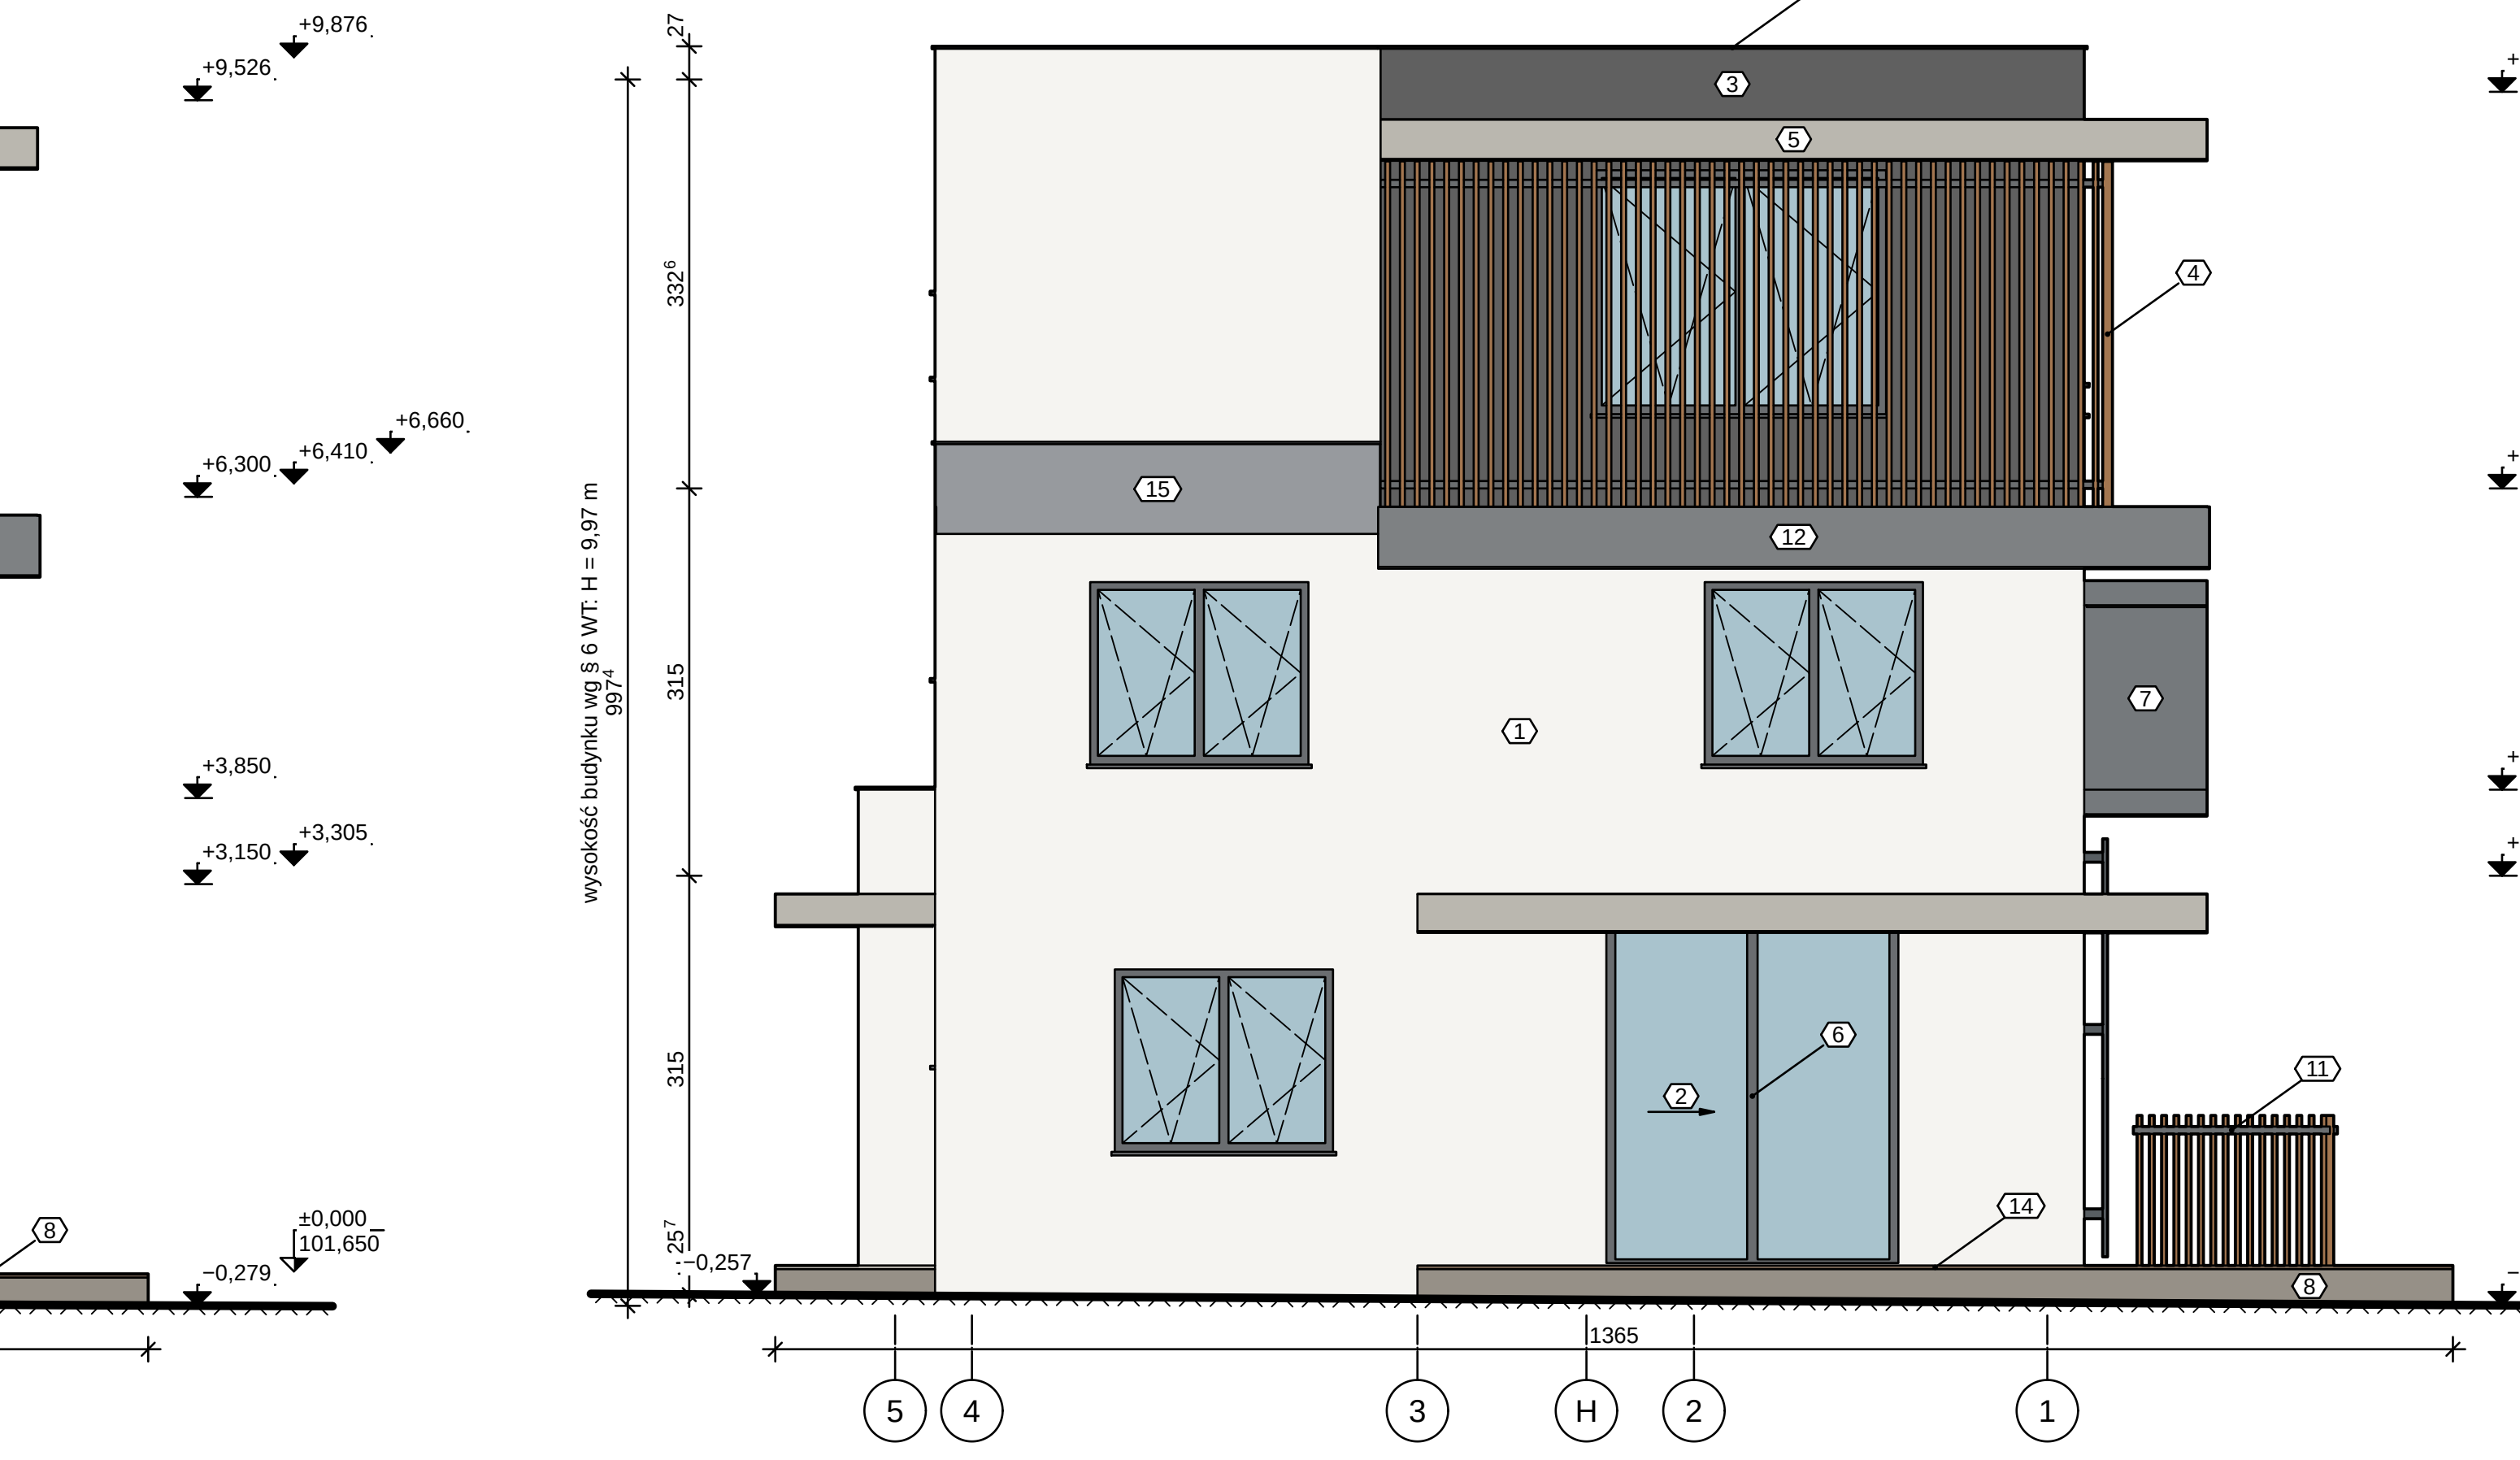

KOLORYSTYKA I MATERIAŁY ELEWACJI

1	ETICS: warstwa zbrojona + tynk silikonowy 1,5 mm (biały) / jasnoszary NCS S 1500-N (TYNK_SIL)
2	Szkoło (szyby zespolone) [SZKLO]
3	Membrana fasadowa wiatroizolacyjna UV-stabilna, czarna (sd = 0,02 m) [MEMB_WIATR]
4	Lamele elewacyjne 40x80 mm, drewno termojest (klasa 1 trwałości), olejowane [DREWNO_TERMO]
5	Żelbet C30/37 XC4XF1 (krawędzie płyt wysuniętych, atyki, belki) [ZB_C30]
6	Stołarka — profile aluminiowe, antracyt [RAMA_ALU]
7	Rama boku C: ruszt stalowy ocynkowany w okładzinie z blachy aluminiowej RAL 7016 (pusta w środku) [RAMA_C]
8	Podbudowa nawierzchni (rusztywo) [NAW_PODBUDOWA]
9	Drzwi zewnętrzne, płycina aluminiowa [DRZWI_ZEWNI]
10	Stal S235 ocynkowana ogniowo, malowana proszkowo RAL 7016 — kratownica pręcy (pręty Ø12 w siatce 0,30 m; rama 40x40) [STAL_OCYNK]
11	Stal malowana proszkowo (balustrady, rylce) [STAL_BAL]
12	Podsiłka zewnętrzna: płyta włóknocementowa 12 mm na ruszcie, RAL 7016 [PODSUF]
13	Obróbki blacharskie (blacha powlekana) [OBRÓBKA_BLACH]
14	Deska tarasowa [NAW_DESKA]
15	Styropian grafitowy EPS 031 (ETICS, NRO w systemie) [EPS031]
16	Brama garażowa segmentowa [BRAMA_GAR]

OBJAŚNIENIA I UWAGI

- Wymiary w cm (mm w indeksie górnym, np. 24" = 24,5 cm), rzędne w m względem s.0.000 = 101,650 m n.p.m. (PL-EVRP2007-NH).
- Rzędne: rdz. i rdz. zaczerpnięte — poziom wykończenia, niezaczerpnięte — kopiec, w pobliżu zaczerpnięte — poziom s.0.000 z rzędnej bezwzględnej (PN-B-01025).
- Wysokość budynku wg § 6 WT: od terenu przy najniższym poziomym wejściu (-0,348) do wierzchu stropodachu D1 (+9,626) — H = 9,97 m (bez atyki).
| 4 | Kolorystyka orientacyjna wg kolorów materiałów w modelu (do potwierdzenia wzrokiem RAL/NCSS). |
| 5 | Rysunek wygenerowany automatycznie z modelu model/budynki/yami (wersja 1.0, 2026-09-25) — generatory lamela views. |

1 0 1 2 3 4 5 m

PODZIAŁKA 1:50

REW.	OPIS ZMIANY	DATA
0	Wydanie — rysunek wygenerowany z modelu	2026-09-25

PRACOWNIA PROJEKTOWA	BRANŻA	STADIUM	ARCHITECTURA (AR)
PRACOWNIA PROJEKTOWA — nazwa do uzupełnienia	PB		

adres pracowni do uzupełnienia

INWESTOR (do uzupełnienia)

OBIEKT / NAZWA ZAMIERZENIA BUDOWLANEGO

Budynek mieszkalny jednorodzinny wolnostojący „Dom LAMELA”

ADRES / LOKALIZACJA (NR DZIAŁKI, OBREB, JEDN. EWIDENCYJNA)

ul. Lipowa (fikcyjna), dz. nr ewid. 123/4, obręb 0005 Przykładowo, gm. Przykładowo (fikcyjna)

KAT. OBIEKTU

I

FUNKCJA	IMIĘ I NAZWISKO	SPECJALNOŚĆ, NR UPRAWNIEN	DATA	PODPIS
Projektant	[DO UZUPEŁNIENIA]	[DO UZUPEŁNIENIA]		
Projektant (wsp.)	[DO UZUPEŁNIENIA]	[DO UZUPEŁNIENIA]		
Sprawdzający	nie dotyczy (art. 20 ust. 3 pkt 2 PB)	—		
Opracował	[DO UZUPEŁNIENIA]	[DO UZUPEŁNIENIA]		

TYTUŁ RYSUNKU	SKALA	FORMAT	DATA WYDANIA	RODZAJ DOK.	NR RYSUNKU	ARKUSZ	REW.
ELEWACJE	1:50	2050x297	2026-09-25	elewacja	PB-AR-05	5/5	0