

PT-1 AR

PROJEKT TECHNICZNY

Tom PT-1 — architektura (AR)

Tom 1 z 4 · branża: architektura · element projektu budowlanego wg art. 34 ust. 3 PB

PRZYKŁAD – NIE DO ZŁOŻENIA

Działka, MPZP, warunki gruntowe i sieci: [DANE PRZYKŁADOWE – FIKCYJNE]. Dane osobowe, numery uprawnień, podpisy i dokumenty organów — pola do uzupełnienia. Opracowanie jest szablonem zgodnym z RPB i nie może zostać złożone bez danych rzeczywistych (rejestr wymagań, sekcja E).

NAZWA ZAMIERZENIA
BUDOWLANEGO

Budowa budynku mieszkalnego jednorodzinnego wolnostojącego „Dom LAMELA” z garażem dwustanowiskowym w bryle budynku, wraz z zagospodarowaniem terenu i infrastrukturą towarzyszącą (zjazd, dojazd i dojście, miejsca postojowe, zbiornik retencyjny wód opadowych, ogrodzenie)

OBIEKT BUDOWLANY

Budynek mieszkalny jednorodzinny wolnostojący „Dom LAMELA”

ADRES OBIEKTU

ul. Lipowa (bez nr porządkowego), gm. Przykładowo, woj. wielkopolskie [DANE PRZYKŁADOWE – FIKCYJNE]

KATEGORIA OBIEKTU
BUDOWLANEGO

I – budynki mieszkalne jednorodzinne (załącznik do ustawy – Prawo budowlane)

DZIAŁKA EWIDENCYJNA

nr 123/4, obręb 0005 Przykładowo, gm. Przykładowo, jedn. ewid.: [DO UZUPEŁNIENIA: jednostka ewidencyjna — kod TERYT WWPPGG_R i nazwa]
identyfikator działki ewidencyjnej: [DO UZUPEŁNIENIA: kod TERYT jedn. ewid. WWPPGG_R].0005.123/4

INWESTOR

[DO UZUPEŁNIENIA: imię i nazwisko lub nazwa inwestora]
adres: [DO UZUPEŁNIENIA: adres inwestora]

OPRACOWANIE — AUTORZY (§ 7 UST. 2 PKT 3 RPB)

Funkcja, branża	Imię i nazwisko	Specjalność i nr uprawnień budowlanych	Zakres opracowania	Podpis
Projektant architektura	[DO UZUPEŁNIENIA: imię i nazwisko]	architektoniczna bez ograniczeń nr upr.: [DO UZUPEŁNIENIA: nr uprawnień budowlanych]	PZT i PAB — rozwiązania architektoniczne i zagospodarowanie działki; PT-1 AR; informacja BIOZ	
Sprawdzający	nie dotyczy (art. 20 ust. 3 pkt 2 PB)			

DATA OPRACOWANIA

25 września 2026 r.

REWIZJA / PLIK

rew. 0 · PT_1_AR_2026.09.25.pdf

ZAWARTOŚĆ TOMU

PT-1 AR – Projekt techniczny

Postać elektroniczna (RPB § 2b): plik PDF opatruje podpisem kwalifikowanym, osobistym albo zaufanym każda osoba opracowująca daną część w zakresie objętym plikiem (§ 7 ust. 4a RPB); pole „Podpis” wypełnia się wyłącznie w postaci papierowej (§ 7 ust. 2 pkt 4 RPB).

SPIS TREŚCI

PT-1 AR — Projekt techniczny

DOKUMENTY DOŁĄCZONE DO PROJEKTU (§ 7 UST. 5 PKT 3 RPB)

Oświadczenie projektanta (art. 34 ust. 3d pkt 3 PB)	3
---	---

CZĘŚĆ OPISOWA (§ 7 UST. 5 PKT 1 RPB)

1. Rozwiązania konstrukcyjno-materiałowe przegród	4
2. Dane dotyczące warunków ochrony przeciwpożarowej	5

CZĘŚĆ RYSUNKOWA (§ 7 UST. 5 PKT 2 RPB)

Karta części rysunkowej i wykaz rysunków	6
T-AR-01 RZUT PARTERU (1:50)	rys.
T-AR-02 RZUT PIĘTRA (1:50)	rys.
T-AR-03 RZUT DACHU (1:50)	rys.
T-AR-04 PRZEKRÓJ A-A (1:50)	rys.
T-AR-05 PRZEKRÓJ B-B (1:50)	rys.
T-AR-06 ELEWACJA POŁUDNIOWA (1:50)	rys.
T-AR-07 ELEWACJA PÓŁNOCNA (1:50)	rys.
T-AR-08 ELEWACJA WSCHODNIA (1:50)	rys.
T-AR-09 ELEWACJA ZACHODNIA (1:50)	rys.

Numeracja stron odrębna dla elementu (§ 6 ust. 1 RPB); rysunki oznaczono numerem rysunku (§ 6 ust. 3 RPB). Pozycje spisu są odnośnikami w pliku PDF.

[DO UZUPEŁNIENIA: miejscowość], dnia 25 września 2026 r.

OŚWIADCZENIE PROJEKTANTA

o sporządzeniu projektu technicznego zgodnie z obowiązującymi przepisami, zasadami wiedzy technicznej, PZT, PAB i rozstrzygnięciami dotyczącymi zamierzenia budowlanego
(art. 34 ust. 3d pkt 3 i art. 41 ust. 4a pkt 2 ustawy z dnia 7 lipca 1994 r. – Prawo budowlane (t.j. Dz.U. 2026 poz. 524 ze zm.))

Zamierzenie budowlane	Budowa budynku mieszkalnego jednorodzinnego wolnostojącego „Dom LAMELA” z garażem dwustanowiskowym w bryle budynku, wraz z zagospodarowaniem terenu i infrastrukturą towarzyszącą (zjazd, dojazd i dojście, miejsca postojowe, zbiornik retencyjny wód opadowych, ogrodzenie)
Obiekt, kategoria	Budynek mieszkalny jednorodzinny wolnostojący „Dom LAMELA” — kategoria I
Adres, działka	ul. Lipowa (bez nr porządkowego), gm. Przykładowo, woj. wielkopolskie [DANE PRZYKŁADOWE – FIKCYJNE]; działka ewid. nr 123/4, obręb 0005 „Przykładowo”, gm. Przykładowo; identyfikator: [DO UZUPEŁNIENIA: kod TERYT jedn. ewid. WWPPGG_R].0005.123/4
Inwestor	[DO UZUPEŁNIENIA: imię i nazwisko lub nazwa inwestora], [DO UZUPEŁNIENIA: adres inwestora]
Element projektu	Projekt techniczny (PT-1 AR)

Działając na podstawie art. 34 ust. 3d pkt 3 ustawy z dnia 7 lipca 1994 r. – Prawo budowlane (t.j. Dz.U. 2026 poz. 524 ze zm.), **oświadczam, że projekt techniczny w zakresie: architektura** dotyczący wyżej wymienionego zamierzenia budowlanego **został sporządzony zgodnie z obowiązującymi przepisami, zasadami wiedzy technicznej, projektem zagospodarowania działki lub terenu oraz projektem architektoniczno-budowlanym oraz rozstrzygnięciami dotyczącymi zamierzenia budowlanego** (brzmienie zgodne z art. 41 ust. 4a pkt 2 PB), w tym z decyzją o pozwoleniu na budowę [DO UZUPEŁNIENIA: nr i data decyzji o pozwoleniu na budowę, organ].

Przepisy techniczno-budowlane wydane na podstawie art. 7 ust. 2 pkt 1 PB — rozporządzenie Ministra Infrastruktury z dnia 12 kwietnia 2002 r. w sprawie warunków technicznych, jakim powinny odpowiadać budynki i ich usytuowanie (t.j. Dz.U. 2022 poz. 1225 ze zm.) — zastosowano w brzmieniu obowiązującym do dnia 19 września 2026 r., na podstawie art. 102a ust. 1 i 2 PB, w związku z oświadczeniem Inwestora z dnia [DO UZUPEŁNIENIA: data złożenia oświadczenia z art. 102a PB].

Osoby biorące udział w opracowaniu projektu (art. 34 ust. 3e pkt 1 PB)

Lp.	Imię i nazwisko	Specjalność uprawnień budowlanych	Nr uprawnień / decyzji	Zakres udziału	Data i podpis
1.	[DO UZUPEŁNIENIA: imię i nazwisko]	architektoniczna bez ograniczeń	[DO UZUPEŁNIENIA: nr uprawnień budowlanych]	PZT i PAB — rozwiązania architektoniczne i zagospodarowanie działki; PT-1 AR; informacja BIOZ	

Projektanci sprawdzający (art. 34 ust. 3e pkt 2 PB): nie dotyczy — projekt budynku mieszkalnego jednorodzinnego nie podlega sprawdzeniu (art. 20 ust. 3 pkt 2 PB).

Kopii decyzji o nadaniu uprawnień budowlanych i zaświadczeń o przynależności do izby samorządu zawodowego (art. 34 ust. 3d pkt 1–2 PB) nie dołącza się dla uprawnień i osób wpisanych do centralnego rejestru osób posiadających uprawnienia budowlane (art. 34 ust. 3da PB) — [DO UZUPEŁNIENIA: potwierdzenie wpisu w e-CRUB albo dołączenie kopii].

Podpisy: postać elektroniczna — podpis kwalifikowany, osobisty albo zaufany pliku (§ 7 ust. 4a RPB), kolumna „Data i podpis” pozostaje pusta; postać papierowa — podpis własnoręczny każdego z projektantów.

OPIS TECHNICZNY — ARCHITEKTURA

§ 23 RPB

1. Rozwiązania konstrukcyjno-materiałowe przegród

§ 23 pkt 4 RPB

Przegrody zewnętrzne zaprojektowano z ciągłą warstwą izolacji cieplnej i szczelności powietrznej; łączniki termoizolacyjne wsporników i płyt wysuniętych wg PT-2 BO. Warstwy i obliczenie U — tabele poniżej [ZaŁ].

Tabela 1. SZ1 — Ściana zewnętrzna nośna, silikat 18 + ETICS EPS 20

Warstwa (od wewnątrz)	d [m]	λ [W/(m·K)]	R [m²·K/W]
opór przejmowania od wewnątrz R _{si} (poziomy strumień ciepła)	—	—	0,130
Tynk gipsowy maszynowy	0,015	0,400	0,037
Błoczek wapienno-piaskowy 18 cm, kl. 20	0,180	0,770	0,234
Styropian grafitowy EPS 031	0,200	0,031	6,452
Tynk silikonowy cienkowarstwowy, biały	0,007	0,700	0,010
opór przejmowania na zewnątrz R _{se}	—	—	0,040
Całkowity opór cieplny R _T / grubość przegrody	0,402	—	6,903

Współczynnik przenikania ciepła: $U = 0,145 \text{ W/(m}^2\cdot\text{K)} \leq U_{\text{max}} = 0,20 \text{ W/(m}^2\cdot\text{K)}$ — spełnia (WT zał. 2 pkt 1.1 lp. 1 (t_i ≥ 16 °C); W-243).

Obliczenie wg PN-EN ISO 6946:2017-10, bez poprawek ΔU na łączniki mechaniczne i nieszczelności — [ZaŁ]; λ — wartości obliczeniowe z modelu materiałów.

Źródło danych: model/test/dom_testowy.yaml — sekcje materiały, przegrody

Tabela 2. POD-0 — Podłoga na gruncie

Warstwa (od wewnątrz)	d [m]	λ [W/(m·K)]	R [m²·K/W]
opór przejmowania od wewnątrz R _{si} (w dół strumień ciepła)	—	—	0,170
Płytki gresowe 60x120	0,010	1,300	0,008
Jastrych cementowy	0,065	1,000	0,065
Polistyren ekstrudowany XPS 300	0,150	0,035	4,286
Beton C25/30 (płyta podkładowa)	0,120	2,000	0,060
Podsypka piaskowa zagęszczona	0,150	2,000	0,075
opór przejmowania na zewnątrz R _{se}	—	—	0,040
Całkowity opór cieplny R _T / grubość przegrody	0,495	—	4,703

Współczynnik przenikania ciepła: $U = 0,213 \text{ W/(m}^2\cdot\text{K)} \leq U_{\text{max}} = 0,30 \text{ W/(m}^2\cdot\text{K)}$ — spełnia (WT zał. 2 pkt 1.1 lp. 6; W-243).

Obliczenie wg PN-EN ISO 6946:2017-10, bez poprawek ΔU na łączniki mechaniczne i nieszczelności — [ZaŁ]; λ — wartości obliczeniowe z modelu materiałów.

Źródło danych: model/test/dom_testowy.yaml — sekcje materiały, przegrody

Tabela 3. SD-D1 — Stropodach pełny, odwrócony spadek PIR

Warstwa (od wewnątrz)	d [m]	λ [W/(m·K)]	R [m²·K/W]
opór przejmowania od wewnątrz R _{si} (w górę strumień ciepła)	—	—	0,100
Membrana EPDM 1,5 mm	0,002	0,250	0,006
Płyty PIR (izolacja spadkowa)	0,220	0,022	10,000
Paroizolacja bitumiczna	0,002	0,230	0,009
Żelbet C30/37	0,200	2,300	0,087

Warstwa (od wewnątrz)	d [m]	λ [W/(m·K)]	R [m²·K/W]
Tynk gipsowy maszynowy	0,010	0,400	0,025
opór przejmowania na zewnątrz R _{se}	—	—	0,040
Całkowity opór cieplny R _T / grubość przegrody	0,433	—	10,267

Współczynnik przenikania ciepła: $U = 0,097 \text{ W/(m}^2\cdot\text{K)} \leq U_{\text{max}} = 0,15 \text{ W/(m}^2\cdot\text{K)}$ — spełnia (WT zał. 2 pkt 1.1 lp. 5; W-243).
Obliczenie wg PN-EN ISO 6946:2017-10, bez poprawek ΔU na łączniki mechaniczne i szczelności — [ZAL]; λ — wartości obliczeniowe z modelu materiałów.
Źródło danych: model/test/dom_testowy.yaml — sekcje materiały, przegrody

Tabela 4. Zestawienie stolarki (generowane z modelu)

Symbol	Rodzaj	Wymiary w świetle muru [cm]	Parapet [cm]	Otwieranie	Oslona	Liczba [szt.]	U _{max} [W/(m²·K)]
HS1	drzwi przesuwne HS	400 × 260	—	HS, prawa	screen ZIP	1	0,9
OP1	okno	180 × 150	90	RU, lewa	żaluzja zewn.	2	0,9
DZ1	drzwi zewnętrzne	110 × 230	—	R, lewa	—	1	1,3
OP2	okno	160 × 120	100	RU, prawa	roleta zewn.	1	0,9
DW1	drzwi wewnętrzne	90 × 210	—	R, prawa	—	4	—
FX1	przeszklenie stałe	200 × 100	110	stałe	—	1	0,9
OP3	okno	150 × 150	90	RU, lewa	żaluzja zewn.	2	0,9
OP4	okno	240 × 160	80	RU, lewa	—	1	0,9
OP5	okno	360 × 240	0	RU, lewa	—	1	0,9
HS2	drzwi przesuwne HS	240 × 230	—	HS, prawa	screen ZIP	1	0,9
OP6	okno	100 × 100	130	U, lewa	roleta zewn.	1	0,9
OP7	okno	180 × 150	90	RU, lewa	roleta zewn.	1	0,9
OP8	okno	140 × 150	90	RU, lewa	żaluzja zewn.	1	0,9
DW2	drzwi wewnętrzne	80 × 210	—	R, lewa	—	1	—

U_{max}: okna i przeszklenia 0,9 — WT zał. 2 pkt 1.2 (okna, drzwi balkonowe, przeszklenia stałe); drzwi zewnętrzne 1,3 — WT zał. 2 pkt 1.2 (także drzwi garaż–dom). Szczelność okien klasa ≥ 3 (WT zał. 2 pkt 2.3.2). Wartości U_w i g wybranych wyrobów [DO UZUPEŁNIENIA: deklaracje producenta, E-13].
Źródło danych: model/test/dom_testowy.yaml — otwory (grupowanie po symbolu)

2. Dane dotyczące warunków ochrony przeciwpożarowej

§ 23 pkt 10 RPB

Klasy reakcji na ogień wyrobów elewacyjnych: ETICS — NRO jako system (WT § 216 w zw. z § 213); przejścia instalacyjne przez strop garażu — uszczelnienia wg PT-3 IS [NZW].


CZĘŚĆ RYSUNKOWA

§ 7 ust. 1 pkt 4, § 10 RPB

OBIEKT	Budynek mieszkalny jednorodzinny wolnostojący „Dom LAMELA”
ELEMENT PROJEKTU	PT-1 AR — Projekt techniczny
BRANŻA	architektura
AUTORZY RYSUNKÓW	[DO UZUPEŁNIENIA: imię i nazwisko] — architektoniczna bez ograniczeń, nr upr. [DO UZUPEŁNIENIA: nr uprawnień budowlanych]
SPRAWDZAJĄCY	nie dotyczy (art. 20 ust. 3 pkt 2 PB)
DATA	25 września 2026 r.
LICZBA RYSUNKÓW	9 rysunków
POSTAĆ	PDF wektorowy (RPB § 2b ust. 2); arkusze w formatach oryginalnych wg PN-EN ISO 5457. W postaci papierowej arkusze składa się do formatu A4 „do wpięcia” (RPB § 2a) — tabliczka na wierzchu.
NUMERACJA	rysunki identyfikuje numer rysunku w metryce (RPB § 6 ust. 3, § 10 ust. 1)

Tabela 5. Wykaz rysunków

Lp.	Nr rysunku	Tytuł rysunku	Skala	Format	Wymiary [mm]	Uwagi
1.	T-AR-01	RZUT PARTERU	1:50	A3×3	891×420	
2.	T-AR-02	RZUT PIĘTRA	1:50	A3×3	891×420	
3.	T-AR-03	RZUT DACHU	1:50	A3×3	891×420	
4.	T-AR-04	PRZEKRÓJ A-A	1:50	A2	594×420	
5.	T-AR-05	PRZEKRÓJ B-B	1:50	A3×3	891×420	
6.	T-AR-06	ELEWACJA POŁUDNIOWA	1:50	A2	594×420	
7.	T-AR-07	ELEWACJA PÓŁNOCNA	1:50	A2	594×420	
8.	T-AR-08	ELEWACJA WSCHODNIA	1:50	A2	594×420	
9.	T-AR-09	ELEWACJA ZACHODNIA	1:50	A2	594×420	

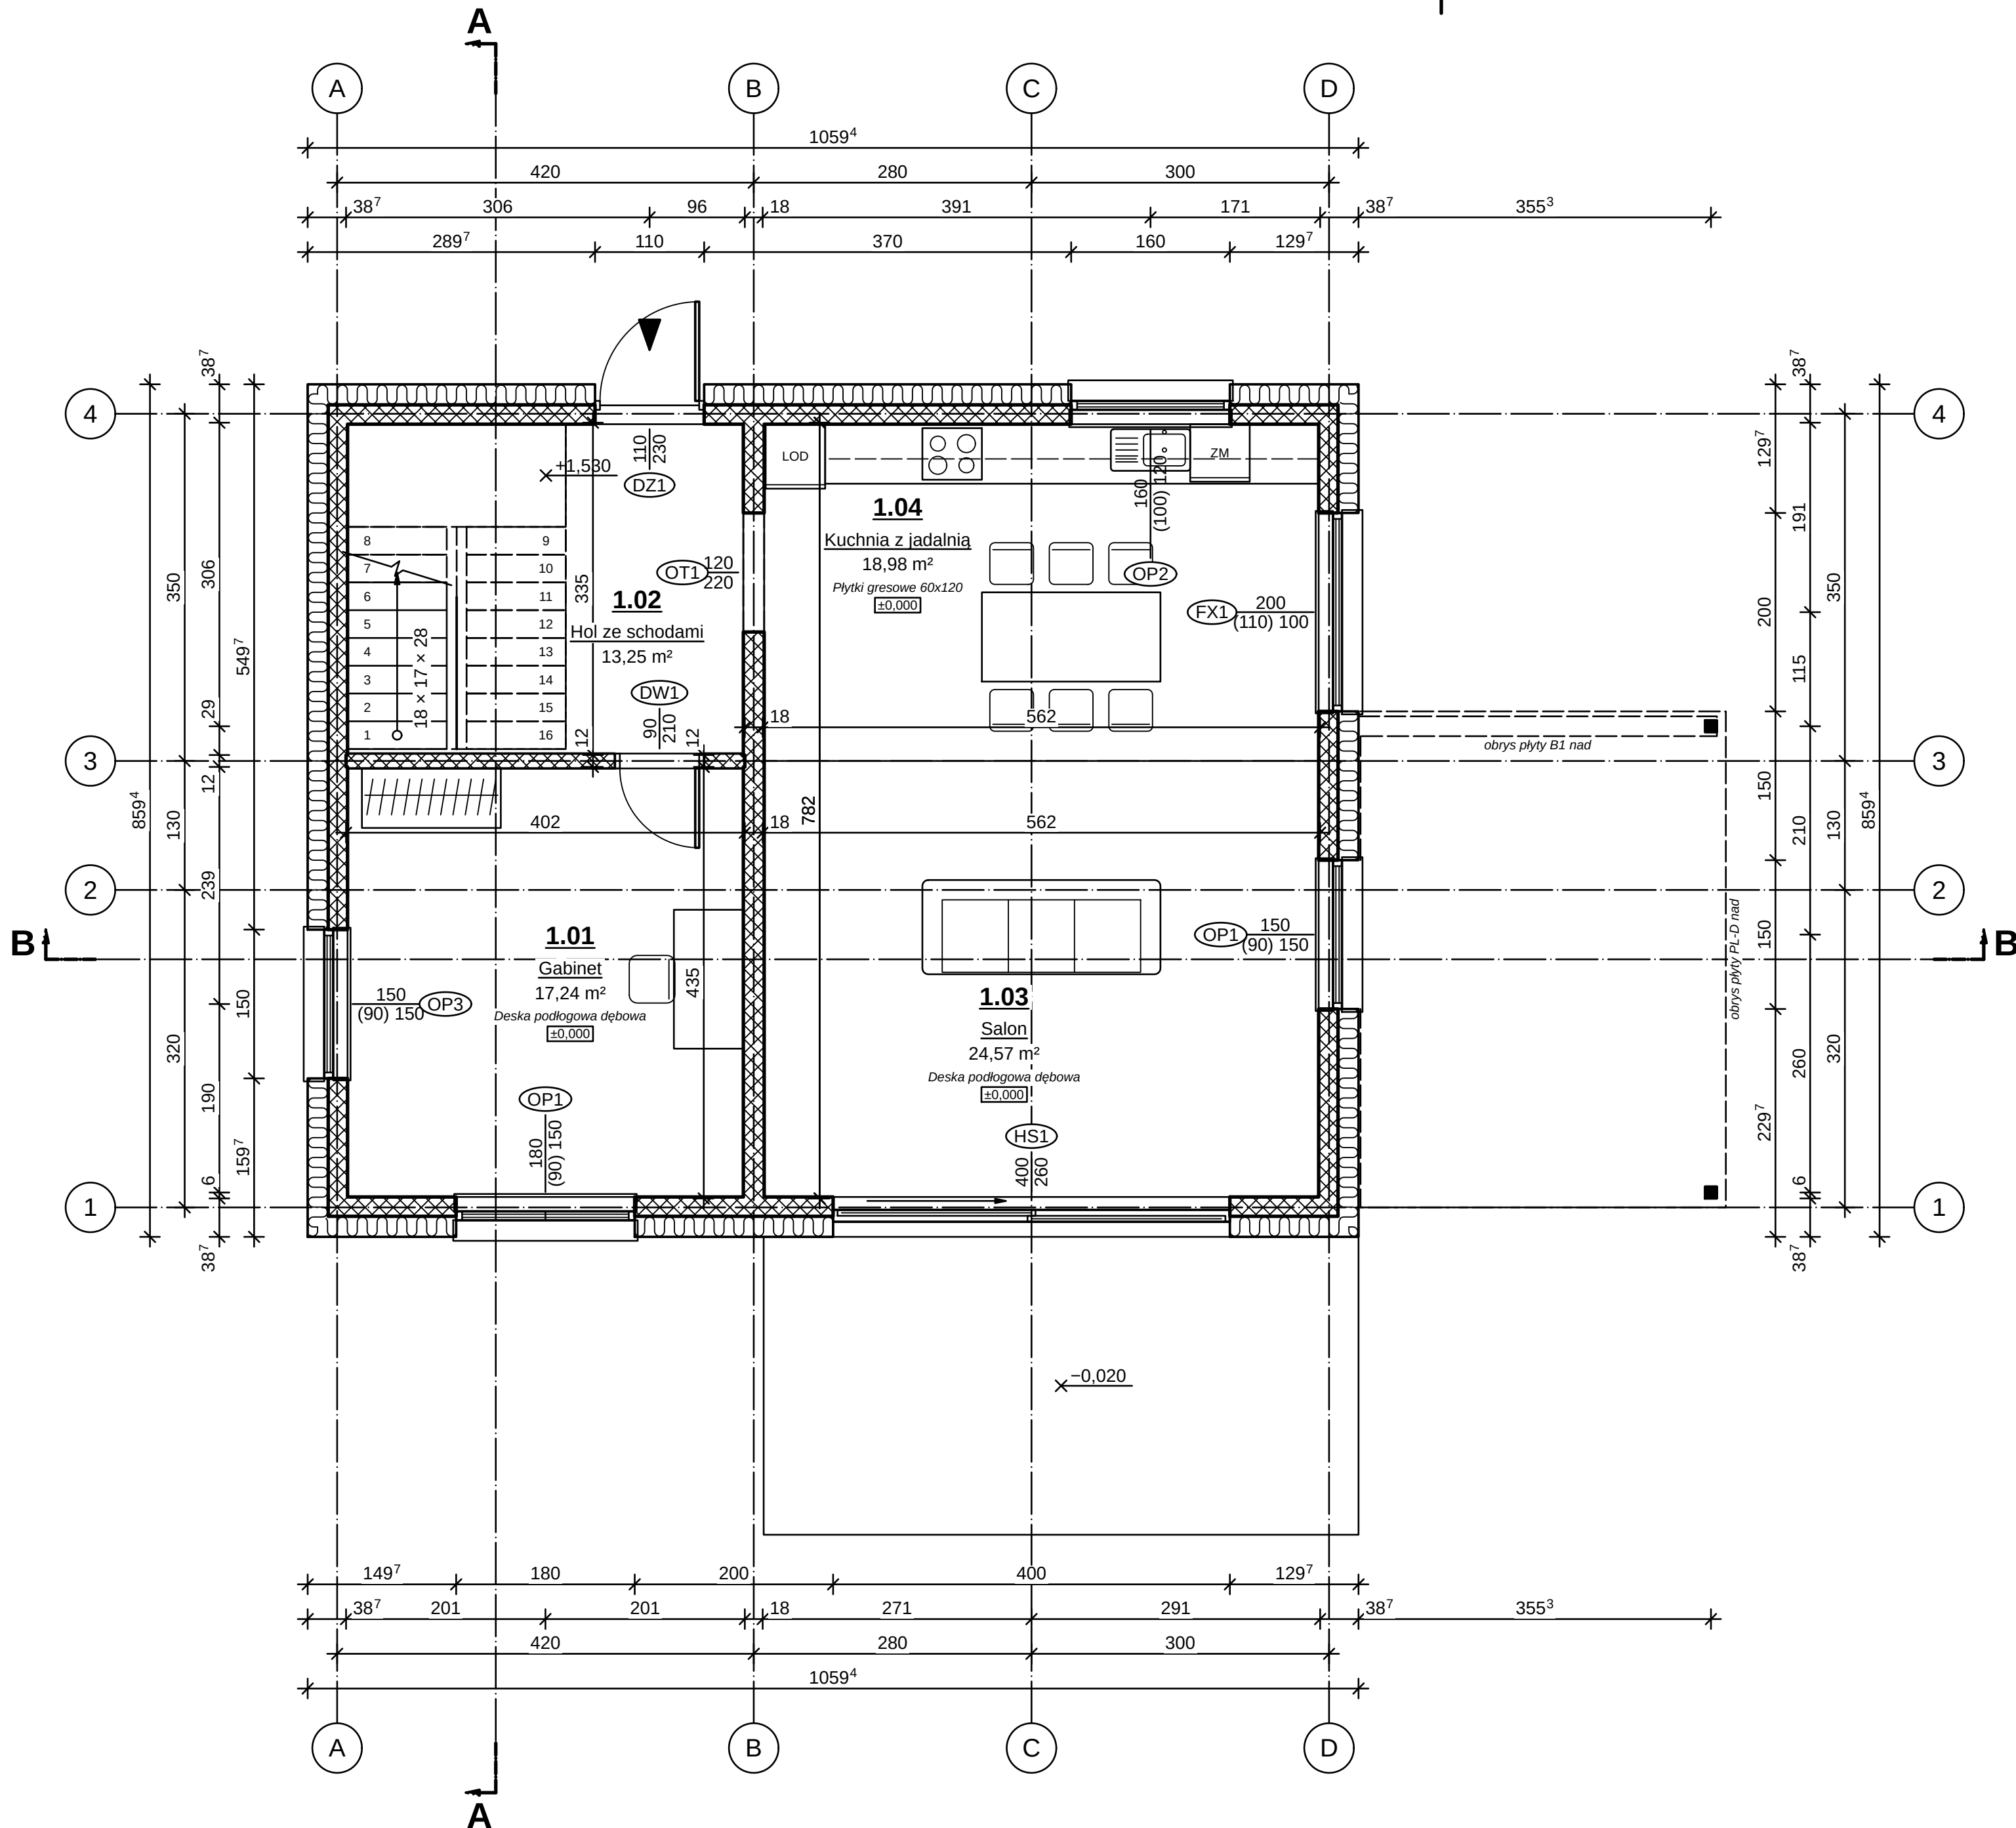

RZUT PARTERU 1:50

ZESTAWIENIE POMIESZCZEŃ

Nr	Nazwa pomieszczenia	Posadzka	Kat.	Wys. [m]	Pow. [m²]
1.03	Salon	Deska podłogowa dębowa	podst.	2,70	24,57
1.04	Kuchnia z jadalnią	Płytki gresowe 60x120	podst.	2,70	18,98
1.01	Gabinet	Deska podłogowa dębowa	podst.	2,70	17,24
1.02	Hol ze schodami	Płytki gresowe 60x120	ruchu	2,70	13,25
RAZEM powierzchnia netto					74,03
w tym użytkowa (podst. + pomoc.)					60,78

OZNACZENIA MATERIAŁÓW (PN-B-01030 + przyjęte)


	Styropian grafitowy EPS 031 — meander „UUU”		Stal konstrukcyjna S355, malowana proszkowo RAL 7016 — zaczemienie
	Bloczek wapienno-piaskowy 12 cm, kl. 15; Bloczek wapienno-piaskowy 18 cm, kl. 20 — kratka ukośna 45°/135°		

OZNACZENIA LINII


---	elementy nad płaszczyzną cięcia (obrysyt płyt, wsporników, brył wyższych kondygnacji)
---	elementy poniżej płaszczyzny cięcia (widok z góry)
---	osie konstrukcyjne; linia punktowa z pogrubionymi końcami — ślad przekroju

OBJAŚNIENIA I UWAGI

- Wymiary w cm (mm w indeksie górnym, np. 24^h = 24,5 cm), rzędne w m względem ±0,000 = 101,650 m n.p.m. (PL-EVRF2007-NH).
- Rzuty: płaszczyzna cięcia +1,10 m nad posadzką kondygnacji. Linia kreskową — elementy nad płaszczyzną cięcia (obrysyt płyt i wsporników, brył wyższych kondygnacji, otwory w stropie nad, belki); linią cieniłą — elementy poniżej (widok).
- Otwory: licznik — szerokość, mianownik — wysokość w świetle muru, w nawiasie wysokość parapetu; symbol stolarki wg zestawienia stolarki.
- Numeracja pomieszczeń wg PN-B-01025 / PN-EN ISO 4157-2: <nr> kondygnacji (partier = 1); <nr> <nr>, identyfikator w modelu: <kond> <nr> (partier = 0).
- Drzwi: strona otwierania (lewej/prawej) wg modelu — patrzeć od strony, w którą otwiera się skrzydło.
- MODEL TESTOWY — rysunek próbny generatorów widoków; dane nie stanowią projektu.
- Rysunek wygenerowany automatycznie z modelu model/test/dom_testowyyami (wersja 1.0, 2026-09-25) — generatory lamela.views.

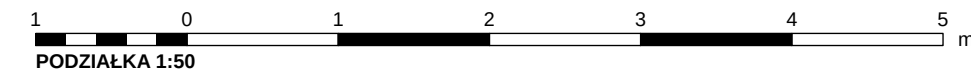

REW.	OPIS ZMIANY			DATA
0	Próba generatorów widoków z modelu testowego			2026-09-25
PRACOWNIA PROJEKTOWA PRACOWNIA PROJEKTOWA — nazwa do uzupełnienia adres pracowni do uzupełnienia			STADIUM PB	BRANŻA ARCHITEKTURA (AR)
INWESTOR (do uzupełnienia)				
OBIEKT / NAZWA ZAMIERZENIA BUDOWLANEGO				
Budynek testowy pipeline'u (model testowy) — NIE jest projektem Domu LAMELA				
ADRES / LOKALIZACJA (NR DZIAŁKI, OBRĘB, JEDN. EWIDENCYJNA) dz. nr ewid. T-1/1, obręb 0000 Testowo				KAT. OBIEKTU I
FUNKCJA	IMIĘ I NAZWISKO	SPECJALNOŚĆ, NR UPRAWNIENI	DATA	PODPIS
Projektant				
Projektant (wsp.)				
Sprawdzający				
Opracował				
TYTUŁ RYSUNKU				
RZUT PARTERU				
SKALA 1:50	FORMAT A3×3	DATA WYDANIA 2026-09-25	RODZAJ DOK. rzut	NR RYSUNKU T-AR-01
			ARKUSZ 1/9	REW. 0

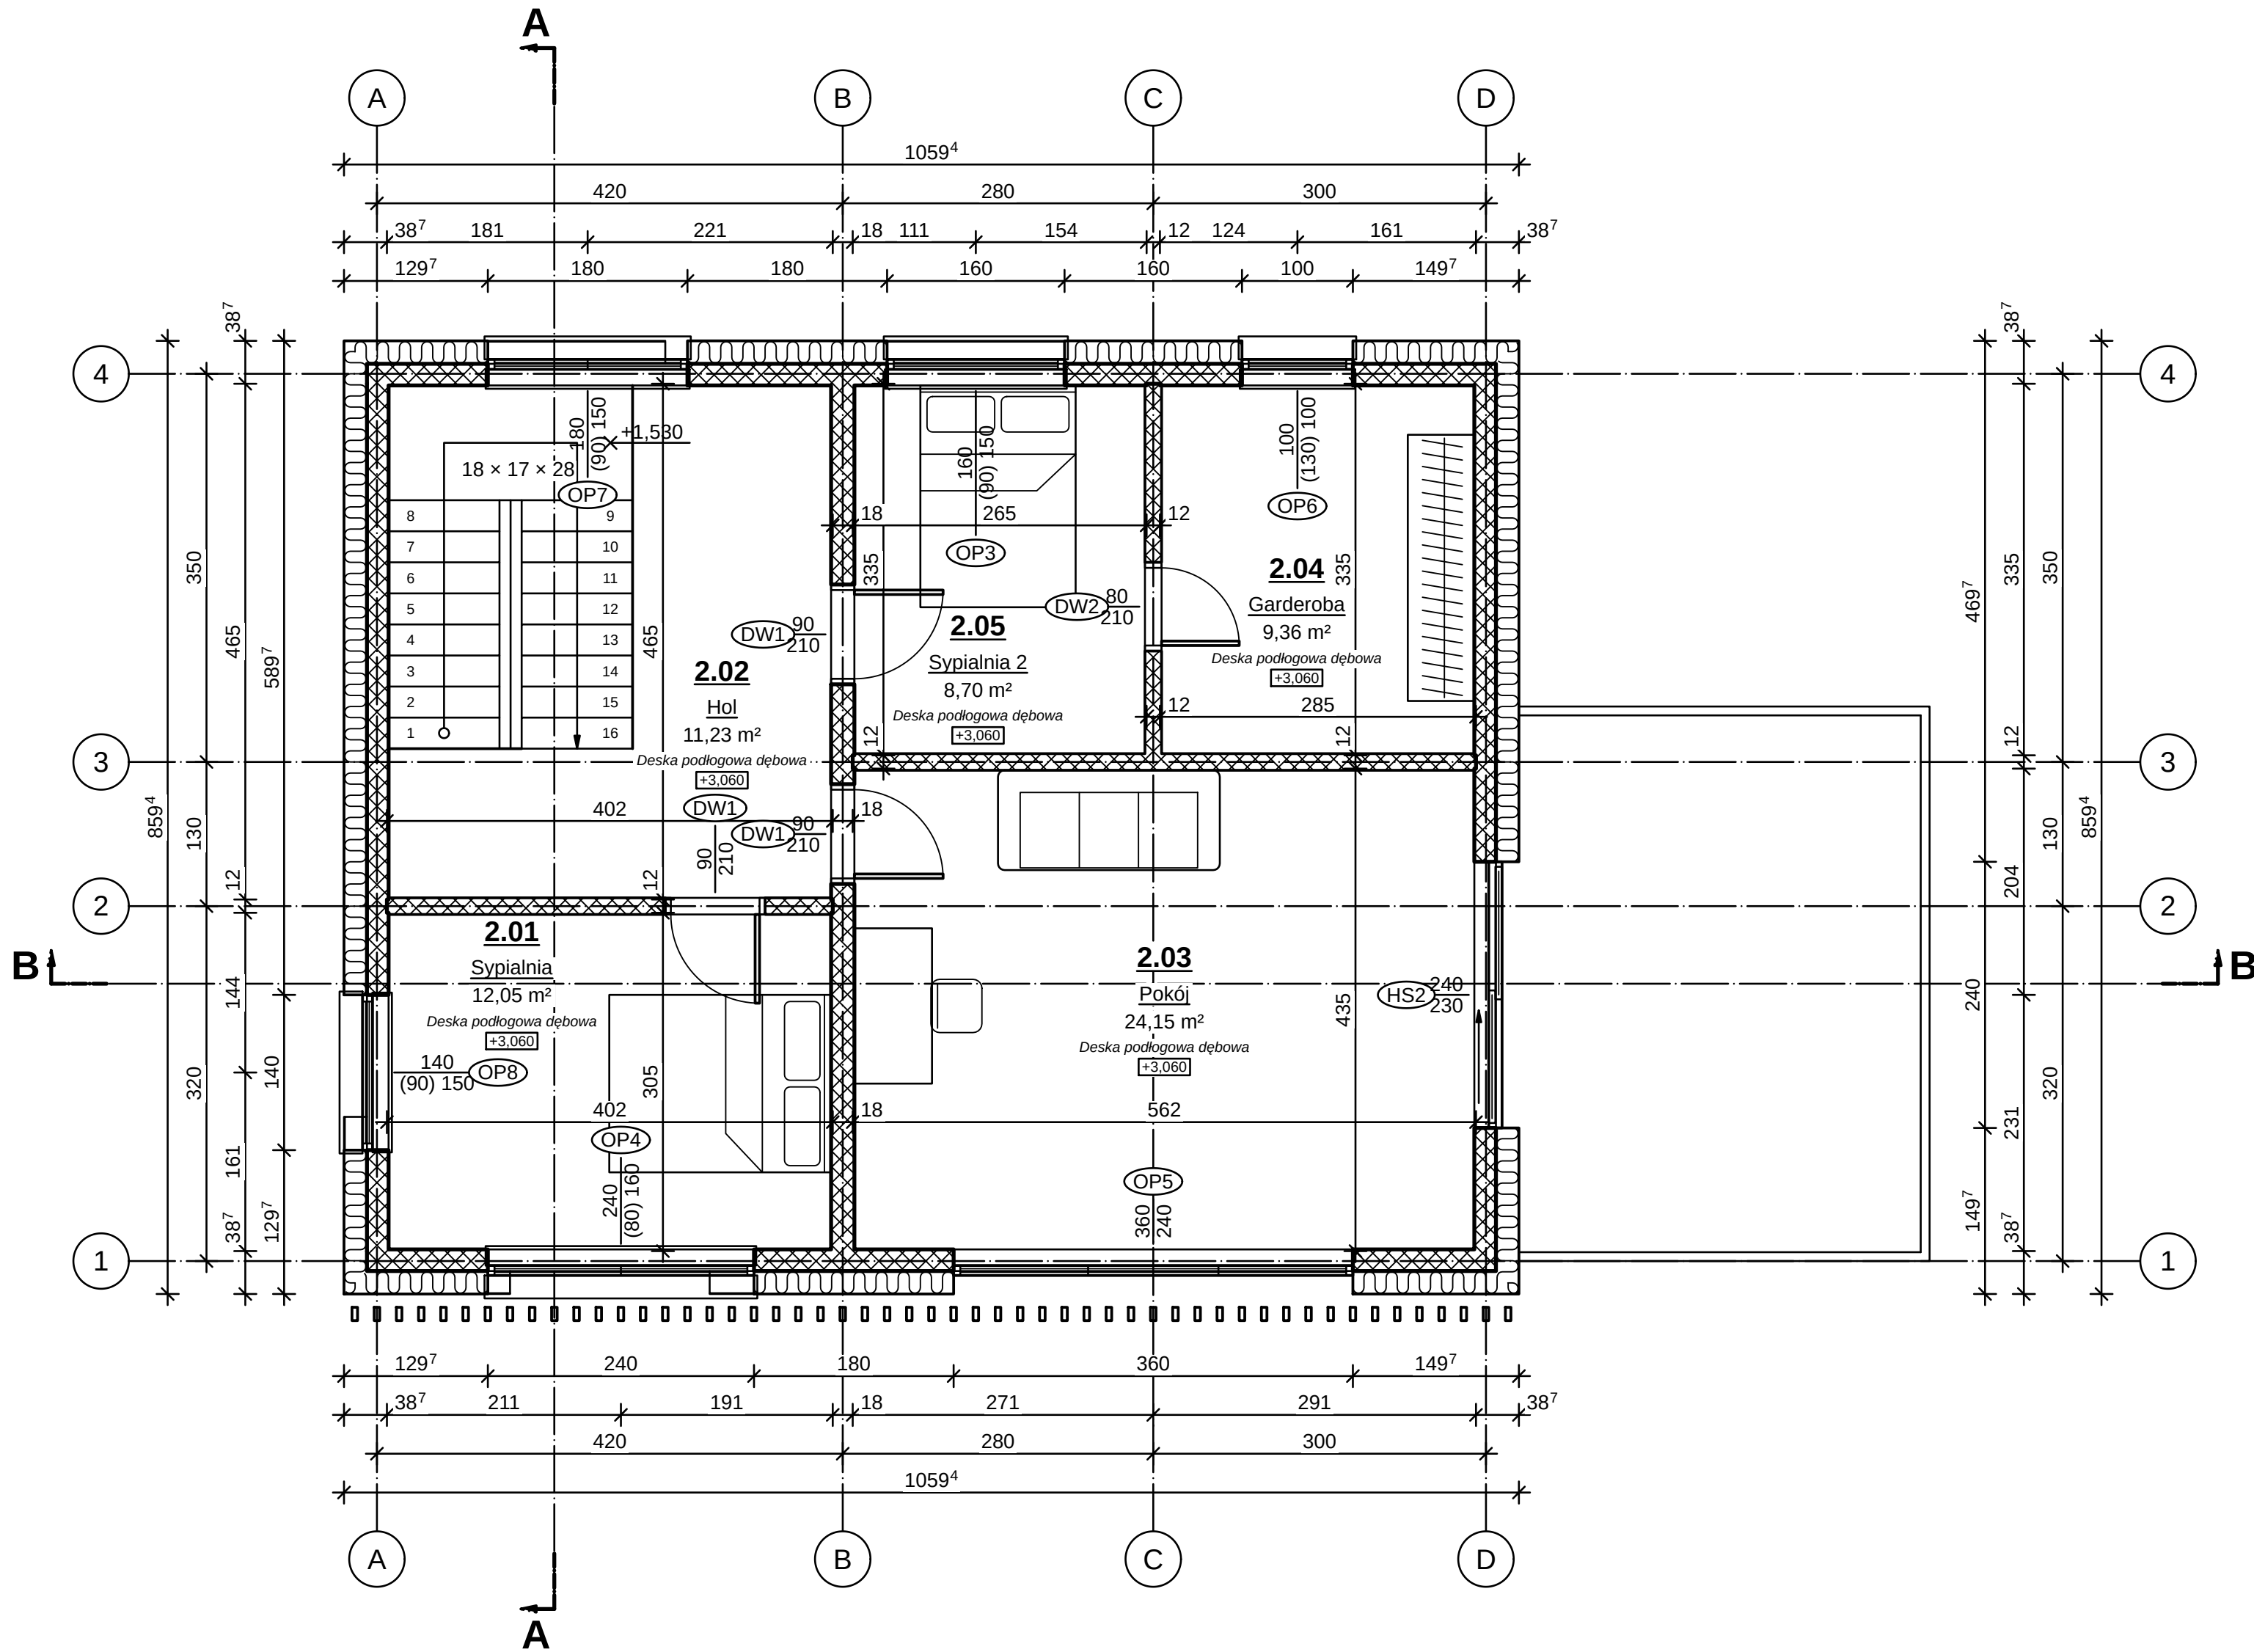

RZUT PIĘTRA 1:50

ZESTAWIENIE POMIESZCZEŃ

Nr	Nazwa pomieszczenia	Posadzka	Kat.	Wys. [m]	Pow. [m²]
2.03	Pokój	Deska podłogowa dębowa	podst.	2,70	24,15
2.01	Sypialnia	Deska podłogowa dębowa	podst.	2,70	12,05
2.02	Hol	Deska podłogowa dębowa	ruchu	2,70	11,23
2.04	Garderoba	Deska podłogowa dębowa	pomoc.	2,70	9,36
2.05	Sypialnia 2	Deska podłogowa dębowa	podst.	2,70	8,70
RAZEM powierzchnia netto					65,49
w tym użytkowa (podst. + pomoc.)					54,26

OZNACZENIA MATERIAŁÓW (PN-B-01030 + przyjęte)


Styropian grafitowy EPS 031 — meander „UUU” Błoczek wapienno-piaskowy 12 cm, kl. 15; Błoczek wapienno-piaskowy 18 cm, kl. 20 — kratka ukośna 45°/135°

OZNACZENIA LINII


— elementy nad płaszczyzną cięcia (obrysy płyt, wsporników, brył wyższych kondygnacji)
— elementy poniżej płaszczyzny cięcia (widok z góry)
- - - osie konstrukcyjne; linia punktowa z pogrubionymi końcami — ślad przekroju

OBJAŚNIENIA I UWAGI

- Wymiary w cm (mm w indeksie górnym, np. 24⁴ = 24,5 cm), rzędne w m względem ±0.000 = 101,650 m n.p.m. (PL-EVRF2007-NH).
- Rzuty: płaszczyzna cięcia +1.10 m nad posadzką kondygnacji. Linia kreskową — elementy nad płaszczyzną cięcia (obrysy płyt i wsporników, brył wyższych kondygnacji, otwory w stropie nad, belki); linia cieniłą — elementy poniżej (widok).
- Otwory: licznik — szerokość, mianownik — wysokość w świetle muru, w nawiasie wysokość parapetu; symbol stolarki wg zestawienia stolarki.
- Numeracja pomieszczeń wg PN-B-01025 / PN-EN ISO 4157-2: <nr kondygnacji (parter = 1)>. <nr>; identyfikator w modelu: <kond>. <nr> (parter = 0).
- Drzwi: strona otwierania (lewe/prawe) wg modelu — patrząc od strony, w którą otwiera się skrzydło.
- MODEL TESTOWY — rysunek próbny generatorów widoków; dane nie stanowią projektu.
- Rysunek wygenerowany automatycznie z modelu model/test/dom_testowy.yamli (wersja 1.0, 2026-09-25) — generatory lamela.views.

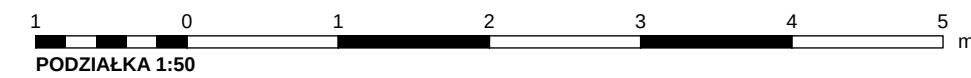


REW.	OPIS ZMIANY			DATA	
0	Próba generatorów widoków z modelu testowego			2026-09-25	
PRACOWNIA PROJEKTOWA PRACOWNIA PROJEKTOWA — nazwa do uzupełnienia adres pracowni do uzupełnienia				STADIUM PB	BRANŻA ARCHITEKTURA (AR)
INWESTOR (do uzupełnienia)					
OBIEKT / NAZWA ZAMIERZENIA BUDOWLANEGO					
Budynek testowy pipeline'u (model testowy) — NIE jest projektem Domu LAMELA					
ADRES / LOKALIZACJA (NR DZIAŁKI, OBRĘB, JEDN. EWIDENCYJNA) dz. nr ewid. T-1/1, obręb 0000 Testowo					KAT. OBIEKTU I
FUNKCJA	IMIĘ I NAZWISKO		SPECJALNOŚĆ, NR UPRAWNIEŃ	DATA	PODPIS
Projektant					
Projektant (wsp.)					
Sprawdzający					
Opracował					
TYTUŁ RYSUNKU					
RZUT PIĘTRA					
SKALA 1:50	FORMAT A3×3	DATA WYDANIA 2026-09-25	RODZAJ DOK. rzut	NR RYSUNKU T-AR-02	ARKUSZ 2/9
					REW. 0

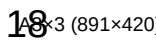

1 0 1 2 3 4 5 m
 PODZIAŁKA 1:50

REW.	OPIS ZMIANY	DATA				
0	Próba generatorów widoków z modelu testowego	2026-09-25				
PRACOWNIA PROJEKTOWA PRACOWNIA PROJEKTOWA — nazwa do uzupełnienia adres pracowni do uzupełnienia		STADIUM PB	BRANŻA ARCHITEKTURA (AR)			
INWESTOR (do uzupełnienia)						
OBJEKT / NAZWA ZAMIERZENIA BUDOWLANEGO						
Budynek testowy pipeline'u (model testowy) — NIE jest projektem Domu LAMELA						
ADRES / LOKALIZACJA (NR DZIAŁKI, OBRĘB, JEDN. EWIDENCYJNA) dz. nr ewid. T-1/1, obręb 0000 Testowo			KAT. OBJEKTU I			
FUNKCJA	IMIĘ I NAZWISKO	SPECJAŁNOŚĆ, NR UPRAWNIENI	DATA	PODPIS		
Projektant						
Projektant (wsp.)						
Sprawdzający						
Opracował						
TYTUŁ RYSUNKU						
RZUT DACHU						
SKALA 1:50	FORMAT A3×3	DATA WYDANIA 2026-09-25	RODZAJ DOK. rzut	NR RYSUNKU T-AR-03	ARKUSZ 3/9	REW. 0

PRZEKRÓJ A-A 1:50

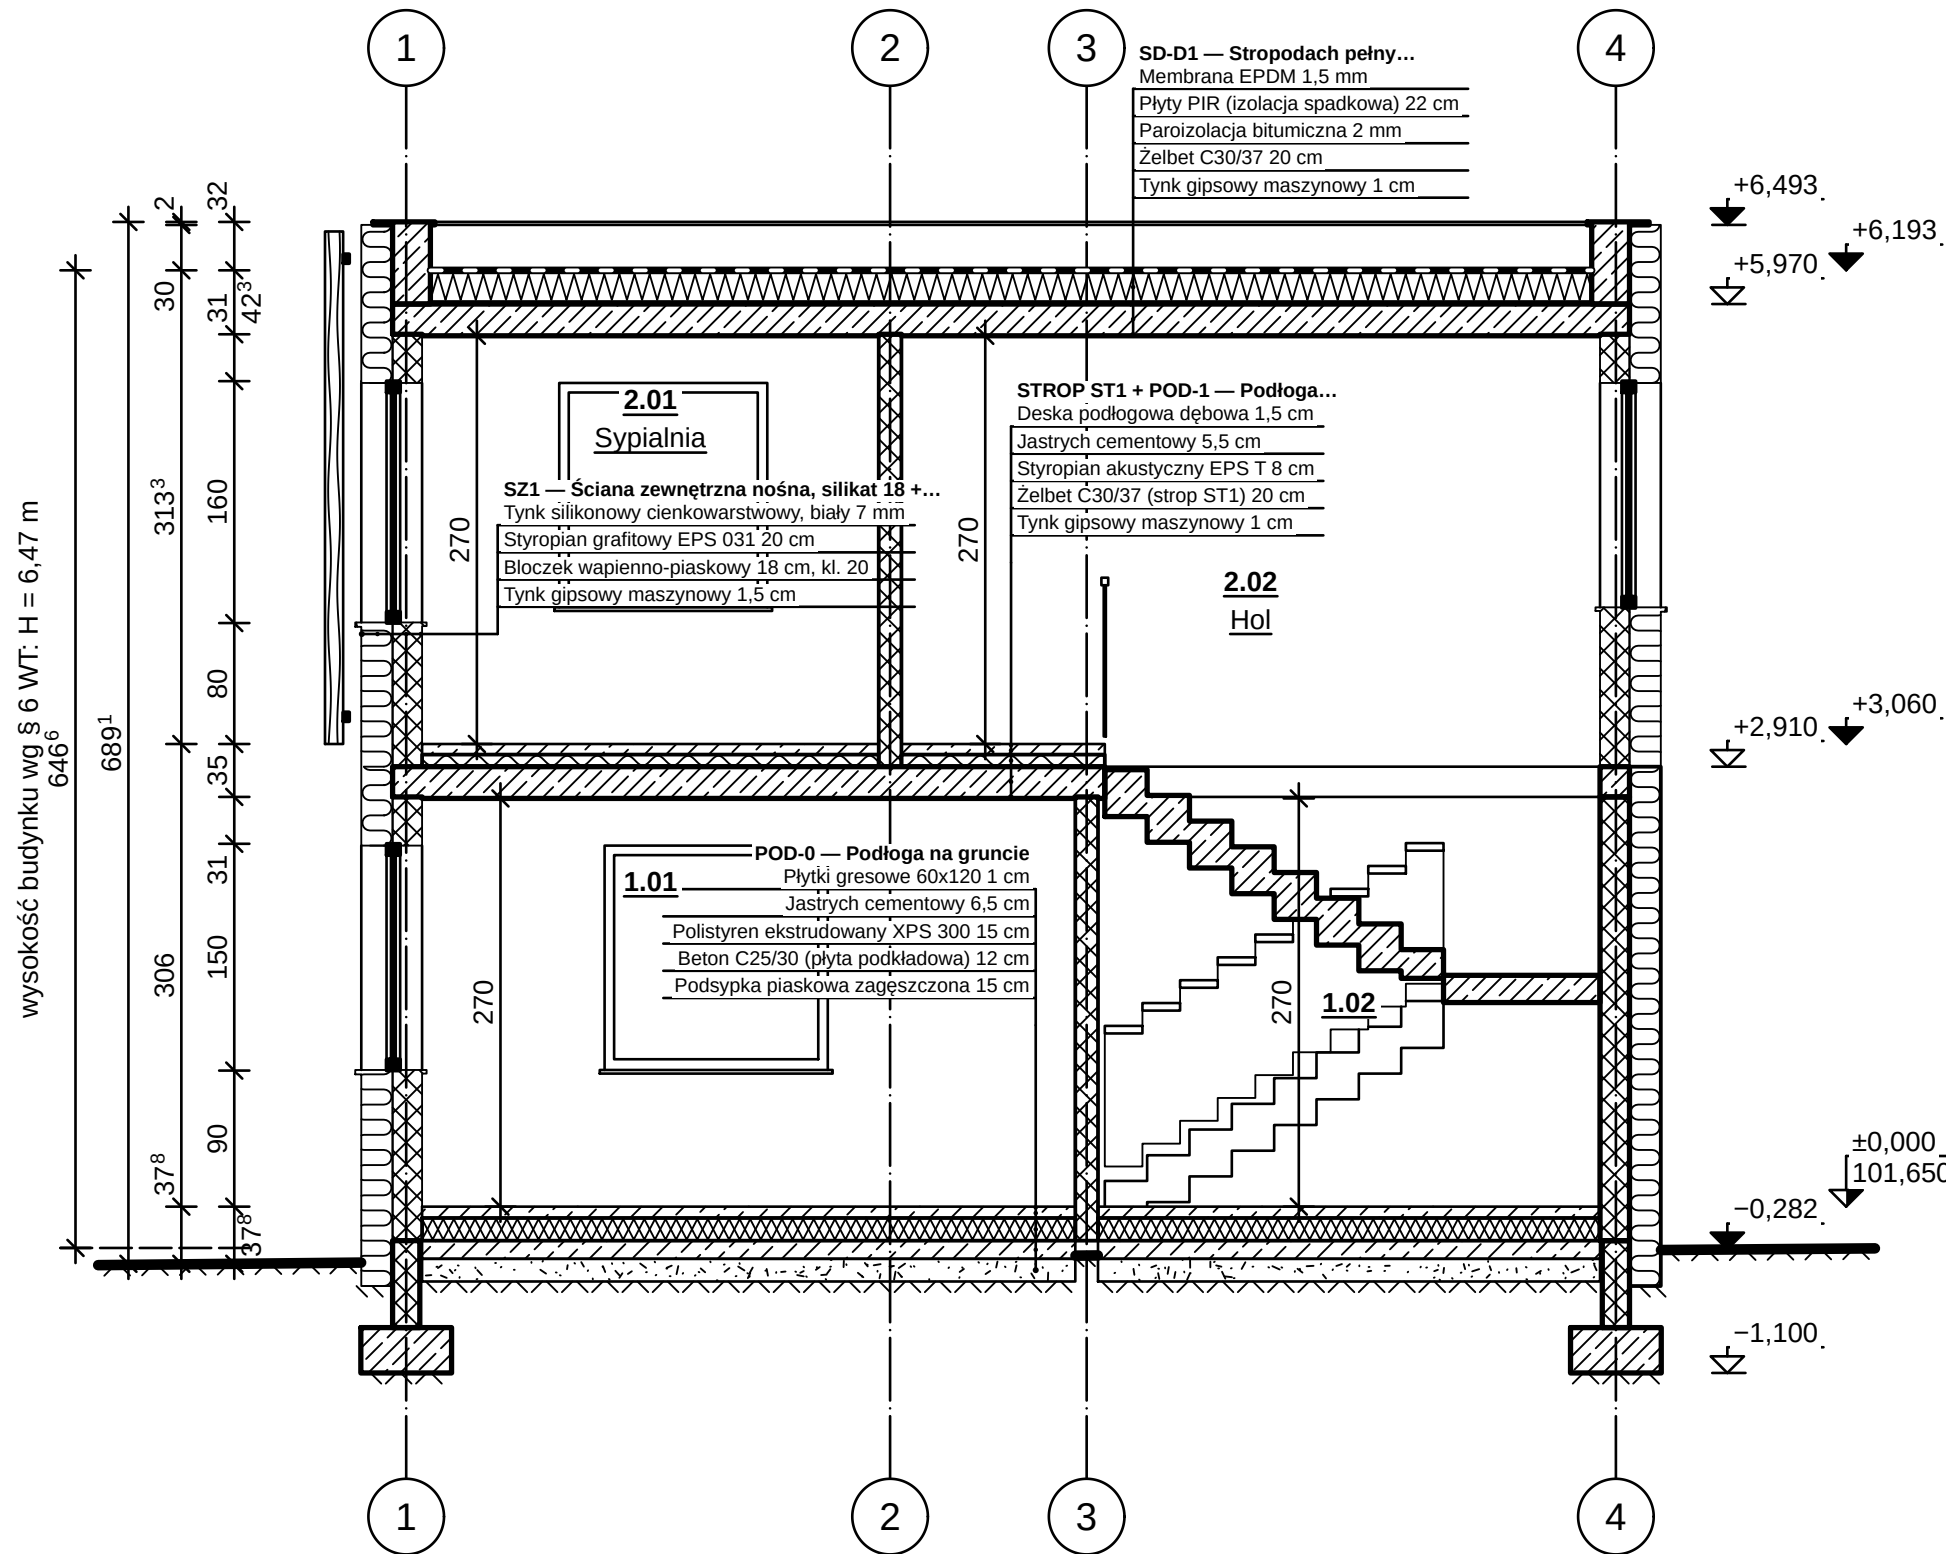


OZNACZENIA MATERIAŁÓW (PN-B-01030 + przyjęte)

	Jastrych cementowy, Beton C25/30 (płyta podkładowa) — 45° przerywane		Polistyren ekstrudowany XPS 300 — zygzak podwójny
	Drewno termojesion (lamelle elewacyjne) — przekrój wzdłuż włókien		Błoczek wapienno-piaskowy 12 cm, kl. 15; Błoczek wapienno-piaskowy 18 cm, kl. 20 — kratka ukośna 45°/135°
	grunt rodzimy		Podsypka piaskowa zagęszczona
	Styropian grafitowy EPS 031; Styropian akustyczny EPS T — meander „UUU”		Paroizolacja bitumiczna — linia kreskowa cienka 3/1 po ciepłej stronie
	Płyty PIR (izolacja spadkowa) — zygzak z okładzinami		Obróbki blacharskie (blacha powlekana); Stolarka — profile aluminiowe, antracyt; Stal malowana proszkowo (balustrady, rygle) — zaczerpienie
	Membrana EPDM 1,5 mm — pas czarno-biały		Schody — płyta żelbetowa z okładziną; Żelbet C30/37 — 45° na przemian ciągle i przerywane


OBJAŚNIENIA I UWAGI

- Wymiary w cm (mm w indeksie górnym, np. 24⁵ = 24,5 cm), rzędne w m względem ±0,000 = 101,650 m n.p.m. (PL-EVRF2007-NH).
- Rzędne: trójkąt zaczerpiony — poziom wykończenia, niezaczerpiony — konstrukcji, w połowie zaczerpiony — poziom ±0,000 z rzędną bezwzględną (PN-B-01025).
- Wysokość budynku wg § 6 WT: od terenu przy najniższej położonym wejściu (−0,273) do wierzchu stropodachu D1 (+6,193) — H = 6,47 m (bez attyk).
- Opisy warstw: kod i nazwa przegrody z modelu, materiały i grubości wg modelu (od góry / od lewej).
- MODEL TESTOWY — rysunek próbny generatorów widoków; dane nie stanowią projektu.
- Rysunek wygenerowany automatycznie z modelu model/test/dom_testowy.yaml (wersja 1.0, 2026-09-25) — generatory lamela.views.

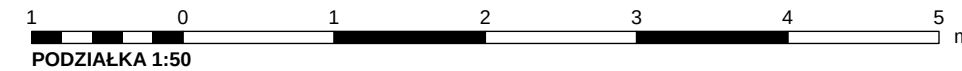

REW.	OPIS ZMIANY			DATA		
0	Próba generatorów widoków z modelu testowego			2026-09-25		
PRACOWNIA PROJEKTOWA PRACOWNIA PROJEKTOWA — nazwa do uzupełnienia adres pracowni do uzupełnienia			STADIUM PB	BRANŻA ARCHITEKTURA (AR)		
INWESTOR (do uzupełnienia)						
OBIEKT / NAZWA ZAMIERZENIA BUDOWLANEGO Budynek testowy pipeline'u (model testowy) — NIE jest projektem Domu LAMELA						
ADRES / LOKALIZACJA (NR DZIAŁKI, OBRĘB, JEDN. EWIDENCYJNA) dz. nr ewid. T-1/1, obręb 0000 Testowo				KAT. OBIEKTU I		
FUNKCJA	IMIĘ I NAZWISKO		SPECJALNOŚĆ, NR UPRAWNIEŃ		DATA	PODPIS
Projektant						
Projektant (wsp.)						
Sprawdzający						
Opracował						
TYTUŁ RYSUNKU PRZEKRÓJ A-A						
SKALA 1:50	FORMAT A2	DATA WYDANIA 2026-09-25	RODZAJ DOK. przekrój	NR RYSUNKU T-AR-04		ARKUSZ 4/9
						REW. 0

PRZEKRÓJ B-B 1:50

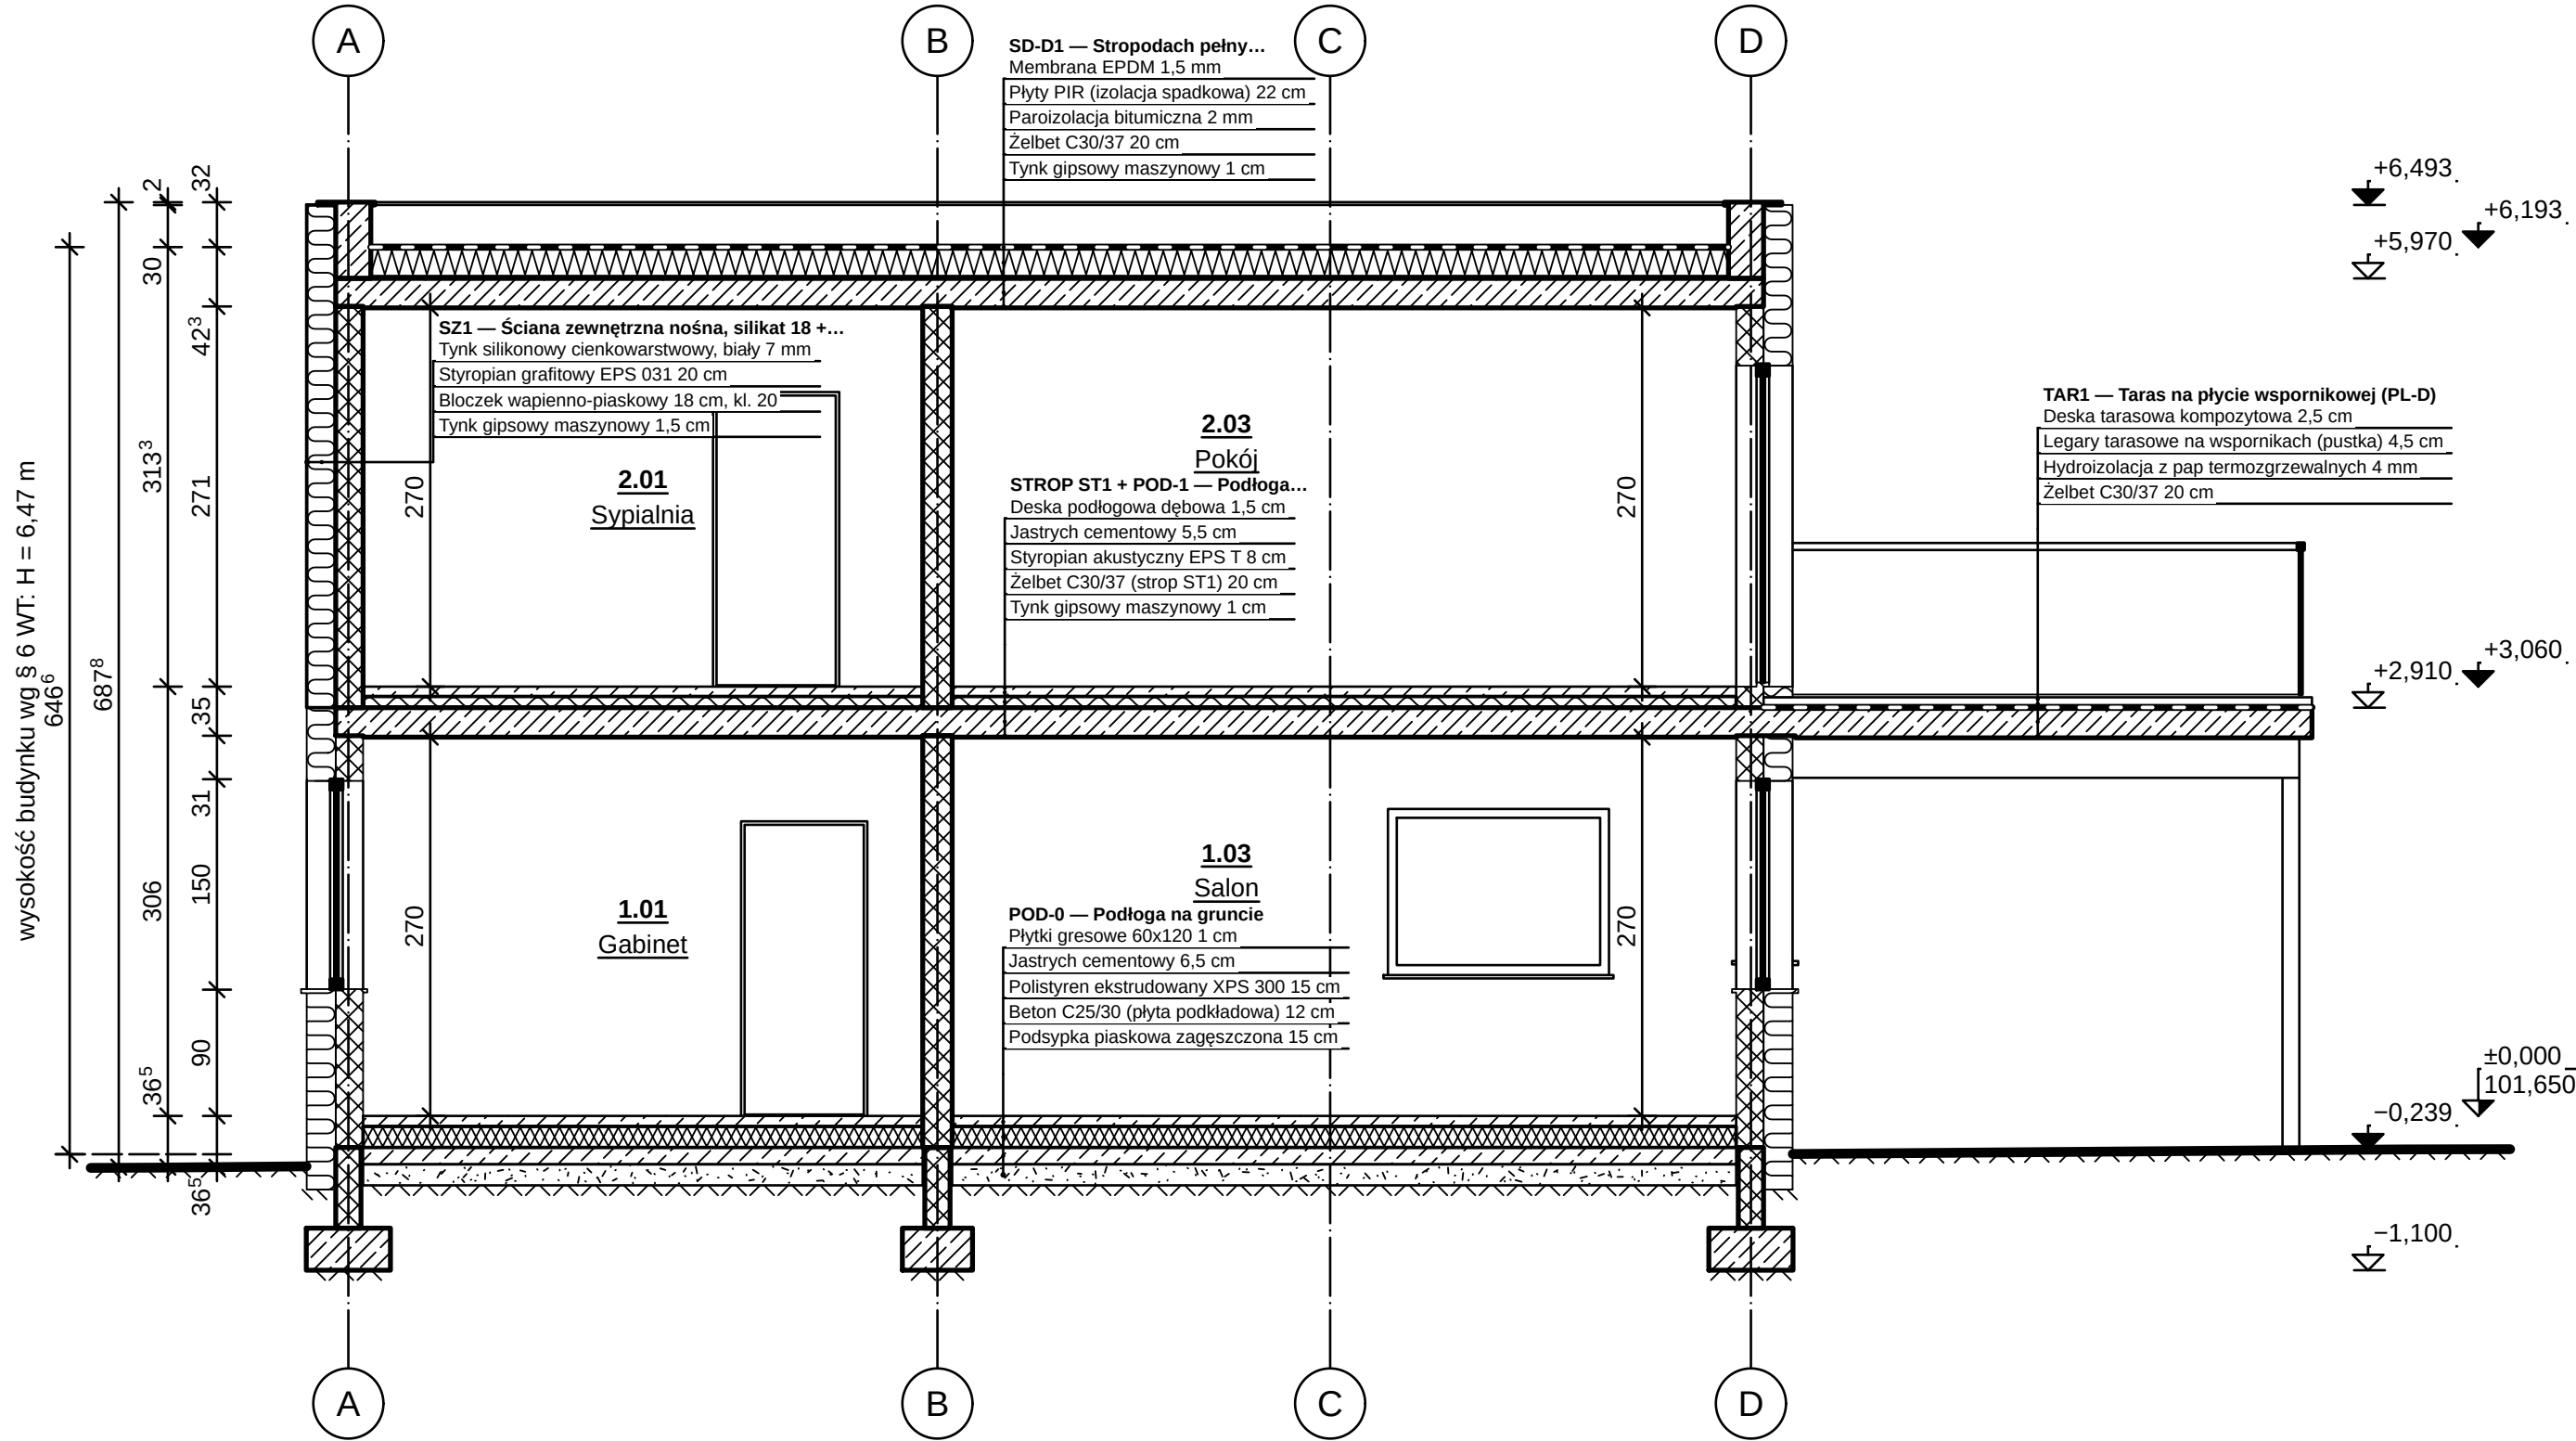

OZNACZENIA MATERIAŁÓW (PN-B-01030 + przyjęte)


	Jastyrych cementowy; Beton C25/30 (płyta podkładowa) — 45°		Błoczek wapienno-piaskowy 18 cm, kl. 20 — kratka ukośna 45°/135°
	grunt rodzimy		Podsypka piaskowa zagęszczona
	Styropian grafitowy EPS 031; Styropian akustyczny EPS T — meander „UUU”		Paroizolacja bitumiczna — linia kreskowa cienka 3/1 po ciepłej stronie
	Płyty PIR (izolacja spadkowa) — zygzak z okładzinami		Obróbki blacharskie (blacha powlekana); Stalarka — profile aluminiowe, antracyt; Stal nierdzewna (pochwyty) — zaczerpnięcie
	Membrana EPDM 1,5 mm; Hydroizolacja z pap termozgrzewalnych — pas czarno-biały		Żelbet C30/37 — 45° na przemiał ciągły i przerywane
	Polistyren ekstrudowany XPS 300 — zygzak podwójny		

OBJAŚNIENIA I UWAGI

- Wymiary w cm (mm w indeksie górnym, np. 24° = 24,5 cm), rzędne w m względem ±0,000 = 101,650 m n.p.m. (PL-EVRF2007-NH).
- Rzędne: trójkąt zaczerpnięty — poziom wykończenia, niezaczerpnięty — konstrukcji, w połowie zaczerpnięty — poziom ±0,000 z rzędną bezwzględną (PN-B-01025).
- Wysokość budynku wg § 6 WT: od terenu przy najniższym położonym wejściu (−0,273) do wierzchu stropodachu D1 (+6,193) — H = 6,47 m (bez attyk).
- Opisy warstw: kod i nazwa przegrody z modelu, materiały i grubości wg modelu (od góry / od lewej).
- MODEL TESTOWY — rysunek próbny generatorów widoków, dane nie stanowią projektu.
- Rysunek wygenerowany automatycznie z modelu model/test/odom_testowy.yam (wersja 1.0, 2026-09-25) — generatory lamela.views.



REW.	OPIS ZMIANY	DATA
0	Próba generatorów widoków z modelu testowego	2026-09-25
PRACOWNIA PROJEKTOWA	PRACOWNIA PROJEKTOWA — nazwa do uzupełnienia	STADIUM PB
adres pracowni do uzupełnienia	BRANZA ARCHITEKTURA (AR)	
INWESTOR (do uzupełnienia)	OBIEKT / NAZWA ZAMIERZENIA BUDOWLANEGO Budynek testowy pipeline'u (model testowy) — NIE jest projektem Domu LAMELA	
ADRES / LOKALIZACJA (NR DZIAŁKI, OBRĘB, JEDN. EWIDENCYJNA) dz. nr ewid. T-1/1, obręb 0000 Testowo	KAT. OBIEKTU I	
FUNKCJA	IMIĘ I NAZWISKO	SPECJALNOŚĆ, NR UPRAWNIENI
Projektant		DATA
Projektant (wsp.)		PODPIS
Sprawdzający		
Opracował		
TYTUŁ RYSUNKU PRZEKRÓJ B-B		
SKALA 1:50	FORMAT A3×3	DATA WYDANIA 2026-09-25
RODZAJ DOK. przekrój	NR RYSUNKU T-AR-05	ARKUSZ 5/9
		REW. 0

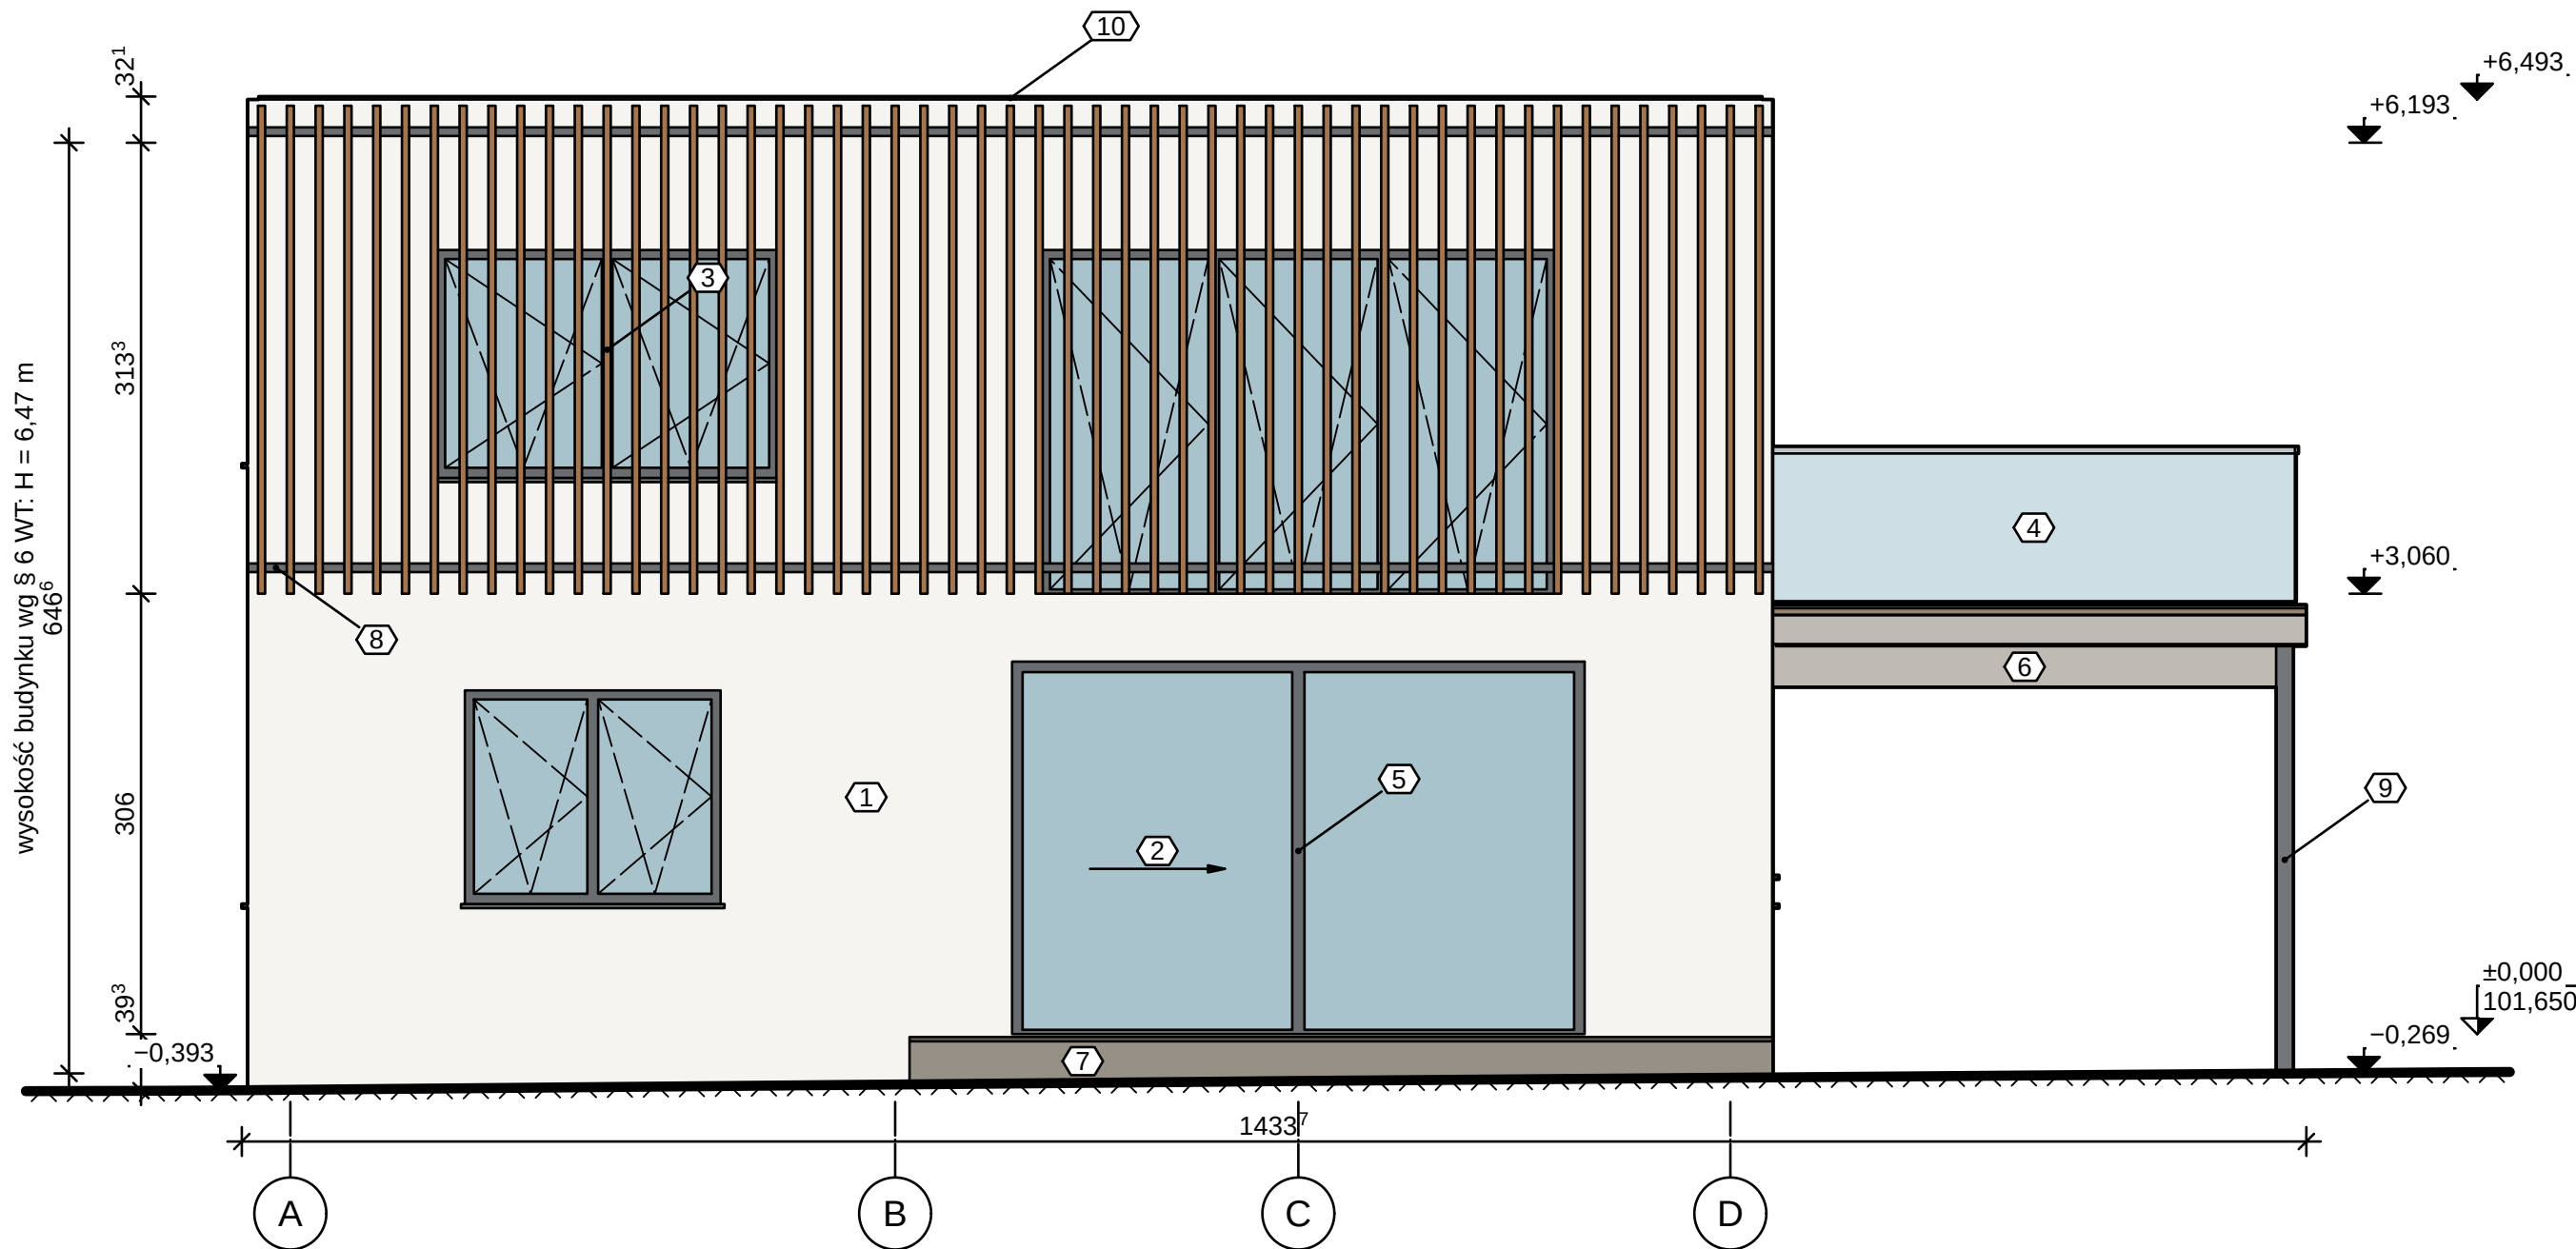


ELEWACJA POŁUDNIOWA 1:50

KOLORYSTYKA I MATERIAŁY ELEWACJI

1	Tynk silikonowy cienkowarstwowy, biały [TYNK_SIL]	#f5f4f0
2	Szkoło (szyby zespolone) [SZKLO]	#a9c3cd
3	Drewno termojesion (łamele elewacyjne) [DREWNO_TERM]	#9b6b41
4	Balustrada — szkło klejone [SZKLO_BAL]	#c9dde2
5	Stołarka — profile aluminiowe, antracyt [RAMA_ALU]	#2b2f33
6	Żelbet C30/37 [ZB_C30]	#b9b6ae
7	Podbudowa nawierzchni (kruszywo) [NAW_PODBUDOWA]	#8d877d
8	Stal malowana proszkowo (balustrady, rygle) [STAL_BAL]	#2c3034
9	Stal konstrukcyjna S355, malowana proszkowo RAL 7016 [STAL_S355]	#383e42
10	Obróbki blacharskie (blacha powlekana) [OBROBKA_BLACH]	#3b3f43

OBJAŚNIENIA I UWAGI

- Wymiary w cm (mm w indeksie górnym, np. 24⁵ = 24,5 cm), rzędne w m względem ±0,000 = 101,650 m n.p.m. (PL-EVRF2007-NH).
- Rzędne: trójkąt zaczerpiony — poziom wykończenia, niezaczerpiony — konstrukcji, w połowie zaczerpiony — poziom ±0,000 z rzędną bezwzględną (PN-B-01025).
- Wysokość budynku wg § 6 WT: od terenu przy najniższym położonym wejściu (-0,273) do wierzchu stropodachu D1 (+6,193) — H = 6,47 m (bez attyk).
- Kolorystyka orientacyjna wg kolorów materiałów w modelu (do potwierdzenia wzornikiem RAL/NCS).
- MODEL TESTOWY — rysunek próbny generatorów widoków; dane nie stanowią projektu.
- Rysunek wygenerowany automatycznie z modelu model/test/dom_testowy.yaml (wersja 1.0, 2026-09-25) — generatory lamela.views.

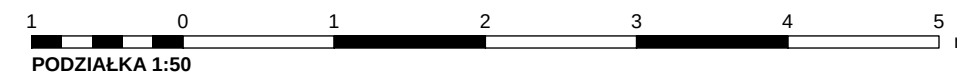

REW.	OPIS ZMIANY			DATA	
0	Próba generatorów widoków z modelu testowego			2026-09-25	
PRACOWNIA PROJEKTOWA PRACOWNIA PROJEKTOWA — nazwa do uzupełnienia			STADIUM PB	BRANŻA ARCHITEKTURA (AR)	
adres pracowni do uzupełnienia					
INWESTOR (do uzupełnienia)					
OBIEKT / NAZWA ZAMIERZENIA BUDOWLANEGO Budynek testowy pipeline'u (model testowy) — NIE jest projektem Domu LAMELA					
ADRES / LOKALIZACJA (NR DZIAŁKI, OBRĘB, JEDN. EWIDENCYJNA) dz. nr ewid. T-1/1, obręb 0000 Testowo				KAT. OBIEKTU I	
FUNKCJA	IMIĘ I NAZWISKO	SPECJALNOŚĆ, NR UPRAWNIEŃ	DATA	PODPIS	
Projektant					
Projektant (wsp.)					
Sprawdzający					
Opracował					
TYTUŁ RYSUNKU ELEWACJA POŁUDNIOWA					
SKALA 1:50	FORMAT A2	DATA WYDANIA 2026-09-25	RODZAJ DOK. elewacja	NR RYSUNKU T-AR-06	ARKUSZ 6/9
				REW.	0

wysokość budynku wg § 6 WT: H = 6.47 m


ELEWACJA PÓŁNOCNA 1:50

KOLORYSTYKA I MATERIAŁY ELEWACJI

1	Tynk silikonowy cienkowarstwowy, biały [TYNK_SIL]	#f5f4f0
2	Szkoło (szyby zespolone) [SZKLO]	#a9c3cd
3	Balustrada — szkło klejone [SZKLO_BAL]	#c9dde2
4	Drzwi zewnętrzne, płycina aluminiowa [DRZWI_ZEWN]	#34383c
5	Stołarka — profile aluminiowe, antracyt [RAMA_ALU]	#2b2f33
6	Żelbet C30/37 [ZB_C30]	#b9b6ae
7	Obróbki blacharskie (blacha powlekana) [OBROBKA_BLACH]	#3b3f43
8	Stal konstrukcyjna S355, malowana proszkowo RAL 7016 [STAL_S355]	#383e42

OBJAŚNIENIA I UWAGI

- Wymiary w cm (mm w indeksie górnym, np. 24⁵ = 24,5 cm), rzędne w m względem ±0,000 = 101,650 m n.p.m. (PL-EVRF2007-NH).
- Rzędne: trójkąt zaczerniony — poziom wykończenia, niezaczerniony — konstrukcji, w połowie zaczerniony — poziom ±0,000 z rzędną bezwzględną (PN-B-01025).
- Wysokość budynku wg § 6 WT: od terenu przy najniższym położonym wejściu (−0,273) do wierzchu stropodachu D1 (+6,193) — H = 6,47 m (bez attyk).
- Kolorystyka orientacyjna wg kolorów materiałów w modelu (do potwierdzenia wzornikiem RAL/NCS).
- MODEL TESTOWY — rysunek próbny generatorów widoków; dane nie stanowią projektu.
- Rysunek wygenerowany automatycznie z modelu model/test/dom_testowy.yaml (wersja 1.0, 2026-09-25) — generatory lamela.views.

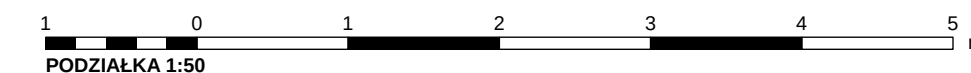



REW.	OPIS ZMIANY		DATA	
0	Próba generatorów widoków z modelu testowego		2026-09-25	
PRACOWNIA PROJEKTOWA		STADIUM	BRANŻA	
PRACOWNIA PROJEKTOWA — nazwa do uzupełnienia		PB	ARCHITEKTURA (AR)	
adres pracowni do uzupełnienia				
INWESTOR				
(do uzupełnienia)				
OBIEKT / NAZWA ZAMIERZENIA BUDOWLANEGO				
Budynek testowy pipeline'u (model testowy) — NIE jest projektem Domu LAMELA				
ADRES / LOKALIZACJA (NR DZIAŁKI, OBRĘB, JEDN. EWIDENCYJNA)			KAT. OBIEKTU	
dz. nr ewid. T-1/1, obręb 0000 Testowo			I	
FUNKCJA	IMIĘ I NAZWISKO	SPECJALNOŚĆ, NR UPRAWNIEŃ	DATA	PODPIS
Projektant				
Projektant (wsp.)				
Sprawdzający				
Opracował				
TYTUŁ RYSUNKU				
ELEWACJA PÓŁNOCNA				
SKALA	FORMAT	DATA WYDANIA	RODZAJ DOK.	NR RYSUNKU
1:50	A2	2026-09-25	elewacja	T-AR-07
			ARKUSZ	REW.
			7/9	0

KOLORYSTYKA I MATERIAŁY ELEWACJI

1		Tynk silikonowy cienkowarstwowy, biały [TYNK_SIL]	#f5f4f0
2		Szkoło (szyby zespolone) [SZKŁO]	#a9c3cd
3		Balustrada — szkło klejone [SZKŁO_BAL]	#c9dde2
4		Stolarka — profile aluminiowe, antracyt [RAMA_ALU]	#2b2f33
5		Żelbet C30/37 [ZB_C30]	#b9b6ae
6		Podbudowa nawierzchni (kruszywo) [NAW_PODBUDOWA]	#8d877d
7		Stal konstrukcyjna S355, malowana proszkowo RAL 7016 [STAL_S355]	#383e42
8		Drewno termojesion (lamelle elewacyjne) [DREWNO_TERMO]	#9b6b41
9		Obróbki blacharskie (blacha powlekana) [OBROBKA_BLACH]	#3b3f43

OBJAŚNIENIA I UWAGI

- Wymiary w cm (mm w indeksie górnym, np. 24⁵ = 24,5 cm), rzędne w m względem ±0,000 = 101,650 m n.p.m. (PL-EVRF2007-NH).
- Rzędne: trójkąt zaczerpiony — poziom wykończenia, niezaczerpiony — konstrukcji, w połowie zaczerpiony — poziom ±0,000 z rzędną bezwzględną (PN-B-01025).
- Wysokość budynku wg § 6 WT: od terenu przy najniższym położonym wejściu (−0,273) do wierzchu stropodachu D1 (+6,193) — H = 6,47 m (bez attyki).
- Kolorystyka orientacyjna wg kolorów materiałów w modelu (do potwierdzenia wzornikiem RAL/NCS).
- MODEL TESTOWY — rysunek próbny generatorów widoków; dane nie stanowią projektu.
- Rysunek wygenerowany automatycznie z modelu model/test/dom_testowy.yaml (wersja 1.0, 2026-09-25) — generatory lamela.views.

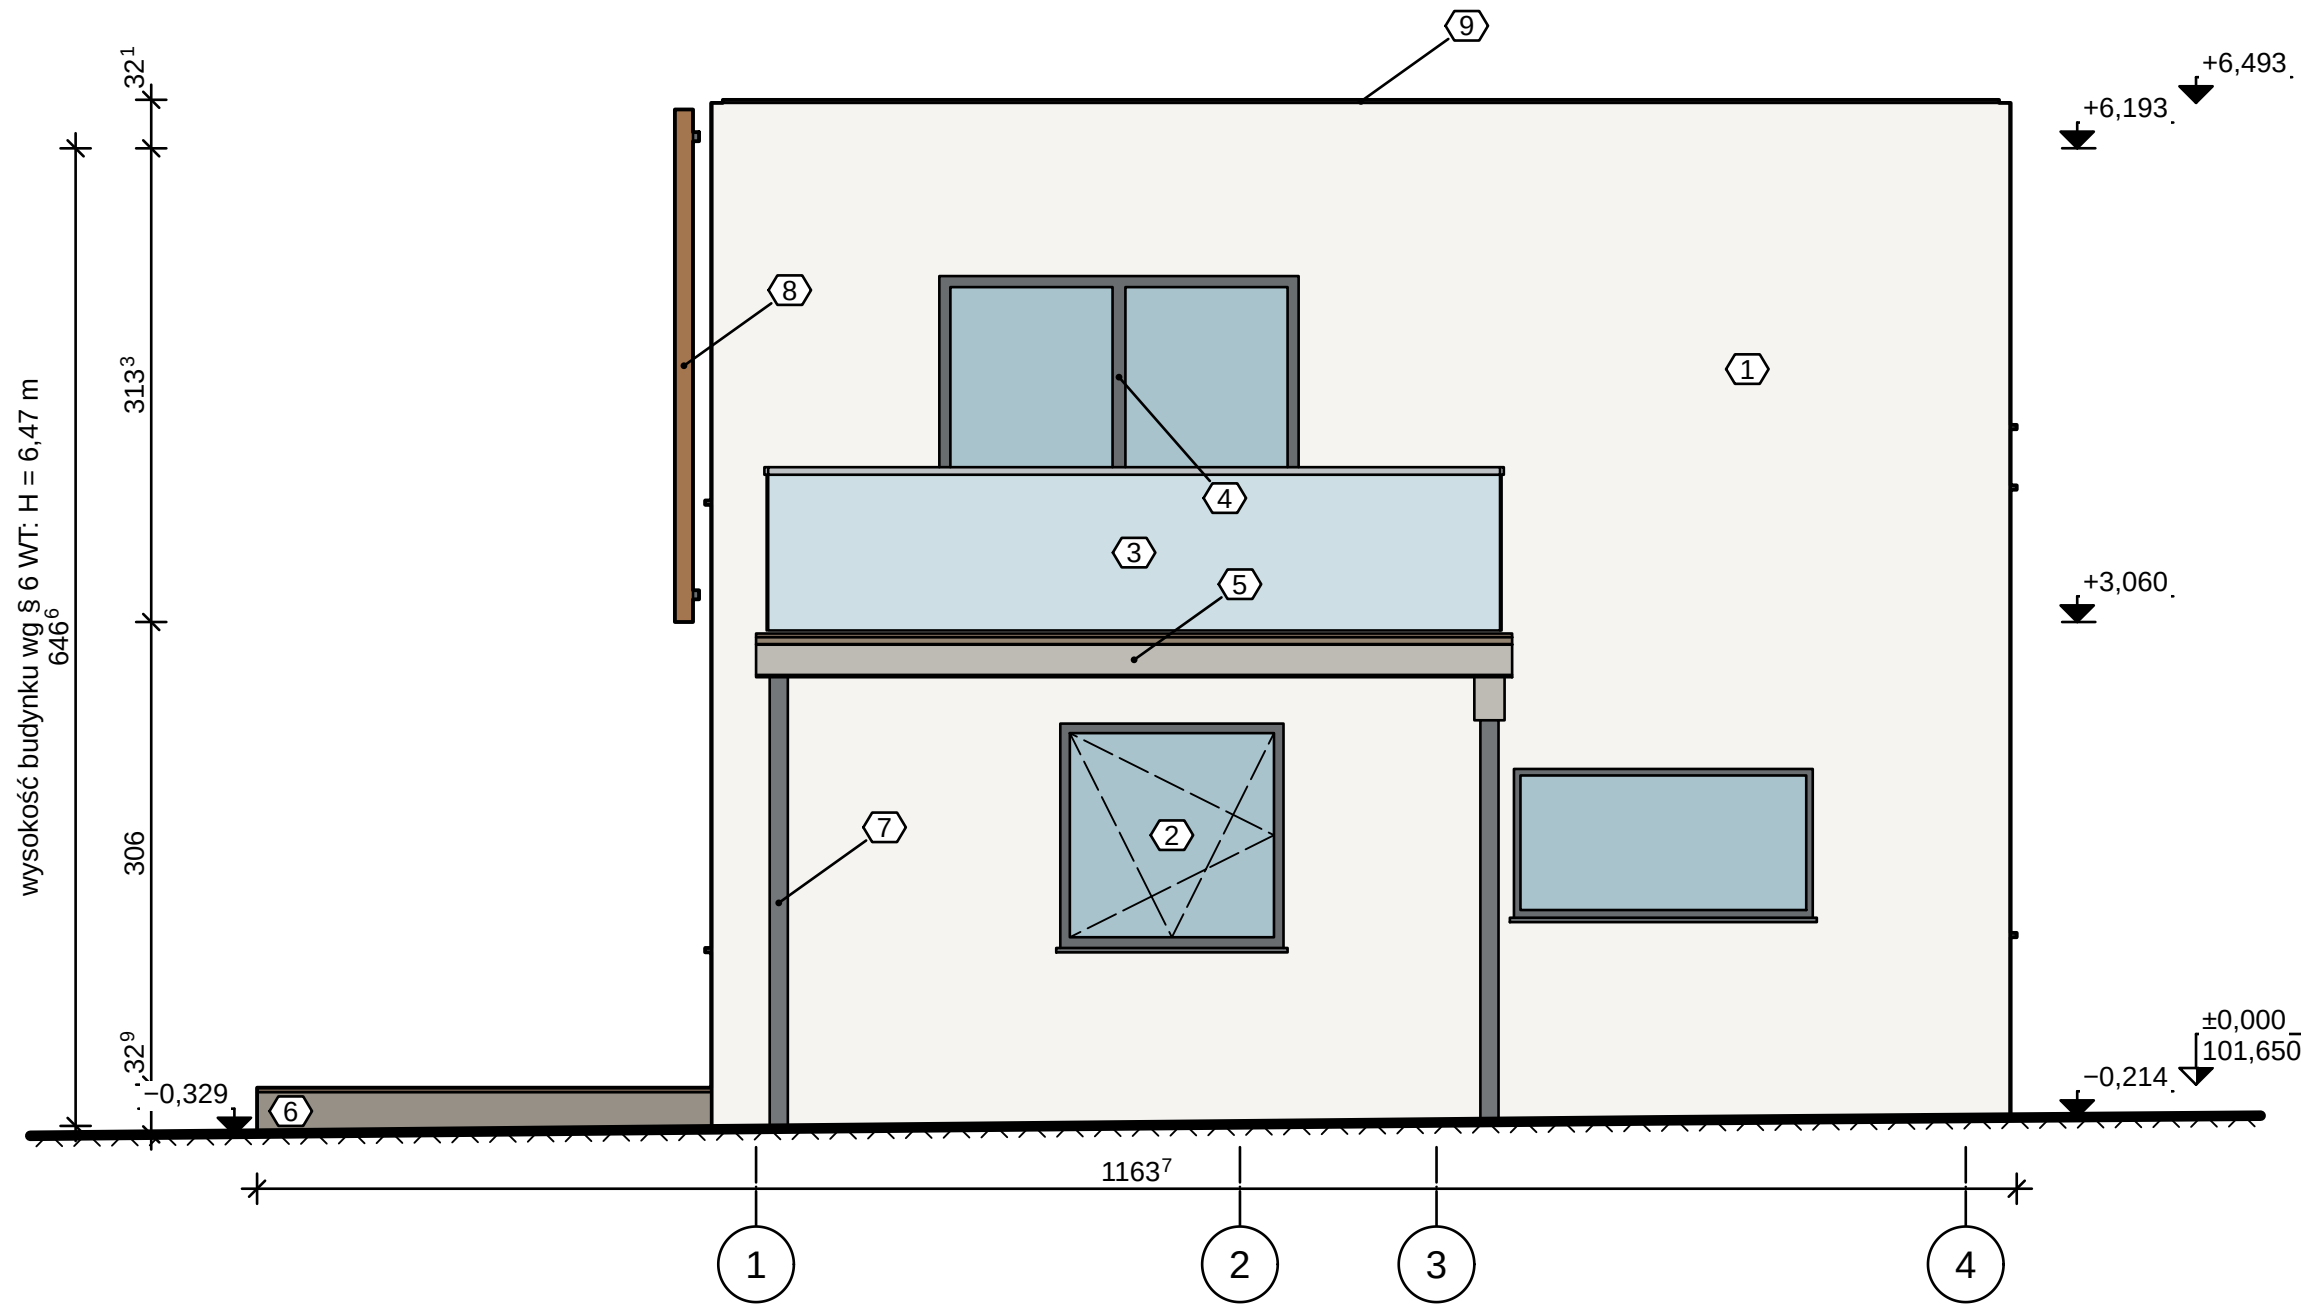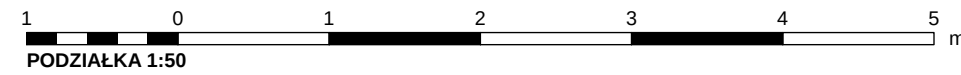

ELEWACJA WSCHODNIA 1:50



REW.	OPIS ZMIANY			DATA	
0	Próba generatorów widoków z modelu testowego			2026-09-25	
PRACOWNIA PROJEKTOWA PRACOWNIA PROJEKTOWA — nazwa do uzupełnienia adres pracowni do uzupełnienia			STADIUM PB	BRANŻA ARCHITEKTURA (AR)	
INWESTOR (do uzupełnienia)					
OBIEKT / NAZWA ZAMIERZENIA BUDOWLANEGO Budynek testowy pipeline'u (model testowy) — NIE jest projektem Domu LAMELA					
ADRES / LOKALIZACJA (NR DZIAŁKI, OBRĘB, JEDN. EWIDENCYJNA) dz. nr ewid. T-1/1, obręb 0000 Testowo				KAT. OBIEKTU I	
FUNKCJA	IMIĘ I NAZWISKO	SPECJALNOŚĆ, NR UPRAWNIEŃ	DATA	PODPIS	
Projektant					
Projektant (wsp.)					
Sprawdzający					
Opracował					
TYTUŁ RYSUNKU ELEWACJA WSCHODNIA					
SKALA 1:50	FORMAT A2	DATA WYDANIA 2026-09-25	RODZAJ DOK. elewacja	NR RYSUNKU T-AR-08	ARKUSZ 8/9
					REW. 0

KOLORYSTYKA I MATERIAŁY ELEWACJI

1	Tynk silikonowy cienkowarstwowy, biały [TYNK_SIL]	#f5f4f0
2	Szkło (szyby zespolone) [SZKLO]	#a9c3cd
3	Podbudowa nawierzchni (kruszywo) [NAW_PODBUDOWA]	#8d877d
4	Stolarka — profile aluminiowe, antracyt [RAMA_ALU]	#2b2f33
5	Drewno termojesion (lamelle elewacyjne) [DREWNO_TERMO]	#9b6b41
6	Obróbki blacharskie (blacha powlekana) [OBROBKA_BLACH]	#3b3f43

OBJAŚNIENIA I UWAGI

- Wymiary w cm (mm w indeksie górnym, np. 24⁵ = 24,5 cm), rzędne w m względem ±0,000 = 101,650 m n.p.m. (PL-EVRF2007-NH).
- Rzędne: trójkąt zaczerniony — poziom wykończenia, niezaczerniony — konstrukcji, w połowie zaczerniony — poziom ±0,000 z rzędną bezwzględną (PN-B-01025).
- Wysokość budynku wg § 6 WT: od terenu przy najniższym położonym wejściu (−0,273) do wierzchu stropodachu D1 (+6,193) — H = 6,47 m (bez attyki).
- Kolorystyka orientacyjna wg kolorów materiałów w modelu (do potwierdzenia wzornikiem RAL/NCS).
- MODEL TESTOWY — rysunek próbny generatorów widoków; dane nie stanowią projektu.
- Rysunek wygenerowany automatycznie z modelu model/test/dom_testowy.yaml (wersja 1.0, 2026-09-25) — generatory lamela.views.

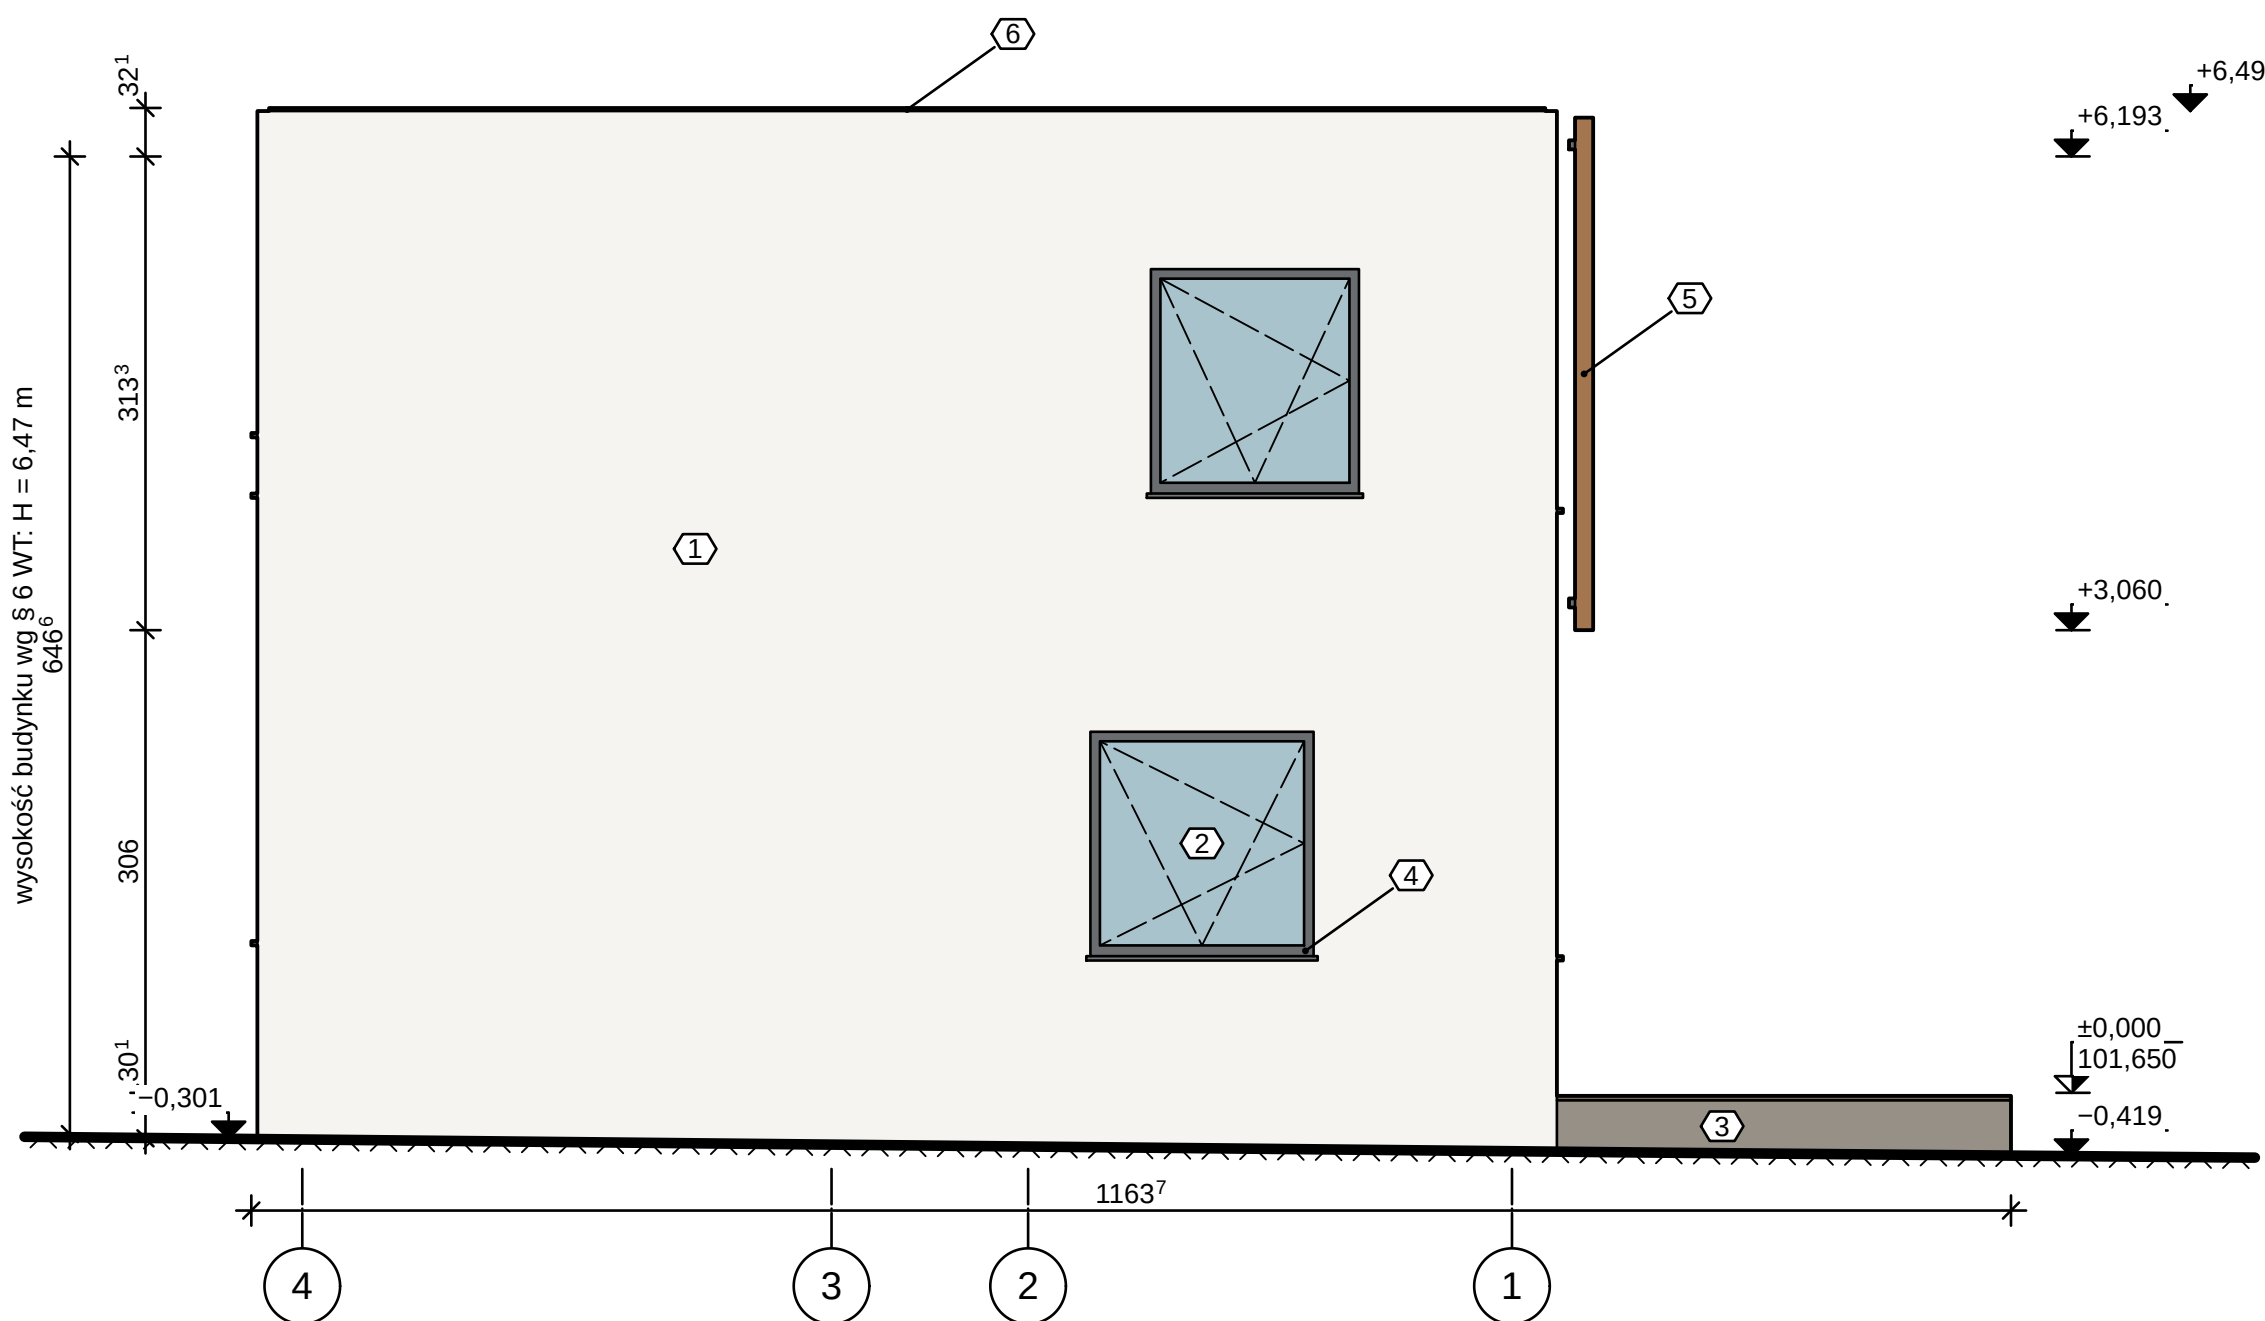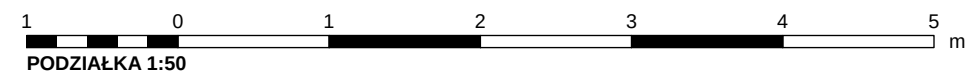

ELEWACJA ZACHODNIA 1:50

REW.	OPIS ZMIANY			DATA	
0	Próba generatorów widoków z modelu testowego			2026-09-25	
PRACOWNIA PROJEKTOWA PRACOWNIA PROJEKTOWA — nazwa do uzupełnienia adres pracowni do uzupełnienia			STADIUM PB	BRANŻA ARCHITEKTURA (AR)	
INWESTOR (do uzupełnienia)					
OBIEKT / NAZWA ZAMIERZENIA BUDOWLANEGO Budynek testowy pipeline'u (model testowy) — NIE jest projektem Domu LAMELA					
ADRES / LOKALIZACJA (NR DZIAŁKI, OBRĘB, JEDN. EWIDENCYJNA) dz. nr ewid. T-1/1, obręb 0000 Testowo				KAT. OBIEKTU I	
FUNKCJA		IMIĘ I NAZWISKO	SPECJALNOŚĆ, NR UPRAWNIEŃ	DATA	PODPIS
Projektant					
Projektant (wsp.)					
Sprawdzający					
Opracował					
TYTUŁ RYSUNKU ELEWACJA ZACHODNIA					
SKALA 1:50	FORMAT A2	DATA WYDANIA 2026-09-25	RODZAJ DOK. elewacja	NR RYSUNKU T-AR-09	ARKUSZ 9/9
					REW. 0