


TOM RYSUNKÓW ARCHITEKTURY — WIDOKI Z MODELU

Lp.	Nr rys.	Tytuł rysunku	Skala	Format
1	PB-AR-01	RZUT PARTERU	1:50	630×594
2	PB-AR-02	RZUT I PIĘTRA	1:50	770×420
3	PB-AR-03	RZUT II PIĘTRA I RZUT DACHU	1:50	590×891
4	PB-AR-04	PRZEKROJE A-A I B-B	1:50	1130×420
5	PB-AR-05	ELEWACJE	1:50	2050×297

PRACOWNIA PROJEKTOWA PRACOWNIA PROJEKTOWA — nazwa do uzupełnienia		STADIUM PB	BRANŻA ARCHITEKTURA (AR)			
INWESTOR (do uzupełnienia)						
OBIEKT / NAZWA ZAMIERZENIA BUDOWLANEGO Budynek mieszkalny jednorodzinny wolnostojący „Dom LAMELA”						
ADRES / LOKALIZACJA (NR DZIAŁKI, OBRĘB, JEDN. EWIDENCYJNA) ul. Lipowa (fikcyjna), dz. nr ewid. 123/4, obręb 0005 Przykładowo, gm. Przykładowo (fikcyjna)			KAT. OBIEKTU I			
FUNKCJA	IMIĘ I NAZWISKO	SPECJALNOŚĆ, NR UPRAWNIENI	DATA	PODPIS		
Projektant	[DO UZUPEŁNIENIA]	[DO UZUPEŁNIENIA]				
Projektant (wsp.)	[DO UZUPEŁNIENIA]	[DO UZUPEŁNIENIA]				
Sprawdzający	nie dotyczy (art. 20 ust. 3 pkt 2 PB)	—				
Opracował	[DO UZUPEŁNIENIA]	[DO UZUPEŁNIENIA]				
TYTUŁ RYSUNKU SPIS RYSUNKÓW						
SKALA —	FORMAT A4	DATA WYDANIA 2026-09-25	RODZAJ DOK. spis	NR RYSUNKU PB-AR-00	ARKUSZ —	REW.

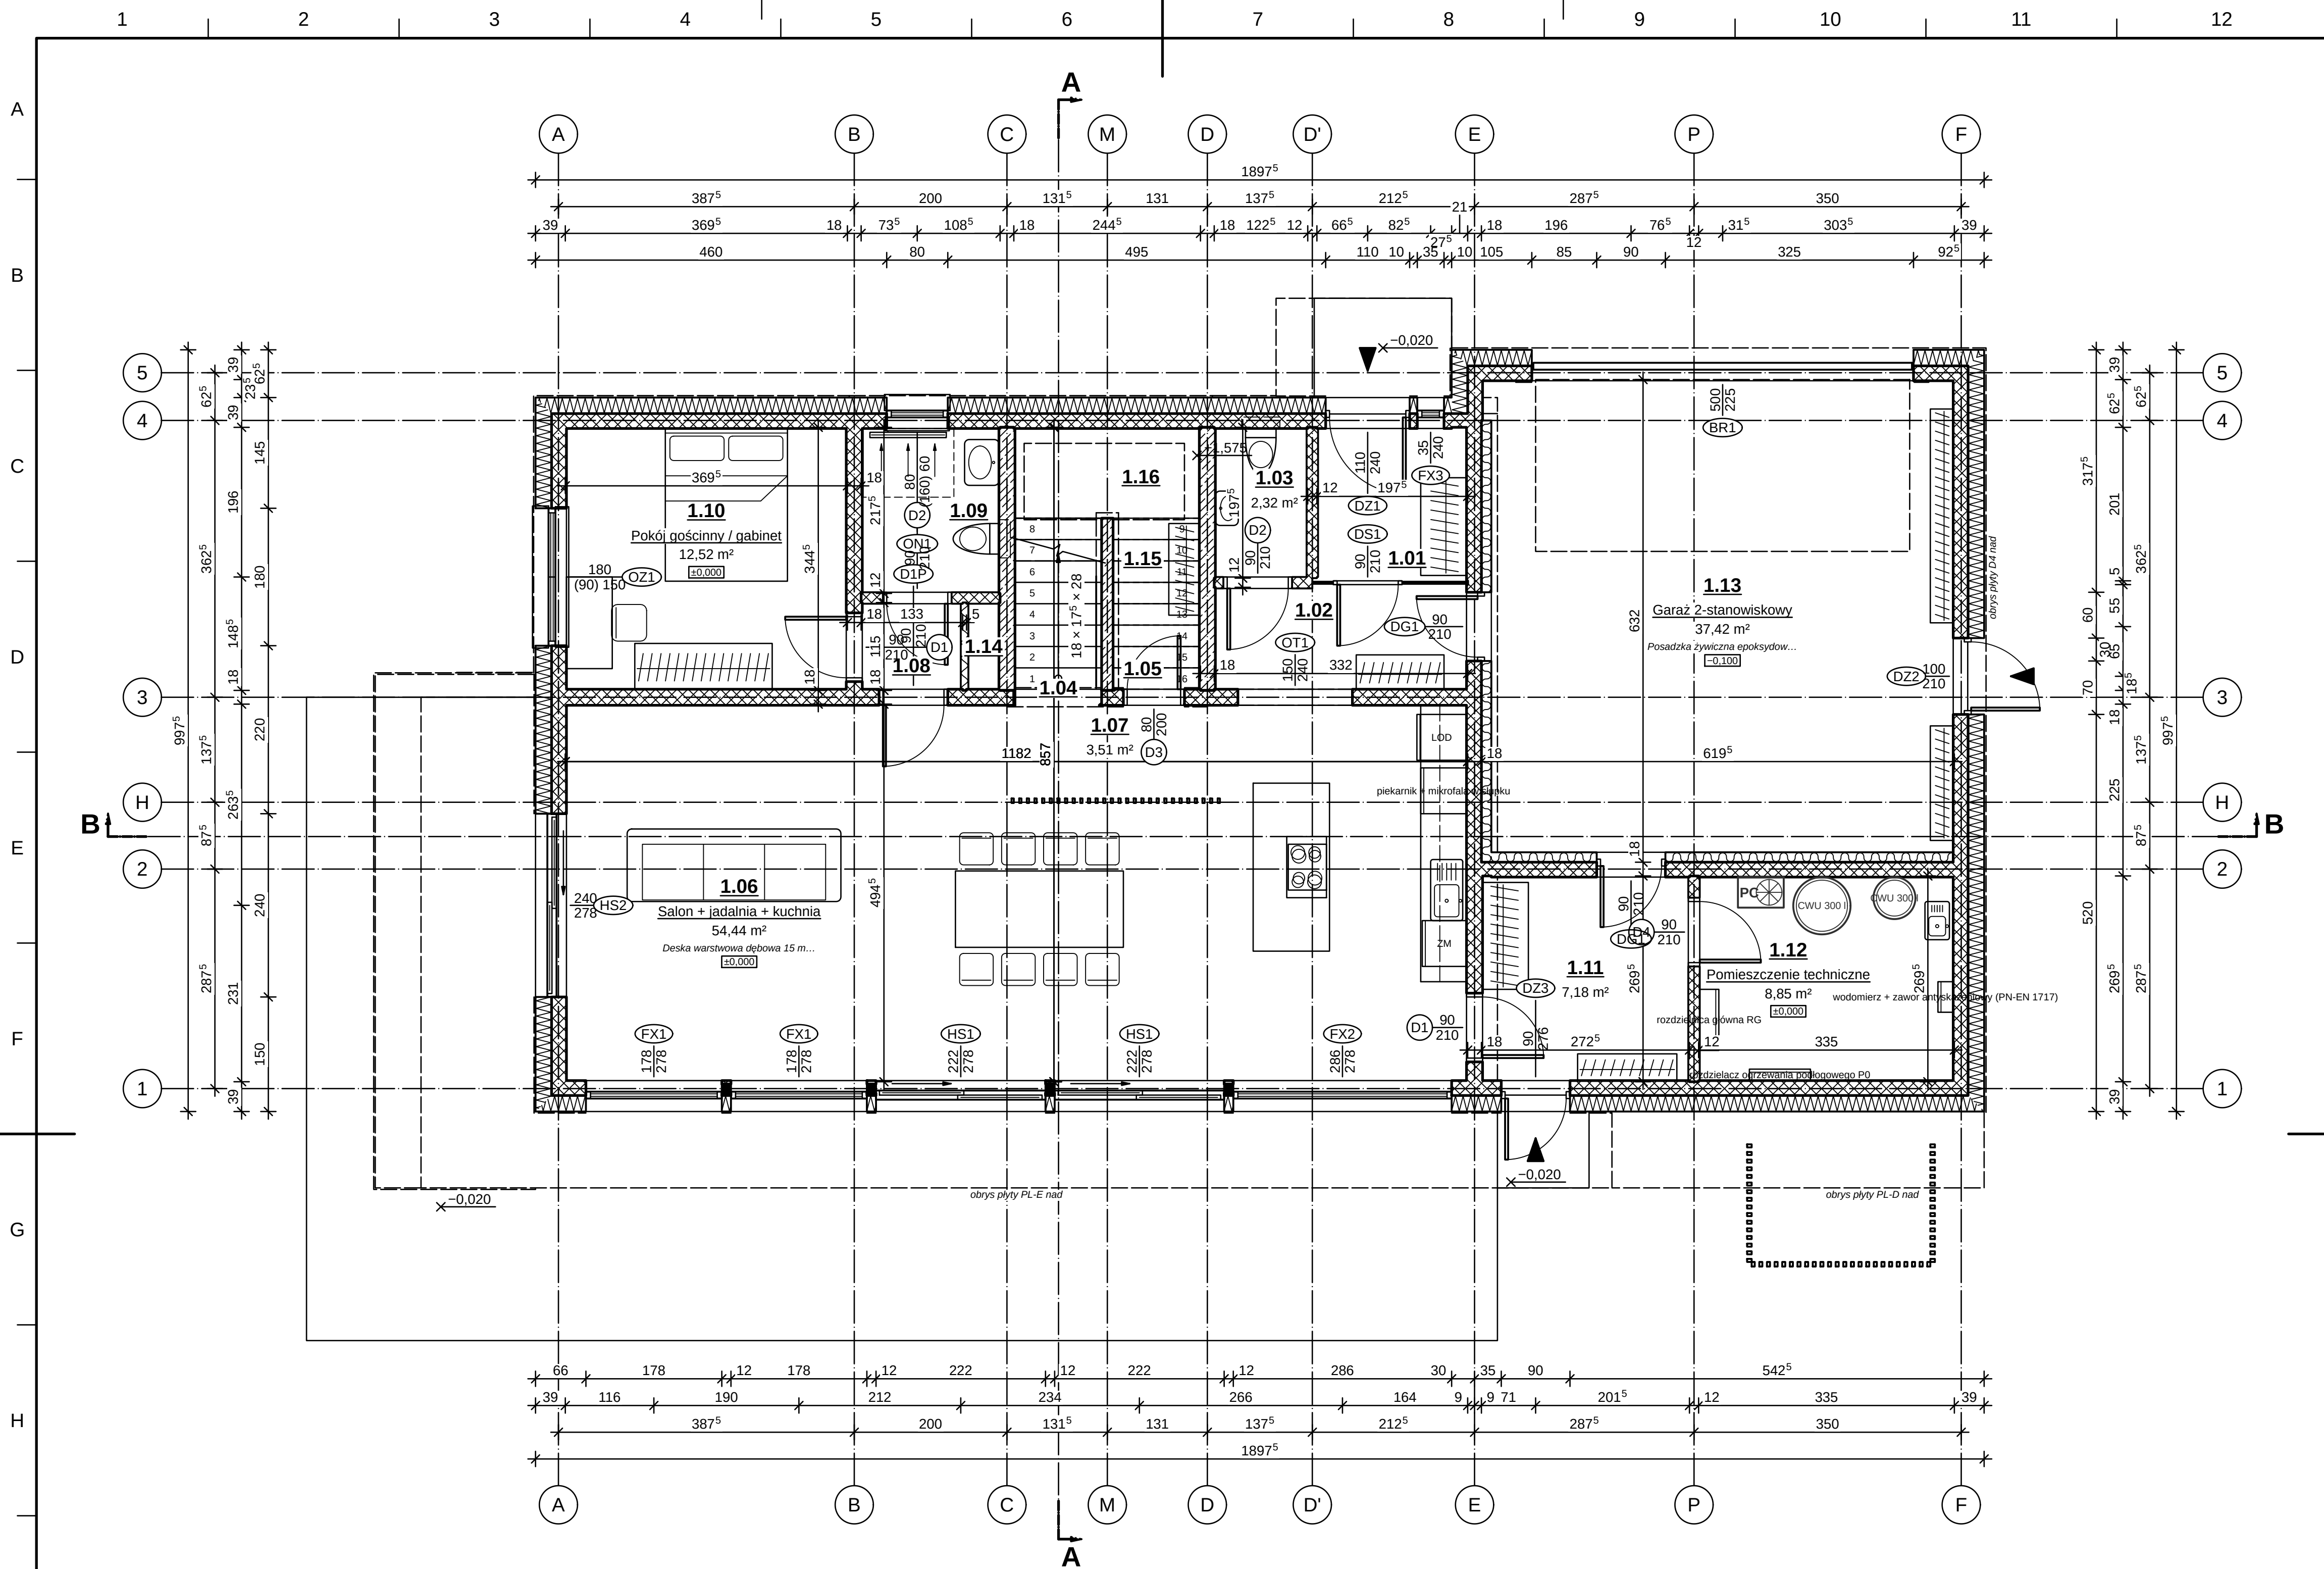

RZUT PARTERU 1:50

ZESTAWIENIE POMIESZCZEŃ

Nr	Nazwa pomieszczenia	Posadzka	Kat.	Wys. [m]	Pow. [m²]
1.06	Salon + jadalnia + kuchnia	Deska warstwowa dębowa 15 mm, klejona	podst.	2,77	54,44
1.13	Garaż 2-stanowiskowy	Posadzka żywiczna epoksydowa antypoślizgowa R11 (garaż)	pomoc.	2,76	37,42
1.10	Pokój gościnny / gabinet	Deska warstwowa dębowa 15 mm, klejona	podst.	2,77	12,52
1.12	Pomieszczenie techniczne	Płytki gresowe 60×120 na kleju C2TE S1	techn.	2,76	8,85
1.11	Przedśionek gospodarczy	Płytki gresowe 60×120 na kleju C2TE S1	ruchu	2,76	7,18
1.02	Hoł	Płytki gresowe 60×120 na kleju C2TE S1	ruchu	2,77	4,44
1.01	Wiatrołap	Płytki gresowe 60×120 na kleju C2TE S1	ruchu	2,77	3,89
1.09	Łazienka gościnna (natrysk)	Płytki gresowe 60×120 na kleju C2TE S1	pomoc.	2,77	3,84
1.07	Pas komunikacyjny przy schodach	Deska warstwowa dębowa 15 mm, klejona	ruchu	2,77	3,51
1.16	Schówek pod spocznikiem (h < 1,40)	Płytki gresowe 60×120 na kleju C2TE S1	pomoc.	1,37	2,91
1.04	Klatka schodowa	Deska warstwowa dębowa 15 mm, klejona	ruchu	2,77	2,78
1.03	WC gościnne	Płytki gresowe 60×120 na kleju C2TE S1	pomoc.	2,77	2,32
1.15	Schówek pod schodami (h 1.40-2.20)	Płytki gresowe 60×120 na kleju C2TE S1	pomoc.	1,80	1,45
1.08	Przedpokój gościnny	Deska warstwowa dębowa 15 mm, klejona	ruchu	2,77	1,44
1.05	Spizarnia	Płytki gresowe 60×120 na kleju C2TE S1	pomoc.	2,77	1,02
1.14	Szacht instalacyjny SI		techn.	2,77	0,45
RAZEM powierzchnia netto					148,45
w tym podstawowa + pomocnicza					115,91

OZNACZENIA MATERIAŁÓW (PN-B-01030 + przyjęte)



	Włna mineralna 035 (szkielet, docieplenia, ściana dom-garaż) — meander „UUU”		Stal konstrukcyjna S355 (słupy RK, rama boksu C), cynkowana ogniowo + malowana proszkowo RAL 7016 — zacierzenie
	Styropian grafitowy EPS 031 (ETICS, NRO w systemie) — zygzak „VVV”		Ścianka szklana VSG 2 × 8 mm w ramie aluminiowej (wiatrołap / hol)
	Błoczek wapienno-piaskowy 12 cm, kl. 15 (ścianki działowe, lico w klatce); Błoczek wapienno-piaskowy (silikat) 18 cm, kl. 20, gr. 1, na zaprawie cienkowarstwowej — krawka ukośna 45°/135°		Żelbet C25/30, B500SP (stropy, płyta fundamentowa, ściany); Żelbet C30/37 XC4/XF1 (krawędzie płyt wysuniętych, attyki, belki) — 45° na przemian ciągłe i przerywane

OZNACZENIA LINII

---	elementy nad płaszczyzną cięcia (obrysy płyt, wsporników, brył wyższych kondygnacji)
---	elementy poniżej płaszczyzny cięcia (widok z góry)
---	osie konstrukcyjne; linia punktowa z pogrubionymi końcami — ślad przekroju

OBJAŚNIENIA I UWAGI

- Wymiary w cm (mm w indeksie górnym, np. 24° = 24,5 cm), rzędne w m względem ±0,000 = 101,650 m n.p.m. (PL-EVRF2007-NH).
- Rzuty: płaszczyzna cięcia +1.10 m nad posadzką kondygnacji. Linia kreskową — elementy nad płaszczyzną cięcia (obrysy płyt i wsporników, brył wyższych kondygnacji, otwory w stropie nad, belki); linią ciekłą — elementy poniżej (widok).
- Otwory: licznik — szerokość, mianownik — wysokość w świetle muru, w nawiasie wysokość parapetu; symbol stolarki wg zestawienia stolarki.
- Numeracja pomieszczeń wg PN-B-01025 / PN-EN ISO 4157-2: <nr kondygnacji (partier = 1)> <nr> <identyfikator w modelu: <kond> <nr> (partier = 0)>.
- Drzwi: strona otwierania (lewe/prawe) wg modelu — patrząc od strony, w którą otwiera się skrzydło.
- Rysunek wygenerowany automatycznie z modelu model/budynek-yaml (wersja 1.0, 2026-09-25) — generatory lamela.views.

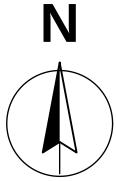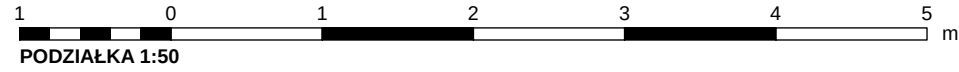

REW.	OPIS ZMIANY			DATA	
0	Wydanie — rysunek wygenerowany z modelu			2026-09-25	
PRACOWNIA PROJEKTOWA				STADIUM	
PRACOWNIA PROJEKTOWA — nazwa do uzupełnienia				PB	
adres pracowni do uzupełnienia				BRANŻA	
ARCHITEKTURA (AR)					
INWESTOR					
(do uzupełnienia)					
OBIEKT / NAZWA ZAMIERZENIA BUDOWLANEGO					
Budynek mieszkalny jednorodzinny wolnostojący „Dom LAMELA”					
ADRES / LOKALIZACJA (NR DZIAŁKI, OBRĘB, JEDN. EWIDENCYJNA)				KAT. OBIEKTU	
ul. Lipowa (fikcyjna), dz. nr ewid. 123/4, obręb 0005 Przykładowo, gm. Przykładowo (fikcyjna)				I	
FUNKCJA		IMIĘ I NAZWISKO	SPECJALNOŚĆ, NR UPRAWNIEN	DATA	PODPIS
Projektant		[DO UZUPEŁNIENIA]	[DO UZUPEŁNIENIA]		
Projektant (wsp.)		[DO UZUPEŁNIENIA]	[DO UZUPEŁNIENIA]		
Sprawdzający		nie dotyczy (art. 20 ust. 3 pkt 2 PB)	—		
Opracował		[DO UZUPEŁNIENIA]	[DO UZUPEŁNIENIA]		
TYTUŁ RYSUNKU					
RZUT PARTERU					
SKALA	FORMAT	DATA WYDANIA	RODZAJ DOK.	NR RYSUNKU	ARKUSZ
1:50	630×594	2026-09-25	rzut	PB-AR-01	1/5
				REW.	0

RZUT II PIĘTRA 1:50

OZNACZENIA LINII


- elementy nad płaszczyzną cięcia (obrysy płyt, wsporników, brył wyższych kondygnacji)
--- elementy poniżej płaszczyzny cięcia (widok z góry)
--- osie konstrukcyjne; linia punktowa z pogrubionymi końcami — ślad przebiegu

RZUT DACHU 1:50

OBJAŚNIENIA I UWAGI

- Wymiary w cm (mm w indeksie górnym, np. 24° = 24,5 cm), rzędne w m względem ±0,000 = 101,650 m n.p.m. (PL-EVRF2007-NH).
- Rzuty: płaszczyzna cięcia +1,10 m nad posadzką kondygnacji. Linia kreskowa — elementy nad płaszczyzną cięcia (obrysy płyt i wsporników, brył wyższych kondygnacji), otwory w stropie nad, belki), linia cienka — elementy poniżej (widok).
- Otwory: licznik — szerokość; mianownik — wysokość w świetle muru, w nawiasie wysokość parapetu; symbol stolarki wg zestawienia stolarki.
- Numeracja pomieszczeń wg PN-B-01025 / PN-EN ISO 4157-2: <nr kondygnacji (parter = 1)> <nr> <identyfikator w modelu: <kond> <nr> (parter = 0).
- Drzwi: strona otwierania (lewe/prawe) wg modelu — patrzeć od strony, w którą otwiera się skrzydło.
- Rysunek wygenerowany automatycznie z modelu model/budynki.yamli (wersja 1.0, 2026-09-25) — generatory lamela.views.

1 0 1 2 3 4 5 m
PODZIAŁKA 1:50

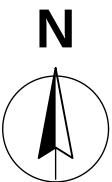

ZESTAWIENIE POMIESZCZEŃ


Nr	Nazwa pomieszczenia	Posadzka	Kat.	Wys. [m]	Pow. [m²]
3.02	Sypialnia rodziców	Deska warstwowa dębowa 15 mm, klejona	podst.	2,77	21,43
3.05	Gabinet / pokój gościnny okazjonalny	Deska warstwowa dębowa 15 mm, klejona	podst.	2,77	16,25
3.03	Garderoba (przedpokój apartamentu)	Deska warstwowa dębowa 15 mm, klejona	pomoc.	2,77	10,49
3.07	Pom. techniczne (centrala rekuperacyjna, wyłaz na dach)	Płytki gresowe 60×120 na kleju C2TE S1	techn.	2,77	5,90
3.01	Hol	Deska warstwowa dębowa 15 mm, klejona	ruchu	2,77	5,74
3.04	Łazienka rodziców	Płytki gresowe 60×120 na kleju C2TE S1	pomoc.	2,77	5,51
3.08	Szacht instalacyjny SI		techn.	2,77	0,45
3.06	Klatka schodowa (wyjście z biegu 2, pustka)	Deska warstwowa dębowa 15 mm, klejona	ruchu	2,77	0,24
RAZEM powierzchnia netto					66,01
w tym podstawowa + pomocnicza					53,67

OZNACZENIA MATERIAŁÓW (PN-B-01030 + przyjęte)


	Włna mineralna 035 (szkielet, docieplenia, ściana dom-garaz); Włna mineralna fasadowa (elewacja wentylowana bryły A, A1) — meander „UUU”		Błoczek wapienno-piaskowy 12 cm, kl. 15 (ściana działowa, łączący w klatce); Błoczek wapienno-piaskowy (silikat) 18 cm, kl. 20, gr. 1, na zaprawie cienkowarstwowej — kratka ukosna 45/7,35°
	Styropian grafitowy EPS 031 (ETICS, NRO w systemie) — zygzrak „VVV”		Żelbet C25/30, B500SP (stropy, płyta fundamentowa, ściany); Żelbet C30/37 XC4/XF1 (krawędzie płyt wysuniętych, atyki, belki) — 45° na przemian cienie i przerywane
	Membrana fasadowa wiatroizolacyjna UV-stabilna, czarna (sd = 0,02 m)		

REW.	OPIS ZMIANY	DATA
0	Wydanie — rysunek wygenerowany z modelu	2026-09-25
PRACOWNIA PROJEKTOWA PRACOWNIA PROJEKTOWA — nazwa do uzupełnienia		STADIUM PB
adres pracowni do uzupełnienia		BRANŻA ARCHITEKTURA (AR)
INWESTOR (do uzupełnienia)		
OBJEKT / NAZWA ZAMIERZENIA BUDOWLANEGO Budynek mieszkalny jednorodzinny wolnostojący „Dom LAMELA”		
ADRES / LOKALIZACJA (NR DZIAŁKI, OBRĘB, JEDN. EWIDENCYJNA) ul. Lipowa (fikcyjna), dz. nr ewid. 123/4, obręb 0005 Przykładowo, gm. Przykładowo (fikcyjna)		KAT. OBJEKTU I
FUNKCJA	IMIĘ I NAZWISKO	SPECJALNOŚĆ, NR UPRAWNIENI
Projektant	[DO UZUPEŁNIENIA]	[DO UZUPEŁNIENIA]
Projektant (wsp.)	[DO UZUPEŁNIENIA]	[DO UZUPEŁNIENIA]
Sprawdzający	nie dotyczy (art. 20 ust. 3 pkt 2 PB)	—
Opracował	[DO UZUPEŁNIENIA]	[DO UZUPEŁNIENIA]
TYTUŁ RYSUNKU RZUT II PIĘTRA I RZUT DACHU		
SKALA 1:50	FORMAT 590×891	DATA WYDANIA 2026-09-25
RODZAJ DOK. Rzut	NR RYSUNKU PB-AR-03	ARKUSZ 3/5
REW. 0		

PRZĘKRÓJ A-A 1:50

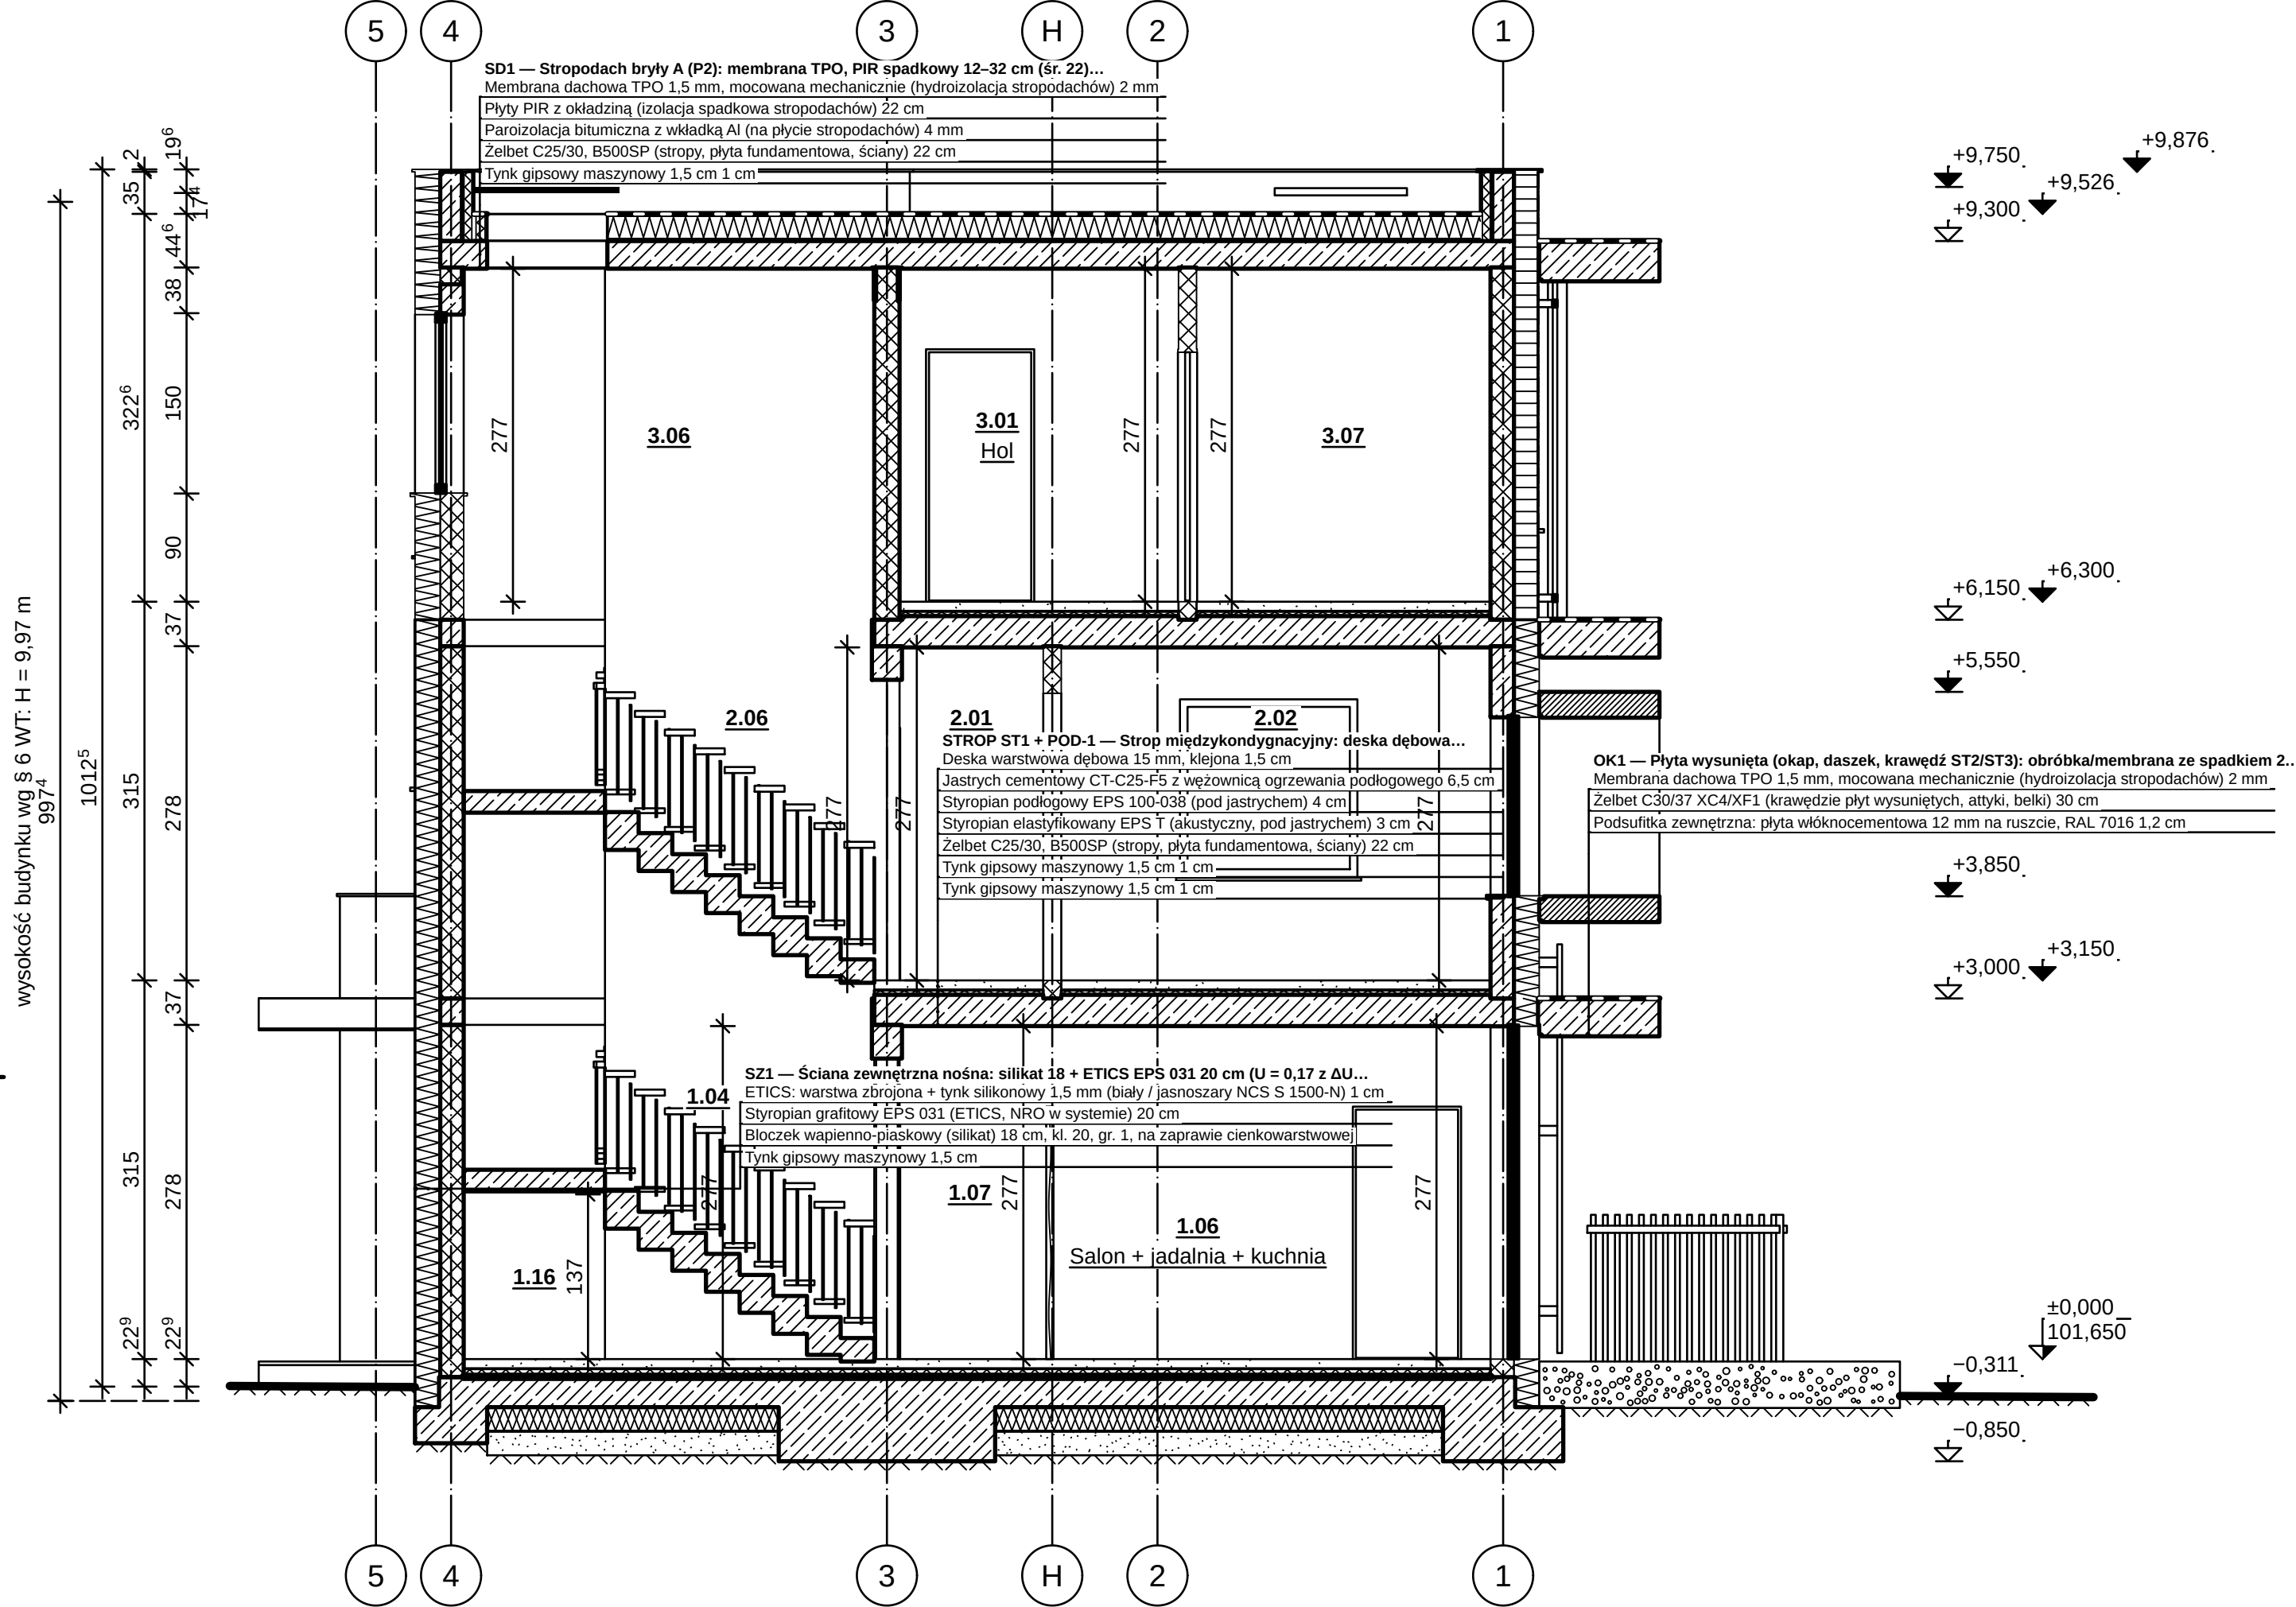

PRZĘKRÓJ B-B 1:50

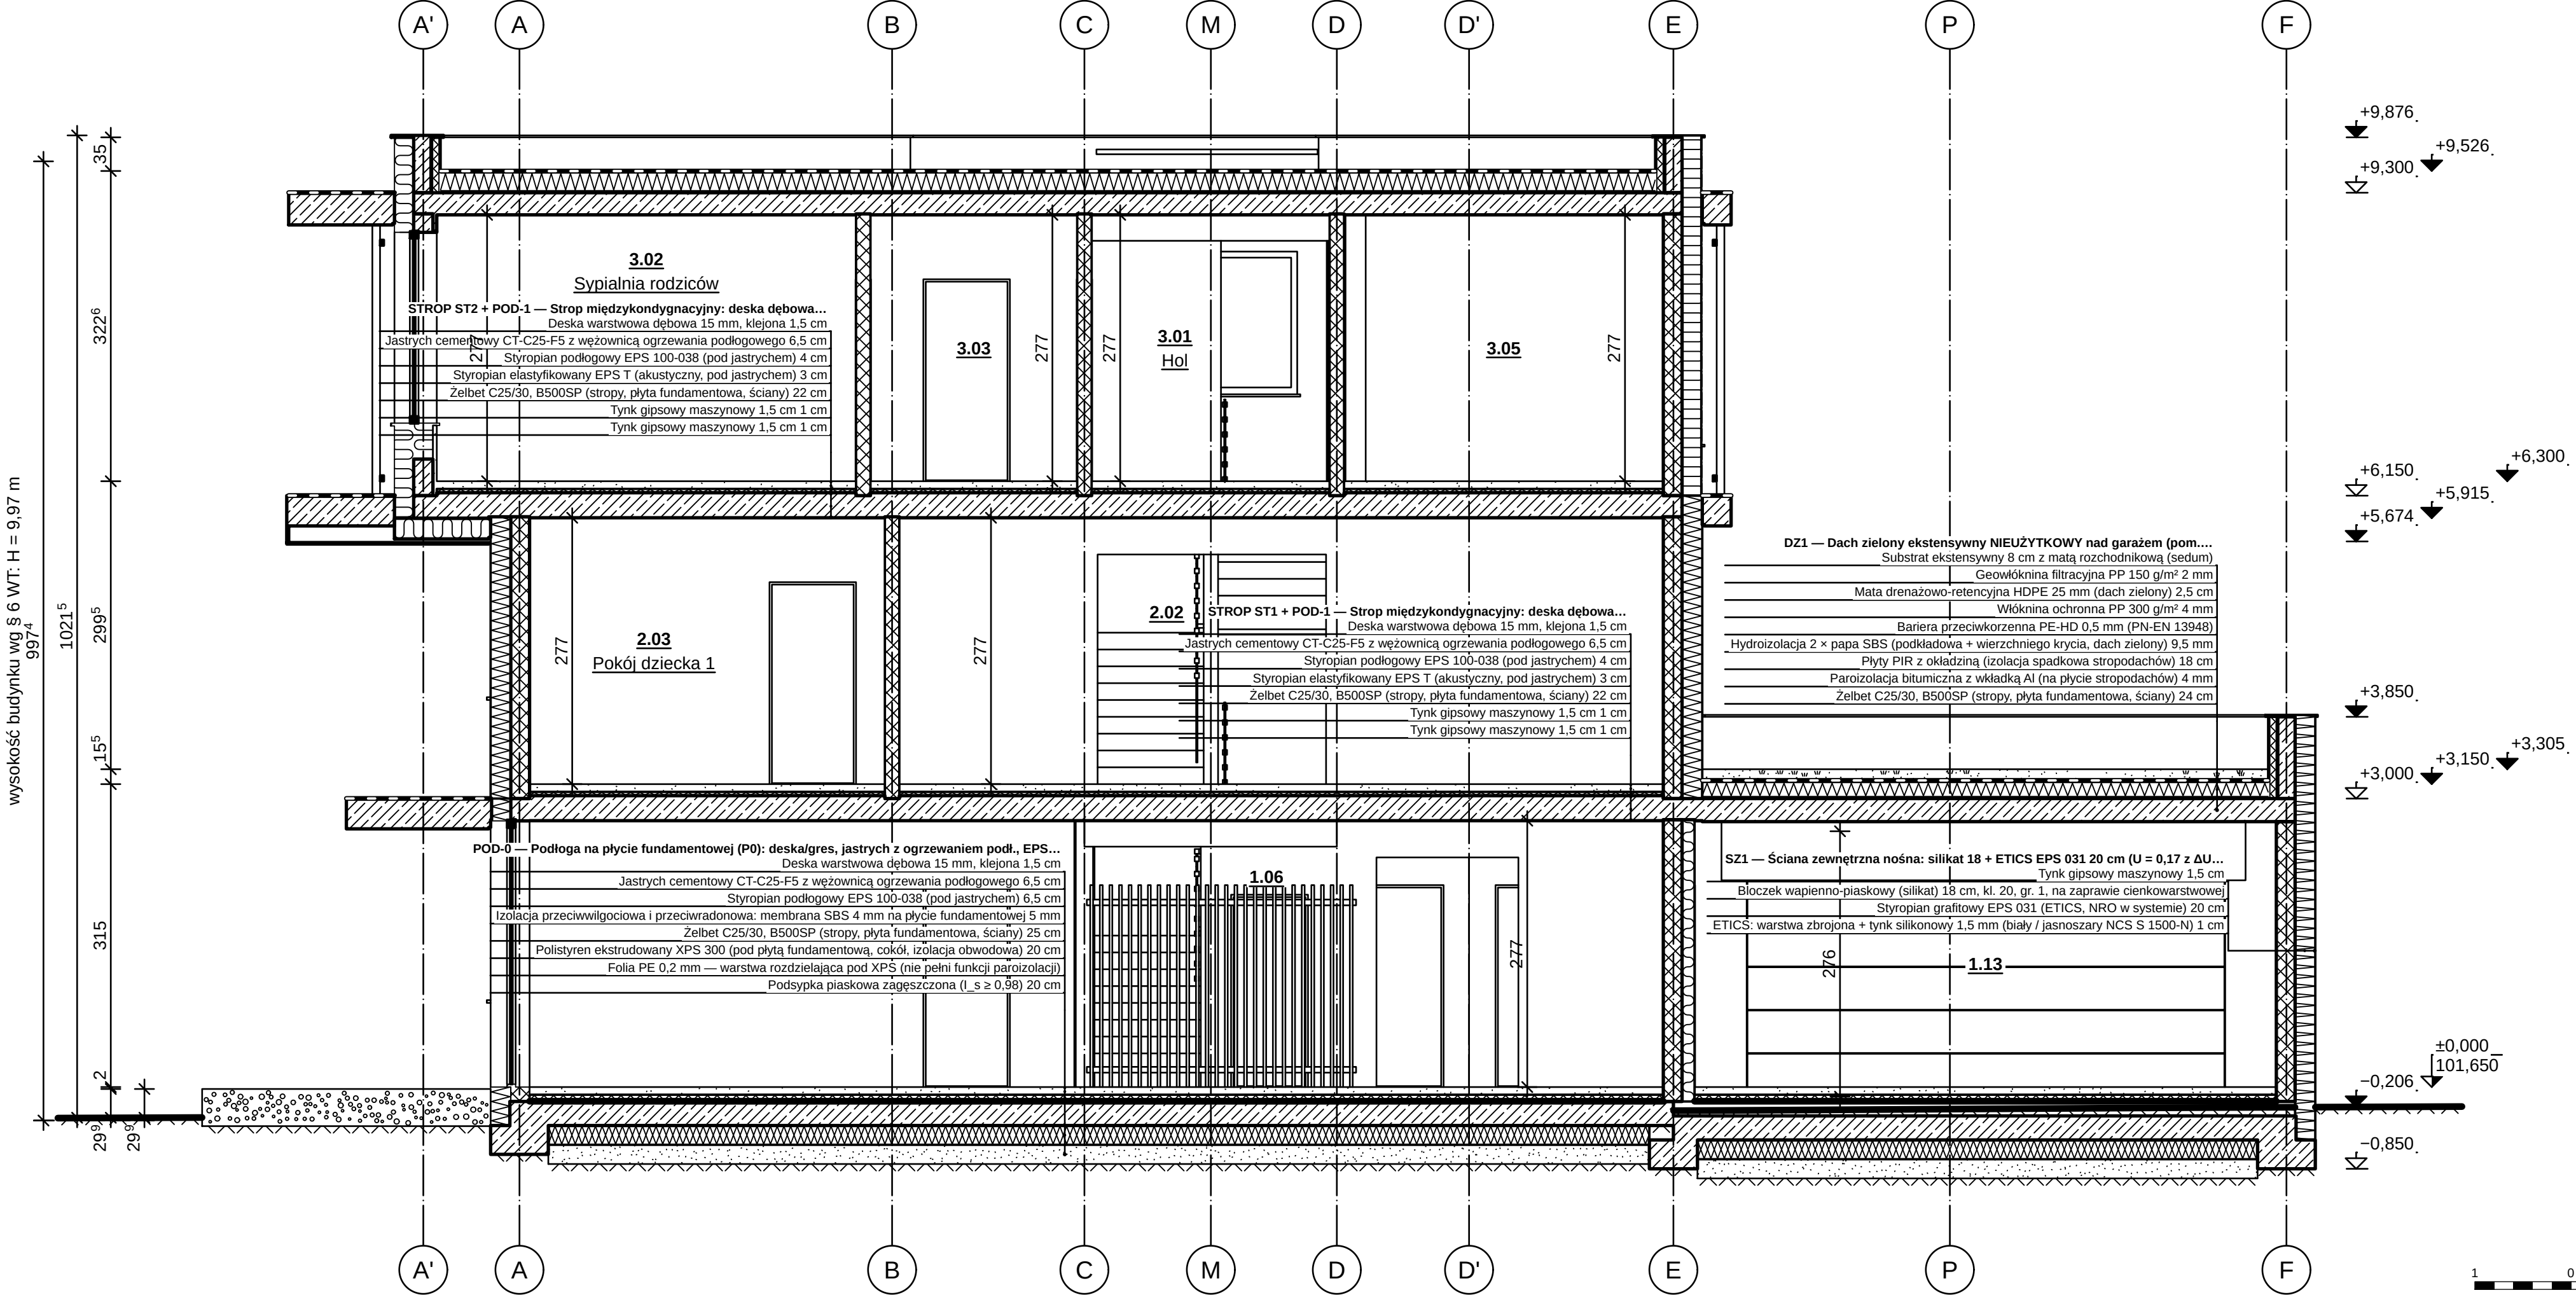

OZNACZENIA MATERIAŁÓW (PN-B-01030 + przyjęte)


- Lamele dębowe 30x60 mm (ekran komunikacji P0, h 2,10 m); Deska warstwowa dębowa 15 mm, klejona — przekrój wzdluż włókien
- grunt rodzimy
- Substrat ekstensywny 8 cm z matą rozchodnikową (sedum)
- Wełna mineralna fasadowa (elewacja wentylowana bryły A, A1); Wełna mineralna 035 (szkielet, docieplenia, ściana dom-garaz) — meander „U”/”
- Płyty PIR z okładziną (izolacja spadkowa stropodachów) — zrygask z okładzinami
- Izolacja przeciwwilgociowa i przeciwradowana: membrana SBS 4 mm na płycie fundamentowej — linia bardzo gruba
- Membrana dachowa TPO 1,5 mm, mocowana mechanicznie (hydroizolacja stropodachów); Hydroizolacja 2 x papa SBS (podkładowa + wierzchnia krycia, dach zielony) — pas czarno-biały
- Szyroplan grafitowy EPS 031 (ETICS, NRO w systemie); Szyroplan podłogowy EPS 100-038 (pod jaskrychem); Szyroplan elastyczny EPS T (akustyczny, pod jaskrychem) — zrygask „V”/”
- Polistyren ekstrudowany XPS 300 (pod płytą fundamentową, cokoł, izolacja obwodowa) — zrygask podkowy
- Jaskrychemy cementowe CT-C25-F5 z węzłownicą ogrzewania podłogowego — kropki
- Membrana fasadowa wiatroizolacyjna UV-stabilna, czarna (sd = 0,02 m)
- Błoczek wapniowo-piaskowy 12 cm, kl. 15 (ściana działowa, lico w klatce); Błoczek wapniowo-piaskowy (silikat) 18 cm, kl. 20, gr. 1, na zaprawie cienkowarstwowej — kratka ukośna 45°/135°
- Paroizolacja bitumiczna z wkładką Al (na płycie stropodachów) — linia kreskowa cienka 3/1 po ciepłej stronie
- Podsyłka piaskowa zagęszczona (l, s ≥ 0,98)
- Płyta gipsowo-kartonowa 12,5 mm (GKB / GKB1 w łazienkach); Podsyłka zewnętrzna: płyta włóknocementowa 12 mm na ruszcie, RAL 7016
- Opórki blacharskie (blacha powlekana); Stalarka — profile aluminiowe, antrycyt; Rama boksu C: ruszt stalowy ocynkowany w okładzinie z blachy aluminiowej RAL 7016 (pusta w środku); Stal malowana proszkowo (balustrady, rylce) — zacementowanie
- Szkoło (szyby zespolone); Ścianka szklana VSG 2 x 8 mm w ramie aluminiowej (wiatrak / hol)
- Zelbet C25/30, B500SP (stropy, płyta fundamentowa, ściany); Zelbet C30/37 XC4/XF1 (krawędzie płyt wysuniętych, atyki, belki) — 45° na przemięcie cięgieł i przerywane
- Podbudowa nawierzchni (kruszywo)

OBJAŚNIENIA I UWAGI


- Wymiary w cm (mm w indeksie górnym, np. 24" = 24,5 cm), rzędne w m względem ±0,000 = 101,650 m n.p.m. (PL-EVRF-2007-144).
- Rzędne: trójką zaznaczony — poziom wykonczenia, niezaznaczony — konstrukcji, w połowie zaznaczony — poziom ±0,000 z rzędnią bezwzględna (PN-B-01025).
- Wysokość budynku wg § 6 WT: od terenu przy najniższym wejściu (-0,348) do wierzchu stropodachu D1 (+9,626) — H = 9,97 m (bez atyki).
- Opisy warstw: kod i nazwa przegrody z modelu, materiały i grubości wg modelu (od góry / od lewej).
- Przekrój A-A: opisy warstw pominięte na rysunku (brak miejsca w podziałce 1:50); POD-0, STROP ST2 + POD-1 — układ warstw wg zestawienia przegrod w części opisowej / przekroju 1:50.
- Przekrój B-B: opisy warstw pominięte na rysunku (brak miejsca w podziałce 1:50); STROP ST2Z + POD-1, SD1, OK1 — układ warstw wg zestawienia przegrod w części opisowej / przekroju 1:50.
- Rysunek wygenerowany automatycznie z modelu model/budynk.yam1 (wersja 1.0, 2026-09-25) — generator lamela.views.

REW. OPIS ZMIANY		DATA		
0) Wydanie — rysunek wygenerowany z modelu		2026-09-25		
PRACOWNIA PROJEKTOWA		STADIUM PB	BRANŻA ARCHITEKTURA (AR)	
PRACOWNIA PROJEKTOWA — nazwa do uzupełnienia				
adres pracowni do uzupełnienia				
INWESTOR				
(do uzupełnienia)				
OBJEKT / NAZWA ZAMIERZENIA BUDOWLANEGO				
Budynek mieszkalny jednorodzinny wolnostojący „Dom LAMELA”				
ADRES / LOKALIZACJA (NR DZIAŁKI, OBRĘB, JEDN. EWIDENCYJNA)			KAT. OBJEKTU I	
ul. Lipowa (fikcyjna), dz. nr ewid. 1234, obręb 0005 Przykładowo, gm. Przykładowo (fikcyjna)				
FUNKCJA	IMIĘ I NAZWISKO	SPECJALNOŚĆ, NR UPRAWNIENI	DATA	PODPIS
Projektant	[DO UZUPEŁNIENIA]	[DO UZUPEŁNIENIA]		
Projektant (wsp.)	[DO UZUPEŁNIENIA]	[DO UZUPEŁNIENIA]		
Sprawdzający	nie dotyczy (art. 20 ust. 3 pkt 2 PB)	—		
Opracował	[DO UZUPEŁNIENIA]	[DO UZUPEŁNIENIA]		
TYTUŁ RYSUNKU				
PRZĘKROJE A-A I B-B				
SKALA 1:50	FORMAT 1130x420	DATA WYDANIA 2026-09-25	RODZAJ DOK. przekrój	NR RYSUNKU PB-AR-04
			ARKUSZ 4/5	REW. 0


odcinek kordonu 100 mm (wygląda 1:1)

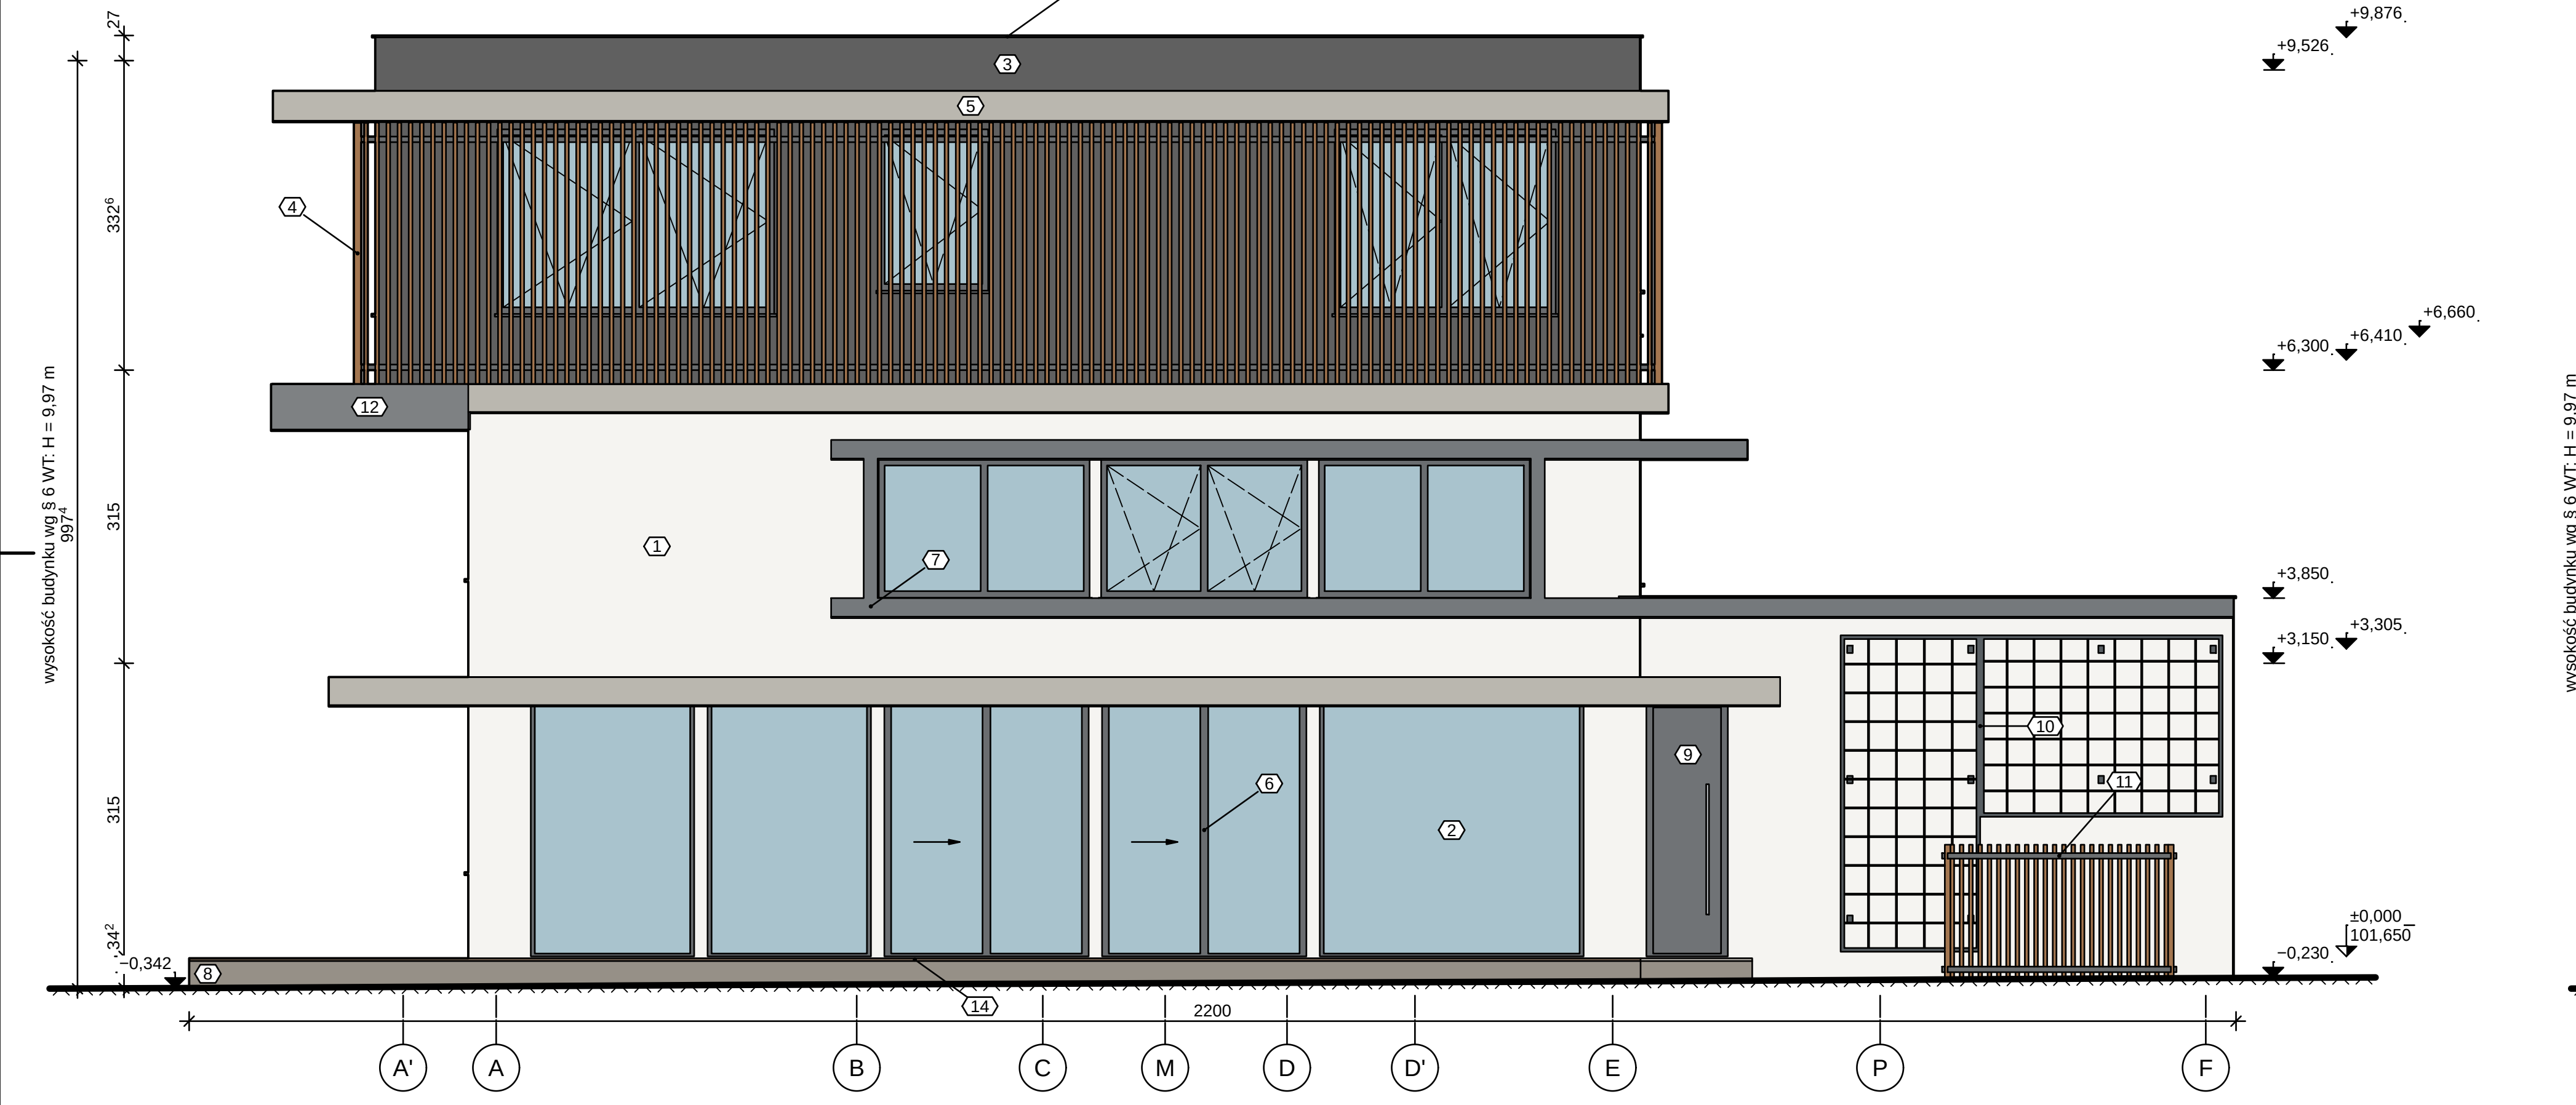


ELEWACJA POŁUDNIOWA (OGRODOWA) 1:50

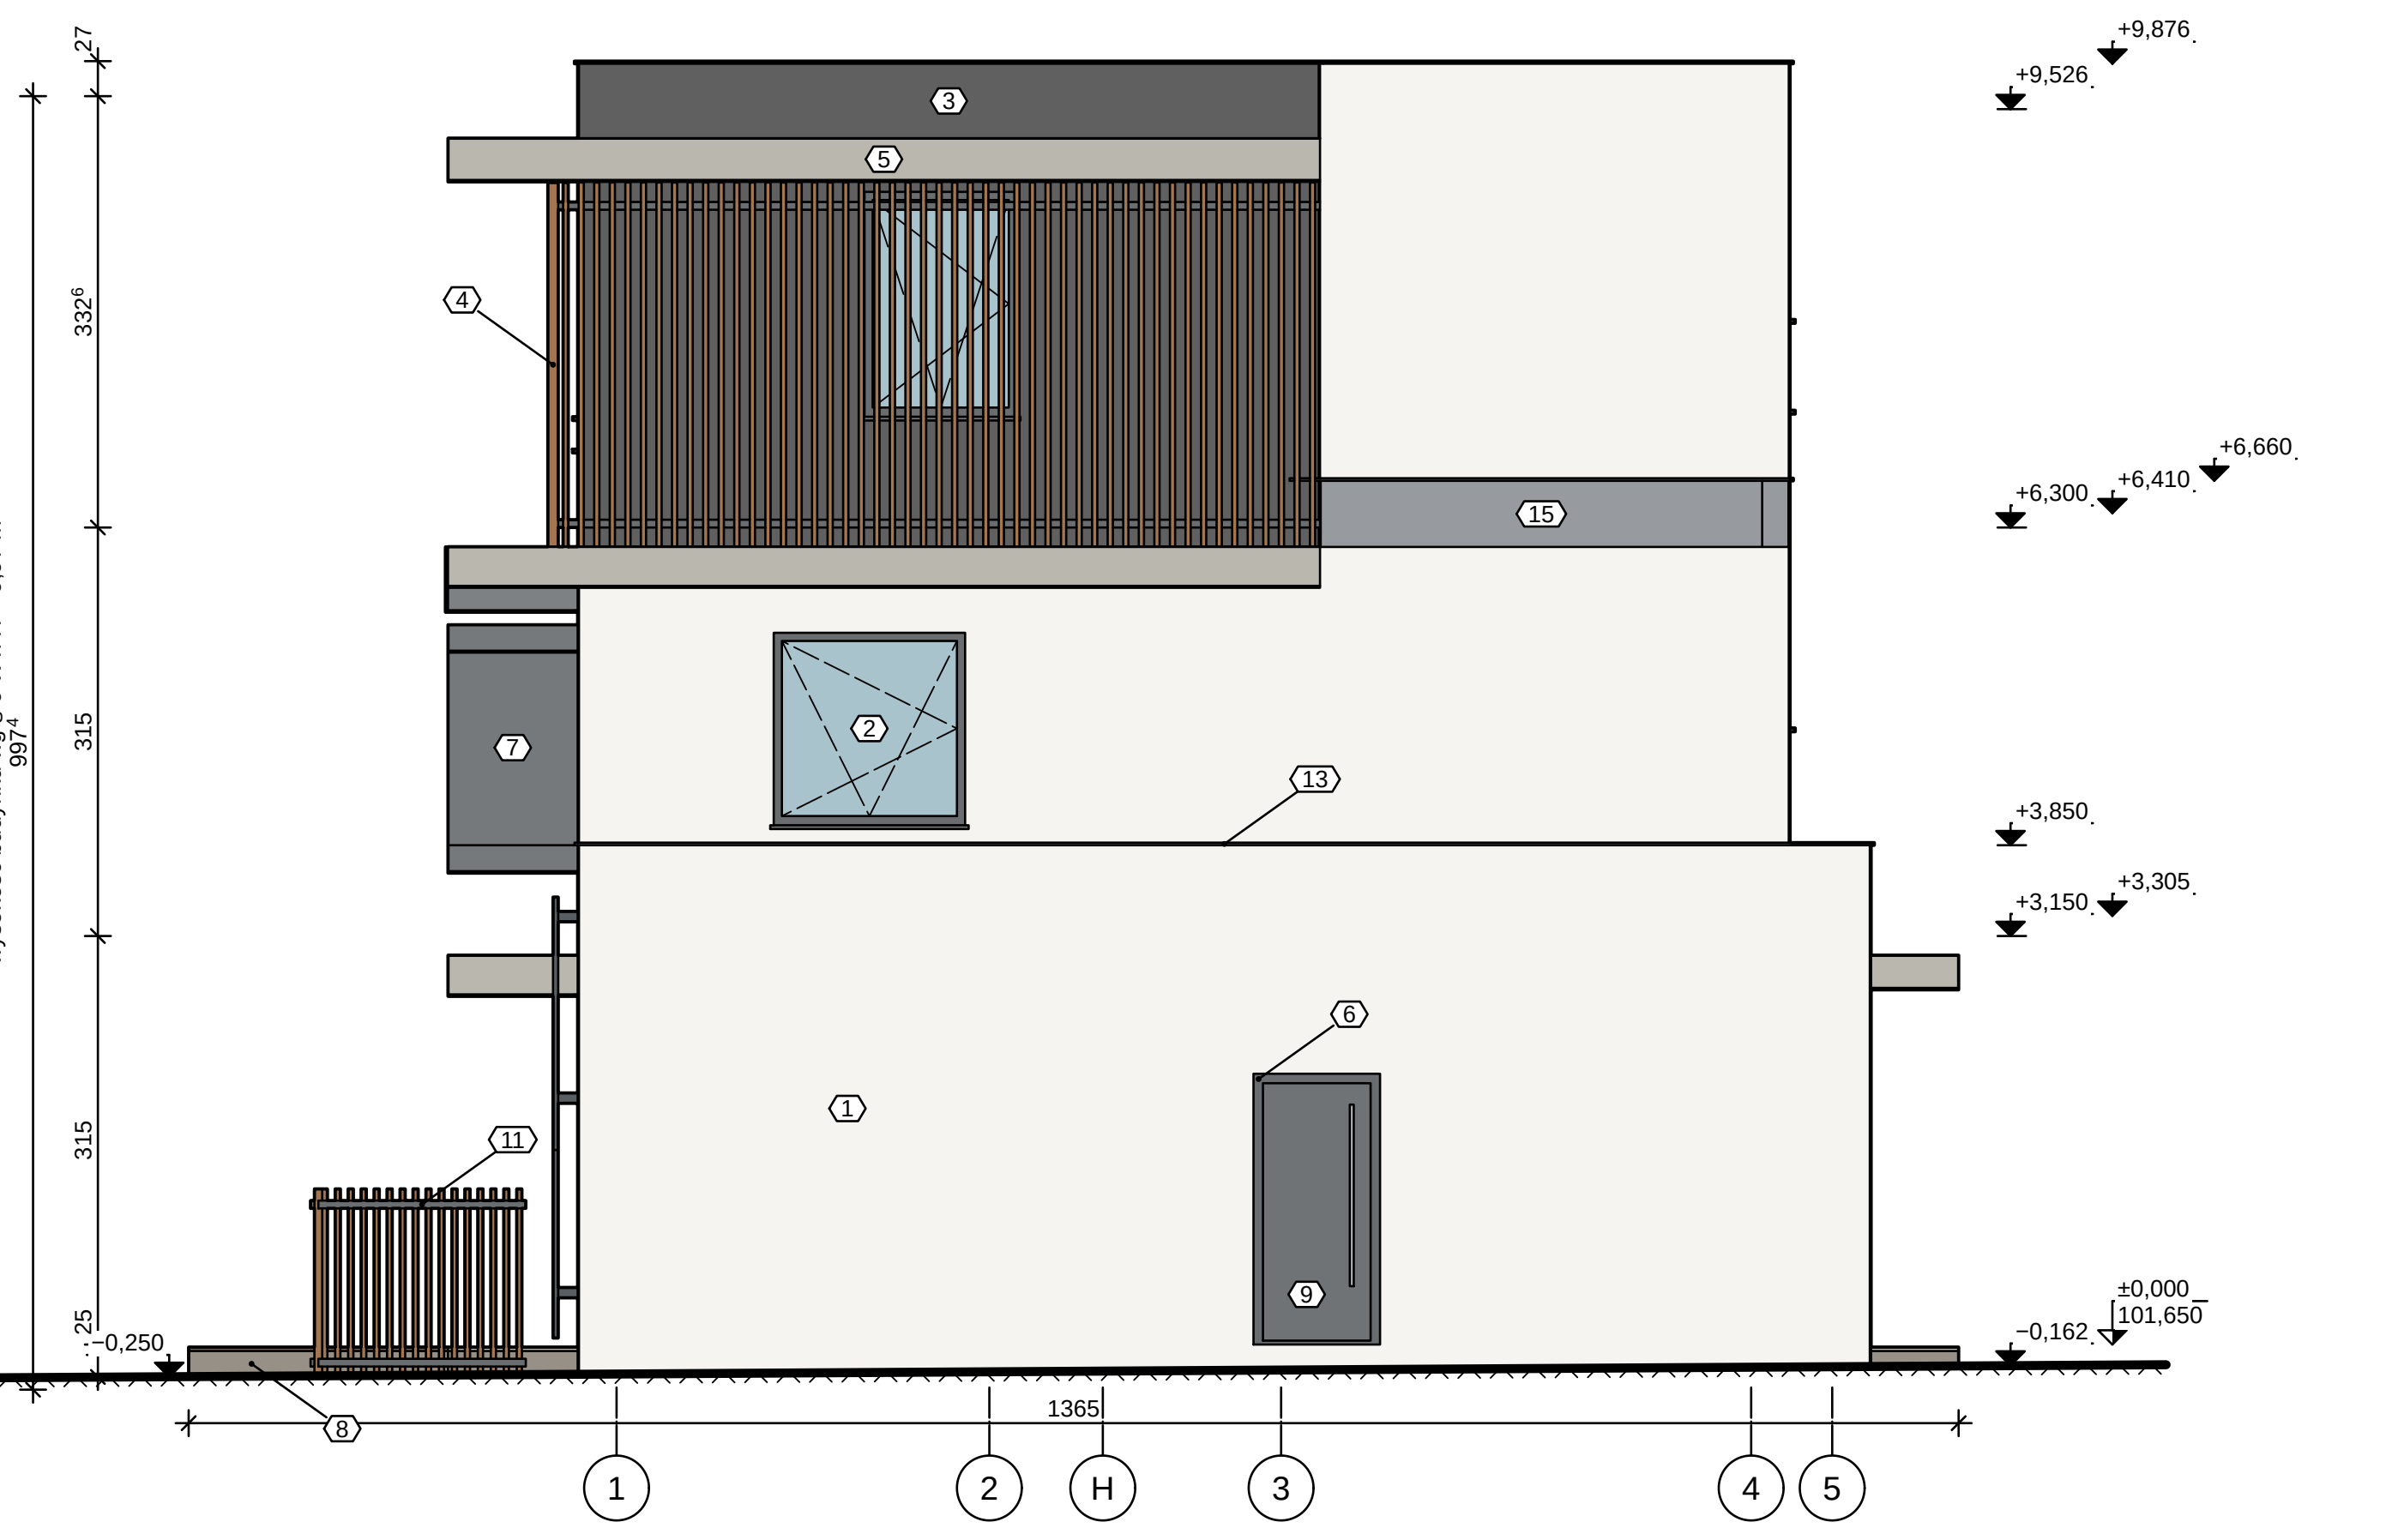

ELEWACJA WSCHODNIA 1:50

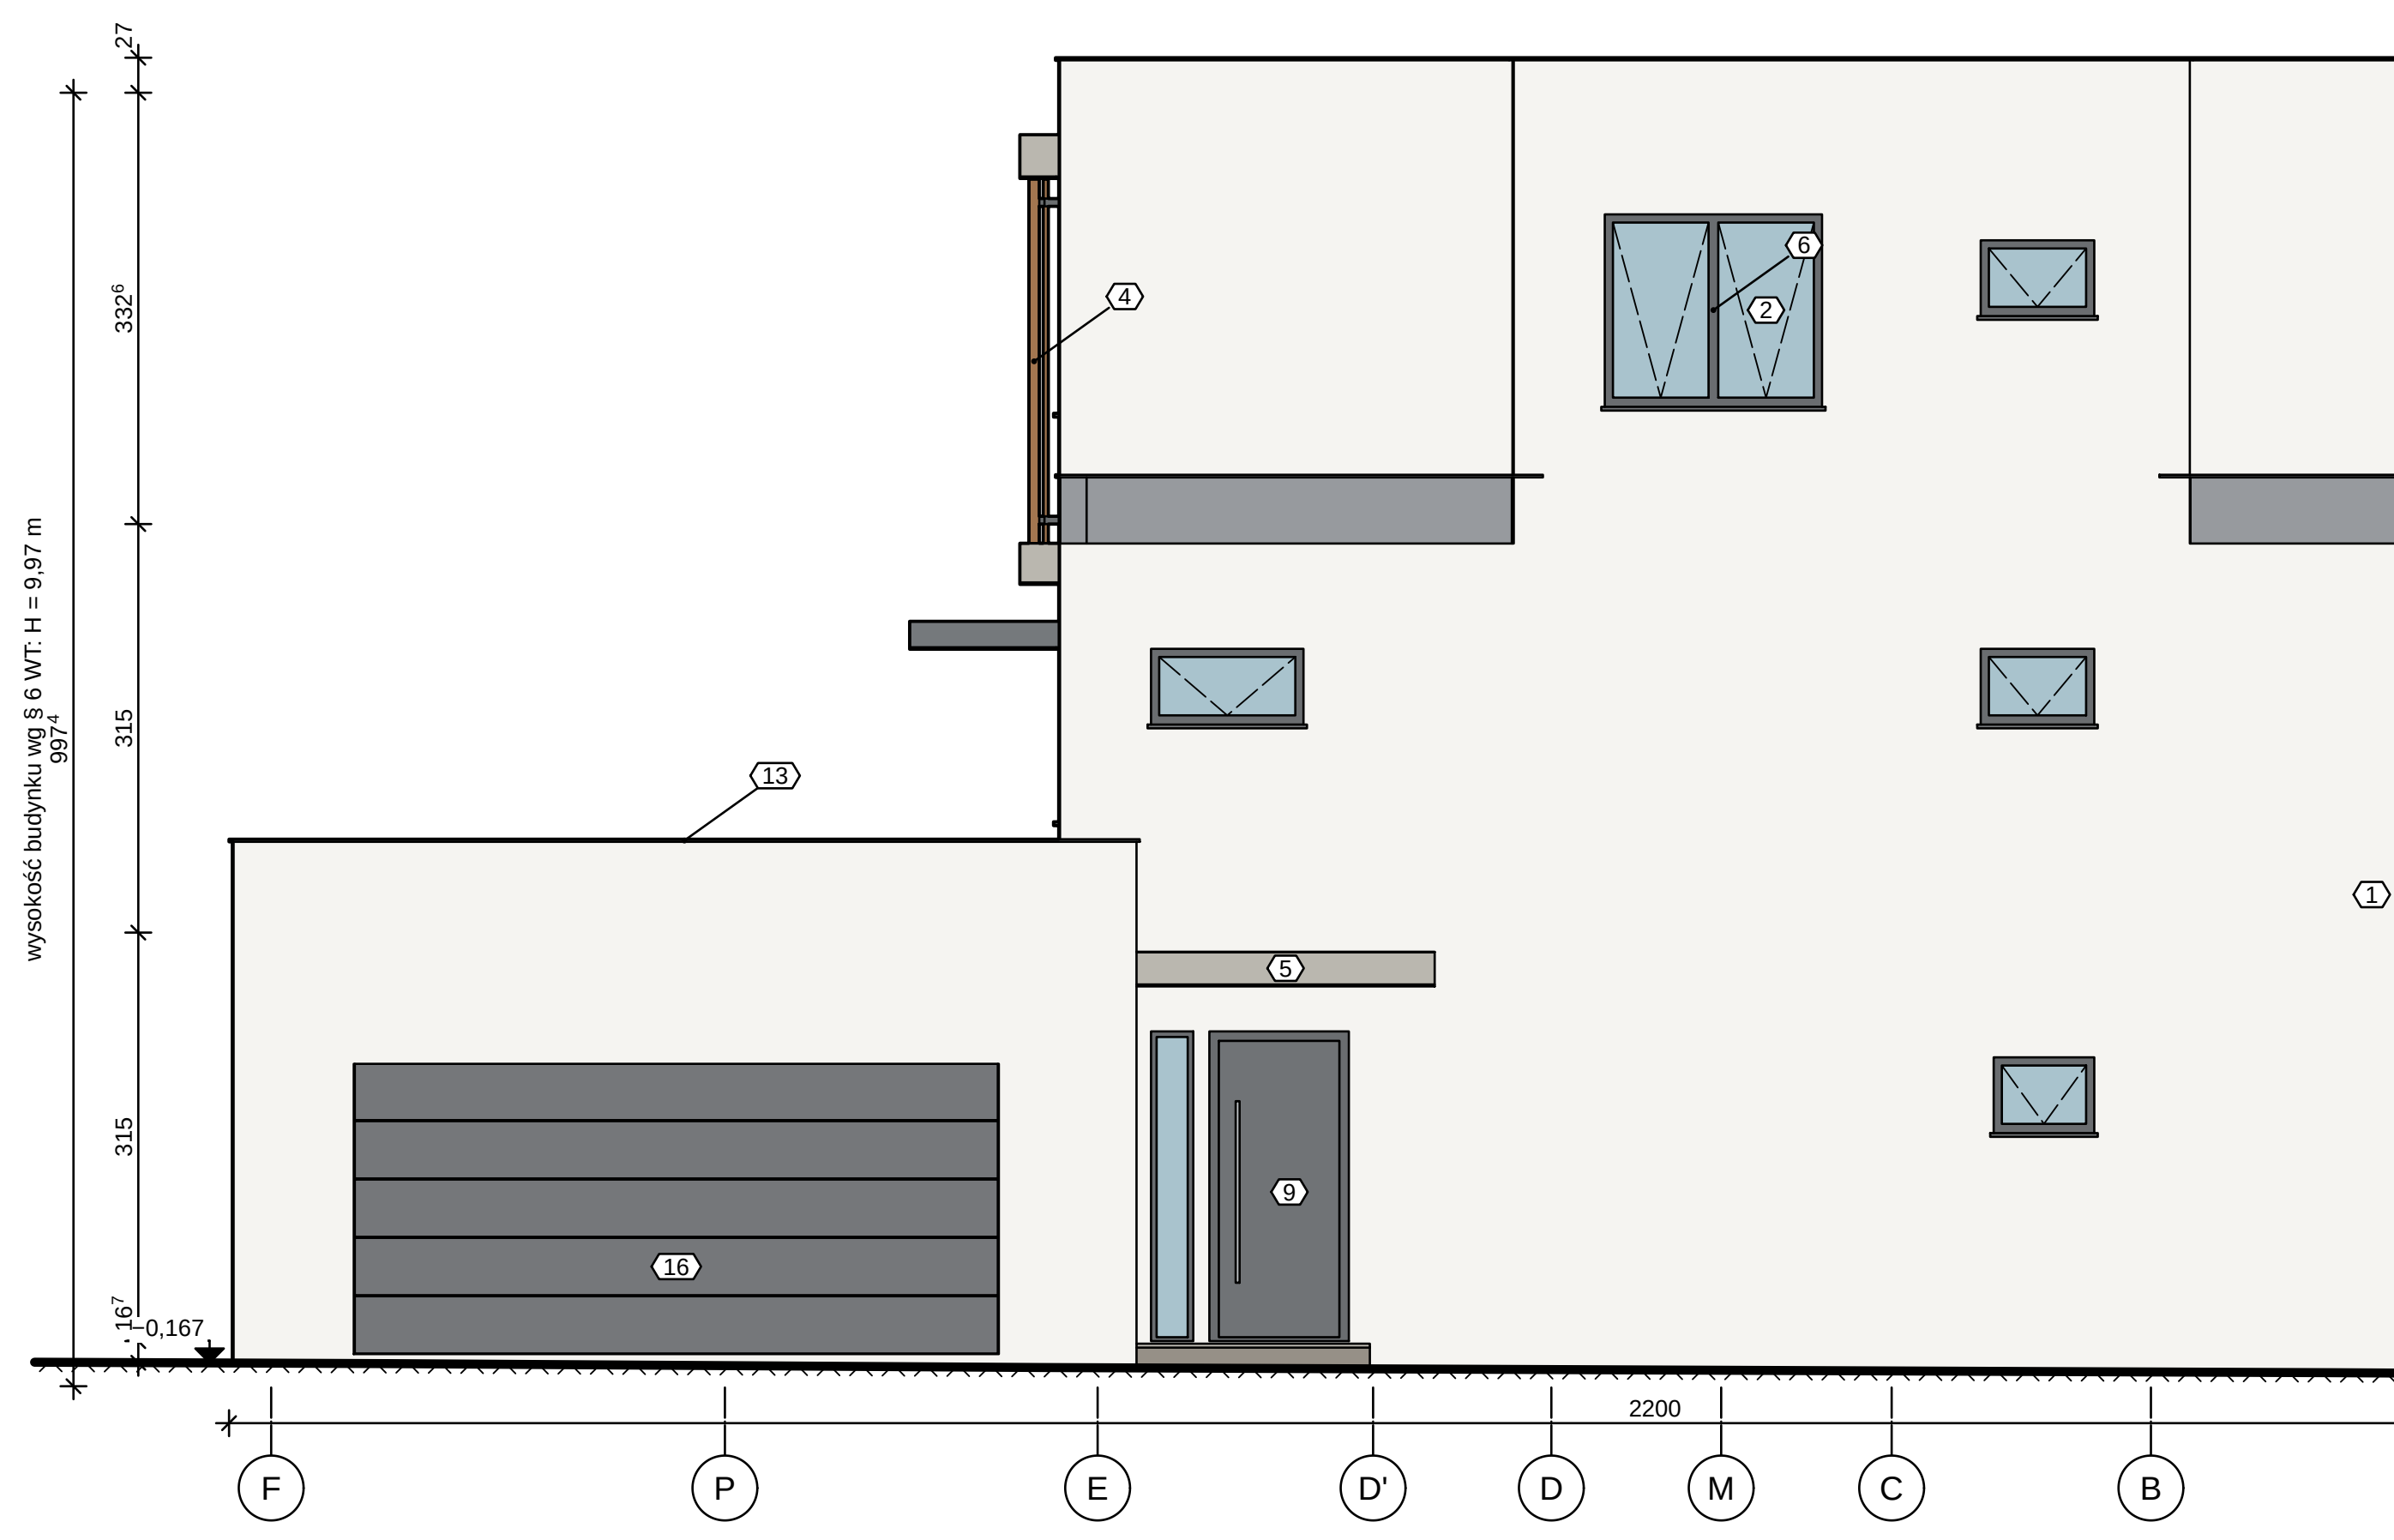

ELEWACJA PÓŁNOCNA (OD ULICY) 1:50

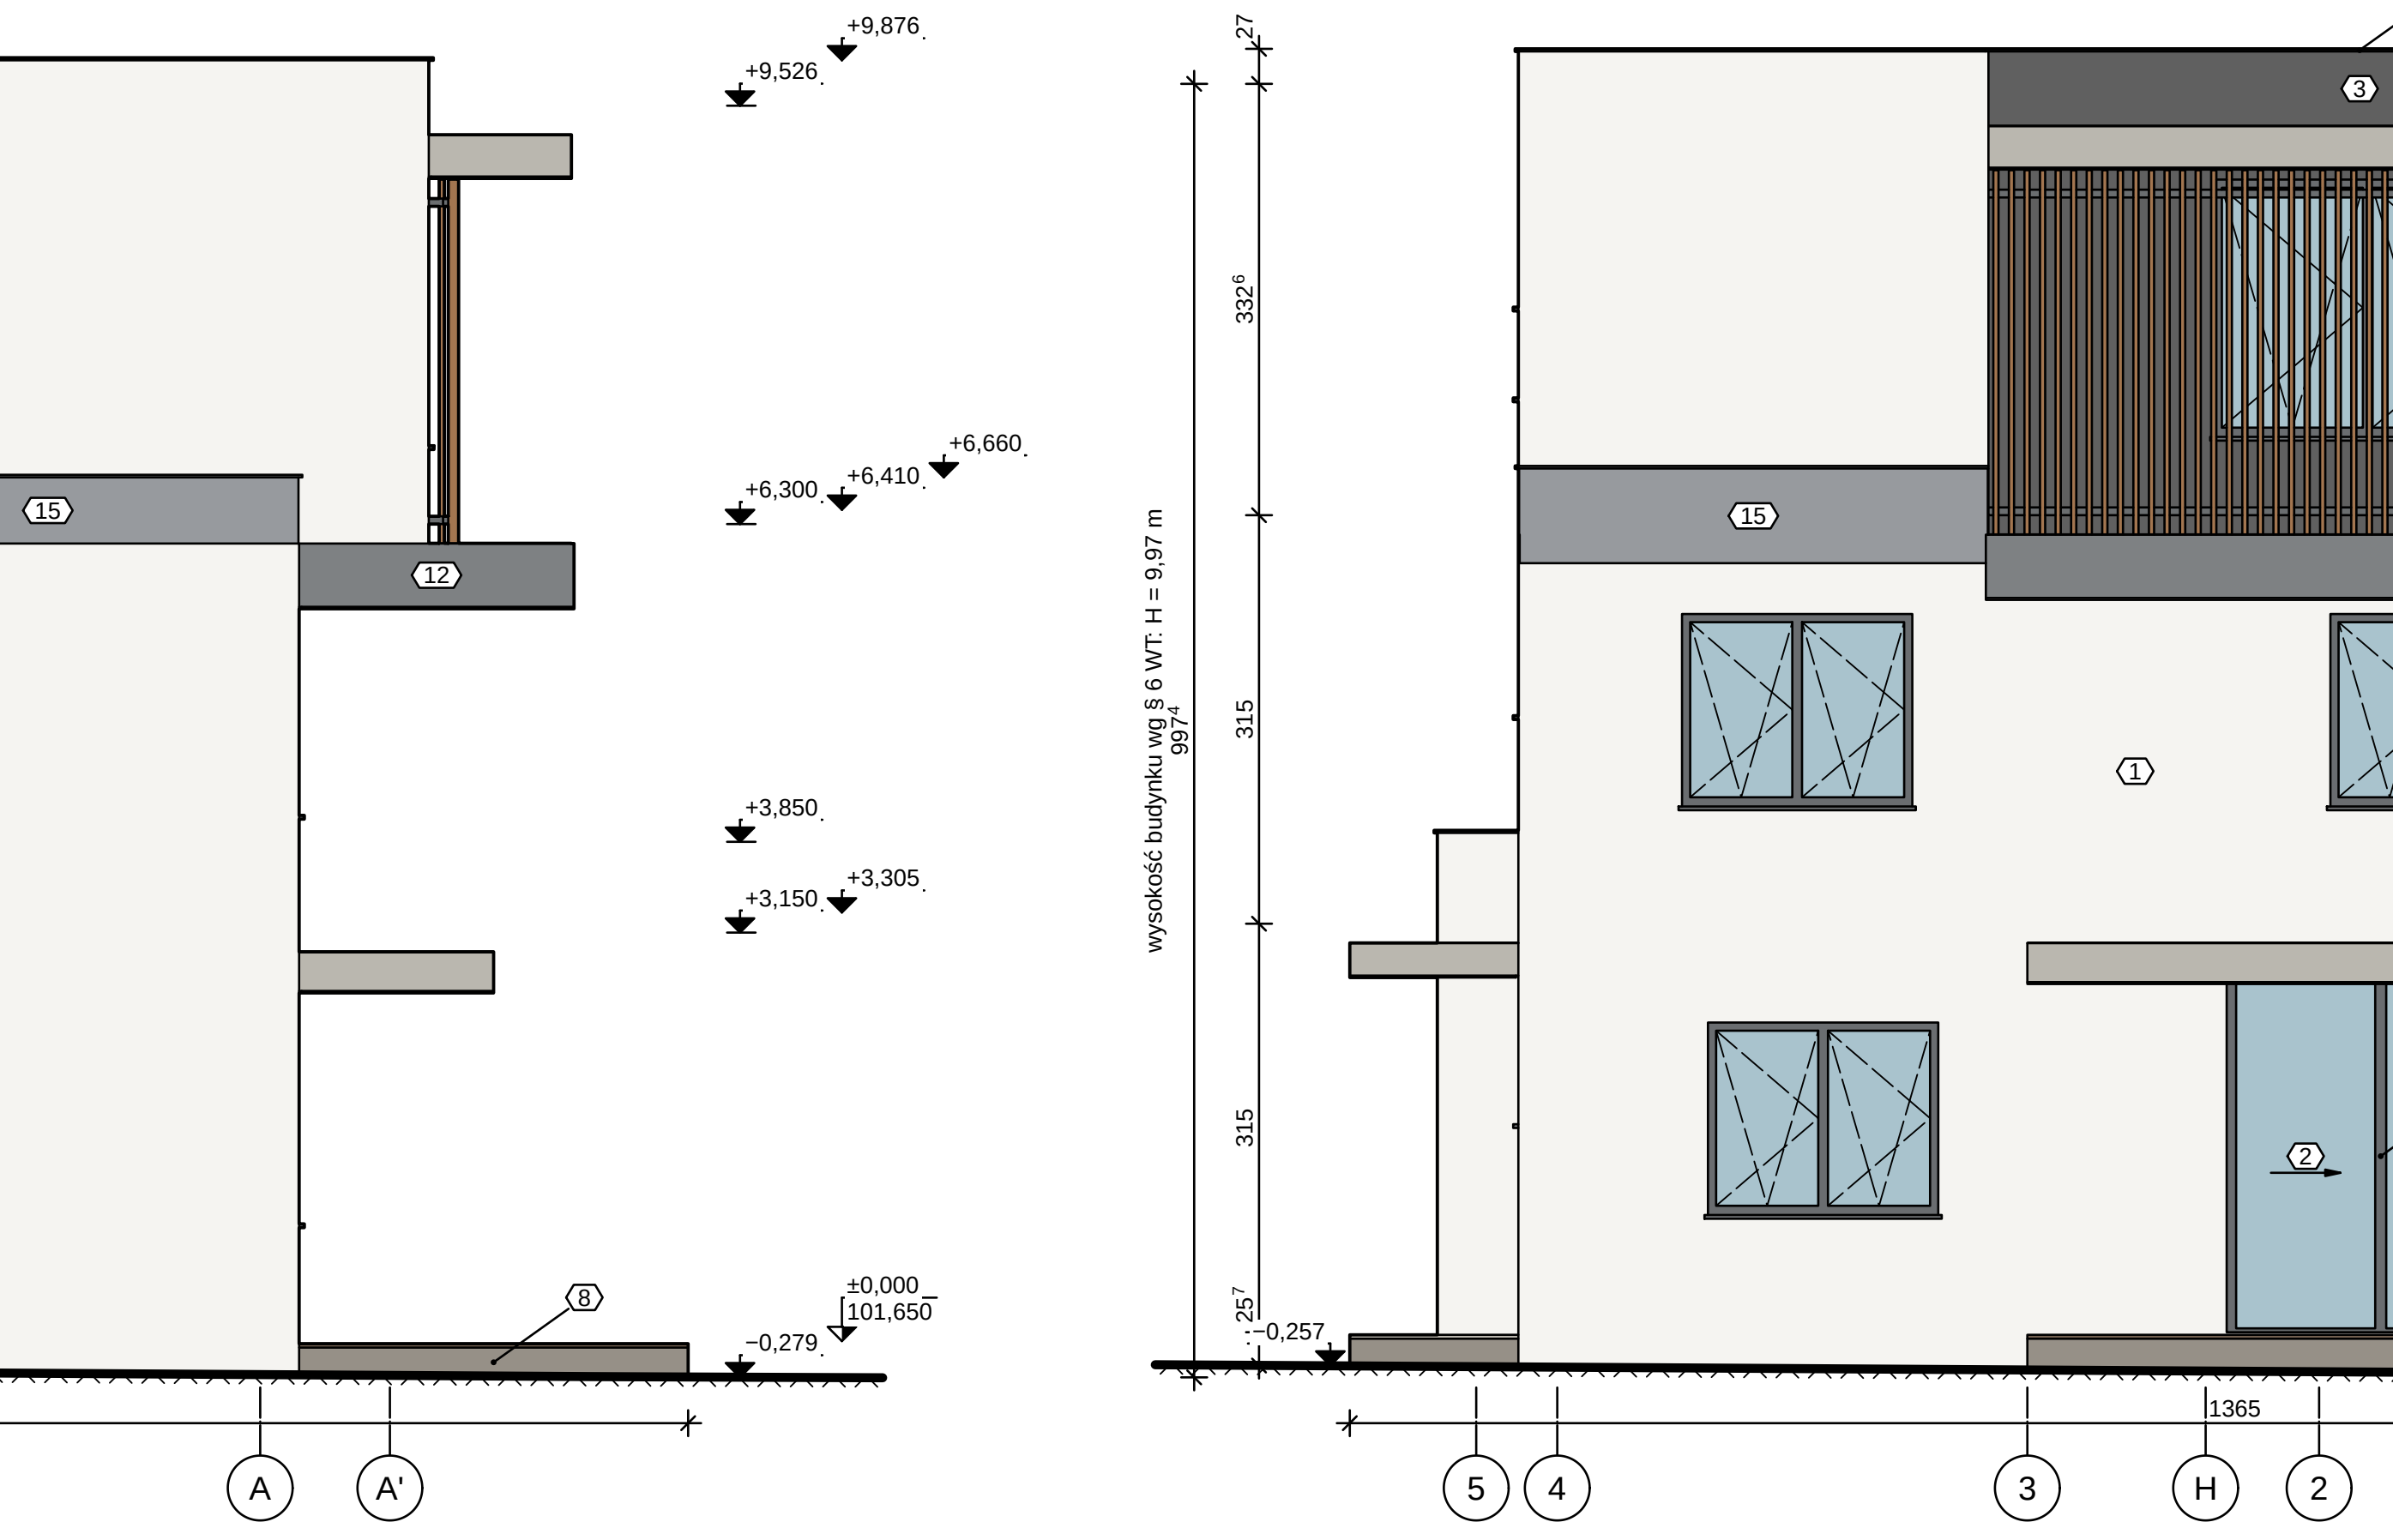

ELEWACJA ZACHODNIA 1:50

KOLORYSTYKA I MATERIAŁY ELEWACJI

1

ETICS: warstwa zbrojona + tynk silikonowy 1,5 mm (biały) / jasnoszary NCS S 1500-N [TYNK_SIL]

#5f4b0

2

Szkoło (szyby zespolone) [SZKŁO]

#a9c3cd

3

Membrana fasadowa wiatroizolacyjna UV-stabilna, czarna (sd = 0,02 m) [MEMB_WIATR]

#1d1d1d

4

Lamele elewacyjne 40x80 mm, drewno termojest (klasa 1 trwałości), olejowane [DREWNO_TERMO]

#6b6b41

5

Żelbet C30/37 XC4XF1 (krawędzie płyt wysuniętych, atyki, belki) [ZB_C30]

#b4b4a9

6

Stołarka — profile aluminiowe, antracyt [RAMA_ALU]

#2b2b33

7

Rama boku C: ruszt stalowy ocynkowany w okładzinie z blachy aluminiowej RAL 7016 (pusta w środku) [RAMA_C]

#3b4044

8

Podbudowa nawierzchni (rusztywo) [NAW_PODBUDOWA]

#8b877d

9

Drzwi zewnętrzne, płycina aluminiowa [DRZWI_ZEWNI]

#34383c

10

Stal S235 ocynkowana ogniotrwała, malowana proszkowo RAL 7016 — kratownica pręcy (pręty Ø12 w siatce 0,30 m; rama 40x40) [STAL_OCYNK]

#4a5055

11

Stal malowana proszkowo (balustrady, rylce) [STAL_BAL]

#2c3034

12

Podsiufka zewnętrzna: płyta włóknocementowa 12 mm na ruszcie, RAL 7016 [PODSUF]

#474b4f

13

Obróbki blacharskie (blacha powlekana) [OBRÓBKA_BLACH]

#3b3b43

14

Deska tarasowa [NAW_DESKA]

#6d5b47

15

Styropian grafitowy EPS 031 (ETICS, NRO w systemie) [EPS031]

#8f9296

16

Brama garażowa segmentowa [BRAMA_GAR]

#3a3a42

OBJAŚNIENIA I UWAGI

1. Wymiary w cm (mm w indeksie górnym, np. 24" = 24,5 cm), rzędne w m względem s0,000 = 101,650 m n.p.m. (PL-EVRP2007-NH).

2. Rzędne: rdz. i rdz. zaczerpnięty — poziom wykończenia, niezaczerpnięty — kopiec, w pobliżu zaczerpnięty — poziom s0,000 z rzędnej bezwzględnej (PN-B-01025).

3. Wysokość budynku wg § 6 WT: od terenu przy najniższym poziomym wejściu (-0,348) do wierzchu stropodachu D1 (+9,826) — H = 9,97 m (bez atyki).

4. Kolorystyka orientacyjna wg kolorów materiałów w modelu (do potwierdzenia wzorem RAL/NCSS).

5. Rysunek wygenerowany automatycznie z modelu model/budynki/yaml (wersja 1.0, 2026-09-25) — generatory lamela views.

1 0 1 2 3 4 5 m

PODZIAŁKA 1:50

REW.	OPIS ZMIANY	DATA
0	Wydanie — rysunek wygenerowany z modelu	2026-09-25
PRACOWNIA PROJEKTOWA — nazwa do uzupełnienia		PB ARCHITEKTURA (AR)
adres pracowni do uzupełnienia		
INWESTOR (do uzupełnienia)		
OBIEKT / NAZWA ZAMIERZENIA BUDOWLANEGO		
Budynek mieszkalny jednorodzinny wolnostojący „Dom LAMELA”		
ADRES / LOKALIZACJA (NR DZIAŁKI, OBREB, JEDN. EWIDENCYJNA)		KAT. OBIEKTU
ul. Lipowa (fikcyjna), dz. nr ewid. 123/4, obręb 0005 Przykładowo, gm. Przykładowo (fikcyjna)		I
FUNKCJA	IMIĘ I NAZWISKO	SPECJALNOŚĆ, NR UPRAWNIEN
Projektant	[DO UZUPEŁNIENIA]	[DO UZUPEŁNIENIA]
Projektant (wsp.)	[DO UZUPEŁNIENIA]	[DO UZUPEŁNIENIA]
Sprawdzający	nie dotyczy (art. 20 ust. 3 pkt 2 PB)	—
Opracował	[DO UZUPEŁNIENIA]	[DO UZUPEŁNIENIA]
TYTUŁ RYSUNKU		
ELEWACJE		
SKALA	FORMAT	DATA WYDANIA
1:50	2050x297	2026-09-25
RODZAJ DOK.	NR RYSUNKU	ARKUSZ
elewacja	PB-AR-05	5/5
REW.	0	

nrst. 2050-297