


MAPA DO CELÓW PROJEKTOWYCH — PODKŁAD PRZYKŁADOWY

PODKŁAD PRZYKŁADOWY — mapa do celów projektowych fikcyjna [DANE PRZYKŁADOWE – FIKCYJNE], narysowana z modelu działki (działka.yaml); w projekcie rzeczywistym — aktualna mapa do celów projektowych wg art. 34 ust. 3 pkt 1 PB (z klauzulą urzędową lub oświadczeniem geodety — art. 34b PB), treść i opis mapy wg § 32–33 rozp. w sprawie standardów technicznych (t.j. Dz.U. 2022 poz. 1670), znaki wg zał. 4 rozp. w sprawie BDOT500 i mapy zasadniczej (Dz.U. 2021 poz. 1385; oba akty zweryfikowane w ELI 25.09.2026 — status: obowiązujące).

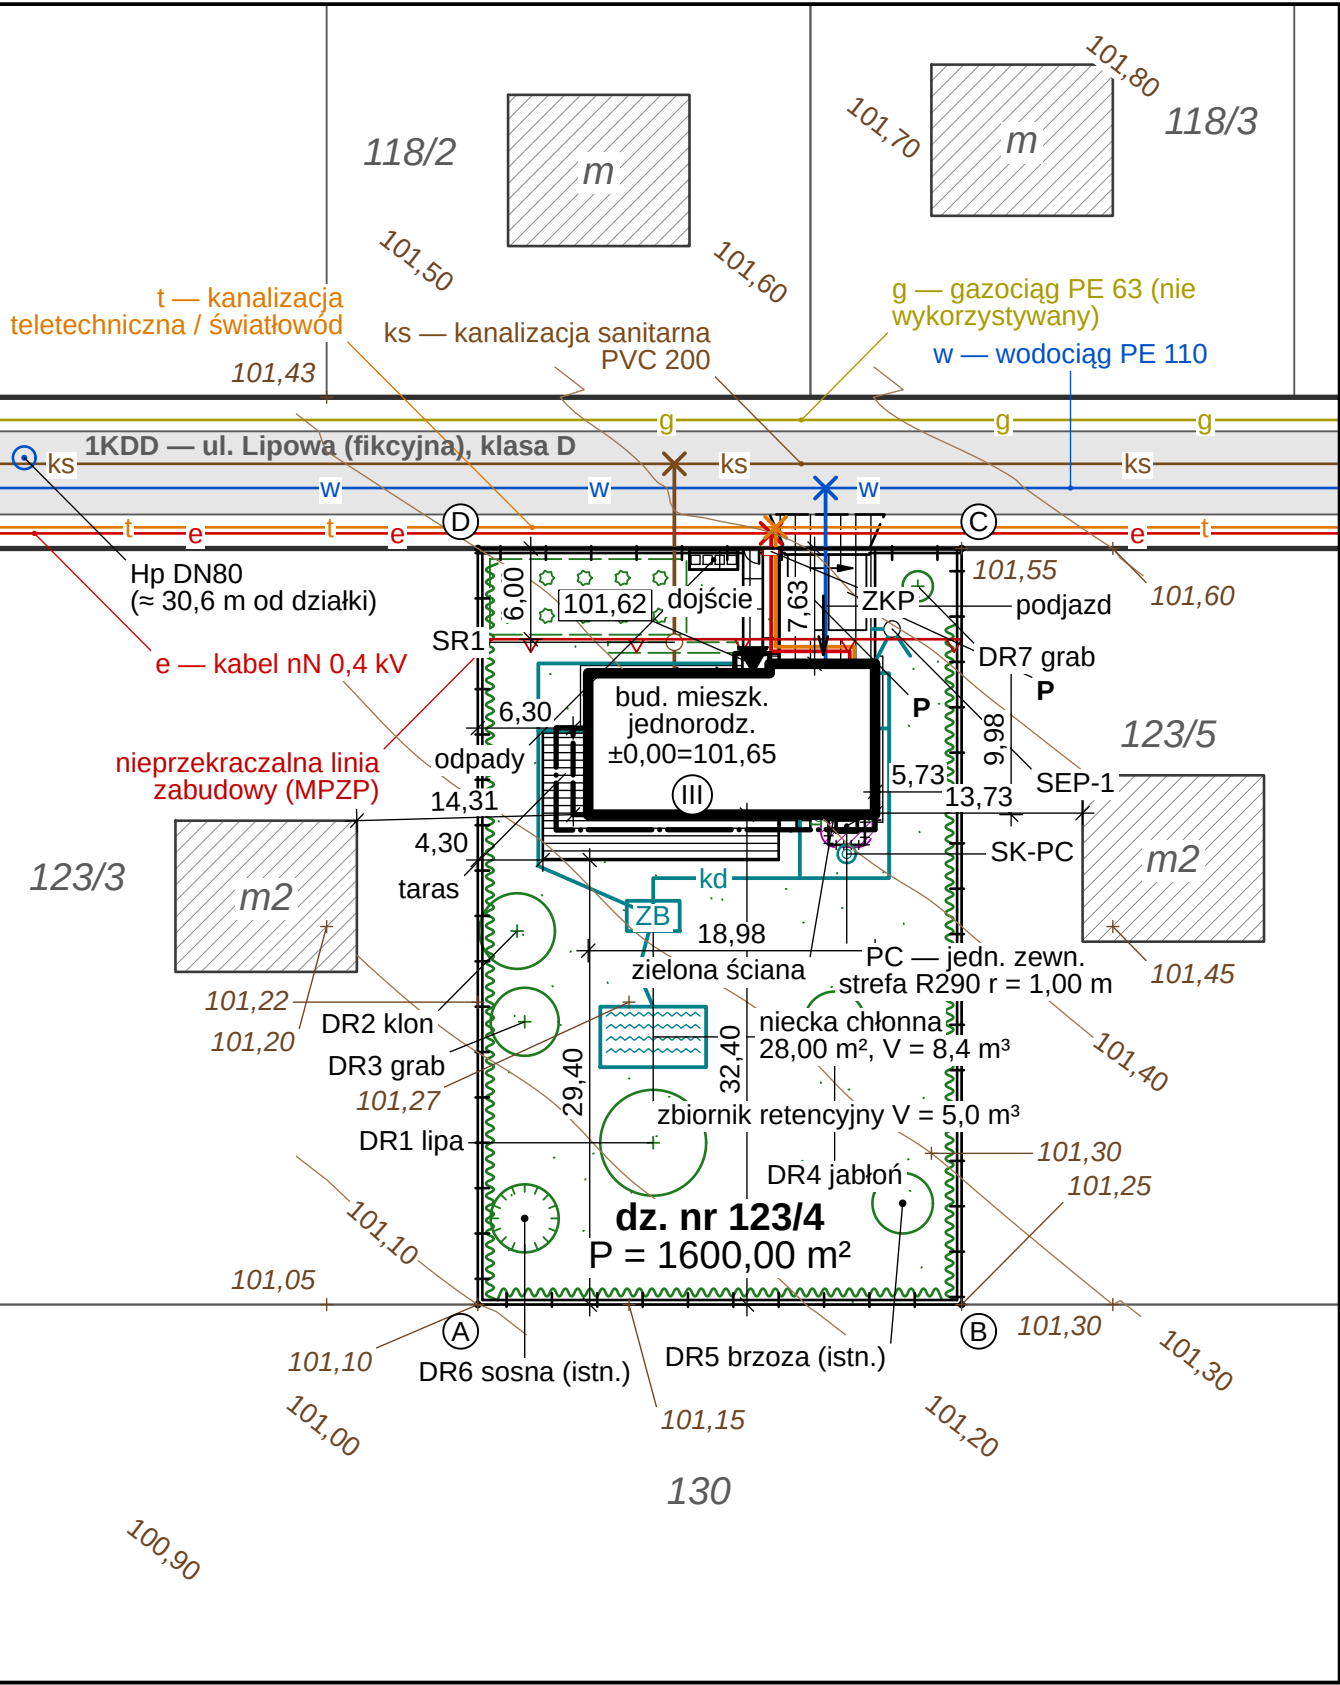

PLAN ZAGOSPODAROWANIA DZIAŁKI 1:500

OBJAŚNIENIA I UWAGI

- Wymiary i odległości w m (dokładność 0,01 m), rzędne w m n.p.m. (PL-EVRF2007-NH).
- Układ współrzędnych: lokalny układ działki (x – wschód, y – północ, początek w narożniku A); w projekcie rzeczywistym — układ PL-2000 strefa 6 z mapy do celów projektowych.
- Obrys budynku — lico zewnętrzne ścian parteru na wys. 1,0 m nad terenem; wspornik bryły A (II piętro) — obrys wyższych kondygnacji; płyty wspornikowe, okapy i daszek — przewieszenia (PN-B-01027 poz. 1.6).
- Wody opadowe zagospodarowane w granicach działki: rury spustowe → kolektory KD → zbiornik retencyjny szczelny → przelew do niecki chłonnej; odwodnienie liniowe przed bramą — brak spływu na drogę (MPZP; u.d.p. art. 39 ust. 1 pkt 9; WT § 28–29).
- Wymiary i rzędne szczegółowe — rys. PZT-02; uzbrojenie i koordynacja sieci — rys. PZT-03.
- Zjazd z drogi 1KDD pokazano jako przedłużenie bramy do krawędzi jezdni — geometria zastępca [DO UZUPEŁNIENIA]; szerokość, skosy/luki, nawierzchnia i przepust wg zezwolenia zarządcy drogi (u.d.p. art. 29 ust. 3a).
- Braki danych modelu (9 poz.) oznaczono [DO UZUPEŁNIENIA]; wykaz: projekt/02\_PZT/BRANKI\_DANYCH.md.
- Rysunek wygenerowany automatycznie z modelu model/budynek.yaml (wersja 1.0, 2026-09-25) — generatory lamela.views.

ZESTAWIENIE POWIERZCHNI I WSKAŹNIKÓW ZAGOSPODAROWANIA (RPB § 14 pkt 4, MPZP)

| Wskaźnik / element                 | Projekt                         | MPZP / wymaganie                             | Zgodność |
|------------------------------------|---------------------------------|----------------------------------------------|----------|
| Powierzchnia działki nr 123/4      | 1600,00 m <sup>2</sup>          | —                                            |          |
| Pow. zabudowy (upzp art. 2 pkt 35) | 187,50 m <sup>2</sup>           | ≤ 480,00 m <sup>2</sup>                      | TAK      |
| Udział pow. zabudowy               | 11,72%                          | ≤ 30%                                        | TAK      |
| – z płytami i okapami (kontrolnie) | 218,08 m <sup>2</sup> (13,63%)  | informacyjnie                                | TAK      |
| Drogi, dojścia, place              | 64,87 m <sup>2</sup>            | —                                            |          |
| Taraszy naziemne, podesty          | 66,62 m <sup>2</sup>            | —                                            |          |
| Opaska zwirowa                     | 13,38 m <sup>2</sup>            | —                                            |          |
| PBC (upzp art. 2 pkt 28)           | 1270,23 m <sup>2</sup> (79,39%) | ≥ 800,00 m <sup>2</sup> (50%)                | TAK      |
| – z 50 % dachu ziel. D4 (rezerwa)  | 1299,76 m <sup>2</sup> (81,24%) | informacyjnie                                |          |
| Pow. kondygnacji nadz. (P0+P1+P2)  | 396,39 m <sup>2</sup>           | 80,00 m <sup>2</sup> –1280,00 m <sup>2</sup> | TAK      |
| Nadziemna intensywność zabudowy    | 0,248                           | 0,05–0,80                                    | TAK      |
| Wysokość zabudowy (art. 2 pkt 30)  | 10,47 m                         | ≤ 11,00 m                                    | TAK      |
| Wysokość budynku (WT § 6)          | 9,97 m                          | N: ≤ 12,00 m                                 | TAK      |
| Kondygnacje nadziemne              | 3                               | ≤ 3                                          | TAK      |
| Miejsca postojowe (garaż + zewn.)  | 2 + 2                           | ≥ 2                                          | TAK      |
| Dach — kąt nachylenia              | 1,1° (płaski)                   | płaski ≤ 12° lub 30–45°                      | TAK      |
| Lico ścian od linii zabudowy       | 1,63 m                          | nie przekraczać                              | TAK      |
| Elementy poza linią zabudowy       | brak                            | —                                            |          |

MPZP: uchwała nr XII/123/2024 Rady Gminy Przykładowo z 21.03.2024 — teren 3MN (fikcyjny). Limity: konfiguracja arkuszy (brief § 3) — BRAK W MODELU [DO UZUPEŁNIENIA]. Wartości z modułu lamela.wskazniki (jedyne źródło; definicje upzp art. 2 pkt 28–35, t.j. Dz.U. 2026 poz. 538): PBC bez nawierzchni ażurowych, opaski, pojemników i terenu nad zbiornikiem; dach zielony (≥ 10 m<sup>2</sup>) w 50 % — tylko rezerwa. Wysokość zabudowy = z\_top 111,85 (wyrzutnia wentylacji (dachowa, szczyt urządzenia)) – t\_śr 101,38 (t\_min 101,29, t\_max 101,48 na obwodzie rzutu ścian zewn.; w każdym punkcie niższa z rzędnych terenu istniejącego/projektowanego). WT § 6: od terenu przy wejściu O0-03 (101,30) do wierzchu stropodachu D1 (bez attyki) — grupa N.

ODLEGŁOŚCI OD GRANIC DZIAŁKI (WT § 12)

| Granica   | Element (płaszczyzna ściany) | Odł. [m] | Wymagana [m]       | Zgodność |
|-----------|------------------------------|----------|--------------------|----------|
| S (130)   | ściana P0 z otworami         | 32,40    | ≥ 4,00             | TAK      |
| S (130)   | T1 — okap/płyta/taras        | 29,40    | ≥ 1,50             | TAK      |
| E (123/5) | ściana P0 z otworami         | 5,73     | ≥ 4,00             | TAK      |
| E (123/5) | ściana P2 bez otworów        | 15,60    | ≥ 3,00             | TAK      |
| E (123/5) | PL-D — okap/płyta/taras      | 5,73     | ≥ 1,50             | TAK      |
| N (1KDD)  | ściana P0 z otworami         | 7,63     | nie dot. (ust. 10) | —        |
| N (1KDD)  | ściana P2 bez otworów        | 11,88    | nie dot. (ust. 10) | —        |
| N (1KDD)  | PL-DA — okap/płyta/taras     | 6,95     | nie dot. (ust. 10) | —        |
| W (123/3) | ściana P2 z otworami         | 6,30     | ≥ 4,00             | TAK      |
| W (123/3) | ściana P2 bez otworów        | 11,18    | ≥ 3,00             | TAK      |
| W (123/3) | T1 — okap/płyta/taras        | 4,30     | ≥ 1,50             | TAK      |



WT § 12 ust. 1: 4,00 m — ściana z oknami/drzwiami, 3,00 m — bez otworów (każda płaszczyzna ściany osobno); ust. 6: 1,50 m — okap, taras, daszek; ust. 10: od działki drogowej — nie dotyczy. Odległość w poziomie w miejscu najmniejszego oddalenia (§ 9). WT stosowane na podstawie art. 102a PB.

LEGENDA

|  |                                                                                                   |  |                                                                                                |
|--|---------------------------------------------------------------------------------------------------|--|------------------------------------------------------------------------------------------------|
|  | zasięg podkładu mapowego (mapa do celów projektowych — PRZYKŁADOWA)                               |  | brama przesuwna (poz. 2.9)                                                                     |
|  | granica działki budowlanej, punkt graniczny, narożnik (PN-B-01027 poz. 2.7)                       |  | furtka otwierana do wewnątrz działki (WT § 42)                                                 |
|  | linia rozgraniczająca drogi publicznej (PN-B-01027 poz. 2.5)                                      |  | jednostka zewn. pompy ciepła (fundament) i strefa czynnika R290                                |
|  | jezdnia drogi publicznej (wg mapy)                                                                |  | azurowa osłona z lamel jednostki PC (bez dachu, prześwit przy terenie)                         |
|  | budynek istniejący (mapa); m2 — mieszkalny, 2 kondygnacje                                         |  | zielona ściana — pnącza na kratownicy stalowej odsuniętej od elewacji (decyzja Inwestora K-13) |
|  | nieprzekraczalna linia zabudowy wg MPZP (PN-B-01027 poz. 2.2)                                     |  | zbiornik retencyjny szczelny (ZB)                                                              |
|  | budynek projektowany — obrys ścian parteru 1,0 m nad terenem (poz. 1.1)                           |  | niecka chłonna — ogród deszczowy (przelew zbiornika)                                           |
|  | obrys wyższych kondygnacji poza obrysem parteru (poz. 1.6 d)                                      |  | miejsce włączenia przyłącza do sieci (PN-B-01027 poz. 6)                                       |
|  | obrys płyt wspornikowych, okapów i daszku — przewieszenia (poz. 1.6 c)                            |  | złącze kablowo-pomiarowe ZKP (w linii ogrodzenia)                                              |
|  | ±0,00=101,65 — rzędna ±0,00 (posadzka parteru) w m n.p.m.; w kółku liczba kondygnacji nadziemnych |  | studzienka rewizyjna kanalizacji                                                               |
|  | wejście główne do budynku (poz. 1.7)                                                              |  | studnia chłonna skroplin pompy ciepła                                                          |
|  | wjazd do garażu                                                                                   |  | hydrant zewnętrzny na sieci (Hp)                                                               |
|  | zjazd z drogi publicznej — wg zezwolenia zarządcy drogi [DO UZUPEŁNIENIA]                         |  | warstwa terenu istniejącego (PN-B-01027 poz. 5.2)                                              |
|  | nawierzchnia z kostki betonowej (poz. 7.10)                                                       |  | rzędna terenu istniejącego [m n.p.m.]                                                          |
|  | nawierzchnia z płyt betonowych (poz. 7.11)                                                        |  | rzędna terenu projektowanego [m n.p.m.]                                                        |
|  | płyty w trawie (ażur) — poza PBC                                                                  |  | wymiar / odległość w m z dokładnością 0,01 m                                                   |
|  | taras naziemny — deska kompozytowa na legarach                                                    |  | w — sieć wodociągowa istniejąca (mapa)                                                         |
|  | opaska zwirowa 16/32 na geowłókninie                                                              |  | w — przyłącze wodociągowe projektowane                                                         |
|  | stanowisko postojowe 2,50 × 5,00 m (WT § 21)                                                      |  | ks — sieć kanalizacji sanitarnej istniejąca (mapa)                                             |
|  | osłona pojemników na odpady — segregacja (WT § 22)                                                |  | ks — przykanalik sanitarny projektowany                                                        |
|  | trawnik projektowany (poz. 7.8)                                                                   |  | kd — kanalizacja deszczowa projektowana (kolektory, przelew)                                   |
|  | rabata z krzewami                                                                                 |  | e — linia kablowa nN istniejąca (mapa)                                                         |
|  | żywoplot projektowany (poz. 7.6)                                                                  |  | e — kabel nN projektowany (ZKP → RG)                                                           |
|  | drzewo liściaste projektowane (poz. 7.1)                                                          |  | t — sieć telekomunikacyjna istniejąca (mapa)                                                   |
|  | drzewo istniejące — zachowane (poz. 7.2)                                                          |  | t — przyłącze telekomunikacyjne projektowane                                                   |
|  | ogrodzenie projektowane (poz. 2.8; na granicy — odsunięte graficznie)                             |  | g — sieć gazowa istniejąca (mapa)                                                              |

OBSZAR ODDZIAŁ YWANIA OBIEKTU (PB art. 3 pkt 20; RPB § 14 pkt 8)

Obszar oddziaływania obiektu mieści się w całości w granicach działki 123/4 (PB art. 3 pkt 20); odległości od granic ≥ 4,0 m (ściany z otworami ≥ 5,70 m, płyty ≥ 5,20 m), przesłanianie i nasłonecznienie sąsiednich budynków (≥ 8 m od granicy) bez ograniczeń (WT §13, §60), hałas PC ≤ 40 dB(A) nocą na granicy (W-024), wody opadowe zagospodarowane na działce (PW art. 234), brak odprowadzania na drogę. Podstawa ustalenia (RPB § 18 pkt 1); WT § 12, 13, 19, 23, 28–29, 60, 271 (art. 102a PB); u.d.p. art. 43; POŚ art. 144 ust. 2 i rozp. MŚ w sprawie dopuszczalnych poziomów hałasu (Dz.U. 2014 poz. 112); PW art. 234; ustalenia MPZP.

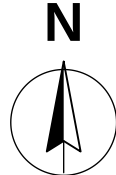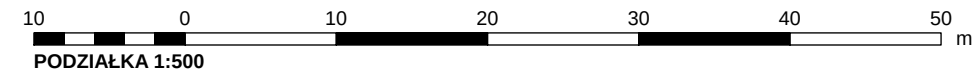

|   |                                         |                                   |
|---|-----------------------------------------|-----------------------------------|
| REW.   | OPIS ZMIANY                             | DATA                              |
| 0   | Wydanie — rysunek wygenerowany z modelu | 2026-09-25                        |
| PRACOWNIA PROJEKTOWA<br>PRACOWNIA PROJEKTOWA — nazwa do uzupełnienia<br>adres pracowni do uzupełnienia                                                      |                                         | STADIUM<br><b>PB</b>              |
| INWESTOR<br>(do uzupełnienia)   |                                         | BRANZA<br>ZAGOSPODAROWANIE TERENU |
| OBIEKT / NAZWA ZAMIERZENIA BUDOWLANEGO<br>Budynek mieszkalny jednorodzinny wolnostojący „Dom LAMELA” z zagospodarowaniem działki                            |                                         |                                   |
| ADRES / LOKALIZACJA (NR DZIAŁKI, OBRĘB, JEDN. EWIDENCYJNA)<br>ul. Lipowa (fikcyjna), dz. nr ewid. 123/4, obręb 0005 Przykładowo, gm. Przykładowo (fikcyjna) |                                         | KAT. OBIEKTU<br>I                 |
| FUNKCJA   | IMIĘ I NAZWISKO                         | SPECJALNOŚĆ, NR UPRAWNIENI        |
| Projektant   | [DO UZUPEŁNIENIA]                       | [DO UZUPEŁNIENIA]                 |
| Projektant (wsp.)   | [DO UZUPEŁNIENIA]                       | [DO UZUPEŁNIENIA]                 |
| Sprawdzający   | nie dotyczy (art. 20 ust. 3 pkt 2 PB)   | —                                 |
| Opracował   | [DO UZUPEŁNIENIA]                       | [DO UZUPEŁNIENIA]                 |
| TYTUŁ RYSUNKU<br><b>PLAN ZAGOSPODAROWANIA DZIAŁKI</b>   |                                         |                                   |
| SKALA<br><b>1:500</b>   | FORMAT<br>A2                            | DATA WYDANIA<br>2026-09-25        |
| RODZAJ DOK.<br>plan zagospodarowania   | NR RYSUNKU<br><b>PZT-01</b>             | ARKUSZ<br>1/3                     |
| REW.<br><b>0</b>   |                                         |                                   |