


RZUT II PIĘTRA 1:50

OZNACZENIA LINII

- elementy nad płaszczyzną cięcia (obrysy płyt, wsporników, brył wyższych kondygnacji)
--- elementy poniżej płaszczyzny cięcia (widok z góry)
--- osie konstrukcyjne; linia punktowa z pogrubionymi końcami — ślad przebiegu

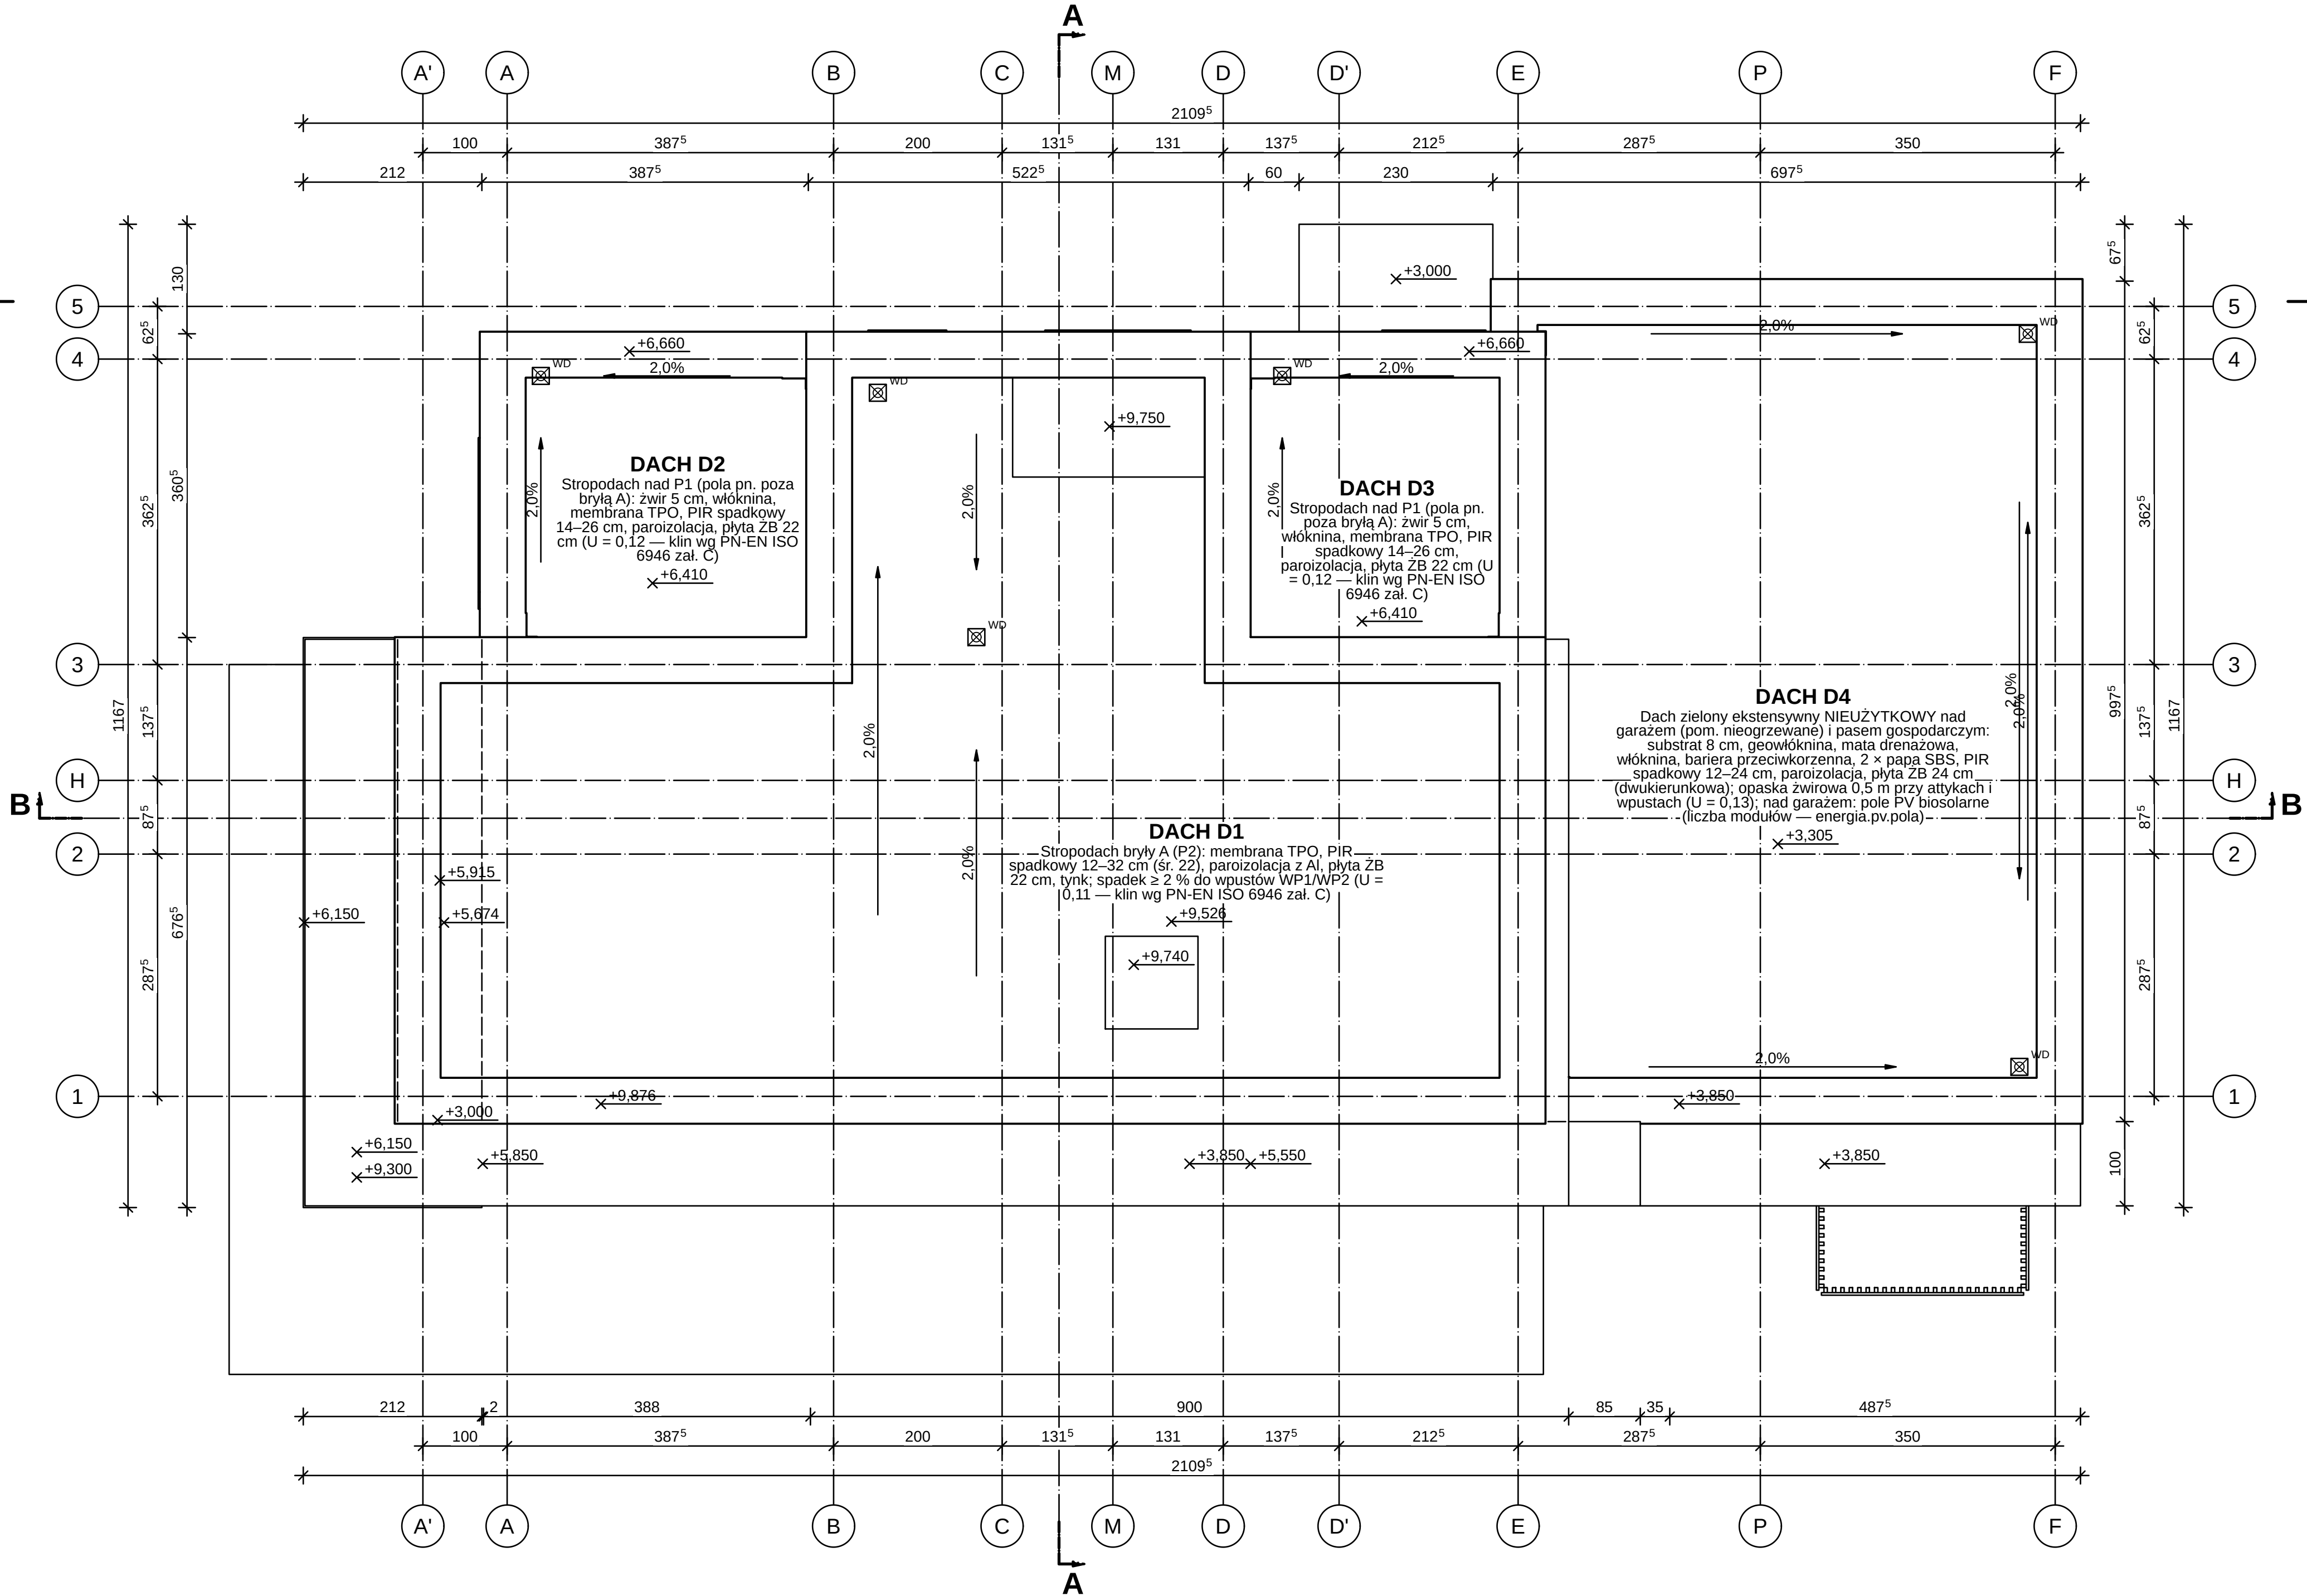

RZUT DACHU 1:50

OZNACZENIA MATERIAŁÓW (PN-B-01030 + przyjęte)

- Włna mineralna 035 (szkielet, docieplenia, ściana dom-garaż);
Wełna mineralna fasadowa (elewacja wentylowana bryły A, A1)
— meander, UUU
Styropian grafityowy EPS 031 (ETICS, NRO w systemie)
— zgrubak, VVV
Membrana fasadowa wiatroizolacyjna UV-stabilna, czarna (sd = 0,02 m)
Błoczek wapniowo-piaskowy 12 cm, kl. 15 (ścianki działowe, boczny w klatce); Błoczek wapniowo-piaskowy (silikat) 18 cm, kl. 20, gr. 1, na zaprawie cienkowarstwowej — kratka ukośna 45°/135°
Żelbet C25/30, B500SP (stropy, płyta fundamentowa, ściany) — 45° na przemiern cięgie i przerywane

OBJAŚNIENIA I UWAGI

1. Wymiary w cm (mm w indeksie górnym, np. 24° = 24,5 cm), rzędne w m względem ±0,000 = 101,650 m n.p.m. (PL-EVRF2007-NH).
2. Rzut: płaszczyzna cięcia +1,10 m nad posadzką kondygnacji. Linia kresek — elementy nad płaszczyzną cięcia (obrysy płyt i wsporników, brył wyższych kondygnacji, otwory w stropie nad, belki); linia ciągła — elementy poniżej (widok).
3. Otwory: licznik — szerokość, mianownik — wysokość w świetle muru, w nawiasie wysokość parapetu; symbol stolarki wg zestawienia stolarki.
4. Numeracja pomieszczeń wg PN-B-01025 / PN-EN ISO 4157-2: <nr> kondygnacji (parter = 1) <nr>; identyfikator w modelu: <kond> <nr> (parter = 0).
5. Dzw: strona otwierania (lewo/prawo) wg modelu — patrz: od strony, w którą otwiera się skrzydło.
6. Rysunek wygenerowany automatycznie z modelu modelbudynek.yamf (wersja 1.0, 2026-09-25) — generatory lamela.views.

1 0 1 2 3 4 5 m
PODZIAŁKA 1:50

ZESTAWIENIE POMIESZCZEŃ

Nr	Nazwa pomieszczenia	Posadzka	Kat.	Wys. [m]	Pow. [m²]
3.02	Sypialnia rodziców	Deska warstwowa dębowa 15 mm, klejona podst.		2,77	21,43
3.05	Gabinet / pokój gościnny okazjonalny	Deska warstwowa dębowa 15 mm, klejona podst.		2,77	16,25
3.03	Garderoba (przedpokój apartamentu)	Deska warstwowa dębowa 15 mm, klejona podst.		2,77	10,49
3.07	Pom. techniczne (centrala rekuperacyjna, wylaz na dach)	Płyty gresowe 60×120 na kleju C2TE \$1 techn.		2,77	5,90
3.01	Hol	Deska warstwowa dębowa 15 mm, klejona podst.		2,77	5,74
3.04	Łazienka rodziców	Płytki gresowe 60×120 na kleju C2TE \$1 techn.		2,77	5,51
3.08	Szacht instalacyjny SI	techn.		2,77	0,45
3.06	Klatka schodowa (wyjście z biegu 2, pustka)	Deska warstwowa dębowa 15 mm, klejona podst.		2,77	0,24
RAZEM powierzchnia netto					66,01
w tym użytkowa (podst. + pomoc.)					53,67

REW.		OPIS ZMIANY		DATA	
0		Wydanie — rysunek wygenerowany z modelu		2026-09-25	
PRACOWNIA PROJEKTOWA PRACOWNIA PROJEKTOWA — nazwa do uzupełnienia adres pracowni do uzupełnienia			STADIUM PB	BRANŻA ARCHITEKTURA (AR)	
INWESTOR (do uzupełnienia)					
OBJEKT / NAZWA ZAMIERZENIA BUDOWLANEGO					
Budynek mieszkalny jednorodzinny wolnostojący „Dom LAMELA”					
ADRES / LOKALIZACJA (NR DZIAŁKI, OBRĘB, JEDN. EWIDENCYJNA) ul. Lipowa (fikcyjna), dz. nr ewid. 123/4, obręb 0005 Przykładowo, gm. Przykładowo (fikcyjna)					KAT. OBJEKTU I
FUNKCJA	IMIĘ I NAZWISKO		SPECJALNOŚĆ, NR UPRAWNIEN		DATA
Projektant	[DO UZUPEŁNIENIA]		[DO UZUPEŁNIENIA]		PODPIS
Projektant (wsp.)	[DO UZUPEŁNIENIA]		[DO UZUPEŁNIENIA]		
Sprawdzający	nie dotyczy (art. 20 ust. 3 pkt 2 PB)		—		
Opracował	[DO UZUPEŁNIENIA]		[DO UZUPEŁNIENIA]		
TYTUŁ RYSUNKU					