


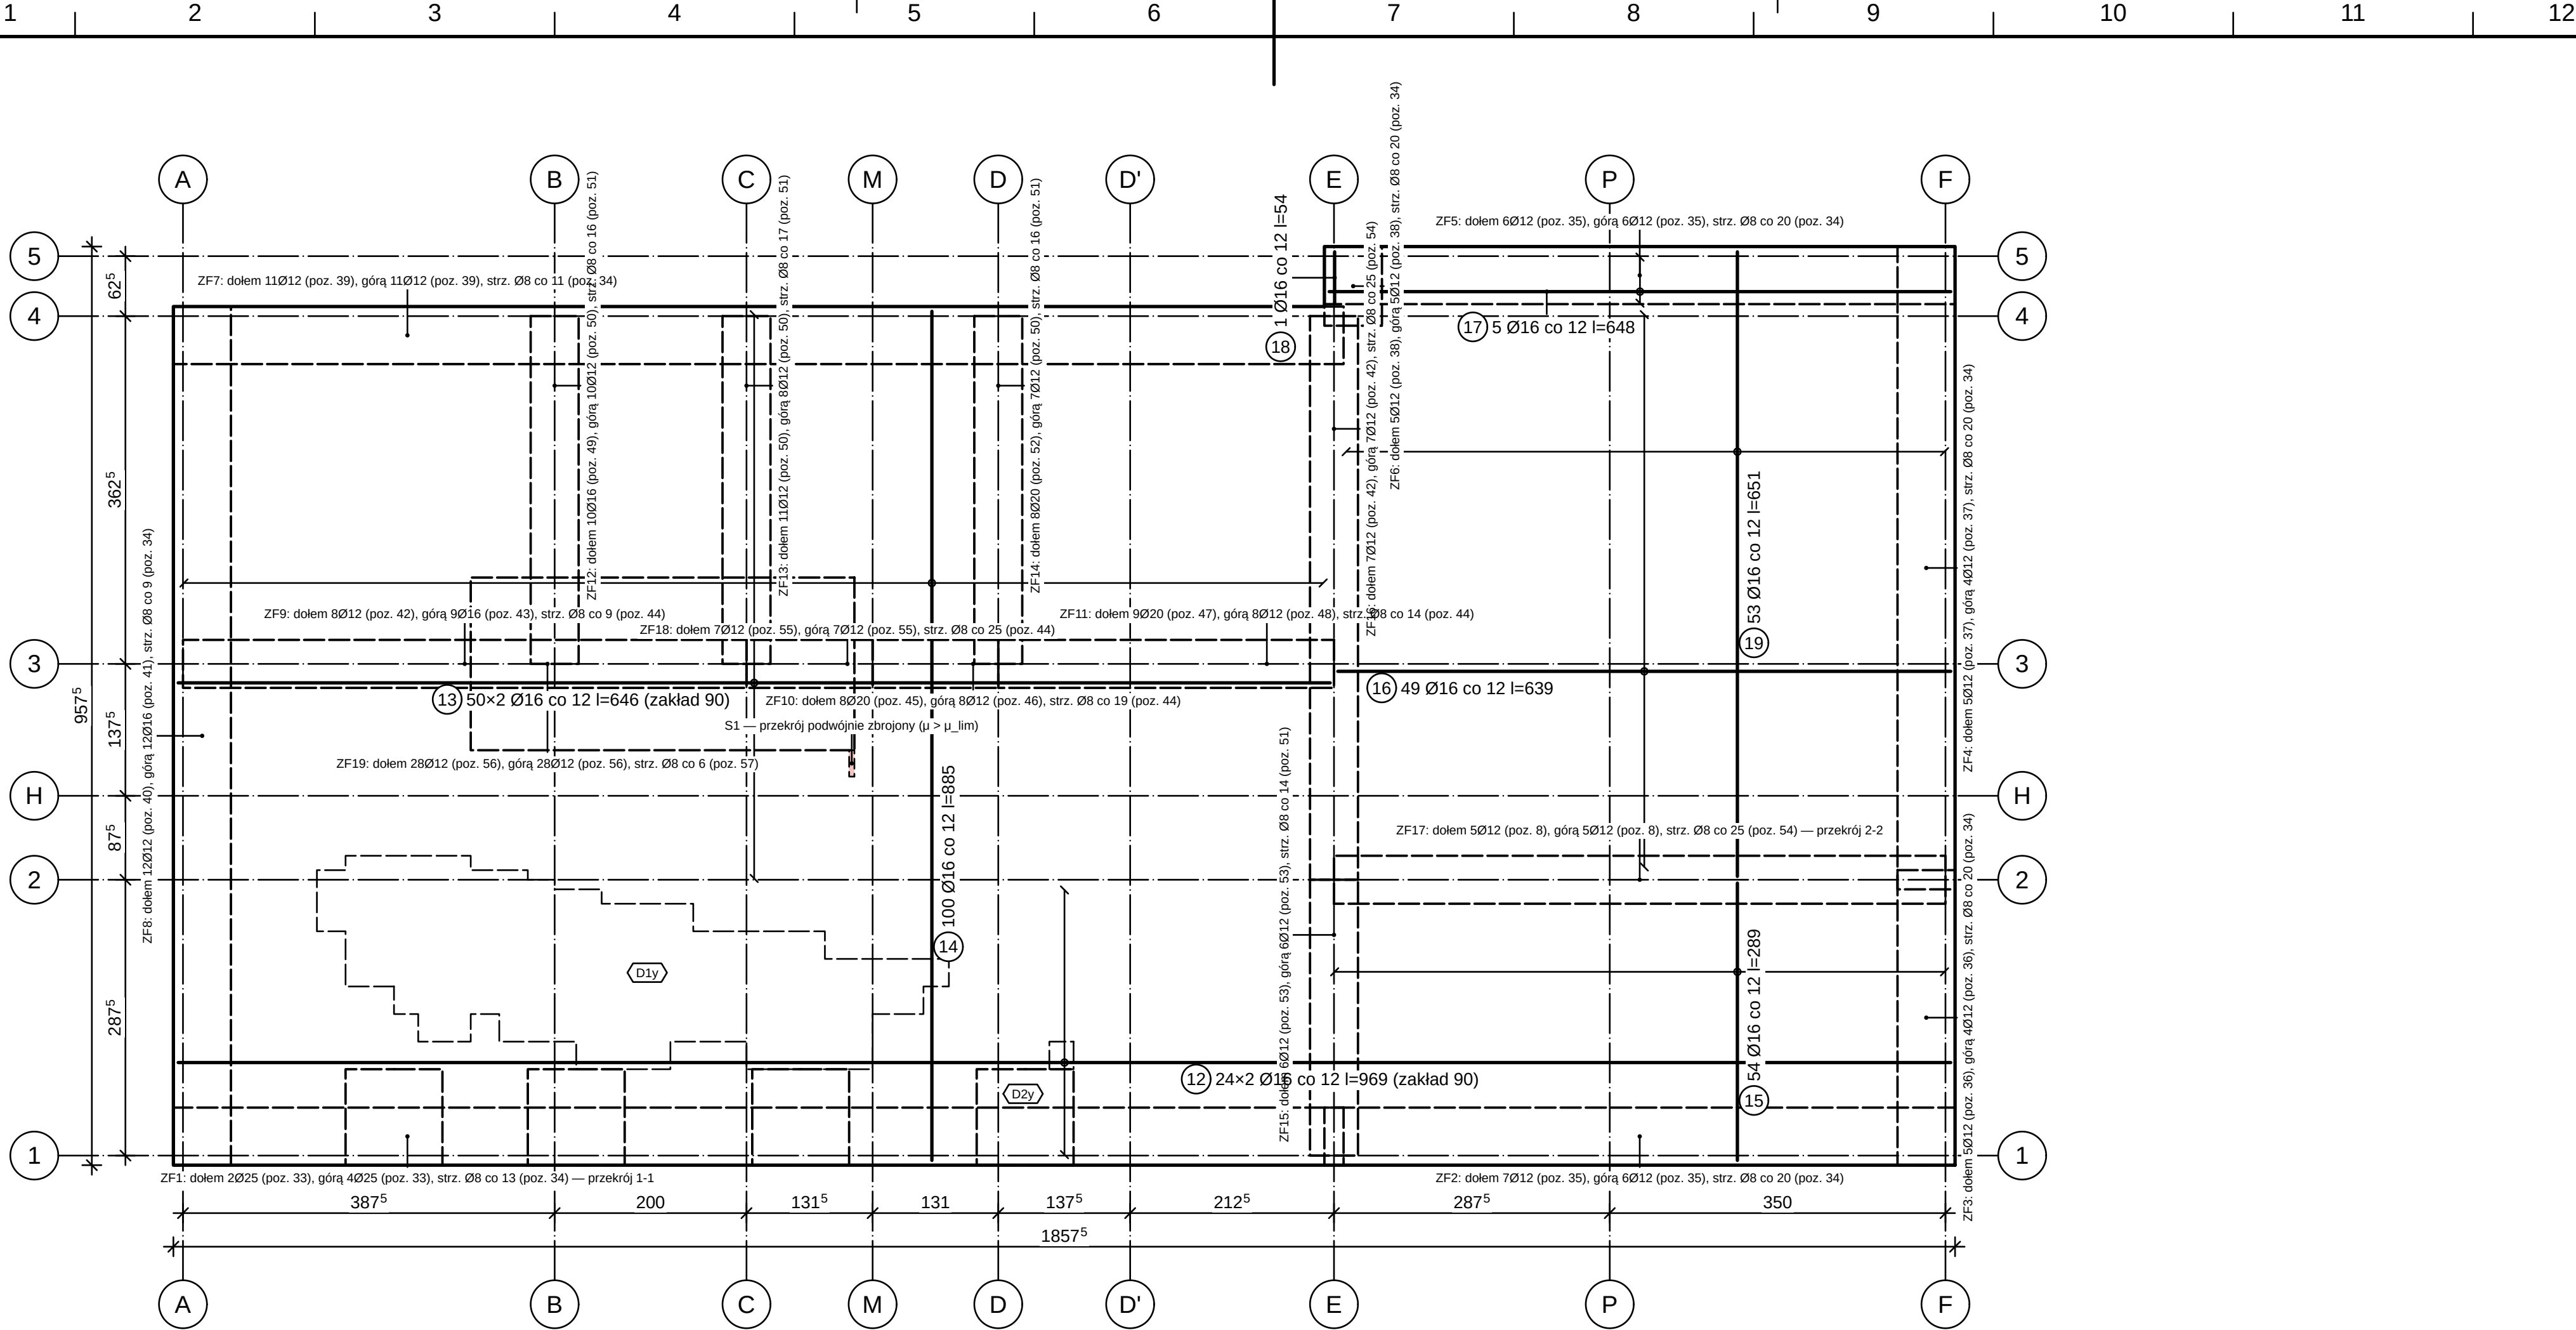


ZBROJENIE GÓRNE PŁYTY FUNDAMENTOWEJ PF1+PF2 1:50

OZNACZENIA NA RYSUNKU

- pręt reprezentatywny grupy (warstwa górna), linia gruba
- pręt z odgięciem 90° — odgięcie (ramię) pokazane w płaszczyźnie rysunku
- linia rozkładu prętów grupy (zasieg), kółko — pręt reprezentatywny
- numer pozycji pręta (zestawienie stali)
- żebra i pogrubienia pod płytą (zbrojenie — przekroje 1-1, 2-2, 3-3)

1 0 1 2 3 4 5 m
PODZIAŁKA 1:50

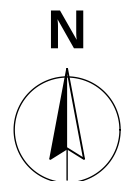

OBJAŚNIENIA I UWAGI

- Wymiary w cm (mm w indeksie górnym, np. 24⁵ = 24,5 cm), rzędne w m względem ±0,000 = 101,650 m n.p.m. (PL-EVRF2007-NH).
- Zestawienie stali, strefy zbrojenia narożnego/na ścinanie i dozbrojenia — arkusz PT-BO-05.
- Stal zbrojeniowa B500SP (klasa ciągliwości C, f_{yk} = 500 MPa) wg PN-H-93220:2018-02 / PN-EN 10080; pręty gięte na zimno na trzpieniach $\phi_m \geq 4\phi$ ($\phi \leq 16$ mm) i $\geq 7\phi$ ($\phi > 16$ mm) — PN-EN 1992-1-1 tabl. 8.1N; oznaczenia prętów i kształtów wg PN-EN ISO 3766 (liczba, nr pozycji, Ø, rozstaw [cm], długość rozwinięcia l [cm]).
- Otuliny zapewnić podkładkami dystansowymi (rozstaw $\leq 1,0$ m, dla siatek górnych — podpórki „kobyłki” $\leq 1,0$ m) — PN-EN 13670 p. 6.5; odchyłka wykonawcza $\Delta c_{dev} = 10$ mm uwzględniona w c_{nom} (PN-EN 1992-1-1 4.4.1.3 + NA).
- Pręty łączące na zakład l₀ (tabela w stopce zestawienia), styki mijankowo — w jednym przekroju ≤ 50 % prętów; odstęp w świetle prętów $\geq \max(\phi; d_g + 5$ mm; 20 mm) — PN-EN 1992-1-1 8.2(2), 8.7.2; pręty dolne w strefie podpory zakotwić $\geq 10\phi$ za licem (9.3.1.2(1) → 9.2.1.5).
- Siatki płyty: dołem Ø12 co 16, górą Ø16 co 12 cm w obu kierunkach — dobór modułu („dobierz siatkę”) z A_{s,req} (MES płyty fundamentowej (90 % pola poza żebrami)); dozbrojenia (obszary kreskowe D...) — pręty między prętami siatki; pręty > 12 m łączone na zakład (mijankowo).
- Kolejność robót: podsypka zagęszczona (l_s $\geq 0,98$) → XPS (płyty układane mijankowo, szczelnie) → folia PE → zbrojenie żeber i płyty, uzioł/przewód wyrównawczy, tuleje przejść → betonowanie płyty z żebrami jednym zabiegiem (bez przerw roboczych) → pielęgnacja ≥ 7 dni (PN-EN 13670 p. 8.5).
- Płyta fundamentowa — analiza MES na podłożu sprężystym (moduł płyta_fundamentowa: płyta ACM z żebrami jako pasma h = h_{płyty} + h_{żebra}, sprężyny Winklera, kontakt jednostronny, 39 obliczeń: kombinacje STR × 3 warianty k_s = 2652, 5303 i 10606 kN/m² z M₀ i wymiarów płyty — Bowles (5-16a), PN-EN 1997-1 zał. F.2; weryfikacja: belka Hetényiego, błąd < 1 %). Maks. docisk p_d = 273 kPa (q_{Rd,lok} = 319 kPa), osiadanie w_k = 33 mm, odrywanie 0 % powierzchni.
- UWAGA — MES płyty wykazuje niespełnione warunki: Przebiec — fundament (6.4.4(2), (6.51)–(6.53)) (1 > 0); Przebiec — fundament (6.4.4(2), (6.51)–(6.53)) (0 > 0) [WYMAGA ZMIANY MODELU].
- Strefy zakreskowane ($\mu > \mu_{lim}$, 1 el. MES): przekrój podwójnie zbrojony — A_{s1} w warstwie rozciąganej (siatka + dozbrojenie/pręty żebra), A_{s2} w warstwie przeciwniej (ujęte w wymaganiiu tej warstwy); pręty ściskane objęte strzemiionami żebra s $\leq 15\phi$ (PN-EN 1992-1-1 9.2.1.2(3)).
- Rysunek wygenerowany automatycznie z modelu model/budynek.yaml (wersja 1.0, 2026-09-25) — generatory lamela.views.

REW.	OPIS ZMIANY		DATA	
0	Wydanie — rysunek wygenerowany z modelu		2026-09-25	
PRACOWNIA PROJEKTOWA PRACOWNIA PROJEKTOWA — nazwa do uzupełnienia adres pracowni do uzupełnienia			STADIUM PT	BRANŻA KONSTRUKCJA (BO)
INWESTOR (do uzupełnienia)				
OBIEKT / NAZWA ZAMIERZENIA BUDOWLANEGO Budynek mieszkalny jednorodzinny wolnostojący „Dom LAMELA”				
ADRES / LOKALIZACJA (NR DZIAŁKI, OBRĘB, JEDN. EWIDENCYJNA) ul. Lipowa (fikcyjna), dz. nr ewid. 123/4, obręb 0005 Przykładowo, gm. Przykładowo (fikcyjna)				KAT. OBIEKTU I
FUNKCJA	IMIĘ I NAZWISKO	SPECJALNOŚĆ, NR UPRAWNIEŃ	DATA	PODPIS
Projektant	[DO UZUPEŁNIENIA]	[DO UZUPEŁNIENIA]		
Projektant (wsp.)	[DO UZUPEŁNIENIA]	[DO UZUPEŁNIENIA]		
Sprawdzający	nie dotyczy (art. 20 ust. 3 pkt 2 PB)	—		
Opracował	[DO UZUPEŁNIENIA]	[DO UZUPEŁNIENIA]		
TYTUŁ RYSUNKU ZBROJENIE GÓRNE PŁYTY FUNDAMENTOWEJ				
SKALA 1:50	FORMAT A2	DATA WYDANIA 2026-09-25	RODZAJ DOK. rysunek zbrojenia	NR RYSUNKU PT-BO-04
				ARKUSZ 4/27
				REW. 0