


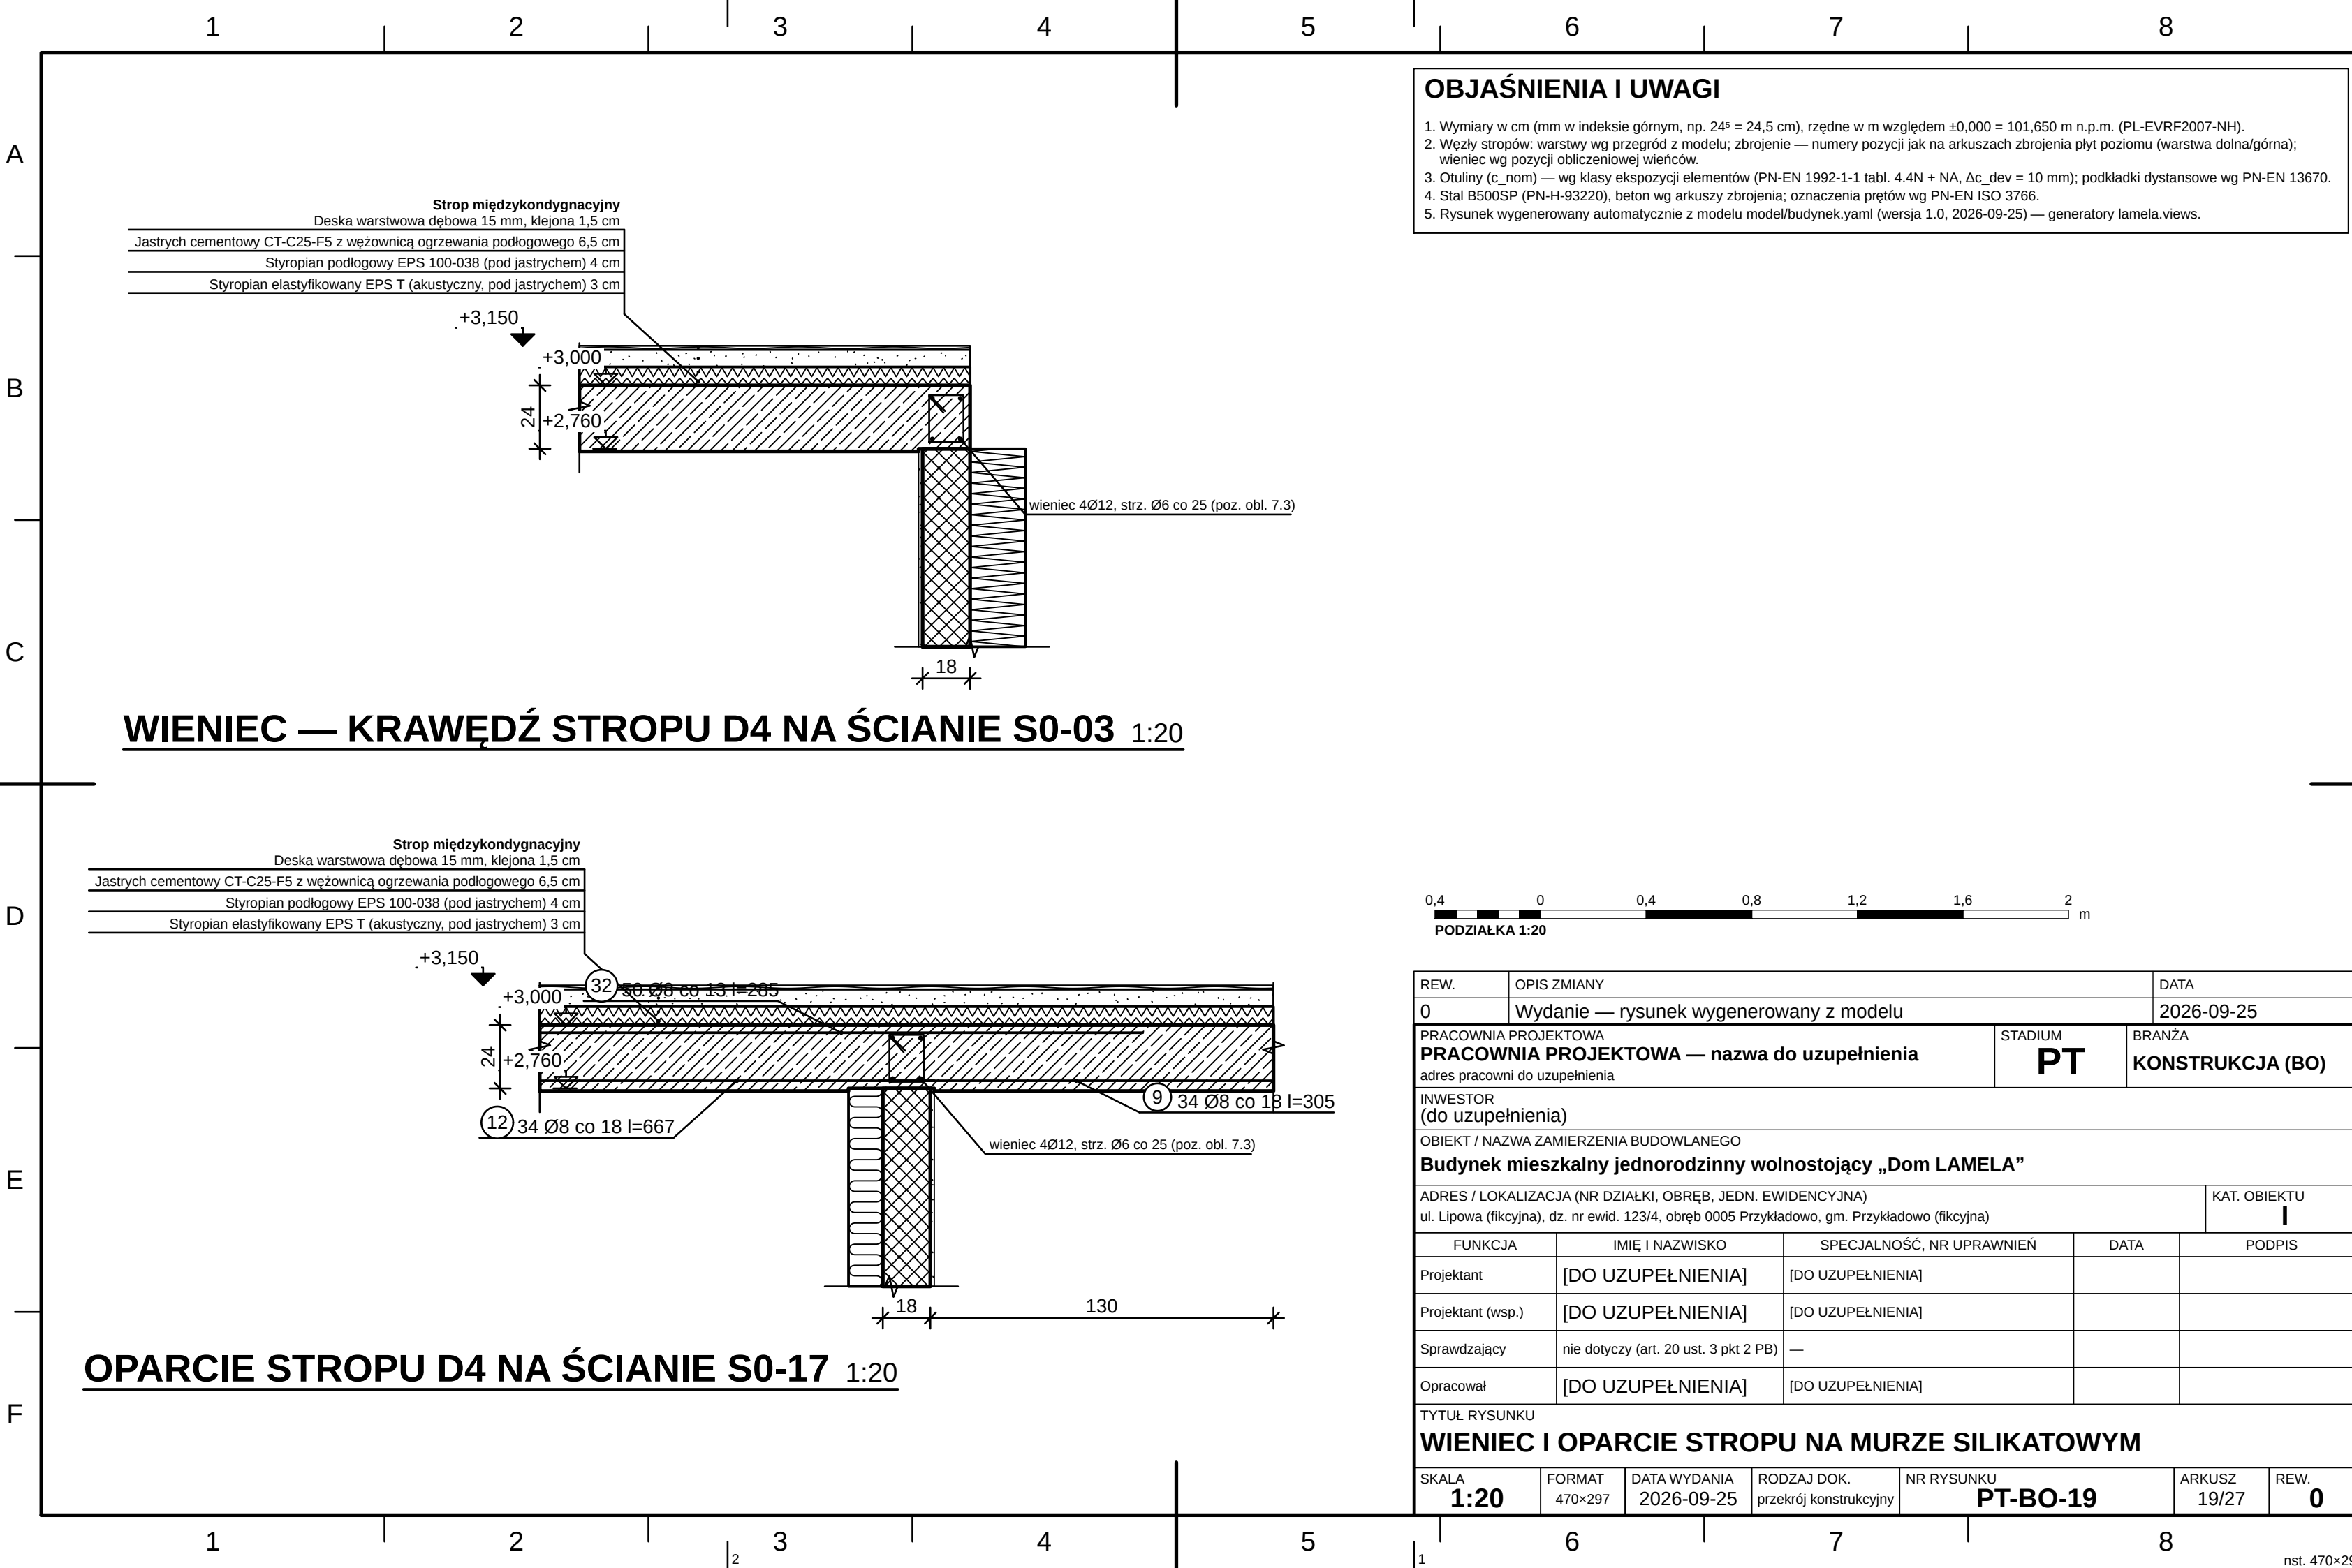

REW.	OPIS ZMIANY			DATA	
0	Wydanie — rysunek wygenerowany z modelu			2026-09-25	
PRACOWNIA PROJEKTOWA PRACOWNIA PROJEKTOWA — nazwa do uzupełnienia adres pracowni do uzupełnienia			STADIUM PT	BRANŻA KONSTRUKCJA (BO)	
INWESTOR (do uzupełnienia)					
OBIEKT / NAZWA ZAMIERZENIA BUDOWLANEGO Budynek mieszkalny jednorodzinny wolnostojący „Dom LAMELA”					
ADRES / LOKALIZACJA (NR DZIAŁKI, OBRĘB, JEDN. EWIDENCYJNA) ul. Lipowa (fikcyjna), dz. nr ewid. 123/4, obręb 0005 Przykładowo, gm. Przykładowo (fikcyjna)				KAT. OBIEKTU I	
FUNKCJA	IMIĘ I NAZWISKO	SPECJALNOŚĆ, NR UPRAWNIEŃ	DATA	PODPIS	
Projektant	[DO UZUPEŁNIENIA]	[DO UZUPEŁNIENIA]			
Projektant (wsp.)	[DO UZUPEŁNIENIA]	[DO UZUPEŁNIENIA]			
Sprawdzający	nie dotyczy (art. 20 ust. 3 pkt 2 PB)	—			
Opracował	[DO UZUPEŁNIENIA]	[DO UZUPEŁNIENIA]			
TYTUŁ RYSUNKU WIENIEC I OPARCIE STROPU NA MURZE SILIKATOWYM					
SKALA 1:20	FORMAT 470×297	DATA WYDANIA 2026-09-25	RODZAJ DOK. przekrój konstrukcyjny	NR RYSUNKU PT-BO-19	ARKUSZ 19/27
				REW. 0	