

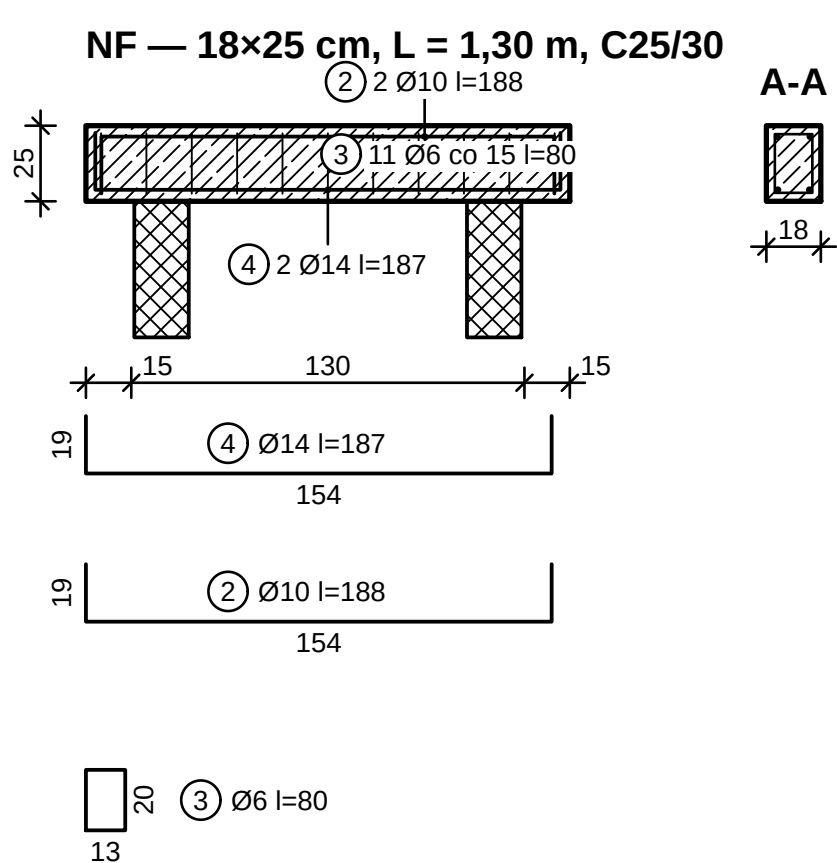
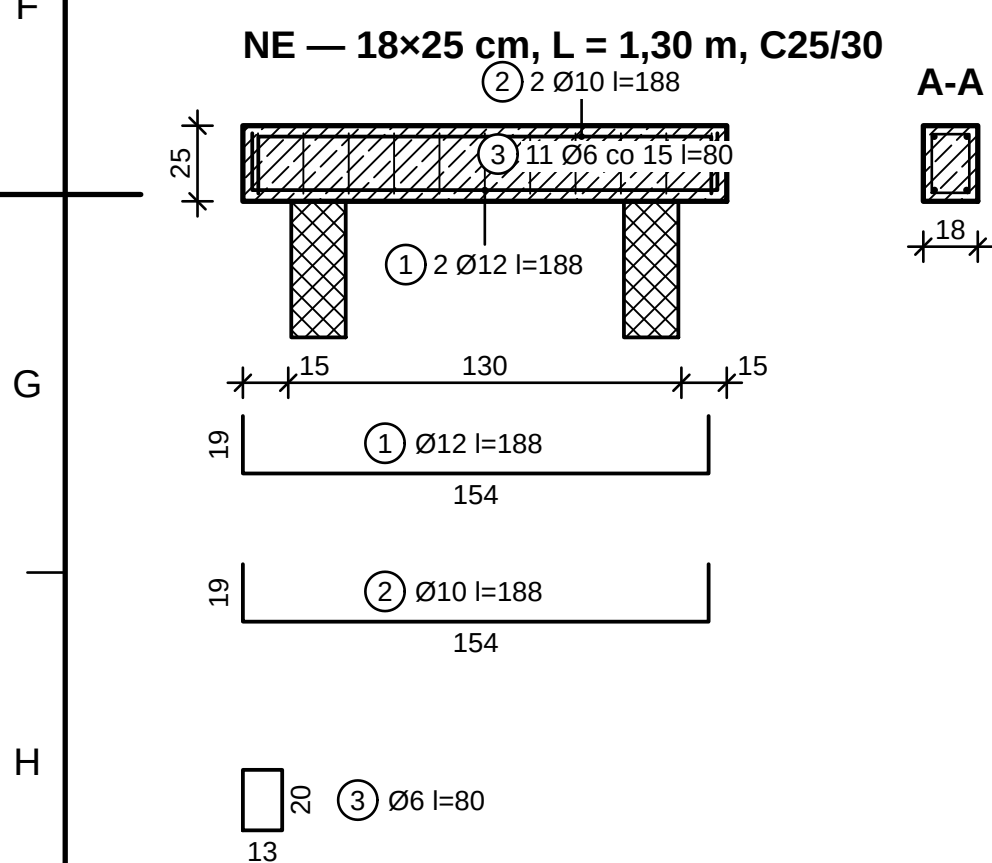
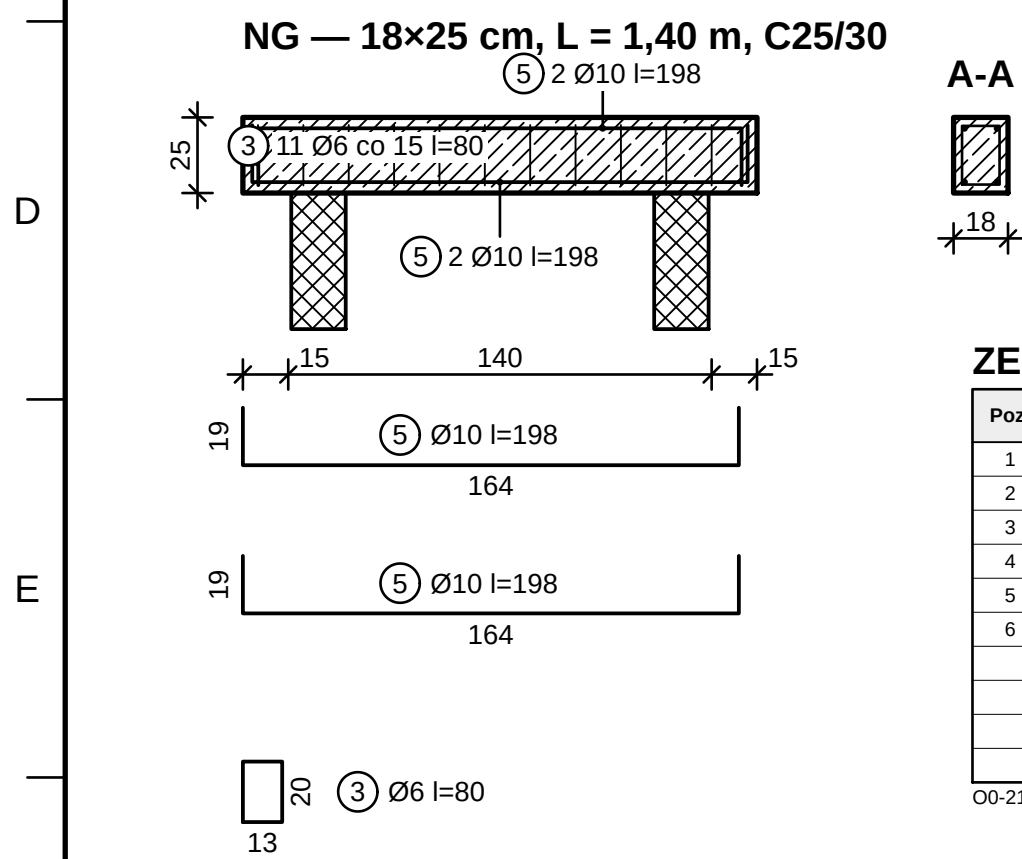


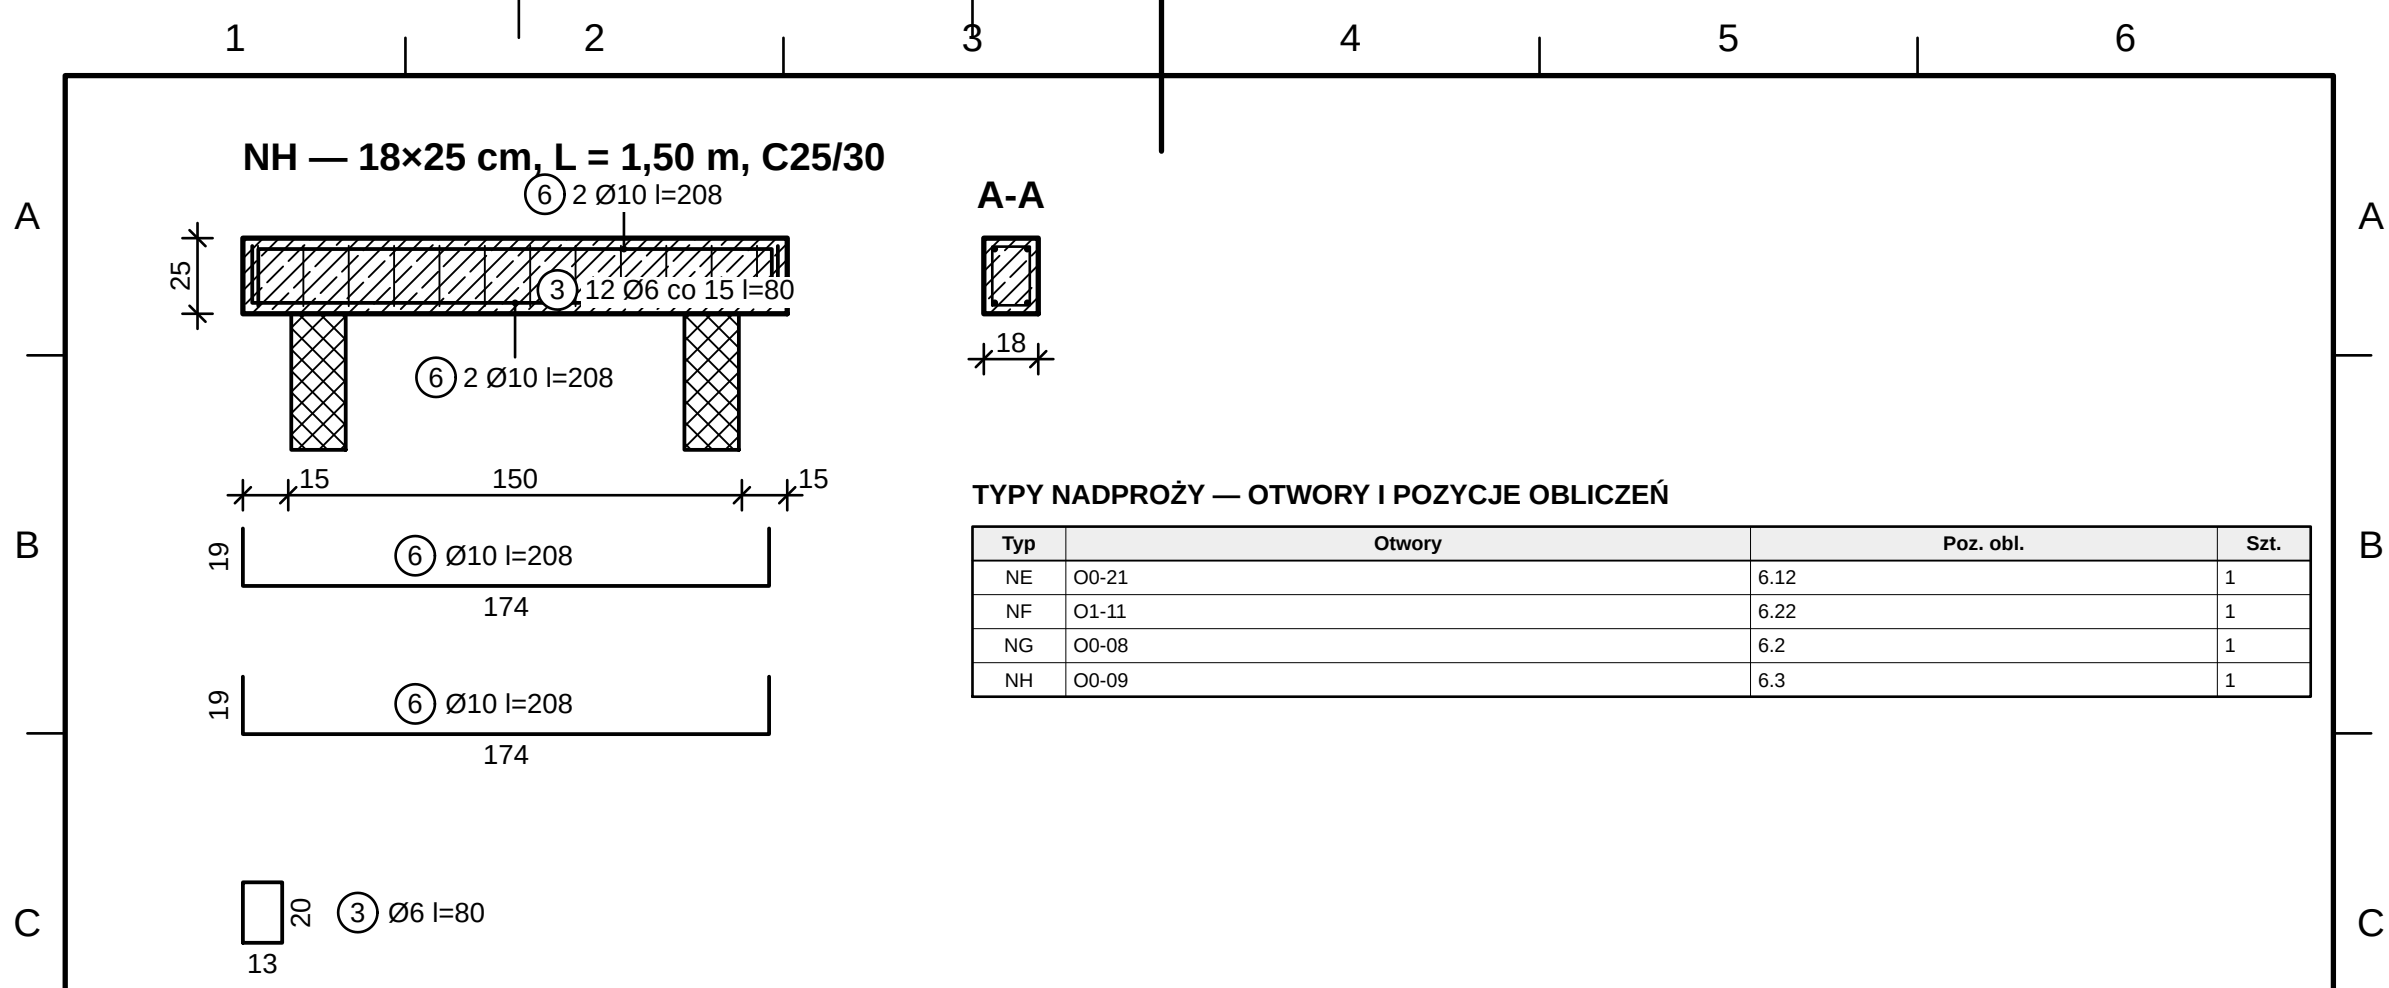

ZBROJENIE NADPROŽY NE, NF, NG, NH 1:25

OBJAŚNIENIA I UWAGI

1. Wymiary w cm (mm w indeksie górnym, np. 24" = 24,5 cm), rzędne w m względem $+0,00 = 101,650$ m n.p.m. (PL-EVR92-1997-20-NH).
2. Belki: przęty łodni i górne z odgięciem 90° w stałych podporach (zakotwienie ≥ 1 łb od lica podpory — PN-EN 1992-1-1 9.2.1.4), strzemięna zamknięte z hakami 135° (8.5, rys. 8.5), pierwsze strzemię 5 cm od lica podpory; rozstaw wg obliczeń (6.2.3), $s \leq \min(0,75 d; 400 \text{ mm})$ (8.6N).
3. Przekrój A-A — w środku rozpięci; długości prętów l — długości rozwinienia (wymiary zewnętrzne, odliczenie gnięcia wg PN-EN ISO 3766).
4. Betonowanie: beton wg PN-EN 206+A2 i PN-B-06285 (klasa, ekspozycja, $D_{\max}$ 16 mm, konsystencja S3; pielęgnacja ≥ 7 dni (klasa pielęgnacji 2 — PN-EN 13670 p. 8.5); przerwy robocze wyłącznie w miejscach ułożonych z projektantem.
5. Rozszalowanie i usunięcie podpór: płyty i belki po uzyskaniu $\geq 70\%$ f_{cd} (PN-EN 13670 p. 5.6 i 8.5), wsporniki — nie wcześniej niż po 28 dniach i po wykonaniu elementów docożających zaplecze; podpory wtórne do 28 dni.
6. Nadproża pogrupowano w typy (jednokowy przekrój, długość i zbrojenie z obliczeń); liczby sztuk w zestawieniu — łącznie dla wszystkich nadproży typu.
7. Rysunek wygenerowany automatycznie z modelu model/budynek.yaml (wersja 1.0, 2026-09-25) — generatory lamela.views.

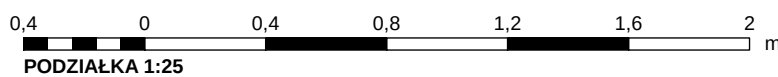

REW.	OPIS ZMIANY			DATA	
0	Wydanie — rysunek wygenerowany z modelu			2026-09-25	
PRACOWNIA PROJEKTOWA PRACOWNIA PROJEKTOWA — nazwa do uzupełnienia adres pracowni do uzupełnienia			STADIUM PT	BRANŻA KONSTRUKCJA (BO)	
INWESTOR (do uzupełnienia)					
OBIEKT / NAZWA ZAMIERZENIA BUDOWLANEGO Budynek mieszkalny jednorodzinny wolnostojący „Dom LAMELA”					
ADRES / LOKALIZACJA (NR DZIAŁKI, OBRĘB, JEDN. EWIDENCYJNA) ul. Lipowa (fikcyjna), dz. nr ewid. 123/4, obręb 0005 Przykładowo, gm. Przykładowo (fikcyjna)				KAT. OBIEKTU I	
FUNKCJA	IMIĘ I NAZWISKO	SPECJALNOŚĆ, NR UPRAWNIENI		DATA	PODPIS
Projektant	[DO UZUPEŁNIENIA]	[DO UZUPEŁNIENIA]			
Projektant (wsp.)	[DO UZUPEŁNIENIA]	[DO UZUPEŁNIENIA]			
Sprawdzający	nie dotyczy (art. 20 ust. 3 pkt 2 PB)	—			
Opracował	[DO UZUPEŁNIENIA]	[DO UZUPEŁNIENIA]			
TYTUŁ RYSUNKU ZBROJENIE NADPROŻY (2)					
SKALA 1:25	FORMAT 330×594	DATA WYDANIA 2026-09-25	RODZAJ DOK. rysunek zbrojenia	NR RYSUNKU PT-BO-24	ARKUSZ 24/27
					REW. 0