
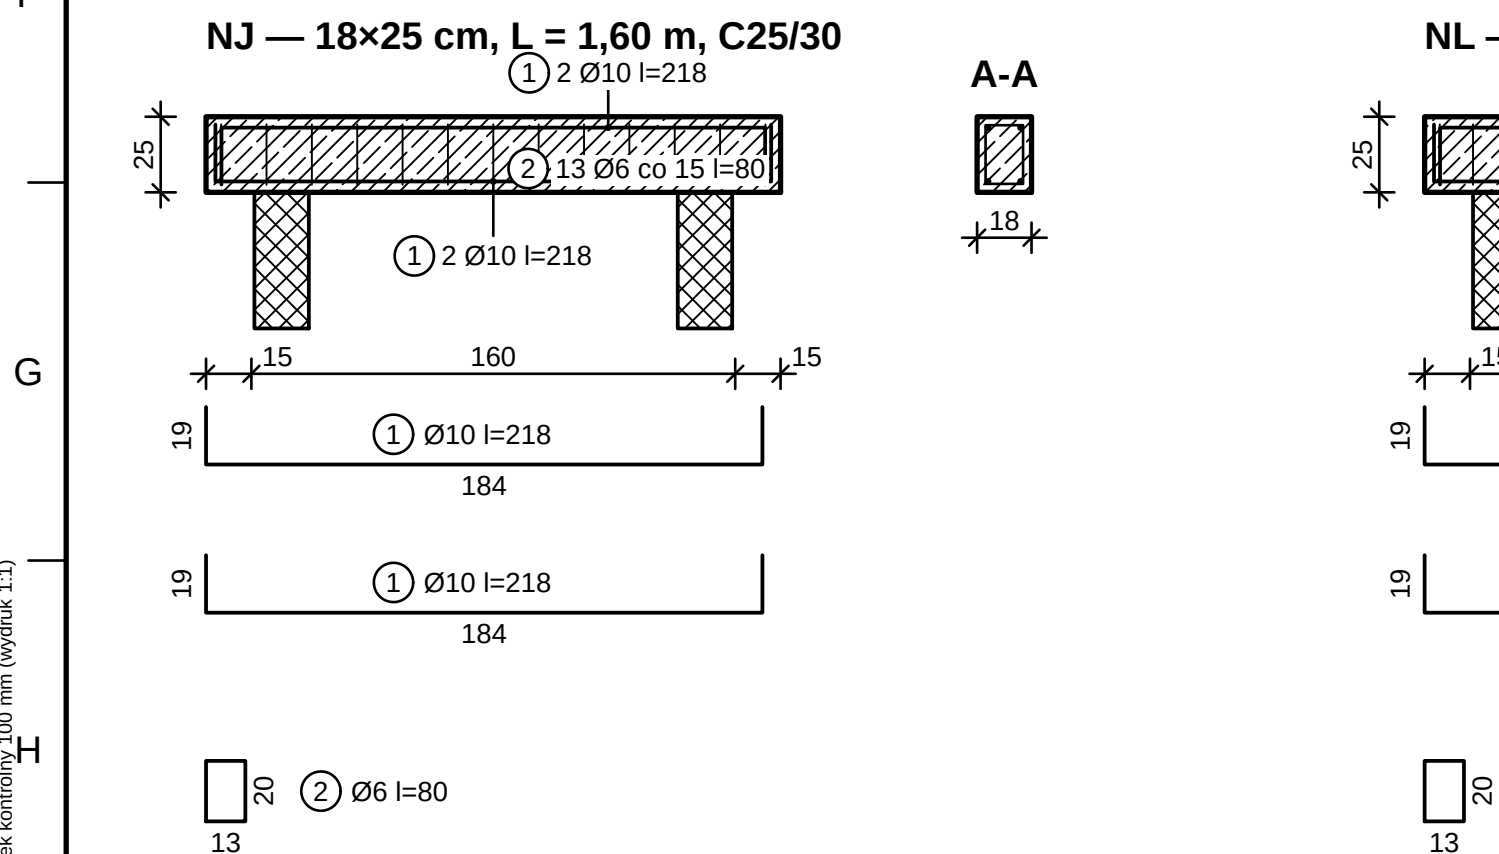
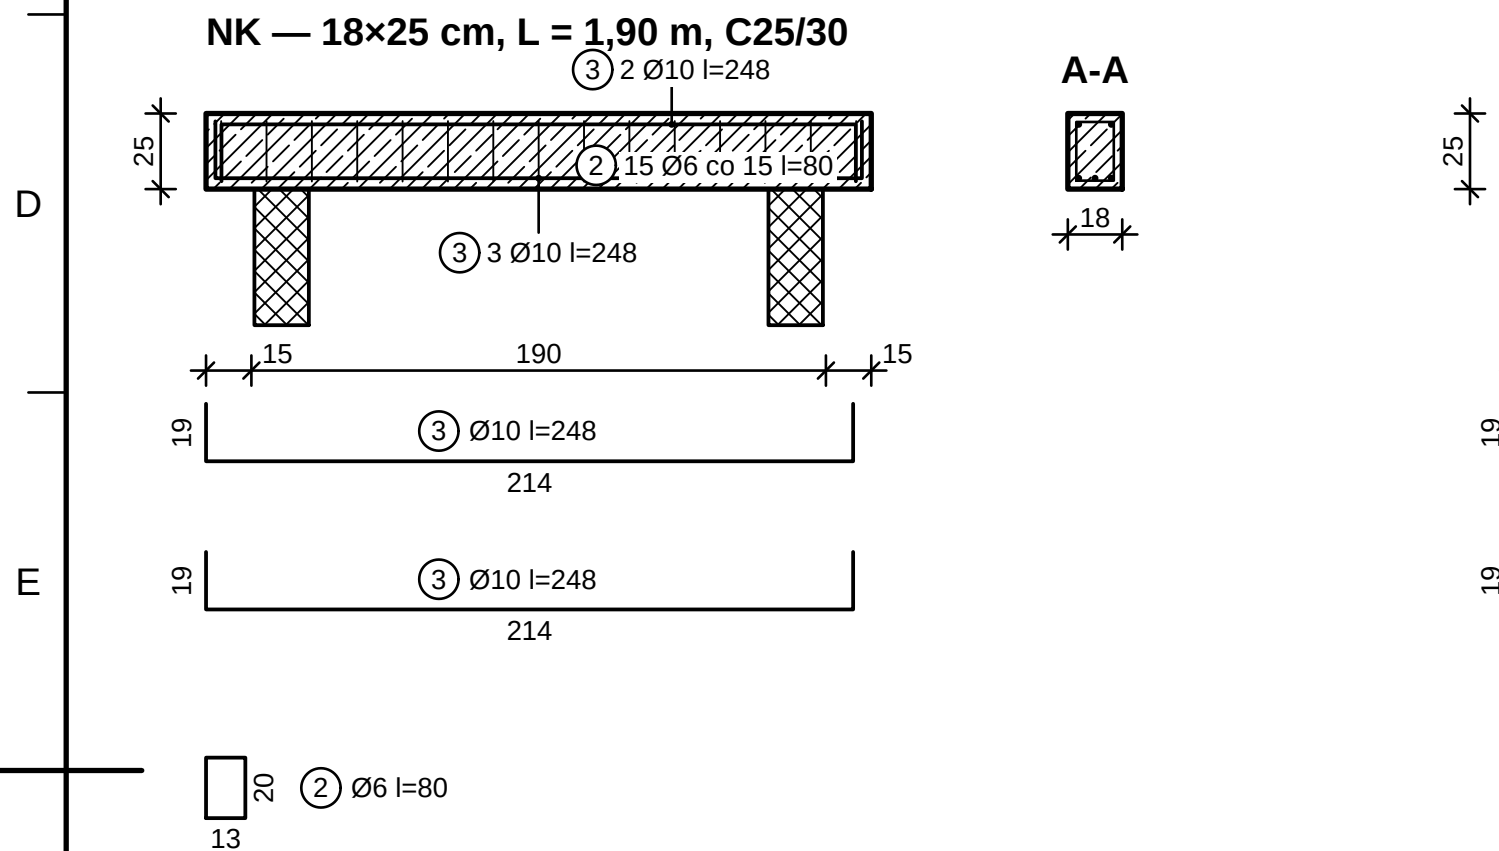


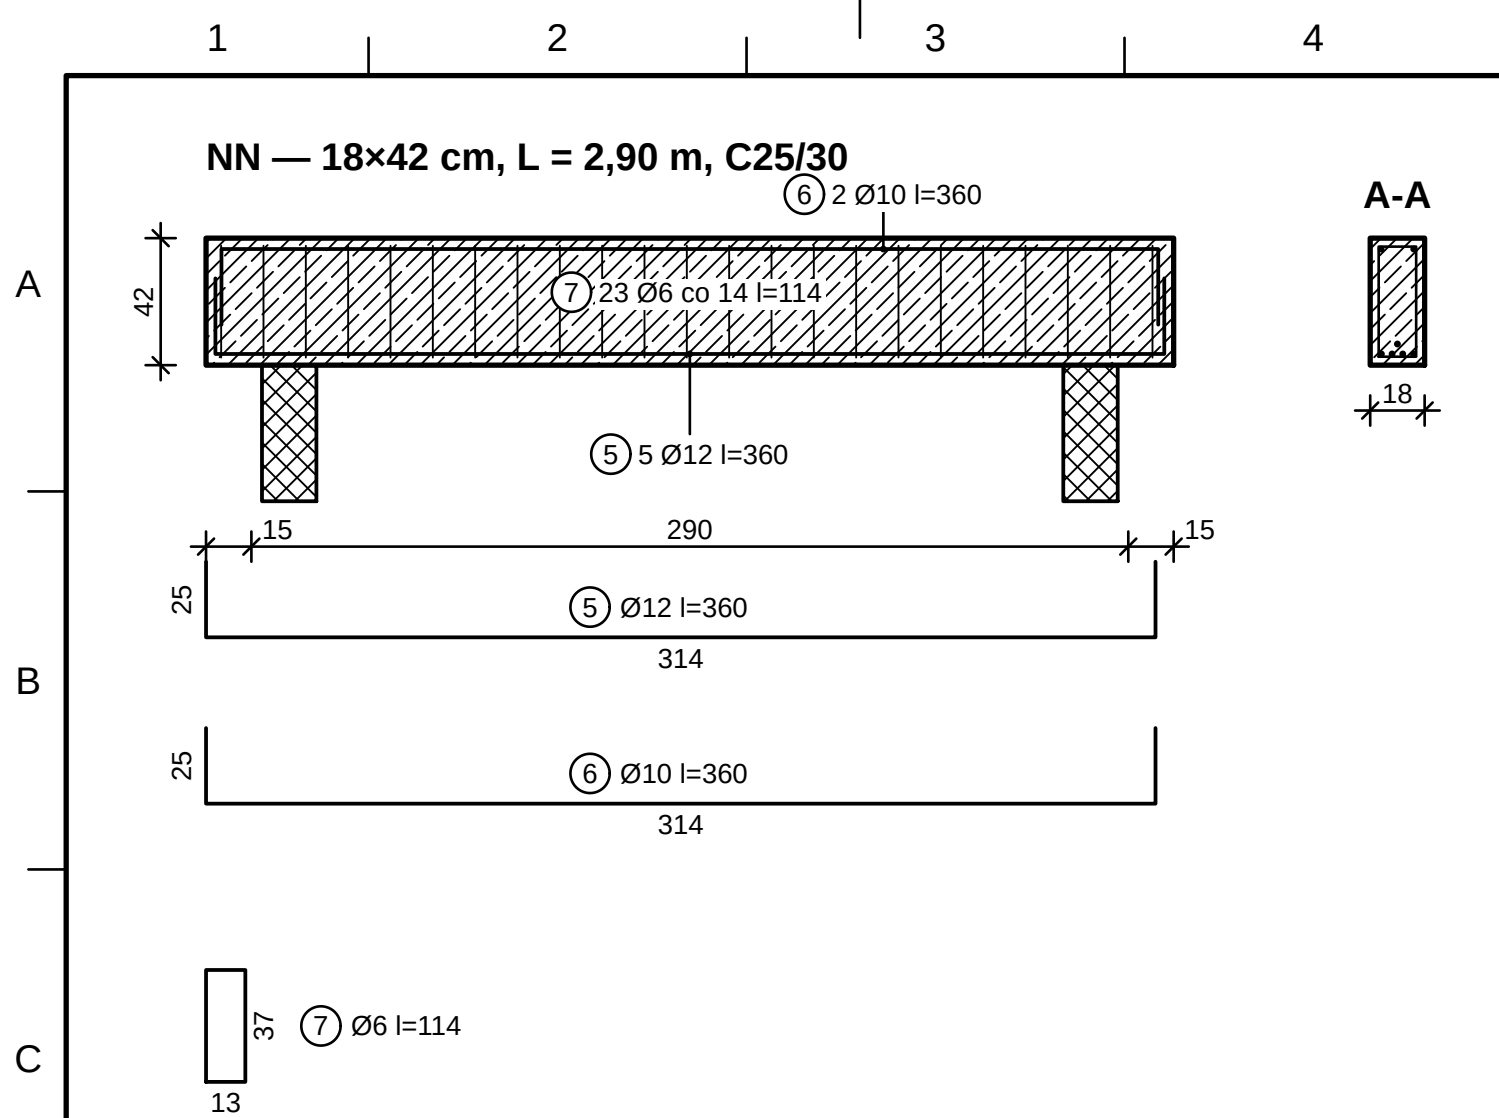

ZBROJENIE NADPROŻY NJ, NK, NL, NM, NN 1:25

TYPY NADPROŻY — OTWORY I POZYCJE OBLICZEŃ

Typ	Otworthy	Poz. obl.	Szt.
NJ	O1-04	6.17	1
NK	O1-02	6.15	1
NL	O0-18	6.11	1
NM	O0-12	6.6	1
NN	O0-11	6.5	1




ZESTAWIENIE STALI

Poz.	Ø [mm]	Kształt ISO 3766, wymiary [cm]	Dług. [cm]	Liczba [szt.]	Elem.	Ø6 [m]	Ø10 [m]	Ø12 [m]
1	10	 21: a=19 b=184 c=19	218	4	N-O1-0		8,72	
2	6	 51: a=13 b=20	80	69	N-O1-0	55,20		
3	10	 21: a=19 b=214 c=19	248	14	N-O1-0		34,72	
4	10	 21: a=19 b=254 c=19	288	4	N-O0-1		11,52	
5	12	 21: a=25 b=314 c=25	360	5	N-O0-1			18,00
6	10	 21: a=25 b=314 c=25	360	2	N-O0-1		7,20	
7	6	 51: a=13 b=37	114	24	N-O0-1	27,36		
		Długość całkowita [m]				82,6	62,2	18,0
		Masa jednostkowa [kg/m]				0,222	0,617	0,888
		Masa [kg]				18,3	38,3	16,0
		RAZEM stal B500SP [kg]						72,6

O1-04, O1-02, O0-18, O0-12, O0-11: beton C25/30, XC1, otulina strzemion $c_{nom} = 25 \text{ mm}$ (tabl. 4.4N + NA).

OBJAŚNIENIA I UWAGI

1. Wymiary w cm (mm w indeksie górnym, np. 24⁵ = 24,5 cm), rzędne w m względem 0,000 = 101,650 m n.p.m. (PL-VERB2007-NH).
2. Belki: przetydłone i górne z odciążeniami 90° w strefach podporowych (zakotwiczenie z 1 b.d od lica podpory; PN-EN 1992-1-1 9.2.1.4), strzemiona z zamkniętymi z hakami 135° (8, rys. 8.5), pierwsze strzemienie 5 cm od lica podpory; rozstaw wg obliczeń (6.2.3), s ≤ min(0,75·d; 400 mm) (9.6N).
3. Przekrój A-A — w środku rozpiętości; długości prętów I — długości rozwinienia (wymiary zewnętrzne, odliczenie gęcia wg PN-EN ISO 3766).
4. Betonowanie: beton wg PN-EN 206+A2 i PN-B-06265 (klasa, ekspozycja, D_{max} 16 mm, konsystencja S3); pielęgnacja ≥ 7 dni (klasa pielęgnacji 2 — PN-EN 13670 p. 8.5); przerwy robocze wyłącznie w miejscach uciążonych z projektem.
5. Rozszalowanie i usunięcie podprór: płyty i belki po uzyskaniu ≥ 70 % f_{cd} (PN-EN 13670 p. 5.6 i 8.5), wsporniki — nie wcześniej niż po 28 dniach i po wykonaniu elementów dociągających zaplecze; podpory wórnó do 28 dni.
6. Nadproża pogrupowane w typy (jednakiwy przekrój, długość i zbrojenie z obliczeń); liczby sztuk w zestawieniu — łącznie dla wszystkich nadprórów typu.
7. Rysunek wygenerowany automatycznie z modelu modelu/budynek.yaml (wersja 1.0, 2026-09-25) — generatory lamela.views.

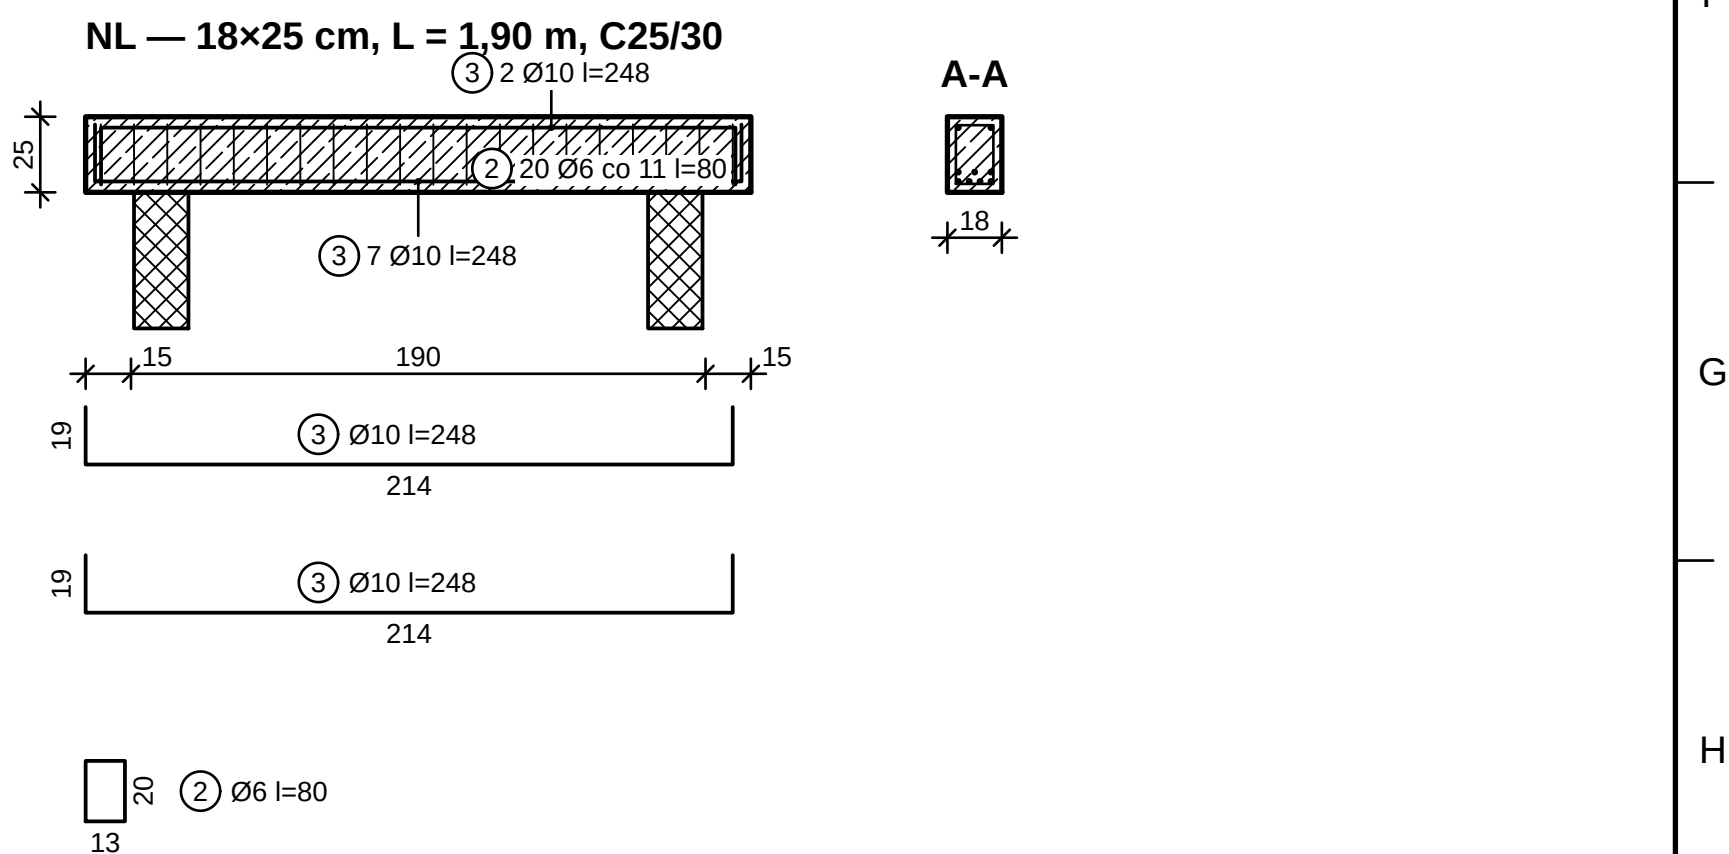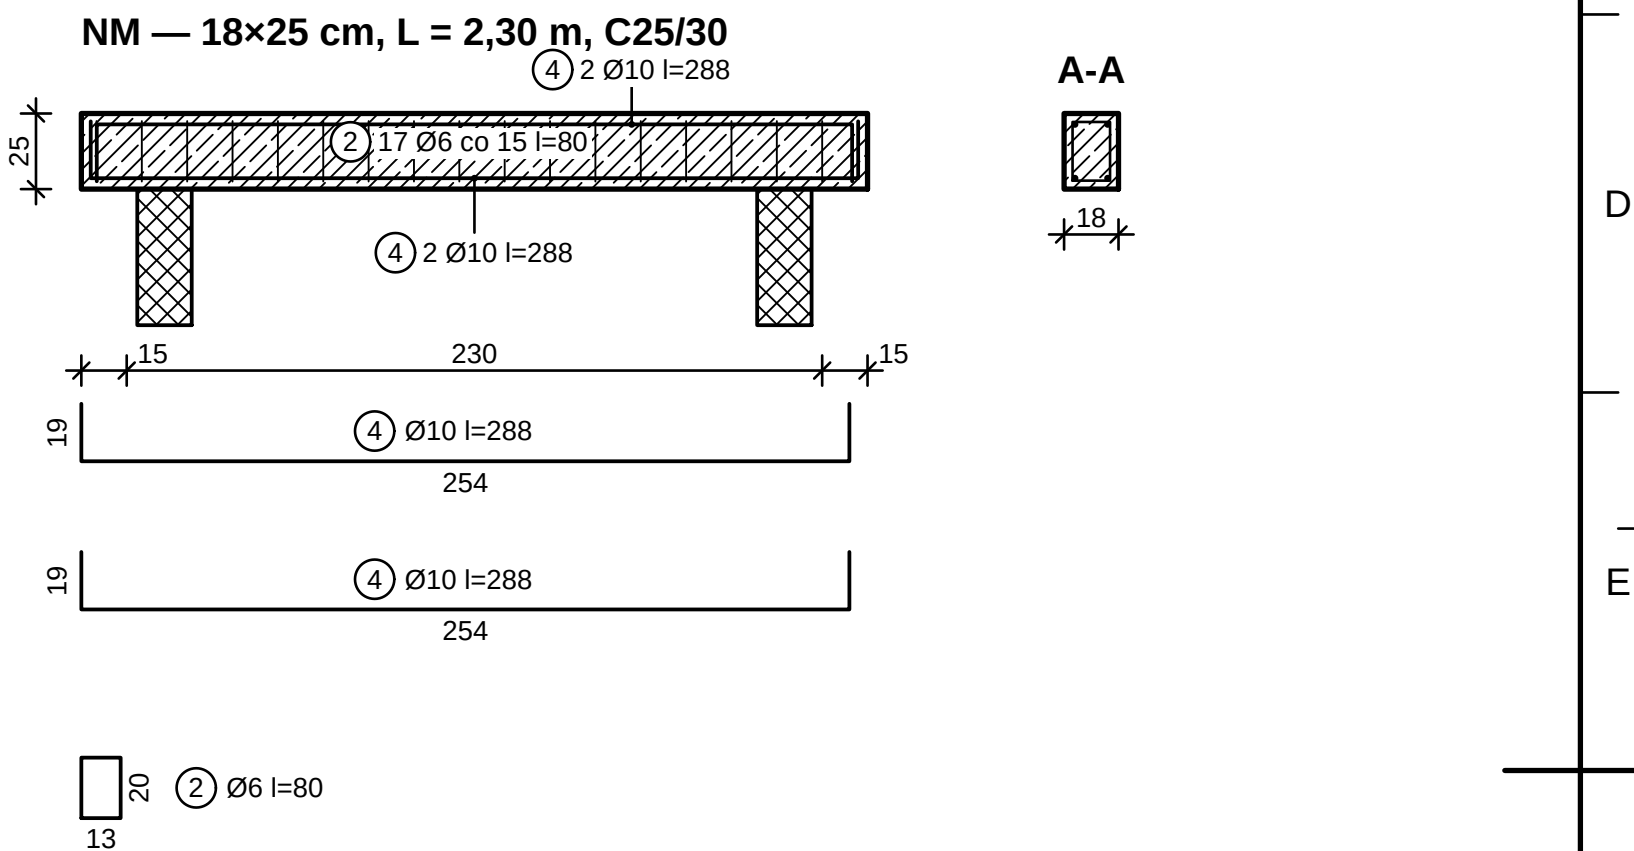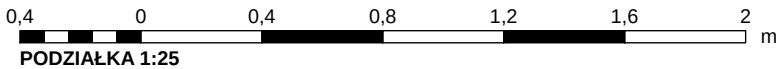

REW.		OPIS ZMIANY		DATA			
0		Wydanie — rysunek wygenerowany z modelu			2026-09-25		
PRACOWNIA PROJEKTOWA PRACOWNIA PROJEKTOWA — nazwa do uzupełnienia adres pracowni do uzupełnienia				STADIUM PT	BRANŻA KONSTRUKCJA (BO)		
INWESTOR (do uzupełnienia)							
OBIEKT / NAZWA ZAMIERZENIA BUDOWLANEGO Budynek mieszkalny jednorodzinny wolnostojący „Dom LAMELA”							
ADRES / LOKALIZACJA (NR DZIAŁKI, OBRĘB, JEDN. EWIDENCYJNA) ul. Lipowa (fikcyjna), dz. nr ewid. 123/4, obręb 0005 Przykładowo, gm. Przykładowo (fikcyjna)					KAT. OBIEKTU I		
FUNKCJA		IMIĘ I NAZWISKO		SPECJALNOŚĆ, NR UPRAWNIENI	DATA	PODPIS	
Projektant		[DO UZUPEŁNIENIA]		[DO UZUPEŁNIENIA]			
Projektant (wsp.)		[DO UZUPEŁNIENIA]		[DO UZUPEŁNIENIA]			
Sprawdzający		nie dotyczy (art. 20 ust. 3 pkt 2 PB)		—			
Opracował		[DO UZUPEŁNIENIA]		[DO UZUPEŁNIENIA]			
TYTUŁ RYSUNKU ZBROJENIE NADPROŻY (3)							
SKALA 1:25		FORMAT 420x530	DATA WYDANIA 2026-09-25	RODZAJ DOK. rysunek zbrojenia	NR RYSUNKU PT-BO-25	ARKUSZ 25/27	REW. 0