


MAPA DO CELÓW PROJEKTOWYCH — PODKŁAD PRZYKŁADOWY

PODKŁAD PRZYKŁADOWY — mapa do celów projektowych fikcyjna [DANE PRZYKŁADOWE – FIKCYJNE], narysowana z modelu działki (działka.yaml); w projekcie rzeczywistym — aktualna mapa do celów projektowych wg art. 34 ust. 3 pkt 1 PB (z klauzulą urzędową lub oświadczeniem geodety — art. 34b PB), treść i opis mapy wg § 32–33 rozp. w sprawie standardów technicznych (t.j. Dz.U. 2022 poz. 1670), znaki wg zał. 4 rozp. w sprawie BDOT500 i mapy zasadniczej (Dz.U. 2021 poz. 1385; oba akty zweryfikowane w ELI 25.09.2026 — status: obowiązujące).

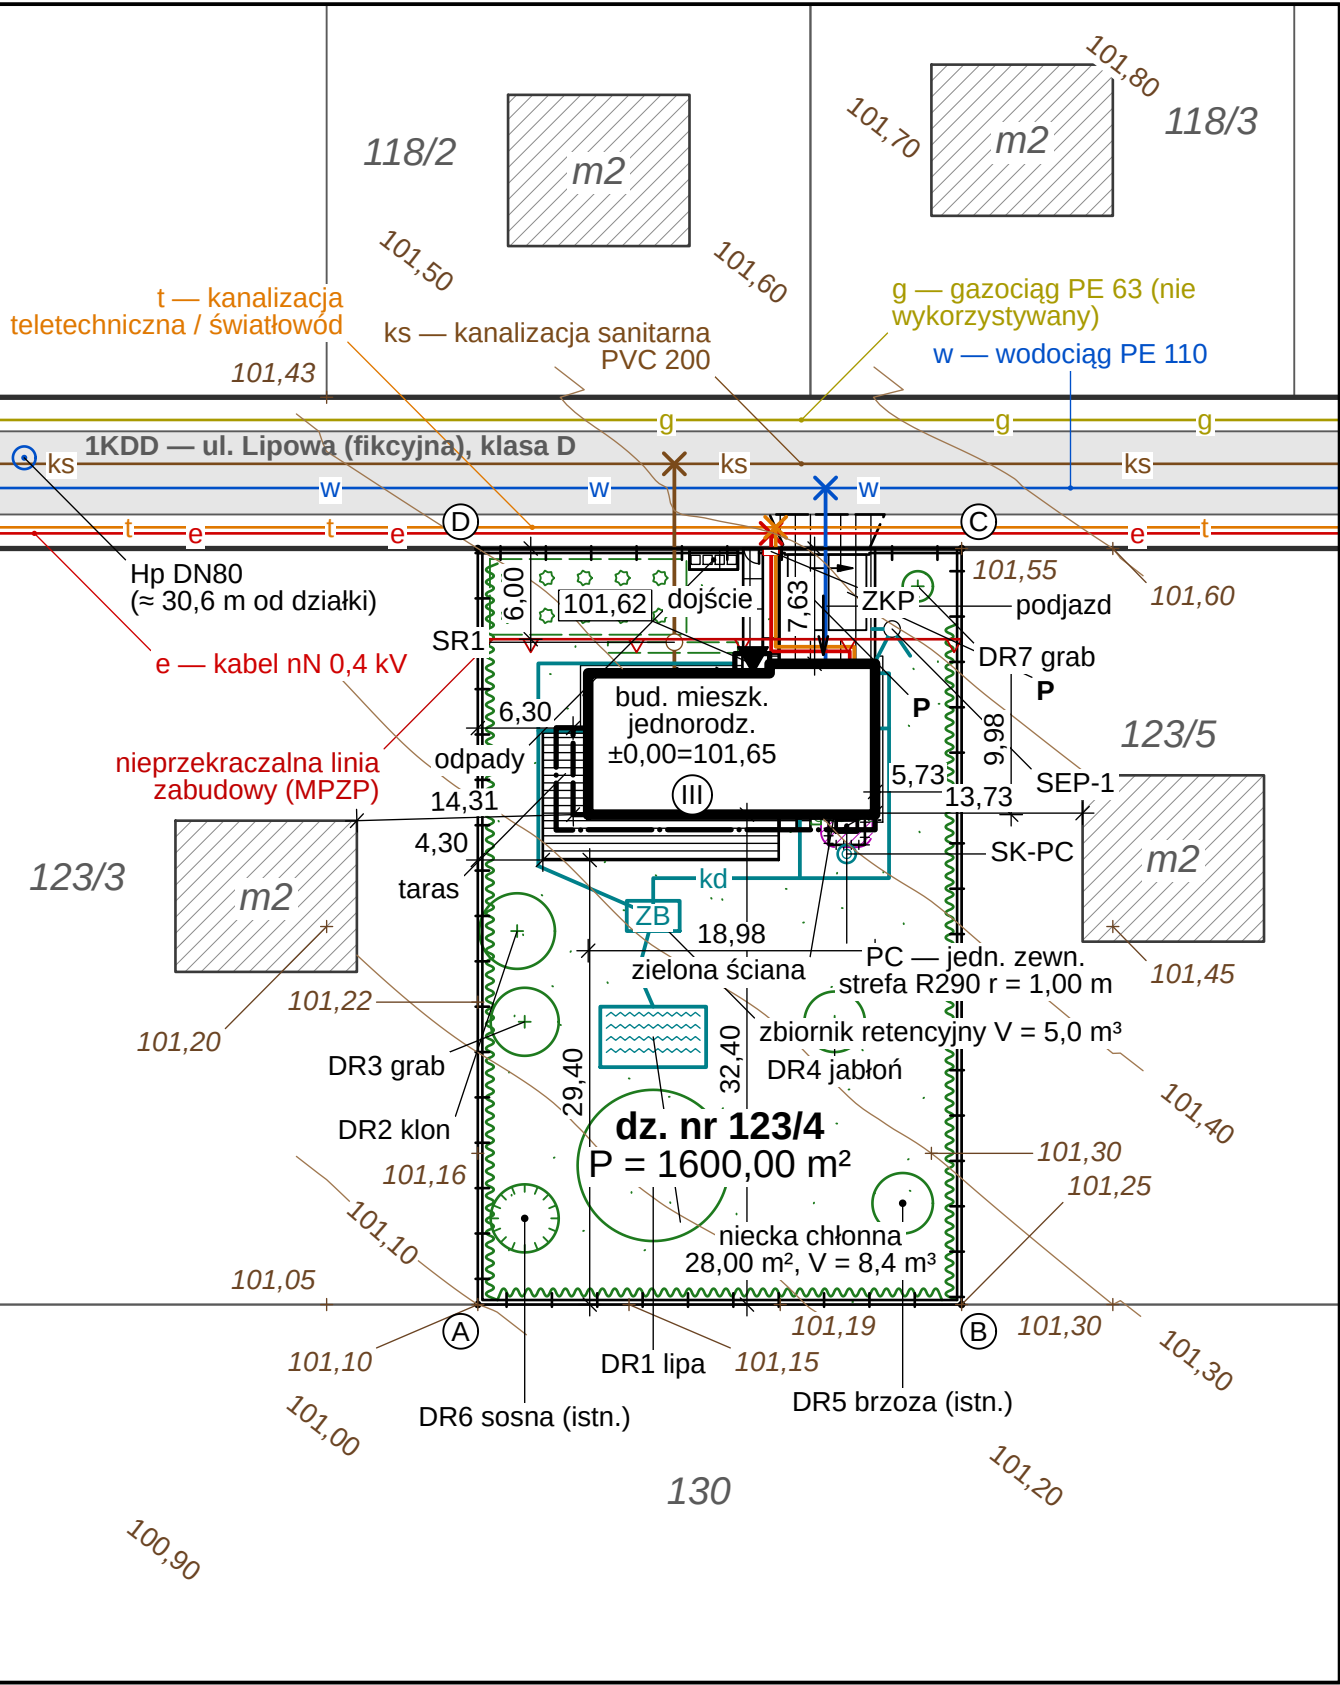

PLAN ZAGOSPODAROWANIA DZIAŁKI 1:500

LEGENDA

- zasięg podkładu mapowego (mapa do celów projektowych — PRZYKŁADOWA)

granicza działki budowlanej, punkt graniczny, narożnik (PN-B-01027 poz. 2.7)

linia rozgraniczająca drogi publicznej (PN-B-01027 poz. 2.5)

jezdnia drogi publicznej (wg mapy)

budynek istniejący (mapa); m2 — mieszkalny, 2 kondygnacje

nieprzekraczalna linia zabudowy wg MPZP (PN-B-01027 poz. 2.2)

budynek projektowany — obrys ścian parteru 1,0 m nad terenem (poz. 1.1)

obrys wyższych kondygnacji poza obrysem parteru (poz. 1.6 d)

obrys płyt wspornikowych, okapów i daszku — przewieszenia (poz. 1.6 c)

±0,00=101,65

rzędna ±0,00 (posadzka parteru) w m n.p.m.; w kółku liczba kondygnacji nadziemnych

wejście główne do budynku (poz. 1.7)

wjazd do garażu

zjazd z drogi publicznej — wg zezwolenia zarządcy drogi [DO UZUPEŁNIENIA]

nawierzchnia z kostki betonowej (poz. 7.10)

nawierzchnia z płyt betonowych (poz. 7.11)

płyty w trawie (ażur) — poza PBC

taras naziemny — deska kompozytowa na legarach

opaska żwirowa 16/32 na geowłókninie

stanowisko postojowe 2,50 × 5,00 m (WT § 21)

osłona pojemników na odpady — segregacja (WT § 22)

trawnik projektowany (poz. 7.8)

rabata z krzewami

żywiopłot projektowany (poz. 7.6)

drzewo liściaste projektowane (poz. 7.1)

drzewo istniejące — zachowane (poz. 7.2)

ogrodzenie projektowane (poz. 2.8; na granicy — odsunięte granicznie)
- brama przesuwna (poz. 2.9)
- furtka otwierana do wewnątrz działki (WT § 42)
- jednostka zewn. pompy ciepła (fundament) i strefa czynnika R290
- ażurowa osłona z lamel jednostki PC (bez dachu, prześwit przy terenie)
- zielona ściana — pnącza na kratownicy stalowej odsuniętej od elewacji
- zbiornik retencyjny szczelny (ZB)
- niecka chłonna — ogród deszczowy (przelew zbiornika)
- miejsce włączenia przyłącza do sieci (PN-B-01027 poz. 6)
- złącze kablowo-pomiarowe ZKP (w linii ogrodzenia)
- studzienka rewizyjna kanalizacji
- studnia chłonna skroplin pompy ciepła
- hydrant zewnętrzny na sieci (Hp)
- warstwa terenu istniejącego (PN-B-01027 poz. 5.2)
- rzędna terenu istniejącego [m n.p.m.]
- rzędna terenu projektowanego [m n.p.m.]
- wymiar / odległość w m z dokładnością 0,01 m
- w — sieć wodociągowa istniejąca (mapa)
- w — przyłącze wodociągowe projektowane
- ks — sieć kanalizacji sanitarnej istniejąca (mapa)
- ks — przykanalik sanitarny projektowany
- kd — kanalizacja deszczowa projektowana (kolektory, przelewy)
- e — linia kablowa nN istniejąca (mapa)
- e — kabel nN projektowany (ZKP → RG)
- t — sieć telekomunikacyjna istniejąca (mapa)
- t — przyłącze telekomunikacyjne projektowane
- g — sieć gazowa istniejąca (mapa)

ZESTAWIENIE POWIERZCHNI I WSKAŹNIKÓW ZAGOSPODAROWANIA (RPB § 14 pkt 4, MPZP)

Wskaźnik / element	Projekt	MPZP / wymaganie	Zgodność
Powierzchnia działki nr 123/4	1600,00 m ²	—	
Pow. zabudowy (upzp art. 2 pkt 35)	187,50 m ²	≤ 480,00 m ²	TAK
Udział pow. zabudowy	11,72%	≤ 30%	TAK
— z płytami i okapami (kontrolnie)	218,08 m ² (13,63%)	informacyjnie	TAK
Drogi, dojścia, place	64,87 m ²	—	
Tarasы naziemne, podesty	66,62 m ²	—	
Opaska żwirowa	13,38 m ²	—	
PBC (upzp art. 2 pkt 28)	1270,23 m ² (79,39%)	≥ 800,00 m ² (50%)	TAK
— z 50 % dachu ziel. D4 (rezerwa)	1299,76 m ² (81,24%)	informacyjnie	
Pow. kondygnacji nadz. (P0+P1+P2)	396,39 m ²	80,00 m ² –1280,00 m ²	TAK
Nadziemna intensywność zabudowy	0,248	0,05–0,80	TAK
Wysokość zabudowy (art. 2 pkt 30)	10,47 m	≤ 11,00 m	TAK
Wysokość budynku (WT § 6)	9,97 m	N: ≤ 12,00 m	TAK
Kondygnacje nadziemne	3	≤ 3	TAK
Miejsca postojowe (garaż + zewn.)	2 + 2	≥ 2	TAK
Dach — kąt nachylenia	1,1° (płaski)	płaski ≤ 12° lub 30–45°	TAK
Lico ścian od linii zabudowy	1,63 m	nie przekraczać	TAK
Elementy poza linią zabudowy	brak	—	

MPZP: uchwała nr XII/123/2024 Rady Gminy Przykładowo z 21.03.2024 — teren 3MN (fikcyjny). Limity: ustalenia MPZP przyjęte w projekcie (dane przykładowe) — wypis i wyrys z MPZP [DO UZUPEŁNIENIA]. Wartości z modułu lamela.wskazniki (jedyne źródło; definicje upzp art. 2 pkt 28–35, t.j. Dz.U. 2026 poz. 538): PBC bez nawierzchni ażurowych, opaski, pojemników i terenu nad zbiornikiem; dach zielony (≥ 10 m²) w 50 % — tylko rezerwa.

Wysokość zabudowy = z_top 111,85 (wyrzutnia wentylacji (dachowa, szczyt urządzenia)) – t_śr 101,38 (t_min 101,29, t_max 101,48 na obwodzie rzutu ścian zewn.; w każdym punkcie niższa z rzędnych terenu istniejącego/projektowanego).

WT § 6: od terenu przy wejściu O0-03 (101,30) do wierzchu stropodachu D1 (bez attyki) — grupa N.

ODLEGŁOŚCI OD GRANIC DZIAŁKI (WT § 12)

Granica	Element (płaszczyzna ściany)	Odl. [m]	Wymagana [m]	Zgodność
S (130)	ściana P0 z otworami	32,40	≥ 4,00	TAK
S (130)	T1 — okap/płyta/taras	29,40	≥ 1,50	TAK
E (123/5)	ściana P0 z otworami	5,73	≥ 4,00	TAK
E (123/5)	ściana P2 bez otworów	15,60	≥ 3,00	TAK
E (123/5)	PL-D — okap/płyta/taras	5,73	≥ 1,50	TAK
N (1KDD)	ściana P0 z otworami	7,63	nie dot. (ust. 10)	—
N (1KDD)	ściana P2 bez otworów	11,88	nie dot. (ust. 10)	—
N (1KDD)	PL-DA — okap/płyta/taras	6,95	nie dot. (ust. 10)	—
W (123/3)	ściana P2 z otworami	6,30	≥ 4,00	TAK
W (123/3)	ściana P2 bez otworów	11,18	≥ 3,00	TAK
W (123/3)	T1 — okap/płyta/taras	4,30	≥ 1,50	TAK



WT § 12 ust. 1: 4,00 m — ściana z oknami/drzwiami, 3,00 m — bez otworów (każda płaszczyzna ściany osobno); ust. 6: 1,50 m — okap, taras, daszek; ust. 10: od działki drogowej — nie dotyczy. Odległość w poziomie w miejscu najmniejszego oddalenia (§ 9). WT stosowane na podstawie art. 102a PB.

OBSZAR ODDZIAŁ YWANIA OBIEKTU (PB art. 3 pkt 20; RPB § 14 pkt 8)

Obszar oddziaływania obiektu mieści się w całości w granicach działki 123/4 (PB art. 3 pkt 20): odległości od granic ≥ 4,0 m (ściany z otworami ≥ 5,70 m, płyty ≥ 5,20 m), przesłanianie i nasłonecznienie sąsiednich budynków (≥ 8 m od granicy) bez ograniczeń (WT §13, §60), hałas PC ≤ 40 dB(A) nocą na granicy (W-024), wody opadowe zagospodarowane na działce (PW art. 234), brak odprowadzania na drogę. Podstawa ustalenia (RPB § 18 pkt 1): WT § 12, 13, 19, 23, 28–29, 60, 271 (art. 102a PB); u.d.p. art. 43; POŚ art. 144 ust. 2 i rozp. MŚ w sprawie dopuszczalnych poziomów hałasu (Dz.U. 2014 poz. 112); PW art. 234; ustalenia MPZP.

OBJAŚNIENIA I UWAGI

- Wymiary i odległości w m (dokładność 0,01 m), rzędne w m n.p.m. (PL-EVRF2007-NH).
- Układ współrzędnych: lokalny układ działki (x → wschód, y → północ, początek w narożniku A); w projekcie rzeczywistym — układ PL-2000 strefa 6 z mapy do celów projektowych.
- Obrys budynku — lico zewnętrzne ścian parteru na wys. 1,0 m nad terenem; wspornik bryły A (II piętro) — obrys wyższych kondygnacji; płyty wspornikowe, okapy i daszek — przewieszenia (PN-B-01027 poz. 1.6).
- Wody opadowe zagospodarowane w granicach działki: rury spustowe → kolektory KD → zbiornik retencyjny szczelny → przelew do niecki chłonnej; odwodnienie liniowe przed bramą — brak wpływu na drogę (MPZP; u.d.p. art. 39 ust. 1 pkt 9; WT § 28–29).
- Wymiary i rzędne szczegółowe — rys. PZT-02; uzbrojenie i koordynacja sieci — rys. PZT-03.
- Zjazd z drogi 1KDD pokazano jako przedłużenie bramy do krawędzi jezdni — geometria zastępcza [DO UZUPEŁNIENIA]; szerokość, skosy/luki, nawierzchnia i przepust wg zezwolenia zarządcy drogi (u.d.p. art. 29 ust. 3a).
- Braki danych modelu (6 poz.) oznaczono [DO UZUPEŁNIENIA]; wykaz: projekt/02_PZT/BRAKI_DANYCH.md.
- Rysunek wygenerowany automatycznie z modelu model/budynek.yaml (wersja 1.0, 2026-09-25) — generatory lamela.views.

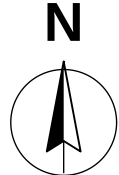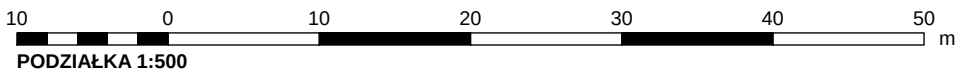

REW.	OPIS ZMIANY			DATA
0	Wydanie — rysunek wygenerowany z modelu			2026-09-25
PRACOWNIA PROJEKTOWA PRACOWNIA PROJEKTOWA — nazwa do uzupełnienia adres pracowni do uzupełnienia			STADIUM PB	BRANŻA ZAGOSPODAROWANIE TERENU
INWESTOR (do uzupełnienia)				
OBIEKT / NAZWA ZAMIERZENIA BUDOWLANEGO Budynek mieszkalny jednorodzinny wolnostojący „Dom LAMELA” z zagospodarowaniem działki				
ADRES / LOKALIZACJA (NR DZIAŁKI, OBRĘB, JEDN. EWIDENCYJNA) ul. Lipowa (fikcyjna), dz. nr ewid. 123/4, obręb 0005 Przykładowo, gm. Przykładowo (fikcyjna)				KAT. OBIEKTU I
FUNKCJA	IMIĘ I NAZWISKO	SPECJALNOŚĆ, NR UPRAWNIENI	DATA	PODPIS
Projektant	[DO UZUPEŁNIENIA]	[DO UZUPEŁNIENIA]		
Projektant (wsp.)	[DO UZUPEŁNIENIA]	[DO UZUPEŁNIENIA]		
Sprawdzający	nie dotyczy (art. 20 ust. 3 pkt 2 PB)	—		
Opracował	[DO UZUPEŁNIENIA]	[DO UZUPEŁNIENIA]		
TYTUŁ RYSUNKU PLAN ZAGOSPODAROWANIA DZIAŁKI				
SKALA 1:500	FORMAT A2	DATA WYDANIA 2026-09-25	RODZAJ DOK. plan zagospodarowania	NR RYSUNKU PZT-01
			ARKUSZ 1/3	REW. 0