


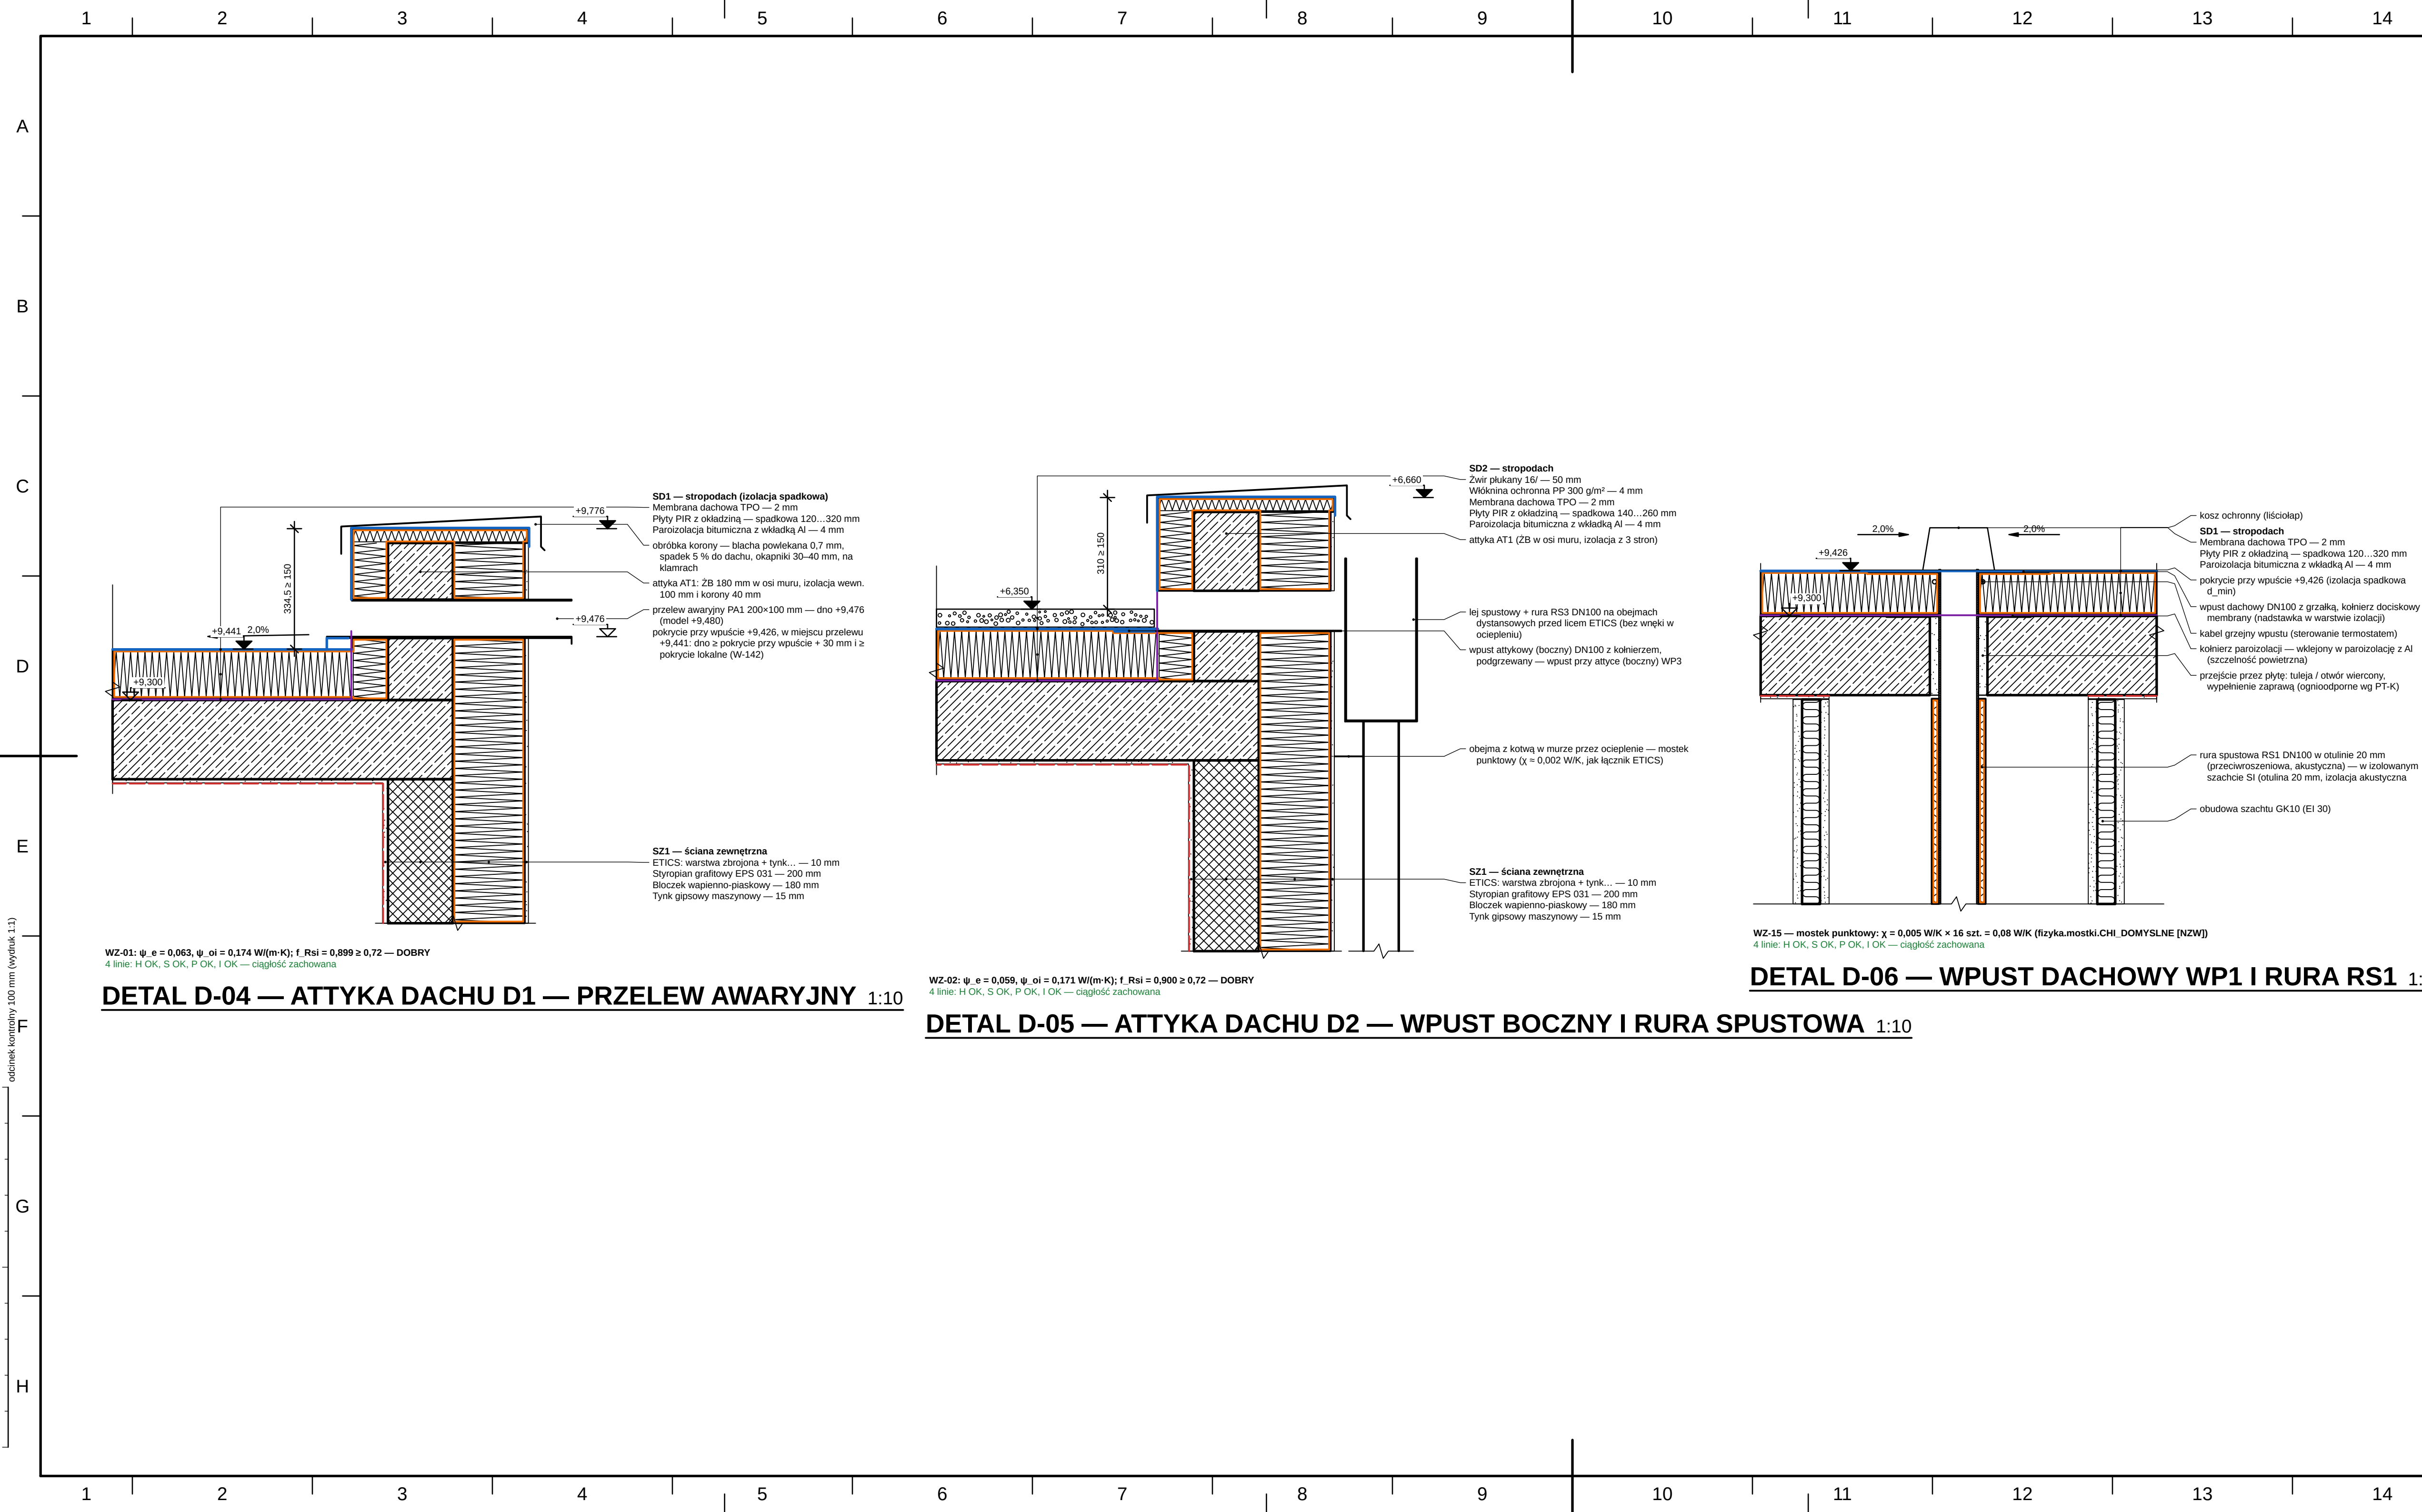

OZNACZENIA MATERIAŁÓW (PN-B-01030 + przyjęte)

 Otulina izolacyjna 20 mm (kauczuk / PE), akustyczna; Wełna mineralna 035 (szkielet, dociepniecia, dach od-garaż)	 Przelew awaryjny – króciec prostokąty ze stali nierdzewnej z kołnierzem; Rura spustowa DN100 / le; ze stali powlekana lub z tworzywa
 Płyty PIR z okładziną (izolacja spadkowa stropodachów) – zysk z okładzinami	 Wypust dachowy PP/PUR z kołnierzem i grzałką
 Syropian grzałkowy EPS 031 (ETICS, NRC w systemie) – zysk z wtyczkami	 Tynk gipsowy maszynowy 1,5 cm; ETICS: warstwa zbrojona + tynk silikonowy 1,5 cm (biały / jasnoniebieski NC S 120); Zaprawa / masa wypełniająca przejście w całość – kropli nierégulujące
 Blozcek wapienno-piaskowy (silikat) 18 cm, kl. 20, gr. 1, na zaprawie cienkowarstwowej – kratka okucowa 45/135"	 Żelbet C25/S0, B50/S0P (stropy, płyta fundamentowa, ściany); Żelbet C30/37 XC4/Xf1 (krzewidze płyt wysuniętych, atyki, belki) – 45" na przemięć gładki / przerywany
 Płyta gipsowa-kartonowa 12,5 mm (GKB / GKBI w faziankach)	 Zwrz płukany 16/32 mm (balast dachu P1, opaska przy atyce)

ZASADA „4 LINII” I OZNACZENIA DETALI

- hydroizolacja / izolacja przeciwwodna i przeciwiogłowa (ochrona przed wodą)
- - - - - hydroizolacja / izolacja powietrznej (tylny wiew, płyta ŻB, OSB, membrana, taśmy)
- paraizolacja / kontrola pary (folia, papa z Al, membrana sd 10 m)
- ▭ izolacja ciepła — obrys ciałej warstwy izolacji (test „ołówka”)
- taśma paroszczelna (od wewnątrz — ciepły montaż)
- taśma paroprzepuszczalna / uszczelnienie zewnętrzne (ciepły montaż, próg)
- — — — — membrana wiatroizolacyjna paroprzepuszczalna
- - - - - geowłókna, bariera przeciwiokrzenna, maty drenażowa
- ▬ obróbka blacharska z okapnikiem (kapinoszem), niena ukryta

WYNIKI MOSTKÓW (PN-EN ISO 10211) I OCENA 4 LINII

D-04: WZ-01: $\psi_e = 0,063$, $\psi_{oi} = 0,174$ W/(m·K); $f_{Rsi} = 0,899 \geq 0,72$ — DOBRY

4 linie: H OK, S OK, P OK, I OK — ciągłość zachowana

D-05: WZ-02: $\psi_e = 0,059$, $\psi_{oi} = 0,171$ W/(m·K); $f_{Rsi} = 0,900 \geq 0,72$ — DOBRY

4 linie: H OK, S OK, P OK, I OK — ciagłość zachowana

D-06: WZ-15 — mostek punktowy: $\chi = 0,005 \text{ W/K} \times 16 \text{ szt.} = 0,08 \text{ W/K}$ (fizyka.mostki.CHI_DOMYSLNE [NZW])

4 linie: H OK, S OK, P OK, I OK — ciągłość zachowana

OBJAŚNIENIA I UWAGI

1. Wymiary w mm, rzędne w mm względem $\pm 0,000 \pm 101,650$ mm (PL-EVPR7007-NH).
2. Kreskowania materiałów wg PN-B-01030-2000 (aktualna) i PN-EN ISO 128-3:2023-02 (zastąpiła wycofane PN-ISO 128-50:2006); oznaczenia sposobu normy – w legendzie arkusza.
3. Opisy warstw od zewnętrzna do wewnątrz (kolejność kropek na linii odnośnika = kolejność wierszy), grubości w mm wg przegród modelu (kontrola zgodności – raport modelu detal).
4. Zasada: 1. linia (bref 9:R-1): hydroizolacja – niebieska, szczelność powietrzna – czerwona przerywana, paroizolacja – fioletowa, izolacja cieplna – obrys pomarańczowy; każda linia ciąga włókno kaburaty owrzęzaną.
5. Wytnijnia hydroizolacji z 15 cm ponad warstwę wierzchnią (zwł. substrat, nawierzchnia) – Wytyczne DAFa dla dachów płaskich; DIN 18531 (pomocznicy); PN-EN 1991 wszystkie wytnięcie nie określa. Kształt uszczelnienie z 30 cm nad brzołem (bref 9:R-4; DIN 18533-1 – pomocznicy) albo odwołanie liniozary przy drzwiach bezprogowych.
6. Wytychy bieżnik termozimocizny, taśmy, profile progowe, konsle) – dane przykładowe *Wg równoznaczniki*; parametry (ETA/DWU) do potwierdzenia przed realizacją.
7. Detal D-4: rzędne przelewów awaryjnych D1: dno = pokrycie przy wpudzie + 0.03...0.05 m, nie niżej niż pokrycie lokoła (tabela R-W2 wg REKOMENDACJEI mstów); wytnijnia z 15 cm ponad warstwę wierzchnią (DAFA).
8. Detal D-5: dach D2: przelew awaryjny przelew P4a w atyce (poda przekrojem, rozwiązanie jak detal D-4a); rura spusztowa do kolektora KD – zbiornik retencyjny (Detal D-07).
9. detal D-6: wyspu i przelew instalacji przed przegrody wentylacyjne – mostki punktowe (X WZ-15, wentylatory typowe); kolnierze paroizolacji i hydroizolacji wpustu – ciągłość 4 lini.
10. Rysunek wygenerowany automatycznie z modelu modelu/budynku.nam (wersja 1.0, 2026-09-25) – gwarantujemy lamela.wiews.



REW.	OPIS ZMIANY				DATA	
0	Wydanie — rysunek wygenerowany z modelu				2026-09-25	
PRACOWNIA PROJEKTOWA PRACOWNIA PROJEKTOWA — nazwa do uzupełnienia adres pracowni do uzupełnienia				STADIUM PT	BRANŻA ARCHITEKTURA (AR)	
INWESTOR (do uzupełnienia)						
OBJEKT / NAZWA ZAMIERZENIA BUDOWLANEGO						
Budynek mieszkalny jednorodzinny wolnostojący „Dom LAMELA”						
ADRES / LOKALIZACJA (NR DZIAŁKI, OBREB, JEDN. EWIDENCYJNA) ul. Lipowa (fikcyjna), dz. nr ewid. 123/4, obręb 0005 Przykładowo, gm. Przykładowo (fikcyjna)					KAT. OBJEKTU I	
FUNKCJA	IMIĘ I NAZWISKO		SPECJALNOŚĆ, NR UPRAWNIENI		DATA	PODPIS
Projektant						
Projektant (wsp.)						
Sprawdzający						
Opracował						
TYTUŁ RYSUNKU						
DETALE — ATTYKI, WPUSTY, PRZELEW AWARYJNY						
SKALA 1:10	FORMAT A3x3	DATA WYDANIA 2026-09-25	RODZAJ DOK. detail	NR RYSUNKU PT-AR-D-03	ARKUSZ 3/6	REW. 0