

# PROJEKT ZAGOSPODAROWANIA DZIAŁKI — CZĘŚĆ


| Lp. | Nr rys. | Tytuł rysunku                           | Skala | Format |
|-----|---------|-----------------------------------------|-------|--------|
| 1   | PZT-01  | PLAN ZAGOSPODAROWANIA DZIAŁKI           | 1:500 | A2     |
| 2   | PZT-02  | PLAN SZCZEGÓŁOWY — WYMIARY I RZĘDNE     | 1:200 | A2     |
| 3   | PZT-03  | RYSUNEK KOORDYNACYJNY UZBROJENIA TERENU | 1:200 | A2     |

|   |                 |                            |                                          |                             |             |      |
|---|-----------------|----------------------------|------------------------------------------|-----------------------------|-------------|------|
| PRACOWNIA PROJEKTOWA<br><b>PRACOWNIA PROJEKTOWA — nazwa do uzupełnienia</b>                                                                                 |                 | STADIUM<br><b>PB</b>       | BRANŻA<br><b>ZAGOSPODAROWANIE TERENU</b> |                             |             |      |
| INWESTOR<br>(do uzupełnienia)   |                 |                            |                                          |                             |             |      |
| OBIEKT / NAZWA ZAMIERZENIA BUDOWLANEGO<br><b>Budynek mieszkalny jednorodzinny wolnostojący „Dom LAMELA” z zagospodarowaniem działki</b>                     |                 |                            |                                          |                             |             |      |
| ADRES / LOKALIZACJA (NR DZIAŁKI, OBRĘB, JEDN. EWIDENCYJNA)<br>ul. Lipowa (fikcyjna), dz. nr ewid. 123/4, obręb 0005 Przykładowo, gm. Przykładowo (fikcyjna) |                 |                            |                                          | KAT. OBIEKTU<br><b>I</b>    |             |      |
| FUNKCJA   | IMIĘ I NAZWISKO | SPECJALNOŚĆ, NR UPRAWNIENI | DATA                                     | PODPIS                      |             |      |
| Projektant   |                 |                            |                                          |                             |             |      |
| Projektant (wsp.)   |                 |                            |                                          |                             |             |      |
| Sprawdzający   |                 |                            |                                          |                             |             |      |
| Opracował   |                 |                            |                                          |                             |             |      |
| TYTUŁ RYSUNKU<br><b>SPIS RYSUNKÓW</b>   |                 |                            |                                          |                             |             |      |
| SKALA<br>—   | FORMAT<br>A4    | DATA WYDANIA<br>2026-09-25 | RODZAJ DOK.<br>spis                      | NR RYSUNKU<br><b>PZT-00</b> | ARKUSZ<br>— | REW. |



A  
B  
C  
D  
E  
F  
G  
H

odcinek kontrolny 100 mm (wydruk 1:1)

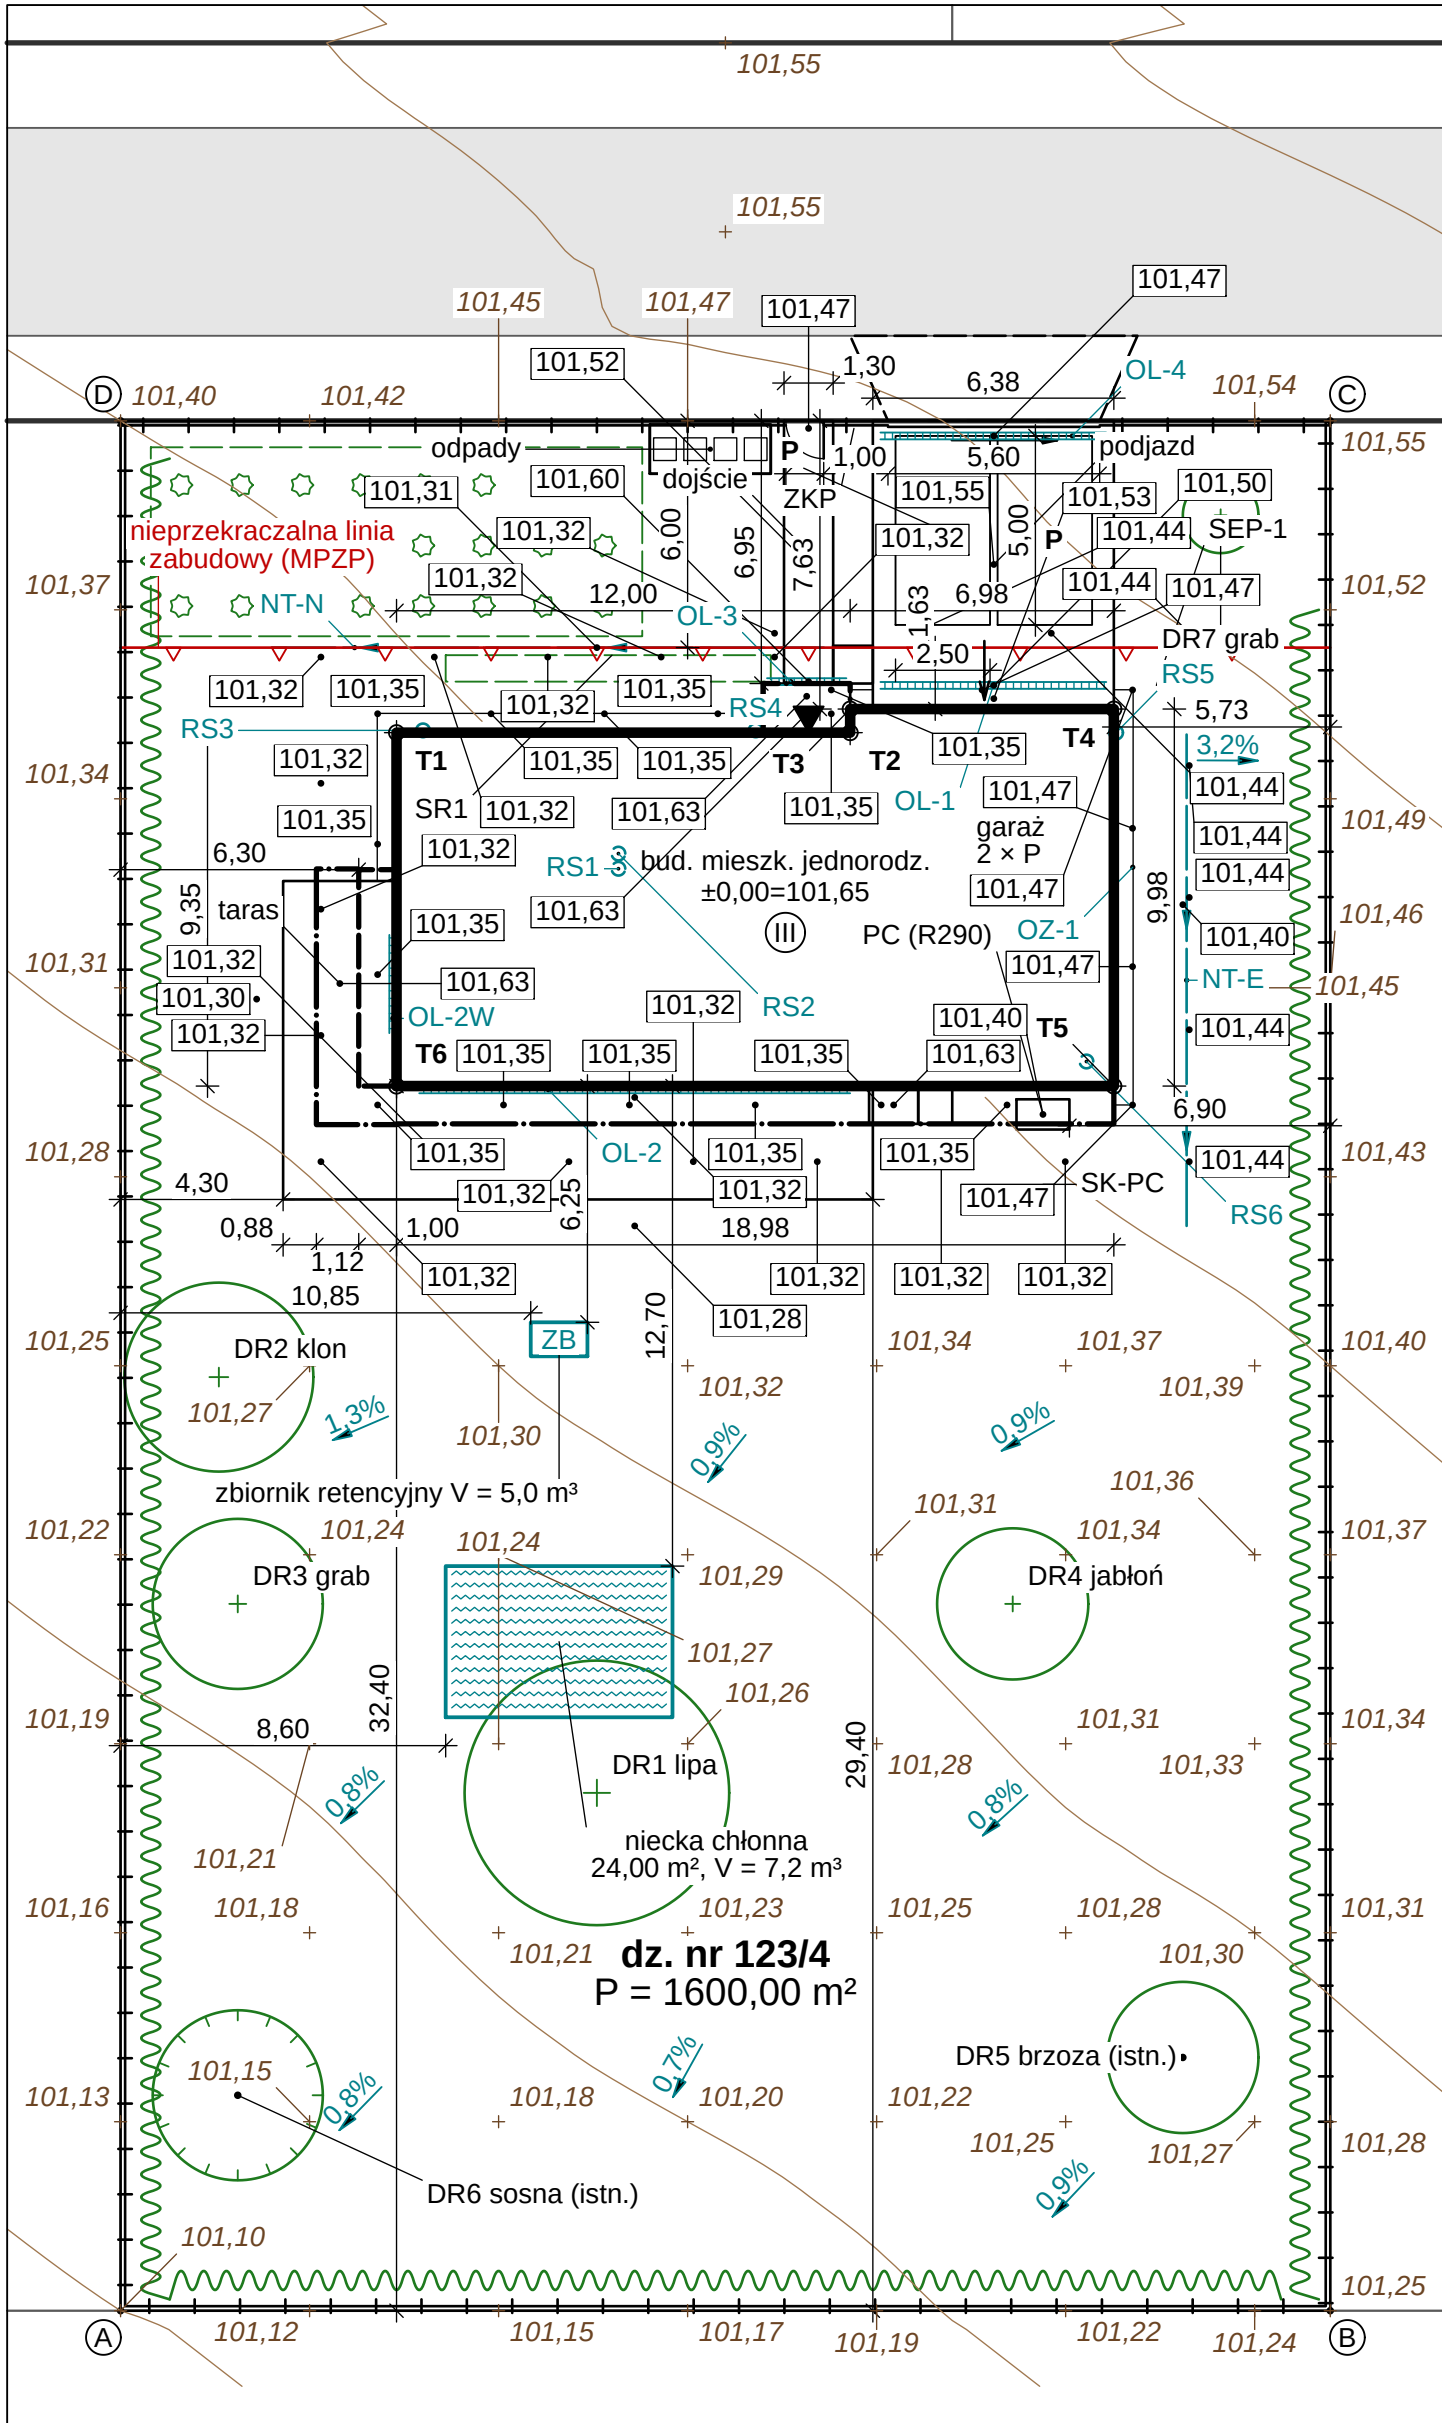

PLAN SZCZEGÓŁOWY — WYMIARY I RZĘDNE 1:200

### WYKAZ PUNKTÓW TYCZENIA I GRANICZNYCH

| Pkt | x [m] | y [m] | Opis                    |
|-----|-------|-------|-------------------------|
| T1  | 7,30  | 41,75 | narożnik obrysu parteru |
| T2  | 19,30 | 41,75 | narożnik obrysu parteru |
| T3  | 19,30 | 42,38 | narożnik obrysu parteru |
| T4  | 26,28 | 42,38 | narożnik obrysu parteru |
| T5  | 26,28 | 32,40 | narożnik obrysu parteru |
| T6  | 7,30  | 32,40 | narożnik obrysu parteru |
| A   | 0,00  | 0,00  | punkt graniczny działki |
| B   | 32,00 | 0,00  | punkt graniczny działki |
| C   | 32,00 | 50,00 | punkt graniczny działki |
| D   | 0,00  | 50,00 | punkt graniczny działki |

Układ lokalny działki: początek — narożnik A, x → wschód, y → północ. W projekcie rzeczywistym współrzędne w układzie PL-2000 (X — północ, Y — wschód) z mapy do celów projektowych; tyczenie — geodeta uprawniony (PB art. 43 ust. 1).

### RZĘDNE CHARAKTERYSTYCZNE [m n.p.m.]

| Poziom                           | Rzędna |
|----------------------------------|--------|
| ±0,00 — posadzka parteru         | 101,65 |
| T1 — deska kompozytowa...        | 101,63 |
| T2 — płyty betonowe 60...        | 101,63 |
| T3 — płyty betonowe 60...        | 101,63 |
| teren proj. przy wejściu głównym | 101,63 |
| teren na obwodzie ścian — min.   | 101,32 |
| teren na obwodzie ścian — maks.  | 101,48 |
| najwyższy punkt budynku          | 111,68 |
| zwierciadło wody gruntowej (ZWG) | 97,60  |

Rzędne projektowane terenu: spadek  $\geq 2\%$  od budynku; na granicach działki rzędne istniejące (bez zmiany spływu na działki sąsiednie — WT § 29, PW art. 234).

### ODWODNIENIE POWIERZCHNIOWE

| Ozn.  | Typ          | Wymiar                   | Spadek | Odbiornik             |
|-------|--------------|--------------------------|--------|-----------------------|
| OL-1  | liniowe      | L = 5,98 m               | 0,5 %  | SEP-1 → NT-E          |
| OL-2  | liniowe      | L = 11,40 m              | 0,5 %  | opaska / KD-W         |
| OL-2W | liniowe      | L = 2,60 m               | 0,5 %  | KD-W                  |
| OL-3  | liniowe      | L = 2,10 m               | 0,5 %  | KD-W                  |
| OL-4  | liniowe      | L = 5,98 m               | 0,5 %  | SEP-1 → NT-E          |
| OZ-1  | opaska żwir. | b = 0,50 m               | —      | —                     |
| NT-N  | niecka       | L = 14,60 m              | 0,5 %  | KD-W                  |
| NT-E  | niecka       | L = 13,00 m              | 0,6 %  | ogród pd.             |
| NCH-1 | niecka       | A = 24,00 m <sup>2</sup> | —      | grunt (piaski, ZWG... |

DR-0: NIE PROJEKTUJE SIĘ — piaski przepuszczalne, ZWG  $\approx 3,8$  m p.p.t., posadowienie  $\approx 0,5$  m p.p.t. (W-285); ochrona płyty: XPS + membrana SBS, opaska żwirowa i spadki terenu

### ODLEGŁOŚCI URZĄDZEŃ RETENCJI I PC

| Element     | Od                         | d [m] | min [m]  | Zgodność |
|-------------|----------------------------|-------|----------|----------|
| zbiornik    | budynek                    | 6,70  | 3,00     | TAK      |
| zbiornik    | granica                    | 11,60 | 2,00     | TAK      |
| zbiornik    | drzewo                     | 9,06  | 1,00     | TAK      |
| niecka      | budynek                    | 12,70 | 3,00     | TAK      |
| niecka      | granica                    | 8,60  | 2,00     | TAK      |
| niecka      | drzewo                     | 2,00  | 1,00     | TAK      |
| strefa R290 | otwory, wpusty, studzienki | —     | r = 1,00 | TAK      |


Wymagania retencji — założenia projektowe (R8 pkt 3.5, W-144/W-145; nie przepis); zbiornik — odległość od środka (brak wymiarów w modelu); strefa R290 — W-156 (wytyczne producenta).

### LEGENDA


|  |                                                                       |
|--|-----------------------------------------------------------------------|
|  | rabata z krzewami                                                     |
|  | żywoplot projektowany (poz. 7.6)                                      |
|  | drzewo liściaste projektowane (poz. 7.1)                              |
|  | drzewo istniejące — zachowane (poz. 7.2)                              |
|  | ogrodzenie projektowane (poz. 2.8; na granicy — odsunięte graficznie) |
|  | brama przesuwana (poz. 2.9)                                           |
|  | furtka otwierana do wewnątrz działki (WT § 42)                        |
|  | zbiornik retencyjny szczelny (ZB)                                     |
|  | niecka chłonna — ogród deszczowy (przelew zbiornika)                  |
|  | odwodnienie liniowe                                                   |
|  | niecka trawiasta — grot w kierunku spływu                             |
|  | rura spustowa: zewnętrzna / w szachcie (RS)                           |
|  | warstwica terenu istniejącego (PN-B-01027 poz. 5.2)                   |
|  | rzędna terenu istniejącego [m n.p.m.]                                 |
|  | rzędna terenu projektowanego [m n.p.m.]                               |
|  | kierunek spływu wód opadowych, spadek terenu [%]                      |
|  | wymiar / odległość w m z dokładnością 0,01 m                          |
|  | punkt tyczenia (narożnik obrysu parteru) — wykaz współrzędnych        |

### OBJAŚNIENIA I UWAGI

- Wymiary i odległości w m (dokładność 0,01 m), rzędne w m n.p.m. (PL-EVRF2007-NH).
- Wymiary obrysu — lico zewnętrzne ścian parteru (1,0 m nad terenem); odległości od granic w miejscu najmniejszego oddalenia (WT § 9), z dokładnością 0,01 m (RPB § 15 ust. 3 w brzmieniu Dz.U. 2026 poz. 597, od 5.11.2026 — stosowane).
- Rzędne terenu istniejącego — z mapy (przykładowej); projektowanego — z modelu (działka.yamli: teren.punkty\_projektowane); spadki nawierzchni wg modelu, kierunek wg terenu projektowanego; kierunki spływu na trawnikach — wg spadku terenu projektowanego (interpolacja).
- Wody opadowe z nawierzchni i dachów — na teren własny, do niecek i zbiornika (WT § 28 ust. 2); zakaz zmiany spływu w kierunku działek sąsiednich (WT § 29) i odprowadzania na drogę (u.d.p. art. 39).
- Punkty tyczenia — narożniki obrysu zewnętrznego ścian parteru; współrzędne w wykazie obok rysunku.
- Zjazd — geometria zastępcza [DO UZUPEŁNIENIA]; wykaz: projekt/02\_PZT/BRAKI\_DANYCH.mdi.
- Braki danych modelu oznaczono [DO UZUPEŁNIENIA]; wykaz: projekt/02\_PZT/BRAKI\_DANYCH.mdi.
- Rysunek wygenerowany automatycznie z modelu /home/user/aihouse/model/budynek.yamli (wersja 1.0, 2026-09-25) — generatory lamela.views.

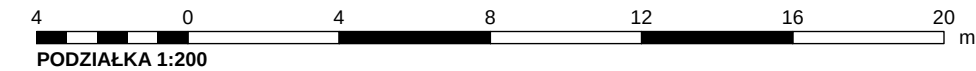

|   |                                         |                            |                                 |                                      |
|---|-----------------------------------------|----------------------------|---------------------------------|--------------------------------------|
| REW.   | OPIS ZMIANY                             |                            |                                 | DATA                                 |
| 0   | Wydanie — rysunek wygenerowany z modelu |                            |                                 | 2026-09-25                           |
| PRACOWNIA PROJEKTOWA<br>PRACOWNIA PROJEKTOWA — nazwa do uzupełnienia<br>adres pracowni do uzupełnienia                                                      |                                         |                            | STADIUM<br>PB                   | BRANŻA<br>ZAGOSPODAROWANIE<br>TERENU |
| INWESTOR<br>(do uzupełnienia)   |                                         |                            |                                 |                                      |
| OBJEKT / NAZWA ZAMIERZENIA BUDOWLANEGO   |                                         |                            |                                 |                                      |
| Budynek mieszkalny jednorodzinny wolnostojący „Dom LAMELA” z zagospodarowaniem działki                                                                      |                                         |                            |                                 |                                      |
| ADRES / LOKALIZACJA (NR DZIAŁKI, OBRĘB, JEDN. EWIDENCYJNA)<br>ul. Lipowa (fikcyjna), dz. nr ewid. 123/4, obręb 0005 Przykładowo, gm. Przykładowo (fikcyjna) |                                         |                            |                                 | KAT. OBIEKTU<br>I                    |
| FUNKCJA   | IMIĘ I NAZWISKO                         | SPECJALNOŚĆ, NR UPRAWNIENI | DATA                            | PODPIS                               |
| Projektant   |                                         |                            |                                 |                                      |
| Projektant (wsp.)   |                                         |                            |                                 |                                      |
| Sprawdzający   |                                         |                            |                                 |                                      |
| Opracował   |                                         |                            |                                 |                                      |
| TYTUŁ RYSUNKU   |                                         |                            |                                 |                                      |
| PLAN SZCZEGÓŁOWY — WYMIARY I RZĘDNE   |                                         |                            |                                 |                                      |
| SKALA<br>1:200   | FORMAT<br>A2                            | DATA WYDANIA<br>2026-09-25 | RODZAJ DOK.<br>plan szczegółowy | NR RYSUNKU<br>PZT-02                 |
|   |                                         |                            | ARKUSZ<br>2/3                   | REW.<br>0                            |

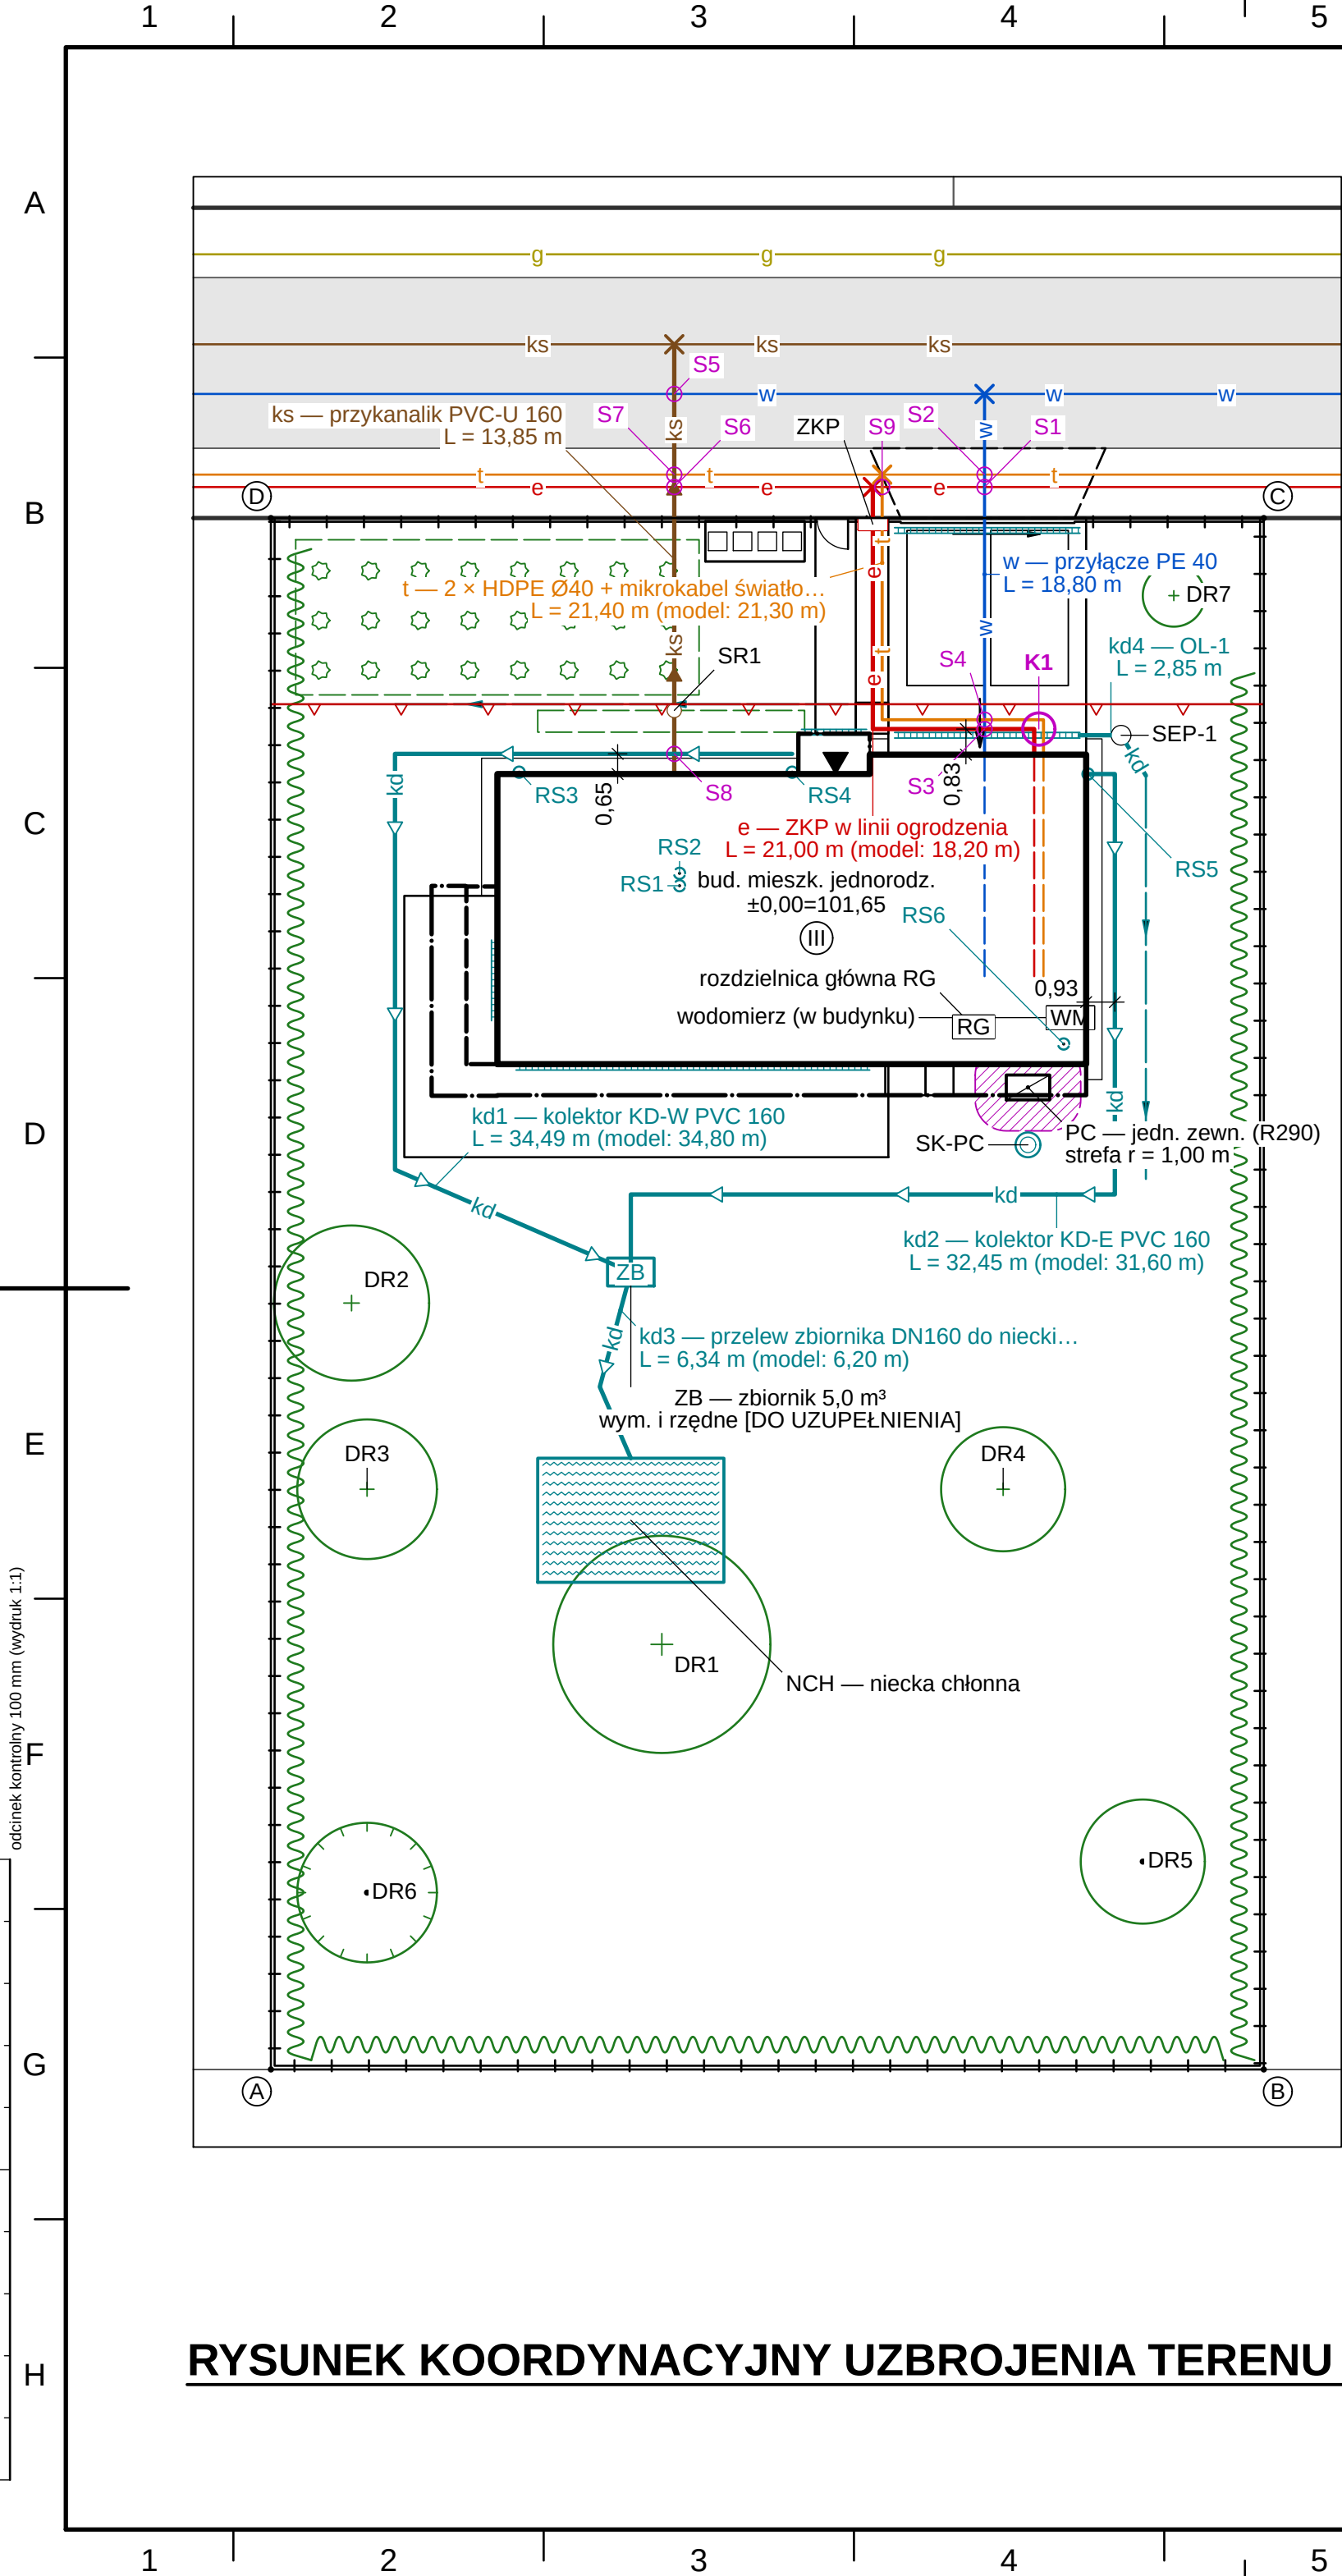

### SIECI I PRZYŁĄCZA — PROJEKTOWANE I ISTNIEJĄCE

| Ozn.    | Sieć                           | Opis                             | L [m] | L model [m] |
|---------|--------------------------------|----------------------------------|-------|-------------|
| w       | przyłłącze wodociągowe         | przyłłącze PE 40                 | 18,80 | 18,80       |
| ks      | kanalizacja sanitarna          | przykanalik PVC-U 160            | 13,85 | 13,90       |
| e       | elektroenergetyczna nN (kabel) | ZKP w linii ogrodzenia           | 21,00 | 18,20       |
| t       | telekomunikacyjna (światłowod) | 2 × HDPE Ø40 + mikrokabel świ... | 21,40 | 21,30       |
| kd1     | kanalizacja deszczowa          | kolektor KD-W PVC 160            | 34,49 | 34,80       |
| kd2     | kanalizacja deszczowa          | kolektor KD-E PVC 160            | 32,45 | 31,60       |
| kd3     | kanalizacja deszczowa          | przelew zbiornika DN160 do ni... | 6,34  | 6,20        |
| kd4     | kanalizacja deszczowa          | OL-1                             | 2,85  | 2,90        |
| w ist.  | istniejąca (mapa)              | wodociąg PE 110                  | —     | —           |
| ks ist. | istniejąca (mapa)              | kanalizacja sanitarna PVC 200    | —     | —           |
| e ist.  | istniejąca (mapa)              | kabel nN 0,4 kV                  | —     | —           |
| t ist.  | istniejąca (mapa)              | kanalizacja teletechniczna /...  | —     | —           |
| g ist.  | istniejąca (mapa)              | gazociąg PE 63 (nie wykorzyst... | —     | —           |

L — długość trasy w rzucie (z częścią pod budynkiem, linia kreskowa); średnice, spadki i rzędne dna przewodów [DO UZUPEŁNIENIA] (RPB § 15 ust. 2 pkt 11 — brak w modelu).

### OBIEKTY UZBROJENIA I ODWODNIENIA

| Ozn.  | Opis                                                   |
|-------|--------------------------------------------------------|
| ZKP   | złącze kablowo-pomiarowe we wnęce ogrodzenia           |
| SR1   | studzienka rewizyjna kanalizacji Ø425                  |
| PC-JZ | jednostka zewn. PC monoblok R290 w osłonie lamelowe... |
| SEP-1 | osadnik z separatorem substancji ropopochodnych        |
| SK-PC | studnia chłonna skroplin PC                            |
| HYDR  | najbliższy hydrant zewnętrzny DN80                     |
| RS1   | rura spustowa DN100 (w szachcie) z dachu D1            |
| RS2   | rura spustowa DN100 (w szachcie) z dachu D1            |
| RS3   | rura spustowa DN100 (zewn.) z dachu D2                 |
| RS4   | rura spustowa DN100 (zewn.) z dachu D3                 |
| RS5   | rura spustowa DN100 (zewn.) z dachu D4                 |
| RS6   | rura spustowa DN100 (w szachcie) z dachu D4            |

### KOORDYNACJA — ODLEGŁOŚCI POZIOME MIĘDZY SIECIAMI

| Para sieci    | d [m] | min [m] | Źródło wymagania                     | Zgodność |
|---------------|-------|---------|--------------------------------------|----------|
| w — ks ist.   | 3,15  | 1,50    | praktyka proj. (COBRTI INSTAL z. 3)* | TAK      |
| w — kd2       | 3,40  | 1,50    | praktyka proj. (COBRTI INSTAL z. 3)* | TAK      |
| w — kd4       | 3,08  | 1,50    | praktyka proj. (COBRTI INSTAL z. 3)* | TAK      |
| e — t ist.    | 1,02  | 0,50    | N SEP-E-004:2014*                    | TAK      |
| e — t         | 0,30  | 0,50    | N SEP-E-004:2014*                    | warunk.  |
| e — kd1       | 2,72  | 0,50    | N SEP-E-004:2014*                    | TAK      |
| e — kd2       | 1,80  | 0,50    | N SEP-E-004:2014*                    | TAK      |
| e — kd4       | 1,48  | 0,50    | N SEP-E-004:2014*                    | TAK      |
| t — kd2       | 1,50  | 0,50    | praktyka proj.*                      | TAK      |
| t — kd4       | 1,18  | 0,50    | praktyka proj.*                      | TAK      |
| e — budynek   | 0,83  | —       | informacyjnie (lico ściany)          | —        |
| kd1 — budynek | 0,65  | —       | informacyjnie (lico ściany)          | —        |
| kd2 — budynek | 0,93  | —       | informacyjnie (lico ściany)          | —        |

\* wartości minimalne wg zasad wiedzy technicznej (N SEP-E-004, praktyka projektowa) — NIE są przepisem: WT § 26–28 określają tylko wymagania ogólne uzbrojenia działki; do potwierdzenia w warunkach przyłączenia gestorów [SPRAWDŹ]. „warunk.” — dopuszczalne przy rurach osłonowych.

### SKRZYŻOWANIA SIECI

| Nr | Sieci       | x [m] | y [m] |
|----|-------------|-------|-------|
| S1 | w × e ist.  | 23,00 | 51,00 |
| S2 | w × t ist.  | 23,00 | 51,40 |
| S3 | w × e       | 23,00 | 43,20 |
| S4 | w × t       | 23,00 | 43,50 |
| S5 | ks × w ist. | 13,00 | 54,00 |
| S6 | ks × e ist. | 13,00 | 51,00 |
| S7 | ks × t ist. | 13,00 | 51,40 |
| S8 | ks × kd1    | 13,00 | 42,40 |
| S9 | t × e ist.  | 19,70 | 51,00 |

Odstęp pionowy na skrzyżowaniach — wg warunków gestorów sieci [DO UZUPEŁNIENIA] (brak rzędnych przewodów w modelu); kable w rurach osłonowych w obrębie skrzyżowań.

### KOLIZJE I ZBLIŻENIA

| Nr | Rodzaj          | Opis                 | Ocena   |
|----|-----------------|----------------------|---------|
| K1 | zbliżenie sieci | e–t: 0,30 m < 0,50 m | warunk. |

K1: dopuszczalne przy ułożeniu w rurach osłonowych — uzgodnić z gestorami

### LEGENDA

|  |                                                                             |  |                                                                 |
|--|-----------------------------------------------------------------------------|--|-----------------------------------------------------------------|
|  | granica działki budowlanej, punkt graniczny, narożnik (PN-B-01027 poz. 2.7) |  | furtka otwierana do wewnątrz działki (WT § 42)                  |
|  | linia rozgraniczająca drogi publicznej (PN-B-01027 poz. 2.5)                |  | jednostka zewn. pompy ciepła (fundament) i strefa czynnika R290 |
|  | jezdnia drogi publicznej (wg mapy)                                          |  | zbiornik retencyjny szczelny (ZB)                               |
|  | nieprzekraczalna linia zabudowy wg MPZP (PN-B-01027 poz. 2.2)               |  | niecka chłonna — ogród deszczowy (przelew zbiornika)            |
|  | budynek projektowany — obrys ścian parteru 1,0 m nad terenem (poz. 1.1)     |  | odwodnienie liniowe                                             |
|  | obrys wyższych kondygnacji poza obrysem parteru (poz. 1.6 d)                |  | niecka trawiasta — grot w kierunku spływu                       |
|  | obrys płyt wspornikowych, okapów i daszku — przewieszenia (poz. 1.6 c)      |  | rura spustowa: zewnętrzna / w szachcie (RS)                     |
|  | ±0,00=101,65                                                                |  | miejsce włączenia przyłącza do sieci (PN-B-01027 poz. 6)        |
|  | wejście główne do budynku (poz. 1.7)                                        |  | złącze kablowo-pomiarowe ZKP (w linii ogrodzenia)               |
|  | wjazd do garażu                                                             |  | studzienka rewizyjna kanalizacji                                |
|  | zjazd z drogi publicznej — wg zezwolenia zarządcy drogi (DO UZUPEŁNIENIA)   |  | studnia chłonna skroplin pompy ciepła                           |
|  | nawierzchnia z kostki betonowej (poz. 7.10)                                 |  | skrzyżowanie sieci — zachować odstęp pionowy (tabela)           |
|  | nawierzchnia z płyt betonowych (poz. 7.11)                                  |  | zbliżenie / kolizja sieci (nr w tabeli koordynacji)             |
|  | płyty w trawie (ażur) — poza PBC                                            |  | w — sieć wodociągowa istniejąca (mapa)                          |
|  | taras naziemny — deska kompozytowa na legarach                              |  | w — przyłącze wodociągowe projektowane                          |
|  | opaska żwirowa 16/32 na geowłókninie                                        |  | ks — sieć kanalizacji sanitarnej istniejąca (mapa)              |
|  | stanowisko postojowe 2,50 × 5,00 m (WT § 21)                                |  | ks — przykanalik sanitarny projektowany                         |
|  | osłona pojemników na odpady — segregacja (WT § 22)                          |  | kd — kanalizacja deszczowa projektowana (kolektory, przelewy)   |
|  | rabata z krzewami                                                           |  | e — linia kablowa nN istniejąca (mapa)                          |
|  | zrywplot projektowany (poz. 7.6)                                            |  | e — kabel nN projektowany (ZKP → RG)                            |
|  | drzewo liściaste projektowane (poz. 7.1)                                    |  | t — sieć telekomunikacyjna istniejąca (mapa)                    |
|  | drzewo istniejące — zachowane (poz. 7.2)                                    |  | t — przyłącze telekomunikacyjne projektowane                    |
|  | ogrodzenie projektowane (poz. 2.8; na granicy — odsunięte graficznie)       |  | g — sieć gazowa istniejąca (mapa)                               |
|  | brama przesuwna (poz. 2.9)                                                  |  |                                                                 |

### OBJAŚNIENIA I UWAGI

- Wymiary i odległości w m (dokładność 0,01 m), rzędne w m n.p.m. (PL-EVRF2007-NH).
- Oznaczenia sieci — kolory i litery wg mapy zasadniczej (zał. 4 rozp. w sprawie BDOT500 i mapy zasadniczej, Dz.U. 2021 poz. 1385): w — wodociąg, ks — kanalizacja sanitarna, kd — kanalizacja deszczowa, e — elektroenergetyczna, t — telekomunikacyjna, g — gazowa; istniejące — linia cienka (wg mapy), projektowane — gruba; w budynku/pod płytą — kreskowa; „x” — włączenie do sieci.
- Przyłącza w granicach działki nie podlegają narzędziu koordynacyjnej ZUD (PGiK art. 28b); roboty w pasie drogowym 1KDD — za zezwoleniem zarządcy drogi (u.d.p. art. 40).
- Skrzyżowań: 9; zbliżeń poniżej wartości minimalnych: 1 (tabela „Kolizje i zbliżenia”).
- Wody opadowe: rury spustowe RS → kolektory kd → zbiornik ZB → przelew do niecki chłonnej NCH; odwodnienia liniowe OL → kolektory kd (WT § 28 ust. 2).
- Drenaż opaskowy DR-0: NIE PROJEKTUJE SIĘ — piaski przepuszczalne, ZWG = 3,8 m p.p.t., posadowienie = 0,5 m p.p.t. (W-285); ochrona płyty: XPS + membrana SBS, opaska żwirowa i spadki terenu
- Braki danych modelu (9 poz.) — [DO UZUPEŁNIENIA]; wykaz: projekt/02\_PZT/BRAKI\_DANYCH.md.
- Rysunek wygenerowany automatycznie z modelu /home/user/aihouse/model/budynek.yaml (wersja 1.0, 2026-09-25) — generatory lamela.views.



|                                                                                               |                                              |                            |
|-----------------------------------------------------------------------------------------------|----------------------------------------------|----------------------------|
| REW.                                                                                          | OPIS ZMIANY                                  | DATA                       |
| 0                                                                                             | Wydanie — rysunek wygenerowany z modelu      | 2026-09-25                 |
| PRACOWNIA PROJEKTOWA                                                                          | PRACOWNIA PROJEKTOWA — nazwa do uzupełnienia | STADIUM                    |
| adres pracowni do uzupełnienia                                                                | PB                                           | BRANŻA                     |
| INWESTOR                                                                                      | ZAGOSPODAROWANIE TERENU                      |                            |
| (do uzupełnienia)                                                                             |                                              |                            |
| OBIEKT / NAZWA ZAMIERZENIA BUDOWLANEGO                                                        |                                              |                            |
| Budynek mieszkalny jednorodzinny wolnostojący „Dom LAMELA” z zagospodarowaniem działki        |                                              |                            |
| ADRES / LOKALIZACJA (NR DZIAŁKI, OBRĘB, JEDN. EWIDENCYJNA)                                    |                                              | KAT. OBIEKTU               |
| ul. Lipowa (fikcyjna), dz. nr ewid. 123/4, obręb 0005 Przykładowo, gm. Przykładowo (fikcyjna) |                                              | I                          |
| FUNKCJA                                                                                       | IMIĘ I NAZWISKO                              | SPECJALNOŚĆ, NR UPRAWNIENI |
| Projektant                                                                                    |                                              | DATA                       |
| Projektant (wsp.)                                                                             |                                              | PODPIS                     |
| Sprawdzający                                                                                  |                                              |                            |
| Opracował                                                                                     |                                              |                            |
| TYTUŁ RYSUNKU                                                                                 |                                              |                            |
| RYSUNEK KOORDYNACYJNY UZBROJENIA TERENU                                                       |                                              |                            |
| SKALA                                                                                         | FORMAT                                       | DATA WYDANIA               |
| 1:200                                                                                         | A2                                           | 2026-09-25                 |
| RODZAJ DOK.                                                                                   | NR RYSUNKU                                   | ARKUSZ                     |
| rysunek koordynacyjny                                                                         | PZT-03                                       | 3/3                        |
| REW.                                                                                          |                                              |                            |
| 0                                                                                             |                                              |                            |