


RZUT II PIĘTRA 1:50

OZNACZENIA LINII

- elementy nad płaszczyzną cięcia (obrys płyt, wsporników, brył wyższych kondygnacji)
--- elementy poniżej płaszczyzny cięcia (widok z góry)
--- osie konstrukcyjne; linia punktowa z pogrubionymi końcami — ślad przebiegu

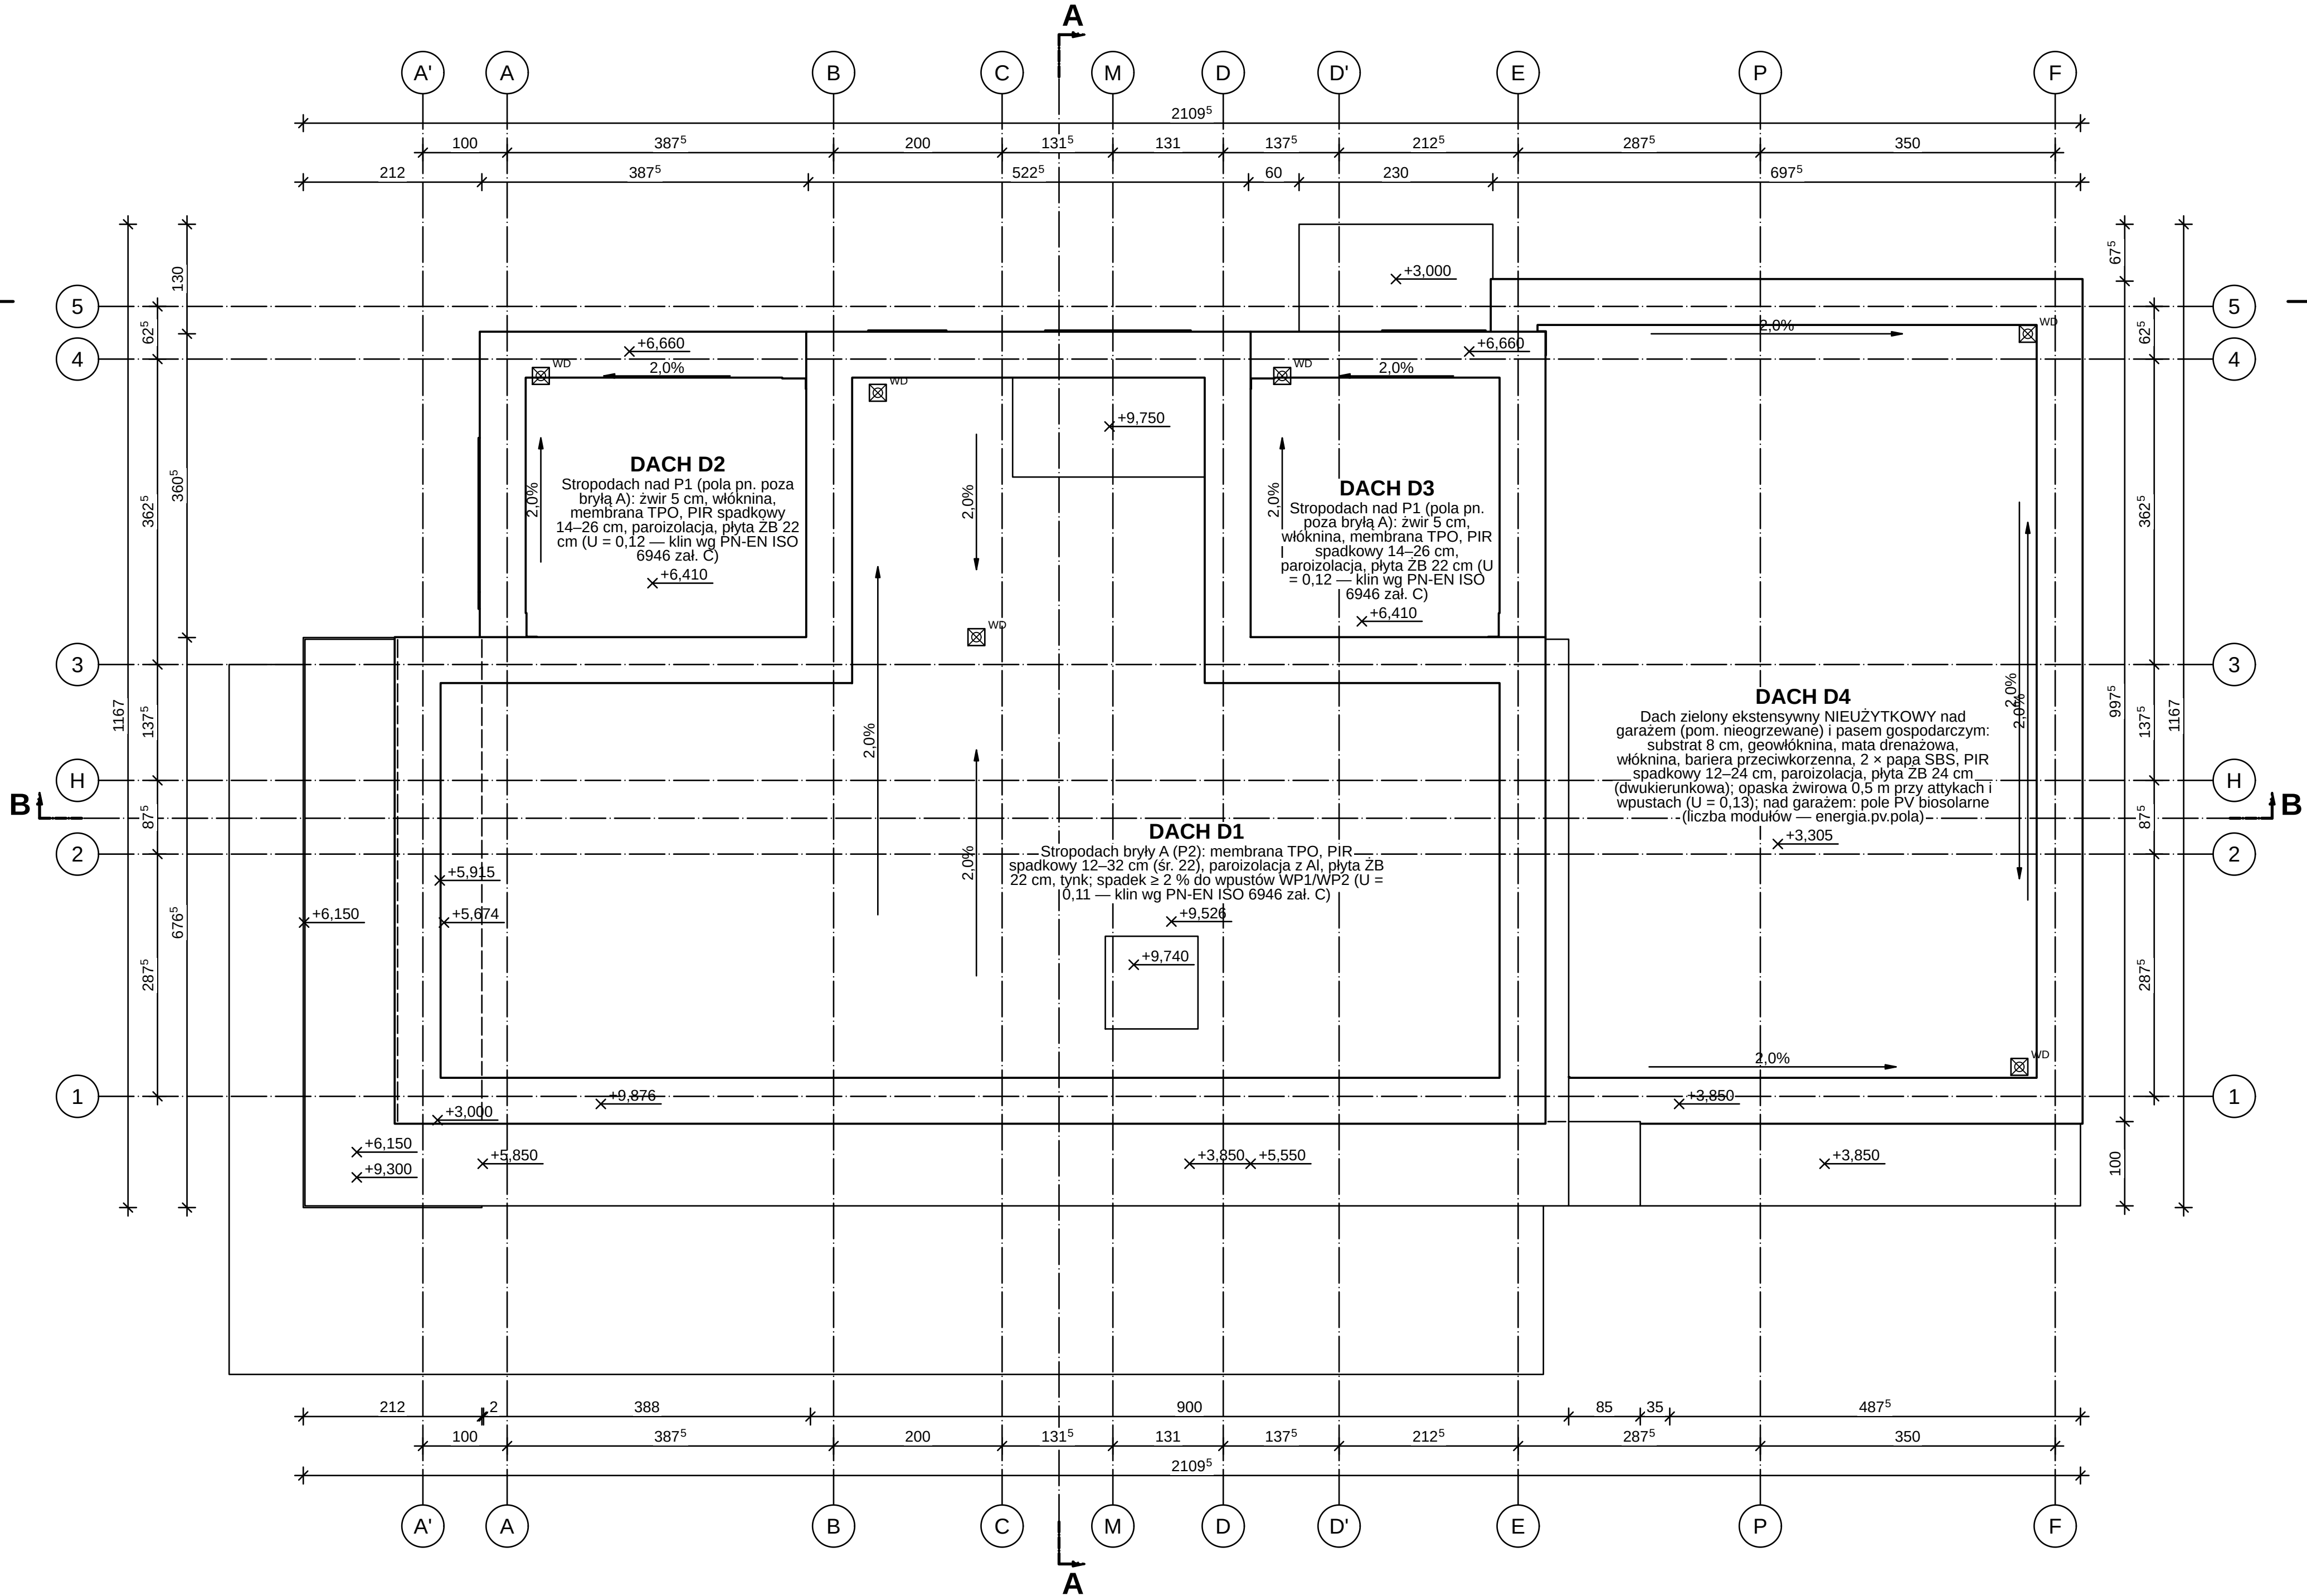


RZUT DACHU 1:50

OZNACZENIA MATERIAŁÓW (PN-B-01030 + przyjęte)

- Włna mineralna 035 (szkielet, docieplenia, ściana dom-garaz);
Włna mineralna: fasadowa (elewacja wentylowana bryły A, A1)
— meander, UUU
Styropian grafityowy EPS 031 (ETICS, NRO w systemie) —
zgracek „VUV”
Membrana fasadowa wiatroizolacyjna UV-stabilna, czarna (sd = 0,02 m)
Błoczek wapniowo-piaskowy 12 cm, kl. 15 (ścianki działowe, boczny w wiatroizacji); Błoczek wapniowo-piaskowy (silikat) 18 cm, kl. 20, gr. 1, na zaprawie cienkowarstwowej — krawka ukośna 45°/135°
Żelbet C25/30, B500SP (stropy, płyta fundamentowa, ściany) —
45° na przemiern cięciu i przerywane

OBJAŚNIENIA I UWAGI

1. Wymiary w cm (mm w indeksie górnym, np. 24° = 24,5 cm), rzędne w m względem ±0,000 = 101,650 m n.p.m. (PL-EVRF2007-NH).
2. Rzut: płaszczyzna cięcia +1,10 m nad posadzką kondygnacji. Linia krekowa — elementy nad płaszczyzną cięcia (obrys płyt i wsporników, brył wyższych kondygnacji, otwory w stropie nad, belki); linia ciągła — elementy poniżej (widok).
3. Otwory: licznik — szerokość, mianownik — wysokość w świetle muru, w nawiasie wysokość parapetu; symbol stolarki wg zestawienia stolarki.
4. Numeracja pomieszczeń wg PN-B-01025 / PN-EN ISO 4157-2: <nr> kondygnacji (parter = 1) <nr>, identyfikator w modelu: <kond> <nr> (parter = 0).
5. Dzw: strona otwierania (lewo/prawo) wg modelu — patrz: od strony, w którą otwiera się skrzydło.
6. Rysunek wygenerowany automatycznie z modelu modelBudynek.yamf (wersja 1.0, 2026-09-25) — generatory lamela.views.

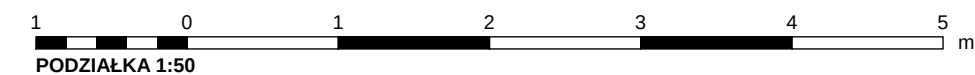

ZESTAWIENIE POMIESZCZEŃ

Nr	Nazwa pomieszczenia	Posadzka	Kat.	Wys. [m]	Pow. [m²]
3.02	Sypialnia rodziców	Deska warstwowa dębowa 15 mm, klejona	podst.	2,77	21,43
3.05	Gabinet / pokój gościnny okazjonalny	Deska warstwowa dębowa 15 mm, klejona	podst.	2,77	16,25
3.03	Garderoba (przedpokój apartamentu)	Deska warstwowa dębowa 15 mm, klejona	pomoc.	2,77	10,49
3.07	Pom. techniczne (centrala rekuperacyjna, wylaz na dach)	Płyty gresowe 60x120 na kleju C2TE \$1 techn.	techn.	2,77	5,90
3.01	Hol	Deska warstwowa dębowa 15 mm, klejona	techn.	2,77	5,74
3.04	Łazienka rodziców	Płytki gresowe 60x120 na kleju C2TE \$1 techn.	techn.	2,77	5,51
3.08	Szacht instalacyjny SI	techn.	techn.	2,77	0,45
3.06	Klatka schodowa (wyjście z biegu 2, pustka)	Deska warstwowa dębowa 15 mm, klejona	techn.	2,77	0,24
RAZEM powierzchnia netto					66,01
w tym użytkowa (podst. + pomoc.)					53,67

REW.	OPIS ZMIANY	DATA
0	Wydanie — rysunek wygenerowany z modelu	2026-09-25
PRACOWNIA PROJEKTOWA — nazwa do uzupełnienia		STADIUM
ul. Lipowa (fikcyjna), dz. nr ewid. 123/4, obręb 0005 Przykładowo, gm. Przykładowo (fikcyjna)		BRANŻA
INWESTOR (do uzupełnienia)		ARCHITEKTURA (AR)
OBJEKT / NAZWA ZAMIERZENIA BUDOWLANEGO		
Budynek mieszkalny jednorodzinny wolnostojący „Dom LAMELA”		
ADRES / LOKALIZACJA (NR DZIAŁKI, OBRĘB, JEDN. EWIDENCYJNA)		KAT. OBJEKTU
ul. Lipowa (fikcyjna), dz. nr ewid. 123/4, obręb 0005 Przykładowo, gm. Przykładowo (fikcyjna)		I
FUNKCJA	IMIĘ I NAZWISKO	SPECJALNOŚĆ, NR UPRAWNIENI
Projektant		DATA
Projektant (wsp.)		PODPIS
Sprawdzający		
Opracował		
TYTUŁ RYSUNKU		
RZUT II PIĘTRA I RZUT DACHU		
SKALA	FORMAT	DATA WYDANIA
1:50	S90x891	2026-09-25
RODZAJ DOK.	NR RYSUNKU	ARKUSZ
Rzut	PB-AR-03	3/5
REW.		0