

PZT

PROJEKT ZAGOSPODAROWANIA DZIAŁKI

element projektu budowlanego wg art. 34 ust. 3 PB

PRZYKŁAD – NIE DO ZŁOŻENIA

Działka, MPZP, warunki gruntowe i sieci: [DANE PRZYKŁADOWE – FIKCYJNE]. Dane osobowe, numery uprawnień, podpisy i dokumenty organów — pola do uzupełnienia. Opracowanie jest szablonem zgodnym z RPB i nie może zostać złożone bez danych rzeczywistych (rejestr wymagań, sekcja E).

NAZWA ZAMIERZENIA
BUDOWLANEGO

Budowa budynku mieszkalnego jednorodzinnego wolnostojącego „Dom LAMELA” z garażem dwustanowiskowym w bryle budynku, wraz z zagospodarowaniem terenu i infrastrukturą towarzyszącą (zjazd, dojazd i dojście, miejsca postojowe, zbiornik retencyjny wód opadowych, ogrodzenie)

OBIEKT BUDOWLANY

Budynek mieszkalny jednorodzinny wolnostojący „Dom LAMELA”

ADRES OBIEKTU

ul. Lipowa (fikcyjna) [DANE PRZYKŁADOWE – FIKCYJNE]

KATEGORIA OBIEKTU
BUDOWLANEGO

I – budynki mieszkalne jednorodzinne (załącznik do ustawy – Prawo budowlane)

DZIAŁKA EWIDENCYJNA

nr 123/4, obręb 0005 Przykładowo, gm. Przykładowo (fikcyjna), jedn. ewid.: [DO UZUPEŁNIENIA: jednostka ewidencyjna — kod TERYT WWPPGG_R i nazwa] identyfikator działki ewidencyjnej: [DO UZUPEŁNIENIA: kod TERYT jedn. ewid. WWPPGG_R].0005.123/4

INWESTOR

[DO UZUPEŁNIENIA: imię i nazwisko lub nazwa inwestora]
adres: [DO UZUPEŁNIENIA: adres inwestora]

OPRACOWANIE — AUTORZY (§ 7 UST. 2 PKT 3 RPB)

Funkcja, branża	Imię i nazwisko	Specjalność i nr uprawnień budowlanych	Zakres opracowania	Podpis
Projektant architektura	[DO UZUPEŁNIENIA: imię i nazwisko]	architektoniczna bez ograniczeń nr upr.: [DO UZUPEŁNIENIA: nr uprawnień budowlanych]	PZT i PAB — rozwiązania architektoniczne i zagospodarowanie działki; PT-1 AR; informacja BIOZ	
Projektant instalacje sanitarne	[DO UZUPEŁNIENIA: imię i nazwisko]	instalacyjna (ciepłne, wentylacyjne, gazowe, wod.-kan.) bez ograniczeń nr upr.: [DO UZUPEŁNIENIA: nr uprawnień budowlanych]	PZT — przyłącza wod.-kan., wody opadowe; PAB — wyposażenie instalacyjne, źródło ciepła; PT-3 IS; oświadczenie z art. 33 ust. 2 pkt 10 PB	
Projektant instalacje elektryczne	[DO UZUPEŁNIENIA: imię i nazwisko]	instalacyjna (elektryczne i elektroenergetyczne) bez ograniczeń nr upr.: [DO UZUPEŁNIENIA: nr uprawnień budowlanych]	PZT — zasilanie nN i teletechnika; PAB — wyposażenie elektryczne; PT-4 IE	
Sprawdzający	nie dotyczy (art. 20 ust. 3 pkt 2 PB)			

DATA OPRACOWANIA

25 września 2026 r.

REWIZJA / PLIK

rew. 0

ZAWARTOŚĆ TOMU

PZT – Projekt zagospodarowania działki

Postać elektroniczna (RPB § 2b): plik PDF opatruje podpisem kwalifikowanym, osobistym albo zaufanym każda osoba opracowująca daną część w zakresie objętym plikiem (§ 7 ust. 4a RPB); pole „Podpis” wypełnia się wyłącznie w postaci papierowej (§ 7 ust. 2 pkt 4 RPB).

SPIS TREŚCI

PZT — Projekt zagospodarowania działki

DOKUMENTY DOŁĄCZONE DO PROJEKTU (§ 7 UST. 5 PKT 3 RPB)

Oświadczenie projektanta (art. 34 ust. 3d pkt 3 PB)	3
---	---

CZĘŚĆ OPISOWA (§ 7 UST. 5 PKT 1 RPB)

1. Przedmiot zamierzenia	4
2. Istniejący stan zagospodarowania działki	5
3. Projektowane zagospodarowanie działki	5
3.1. Urządzenia budowlane związane z budynkiem	5
3.2. Sposób odprowadzania ścieków i wód opadowych	6
3.3. Układ komunikacyjny	6
3.4. Sposób dostępu do drogi publicznej	6
3.5. Parametry techniczne sieci i urządzeń uzbrojenia terenu	6
3.6. Ukształtowanie terenu i układ zieleni	7
4. Zestawienie powierzchni i wskaźników zagospodarowania	8
5. Informacje o ograniczeniach, zabytkach, wpływie eksploatacji górniczej i zagrożeniach	10
5.1. Ograniczenia i zakazy wynikające z aktów prawa miejscowego	10
5.2. Ochrona konserwatorska	10
5.3. Wpływ eksploatacji górniczej	10
5.4. Zagrożenia dla środowiska oraz higieny i zdrowia	10
6. Dane dotyczące warunków ochrony przeciwpożarowej	11
7. Dane dotyczące ochrony ludności	11
8. Inne dane wynikające ze specyfiki zamierzenia	11
8.1. Retencja i zagospodarowanie wód opadowych	11
8.2. Warunki gruntowe i pozostałe dane	12
9. Informacja o obszarze oddziaływania obiektu	12

CZĘŚĆ RYSUNKOWA (§ 7 UST. 5 PKT 2 RPB)

Karta części rysunkowej i wykaz rysunków	14
PZT-01 PLAN ZAGOSPODAROWANIA DZIAŁKI (1:500)	rys.
PZT-02 PLAN SZCZEGÓŁOWY — WYMIARY I RZĘDNE (1:200)	rys.
PZT-03 RYSUNEK KOORDYNACYJNY UZBROJENIA TERENU (1:200)	rys.

Numeracja stron odrębna dla elementu (§ 6 ust. 1 RPB); rysunki oznaczono numerem rysunku (§ 6 ust. 3 RPB). Pozycje spisu są odnośnikami w pliku PDF.

[DO UZUPEŁNIENIA: miejscowość], dnia 25 września 2026 r.

OŚWIADCZENIE PROJEKTANTA

o sporządzeniu projektu zagospodarowania działki zgodnie z obowiązującymi przepisami oraz zasadami wiedzy technicznej
(art. 34 ust. 3d pkt 3 ustawy z dnia 7 lipca 1994 r. – Prawo budowlane (t.j. Dz.U. 2026 poz. 524 ze zm.))

Zamierzenie budowlane	Budowa budynku mieszkalnego jednorodzinnego wolnostojącego „Dom LAMELA” z garażem dwustanowiskowym w bryle budynku, wraz z zagospodarowaniem terenu i infrastrukturą towarzyszącą (zjazd, dojazd i dojście, miejsca postojowe, zbiornik retencyjny wód opadowych, ogrodzenie)
Obiekt, kategoria	Budynek mieszkalny jednorodzinny wolnostojący „Dom LAMELA” — kategoria I
Adres, działka	ul. Lipowa (fikcyjna) [DANE PRZYKŁADOWE – FIKCYJNE]; działka ewid. nr 123/4, obręb 0005 „Przykładowo”, gm. Przykładowo (fikcyjna); identyfikator: [DO UZUPEŁNIENIA: kod TERYT jedn. ewid. WWPPGG_R].0005.123/4
Inwestor	[DO UZUPEŁNIENIA: imię i nazwisko lub nazwa inwestora], [DO UZUPEŁNIENIA: adres inwestora]
Element projektu	Projekt zagospodarowania działki (PZT)

Działając na podstawie art. 34 ust. 3d pkt 3 ustawy z dnia 7 lipca 1994 r. – Prawo budowlane (t.j. Dz.U. 2026 poz. 524 ze zm.), **oświadczam, że projekt zagospodarowania działki dla wyżej wymienionego zamierzenia budowlanego został sporządzony zgodnie z obowiązującymi przepisami oraz zasadami wiedzy technicznej.**

Przepisy techniczno-budowlane wydane na podstawie art. 7 ust. 2 pkt 1 PB — rozporządzenie Ministra Infrastruktury z dnia 12 kwietnia 2002 r. w sprawie warunków technicznych, jakim powinny odpowiadać budynki i ich usytuowanie (t.j. Dz.U. 2022 poz. 1225 ze zm.) — zastosowano w brzmieniu obowiązującym do dnia 19 września 2026 r., na podstawie art. 102a ust. 1 PB, w związku z oświadczeniem Inwestora z dnia [DO UZUPEŁNIENIA: data złożenia oświadczenia z art. 102a PB].

Osoby biorące udział w opracowaniu projektu (art. 34 ust. 3e pkt 1 PB)

Lp.	Imię i nazwisko	Specjalność uprawnień budowlanych	Nr uprawnień / decyzji	Zakres udziału	Data i podpis
1.	[DO UZUPEŁNIENIA: imię i nazwisko]	architektoniczna bez ograniczeń	[DO UZUPEŁNIENIA: nr uprawnień budowlanych]	PZT i PAB — rozwiązania architektoniczne i zagospodarowanie działki; PT-1 AR; informacja BIOZ	
2.	[DO UZUPEŁNIENIA: imię i nazwisko]	instalacyjna (ciepłne, wentylacyjne, gazowe, wod.-kan.) bez ograniczeń	[DO UZUPEŁNIENIA: nr uprawnień budowlanych]	PZT — przyłącza wod.-kan., wody opadowe; PAB — wyposażenie instalacyjne, źródło ciepła; PT-3 IS; oświadczenie z art. 33 ust. 2 pkt 10 PB	
3.	[DO UZUPEŁNIENIA: imię i nazwisko]	instalacyjna (elektryczne i elektroenergetyczne) bez ograniczeń	[DO UZUPEŁNIENIA: nr uprawnień budowlanych]	PZT — zasilanie nN i teletechnika; PAB — wyposażenie elektryczne; PT-4 IE	

Projektanci sprawdzający (art. 34 ust. 3e pkt 2 PB): nie dotyczy — projekt budynku mieszkalnego jednorodzinnego nie podlega sprawdzeniu (art. 20 ust. 3 pkt 2 PB).

Kopie decyzji o nadaniu uprawnień budowlanych i zaświadczeń o przynależności do izby samorządu zawodowego (art. 34 ust. 3d pkt 1–2 PB) nie dołącza się dla uprawnień i osób wpisanych do centralnego rejestru osób posiadających uprawnienia budowlane (art. 34 ust. 3da PB) — [DO UZUPEŁNIENIA: potwierdzenie wpisu w e-CRUB albo dołączenie kopii]. Przy tym samym autorze PZT i PAB kopie dołącza się tylko do jednego z projektów (§ 8 ust. 1 RPB), a w sprawie wielotomowej — do pierwszego tomu (§ 8 ust. 2 RPB).

Podpisy: postać elektroniczna — podpis kwalifikowany, osobisty albo zaufany pliku (§ 7 ust. 4a RPB), kolumna „Data i podpis” pozostaje pusta; postać papierowa — podpis własnoręczny każdego z projektantów.

OPIS TECHNICZNY DO PROJEKTU ZAGOSPODAROWANIA DZIAŁKI

§ 14 RPB

Opis sporządzono w zakresie określonym w § 14 rozporządzenia Ministra Rozwoju z dnia 11 września 2020 r. w sprawie szczegółowego zakresu i formy projektu budowlanego (t.j. Dz.U. 2022 poz. 1679, zm. Dz.U. 2023 poz. 2405 i Dz.U. 2026 poz. 597) — dalej **RPB**. Wymagania techniczno-budowlane przyjęto wg rozporządzenia Ministra Infrastruktury w sprawie warunków technicznych, jakim powinny odpowiadać budynki i ich usytuowanie (t.j. Dz.U. 2022 poz. 1225 ze zm.) — dalej **WT** — w brzmieniu obowiązującym do 19.09.2026 r., stosowanego na podstawie art. 102a ust. 1 ustawy – Prawo budowlane (t.j. Dz.U. 2026 poz. 524 ze zm.) — dalej **PB** — w związku z oświadczeniem Inwestora ([DO UZUPEŁNIENIA: data złożenia oświadczenia z art. 102a PB]; wzór — ZL).

Działka, ustalenia miejscowego planu zagospodarowania przestrzennego (MPZP), uzbrojenie terenu i warunki gruntowe są danymi przykładowymi [DANE PRZYKŁADOWE – FIKCYJNE]. Wartości liczbowe opisu wygenerowano z modelu projektu (model/budynek.yaml, model/działka.yaml) i obliczeń (lamela.wskazniki, audyt WT, lamela.obliczenia). Rzędne w układzie wysokościowym PL-EVRF2007-NH; ±0,00 = 101,65 m n.p.m. Rysunki: PZT-01 (plan zagospodarowania, 1:500), PZT-02 (plan szczegółowy — wymiary i rzędne, 1:200), PZT-03 (rysunek koordynacyjny uzbrojenia terenu, 1:200).

1. Przedmiot zamierzenia

§ 14 pkt 1 RPB

Przedmiotem zamierzenia budowlanego jest **budowa budynku mieszkalnego jednorodzinnego wolnostojącego „Dom LAMELA”** (PB art. 3 pkt 2a) — 3 kondygnacje nadziemne (parter, I piętro, II piętro), bez podpiwniczenia, z garażem 2-stanowiskowym w bryle parteru — wraz z zagospodarowaniem działki nr ewid. 123/4 i urządzeniami budowlanymi związanymi z budynkiem (PB art. 3 pkt 9). Zamierzenie obejmuje jeden obiekt budowlany; zakres całego zamierzenia:

- 1) budynek mieszkalny jednorodzinny z garażem w bryle — obiekt kategorii I (załącznik do PB);
- 2) zjazd z drogi publicznej 1KDD (ul. Lipowa (fikcyjna), klasa D) — w zakresie i na warunkach zezwolenia zarządcy drogi (u.d.p. art. 29 ust. 1, 3a; ZL);
- 3) podjazd (kostka betonowa 8 cm grafit na podbudowie (2,5 t)), dojście (płyty betonowe 60×60 cm, szer. 1,30 m), 2 stanowiska postojowe naziemne dla gości;
- 4) tarasy i podesty naziemne (3 szt., łącznie 66,75 m²);
- 5) stanowisko pojemników na odpady — osłona z lamel na 4 pojemniki 240 l (segregacja), przy furtce;
- 6) zagospodarowanie wód opadowych: szczelny zbiornik retencyjny 5,0 m³, niecka chłonna (ogród deszczowy) 28,0 m², osadnik z separatorem substancji ropopochodnych SEP-1, odwodnienia liniowe, kanalizacja deszczowa na działce;
- 7) fundament jednostki zewnętrznej pompy ciepła i studnia chłonna skroplin SK-PC;
- 8) ogrodzenie z bramą przesuwą (5,60 m) i furtką (1,00 m);
- 9) przyłącza: wodociągowe, kanalizacji sanitarnej, elektroenergetyczne nN, telekomunikacyjne (kanalizacja kablowa ze światłowodem) — wg warunków przyłączenia gestorów sieci [DO UZUPEŁNIENIA: nr i data warunków przyłączenia (E-05)]; przyłącza gazowego nie projektuje się — budynek bez instalacji gazowej (ogrzewanie i c.w.u. z pompy ciepła);
- 10) zieleni: trawniki, żywopłoty, rabaty, 5 drzew projektowanych; zachowanie drzew istniejących.

2. Istniejący stan zagospodarowania działki

§ 14 pkt 2 RPB

Działka nr ewid. 123/4, obręb 0005 Przykładowo, gm. Przykładowo (fikcyjna), ma kształt prostokąta 32,00 × 50,00 m o powierzchni 1 600,00 m² [DANE PRZYKŁADOWE – FIKCYJNE]. Działka jest niezabudowana; brak obiektów budowlanych przeznaczonych do rozbiórki. Teren jest płaski: rzędne terenu istniejącego w granicach działki 101,10–101,55 m n.p.m. (88 punktów wysokościowych), spadek ok. 0,6 % ku południu i ok. 0,5 % ku zachodowi. Grunt: 0,0–0,4 ziemia urodzajna; piaski średnie I_D ≈ 0,6; ZWG ≈ 3,8 m p.p.t. [DANE PRZYKŁADOWE – FIKCYJNE].

Otoczenie: od północy droga publiczna gminna 1KDD — ul. Lipowa (fikcyjna), klasa D, w liniach rozgraniczających 10,00 m, jezdnia asfalt szer. 5,50 m; działka nr 123/3 — dom jednorodzinny, 2 kondygnacje, dach dwuspadowy (≥ 8 m od granicy); działka nr 123/5 — dom jednorodzinny parterowy z poddaszem (≥ 8 m od granicy); działka nr 130 — teren rolny (R IVb) — niezabudowany.

Zieleń istniejąca: 2 drzewa (brzoza brodawkowata; sosna zwyczajna), zachowywane; drzew i krzewów do usunięcia: brak. Uzbrojenie istniejące w pasie drogi 1KDD: wodociąg PE 110 (ul. Lipowa); kanalizacja sanitarna PVC 200, dno ≈ 99,20; kabel nN 0,4 kV (OSD); kanalizacja teletechniczna / światłowód; gazociąg PE 63 — NIE wykorzystywany (dom all-electric) [DANE PRZYKŁADOWE – FIKCYJNE]. Stan istniejący — na mapie do celów projektowych [DO UZUPEŁNIENIA: mapa do celów projektowych z klauzulą urzędową lub oświadczeniem geodety (E-01)] (rys. PZT-01).

3. Projektowane zagospodarowanie działki

§ 14 pkt 3 RPB

3.1. Urządzenia budowlane związane z budynkiem

§ 14 pkt 3 lit. a

Urządzenia budowlane (PB art. 3 pkt 9) projektowane na działce — położenie na rys. PZT-01 i PZT-03:

Tabela 1. Urządzenia budowlane (z modelu `dzialka.yaml`)

Lp.	Element	Opis
1.	ZKP	złącze kablowo-pomiarowe we wnęce ogrodzenia, PWP przy wejściu (W-190)
2.	SR1	studzienka rewizyjna kanalizacji Ø425 (poza garażem — W-118)
3.	PC-JZ	jednostka zewn. PC monoblok R290 w osłonie lamelowej z ekranem akustycznym od tarasu; 7,0 m od granicy E (≥ 6,0 — W-024); strefa R290 1,0 m bez otworów, wpustów i studzienek (W-156)
4.	SEP-1	osadnik z separatorem substancji ropopochodnych (mini, klasa I, PN-EN 858) dla OL-1/OL-4 (podjazd, posadzka garażu); odpływ do niecki NT-E, poza zbiornikiem retencyjnym (audyt A1, W-114)
5.	SK-PC	studnia chłonna skroplin PC (żwir, ≥ 0,8 m p.p.t.), poza strefą R290 (W-146)
6.	zbiornik retencyjny	szczelny zbiornik PE 5,0 m ³ z osadnikiem i filtrem, pompa do podlewania, przelew DN160 do niecki; ≥ 3,0 m od budynku, ≥ 2,0 m od granic (W-145: wariant bazowy, nie jest urządzeniem wodnym)
7.	niecka chłonna	niecka chłonna (ogród deszczowy) 28 m ² (powiększona — weryfikacja §6 B6), głęb. 0,30 m, ≥ 3,0 m od fundamentów, ≥ 2,0 m od granic, ≥ 1,0 m od rzutu korony dojrzałych drzew (W-144, K-2)
8.	ogrodzenie od drogi	od drogi: ażurowe; h = 1,50 m; łącznie 25,40 m
9.	ogrodzenie pozostałe	panele siatkowe zgrzewane grafit z żywoplotem, h = 1,50 m, 132,00 m
10.	przesuwna	szer. w świetle 5,60 m, h = 1,50 m
11.	furtka	szer. w świetle 1,00 m, h = 1,50 m
12.	stanowisko pojemników	osłona z lamel na 4 pojemniki 240 l (segregacja), przy furtce; odległości wg WT §23 ust. 4 nieokreślone dla zabudowy jednorodzinnej (W-016)

Źródło danych: model/dzialka.yaml — uzbrojenie.obiekty, retencja, ogrodzenie, bramy, odpady

3.2. Sposób odprowadzania ścieków i wód opadowych

§ 14 pkt 3 lit. b

Ścieki bytowe — grawitacyjnie do sieci kanalizacji sanitarnej (kanalizacja sanitarna PVC 200, dno $\approx 99,20$) w drodze 1KDD: przykanalik PVC-U SN8 160 o spadku 2,0 % [ZAŁ — warunki gestora], ze studzienką rewizyjną SR1 (studzienka rewizyjna kanalizacji $\varnothing 425$ (poza garażem — W-118)); długość trasy na działce i w pasie drogowym 13,9 m (rys. PZT-03). Ścieki przemysłowe nie powstają.

Wody opadowe i roztopowe — zagospodarowane w całości w granicach działki (MPZP 3MN; WT § 28 ust. 2 [W-145]). Dachy o łącznej powierzchni rzutu 249,0 m² (przepływ obliczeniowy 11,46 l/s, PN-EN 12056-3) odwadniane rurami spustowymi do kolektorów kanalizacji deszczowej na działce (7 odcinków, łącznie 84,0 m) i dalej do szczelnego zbiornika retencyjnego z przelewem do niecki chłonnej (obliczenie — pkt 7). Wody z podjazdu i posadzki garażu (możliwe węglowodory) — odwodnieniami liniowymi przez osadnik z separatorem do niecki trawiastej, z pominięciem zbiornika. Skropliny pompy ciepła — do studni chłonnej. Wody opadowe nie są odprowadzane na drogę ani na działki sąsiednie (odwodnienie liniowe przy bramie wjazdowej; spadki terenu — lit. f).

3.3. Układ komunikacyjny

§ 14 pkt 3 lit. c

Wjazd bramą przesuwą w ogrodzeniu od drogi 1KDD; podjazd przed garażem szer. 6,38 m i dł. 7,62 m (nawierzchnia: kostka betonowa 8 cm grafit na podbudowie (2,5 t), spadek 1,5 % od budynku) — dojazd szerszy od wymaganego 3,00 m (WT §14 ust. 1). Dojście piesze od furtki do wejścia głównego: płyty betonowe 60×60 cm, szer. 1,30 m. Stanowiska postojowe:

Tabela 2. Stanowiska postojowe

Lp.	Stanowisko	Rodzaj	Wymiary [m]	Odl. od granic niedrogowych [m]	Ocena
1.	MP1	w garażu	2,50 × 5,90	9,38	spełnia
2.	MP2	w garażu	2,50 × 5,90	6,83	spełnia
3.	MP3	naziemne, niezadaszone	2,50 × 5,00	9,00	spełnia
4.	MP4	naziemne, niezadaszone	2,50 × 5,00	6,30	spełnia

Stanowisko $\geq 2,50 \times 5,00$ m — WT §21 ust. 1 pkt 1; odległość stanowisk naziemnych od granicy działki $\geq 3,00$ m — WT §19 ust. 2 pkt 1 lit. a (nie dotyczy granicy z działką drogową, ust. 7). Liczba stanowisk a MPZP — pkt 4.

3.4. Sposób dostępu do drogi publicznej

§ 14 pkt 3 lit. d

Dostęp do drogi publicznej gminnej 1KDD (ul. Lipowa (fikcyjna), klasa D) — **projektowanym zjazdem indywidualnym** w osi bramy wjazdowej, na podstawie zezwolenia zarządcy drogi na lokalizację zjazdu (u.d.p. art. 29 ust. 1; zezwolenie dołącza się do wniosku o pozwolenie na budowę — art. 29 ust. 3a; ZL) [DO UZUPEŁNIENIA: nr i data zezwolenia zarządcy drogi]. Parametry zjazdu przyjęto wstępnie: szerokość jezdni zjazdu 5,00 m [ZAŁ] (rozp. Dz.U. 2022 poz. 1518 §54–56 (brak wartości); parametry wg decyzji zarządcy); ostateczne — wg zezwolenia; PZT w zakresie zjazdu podlega uzgodnieniu z zarządcą drogi (u.d.p. art. 29 ust. 3 pkt 2). Roboty w pasie drogowym — po uzyskaniu zezwolenia zarządcy drogi na ich prowadzenie (u.d.p. art. 29 ust. 3 pkt 1 lit. b). Brama przesuwna 5,60 m $\geq 2,40$ m, furtka 1,00 m $\geq 0,90$ m (WT §43).

3.5. Parametry techniczne sieci i urządzeń uzbrojenia terenu

§ 14 pkt 3 lit. e

Przebieg przyłączy i sieci na działce — rys. PZT-03 (rysunek koordynacyjny); parametry z modelu:

Tabela 3. Projektowane przyłącza i przewody na działce

Lp.	Branża	Parametry (model)	Długość [m]
1.	wodociąg	przyłącze PE 40, przykrycie $\geq 1,20$ m (W-141), pod podjazdem i płytą garażu w rurze osłonowej, wodomierz w pom. 0.12	18,8

Lp.	Branża	Parametry (model)	Długość [m]
2.	kanalizacja sanitarna	przykanalik PVC-U 160, $i \geq 2\%$, studzienka rewizyjna SR1 Ø425 (x 13,0; y 43,8) — wyjście z płyty pod ścianą pn. (piony K1, K2)	13,9
3.	elektroenergetyczna nN	ZKP w linii ogrodzenia (pole odczytowe $\geq 0,48$ m nad terenem) → WLZ YKY 5×16 do RG w pom. 0.12, rura osłonowa pod podjazdem/garażem	18,2
4.	telekomunikacyjna	2 × HDPE Ø40 + mikrokabel światłowodowy (W-196)	21,3
5.	kanalizacja deszczowa	kolektor KD-W PVC 160 (RS3, RS4, RS1/RS2 z SI)	34,8
6.	kanalizacja deszczowa	kolektor KD-E PVC 160 (RS5 dach garażu, RS6 z pom. technicznego)	31,6
7.	kanalizacja deszczowa	przelew zbiornika DN160 do niecki chłonnej	6,2
8.	kanalizacja deszczowa	OL-1 (i OL-4 kanałem wzdłuż podjazdu) → separator SEP-1 → niecka NT-E (PVC 160)	3,3
9.	kanalizacja deszczowa	RS7 (rynnny zach. PL-E i PL-2) → KD-W, PVC 110	3,2
10.	kanalizacja deszczowa	RS8 (rynnny PL-E pd. i PL-D) + OL-6 (próg DZ3) → KD-E, PVC 110	4,1
11.	kanalizacja deszczowa	OL-5 (próg DZ2 garażu) → KD-E, PVC 110 (woda czysta z podestu — nie z posadzki garażu)	0,8

Średnice, spadki i rzędne w punktach załamania i włączenia — rys. PZT-03 oraz PT-3 IS / PT-4 IE; parametry przyłączy wg warunków przyłączenia [DO UZUPEŁNIENIA: warunki przyłączenia: ENEA Operator (nN), gestor wod.-kan., operator telekomunikacyjny — E-05].

Źródło danych: model/dzialka.yaml — uzbrojenie.projektowane

3.6. Ukształtowanie terenu i układ zieleni

§ 14 pkt 3 lit. f

Projektuje się niwelację terenu wyłącznie w otoczeniu budynku i utwardzeń: rzędne terenu projektowanego 101,20–101,63 m n.p.m. (teren istniejący 101,10–101,55 m n.p.m.); posadzka parteru $\pm 0,00 = 101,65$ m n.p.m., tj. 0,27 m ponad średni poziom terenu przy budynku. Teren przy budynku ze spadkiem $\geq 2\%$ od ścian (WT §316 ust. 2 (wymóg spływu); 2% — R8 3.5; W-019), opaska żwirowa wokół budynku ($13,3 \text{ m}^2$), odwodnienia liniowe przy drzwiach bezprogowych, przed garażem i przy bramie; na granicach działki rzędne projektowane równe istniejącym. Drenażu opaskowego nie projektuje się — piaski przepuszczalne, ZWG $\approx 3,8$ m p.p.t., posadowienie $\approx 0,5$ m p.p.t. (W-285); ochrona płyty: XPS + membrana SBS, opaska żwirowa i spadki terenu. Rzędne — rys. PZT-02.

Tabela 4. Odwodnienie powierzchniowe

Symbol	Rodzaj	Opis	Odbiornik
OL-1	liniowe	odwodnienie liniowe przed bramą garażu	SEP-1 → NT-E
OL-2	liniowe	odwodnienie liniowe przy progach HS	opaska / KD-W
OL-2W	liniowe	odwodnienie liniowe przy HS zach.	KD-W
OL-3	liniowe	odwodnienie liniowe podestu wejścia	KD-W
OL-4	liniowe	odwodnienie liniowe przy bramie wjazdowej — woda nie spływa na drogę	SEP-1 → NT-E
OZ-1	opaska żwirowa	opaska żwirowa 16/32 szer. 0,5 m na geowłókninie wokół budynku	—
NT-N	niecka	płytki niecka trawiasta przed elewacją pn.	pas zach. → ogród pd.
NT-E	niecka	płytki niecka trawiasta 2,3 m od elewacji wsch. garażu	ogród pd.
OL-5	liniowe	odwodnienie liniowe przed progiem DZ2 na szer. drzwi + 0,15 m z każdej strony	KD-E

Symbol	Rodzaj	Opis	Odbiornik
OL-6	liniowe	odwodnienie liniowe przy progu DZ3	RS8 → KD-E
NCH-1	niecka	niecka chłonna — przelew zbiornika	grunt (piaski, ZWG 3,8 m p.p.t.)

Źródło danych: model/dzialka.yaml — odwodnienia

Zieleń: trawniki (pozostała powierzchnia biologicznie czynna — pkt 4), żywopłoty na granicach bocznych i tylnej (122,8 m²), rabaty (71,0 m²), niecka chłonna jako ogród deszczowy. Drzewa:

Tabela 5. Drzewa istniejące i projektowane

Nr	Gatunek	Stan	Średnica korony [m]	Wysokość [m]
DR1	lipa drobnolistna (soliter na osi ogrodu)	projektowane	7,0	10,0
DR2	klon polny (cień letni tarasu zach.)	projektowane	5,0	8,0
DR3	grab pospolity	projektowane	4,5	7,0
DR4	jabłoń	projektowane	4,0	5,0
DR5	brzoza brodawkowata	istniejące — zachowane	4,0	12,0
DR6	sosna zwyczajna	istniejące — zachowane	4,5	11,0
DR7	grab kolumnowy (zieleń przy wjeździe)	projektowane	2,0	6,0

Przy drzewach zachowywanych — ochrona pni i systemu korzeniowego w zasięgu korony podczas robót. Obwody pni drzew istniejących [DO UZUPEŁNIENIA: obwód na wys. 5 cm — mapa do celów projektowych (u.o.p. art. 83f)].

4. Zestawienie powierzchni i wskaźników zagospodarowania

§ 14 pkt 4 RPB

Powierzchnie obliczono z geometrii modelu (lamała.wskazniki) wg definicji ustawy o planowaniu i zagospodarowaniu przestrzennym (upzp, t.j. Dz.U. 2026 poz. 538) art. 2 pkt 28–35 oraz § 14 pkt 4 RPB; powierzchnię zabudowy budynku pomniejsza się o tarasy naziemne, gzymsy, balkony i loggie (§ 14 pkt 4 lit. a RPB). Powierzchnie w m² z dokładnością do 0,01 m².

Tabela 6. Zestawienie powierzchni — działka nr ewid. 123/4 (1 600,00 m²)

Pozycja	Powierzchnia [m²]	Udział [%]
a) powierzchnia zabudowy		
budynek projektowany — rzut ścian zewnętrznych wszystkich kondygnacji nadziemnych	187,50	11,72
obiekty istniejące	0,00	0,00
informacyjnie: wariant kontrolny z rzutem płyt wysuniętych i okapów	218,08	13,63
b) drogi, parkingi, place i chodniki		
U1 — podjazd	48,61	3,04
U2 — dojście	9,04	0,56
U3 — łącznik dojście–podjazd	1,05	0,07
U4 — stanowisko pojemników	4,16	0,26
U5 — fundament jednostki zewn. PC na wibroizolacji	1,12	0,07
U6 — ścieżka gospodarcza	0,90	0,06
razem lit. b	64,87	4,05
c) powierzchnia biologicznie czynna		

Pozycja	Powierzchnia [m²]	Udział [%]
teren biologicznie czynny (upzp art. 2 pkt 28)	1 270,15	79,38
informacyjnie: 50 % dachu zielonego (rezerwa — nie wliczana)	29,53	1,85
d) inne części terenu (zgodność z MPZP)		
tarasy i podesty naziemne	66,75	4,17
opaska żwirowa przy budynku	13,33	0,83
powierzchnia kondygnacji P0 (upzp art. 2 pkt 33)	181,78	—
powierzchnia kondygnacji P1 (upzp art. 2 pkt 33)	117,81	—
powierzchnia kondygnacji P2 (upzp art. 2 pkt 33)	96,80	—
suma powierzchni kondygnacji nadziemnych (art. 2 pkt 32)	396,39	—

Powierzchnia zabudowy: suma rzutu poziomego budynku po zewnętrznym obrysie ścian zewnętrznych wszystkich kondygnacji nadziemnych (lico ocieplenia; wspornik bryły wyższej kondygnacji wliczony); tarasy naziemne, okapy, płyty wysunięte — nie wliczane.

Powierzchnia biologicznie czynna: teren zieleni modelu (trawnik, rabaty, żywopłoty, niecka chłonna) minus: parter, tarasy, utwardzenia (także ażurowe), opaska żwirowa, pojemniki, teren nad zbiornikiem (rzut ZAŁOŻONY — brak wymiarów zbiornika).

Źródło danych: lamela.wskazniki (model/budynek.yaml + model/działka.yaml)

Tabela 7. Bilans pokrycia terenu działki

Pokrycie terenu	Powierzchnia [m²]	Udział [%]
rzut parteru (teren pod budynkiem)	181,78	11,36
tarasy i podesty naziemne	66,75	4,17
utwardzenia (lit. b)	64,87	4,05
opaska żwirowa	13,33	0,83
teren biologicznie czynny (lit. c)	1 270,15	79,38
pozostałe (teren nad zbiornikiem retencyjnym, styki warstw)	3,12	0,19
Powierzchnia działki	1 600,00	100,00

Rzut parteru jest mniejszy od powierzchni zabudowy o rzut wysuniętych części wyższych kondygnacji (wspornik) nad terenem.

Tabela 8. Zgodność z ustaleniami MPZP — uchwała nr XII/123/2024 Rady Gminy Przykładowo z 21.03.2024 — teren 3MN (fikcyjny)

Lp.	Parametr	Wartość	Wymaganie	Podstawa	Wynik
1.	Udział powierzchni zabudowy	11,72 %	≤ 30 %	MPZP 3MN; upzp art. 2 pkt 35 [W-030]	✓ spełnia
2.	Udział powierzchni biologicznie czynnej (bez rezerwy dachu zielonego)	79,38 %	≥ 50 %	MPZP 3MN; upzp art. 2 pkt 28–29 [W-031]	✓ spełnia
3.	Intensywność zabudowy (nadziemna)	0,248	0,05–0,80	MPZP 3MN; upzp art. 2 pkt 31–33 (nadziemna) [W-032]	✓ spełnia
4.	Wysokość zabudowy (czerpnia wentylacji (dachowa))	10,27 m	≤ 11,00 m (rezerwa proj. 0,30 m)	MPZP 3MN; upzp art. 2 pkt 30 [W-033]	✓ spełnia
5.	Liczba kondygnacji nadziemnych	3	≤ 3	MPZP 3MN; warunek WT §213 pkt 1 lit. a [W-034]	✓ spełnia
6.	Spadek dachów (dachy płaskie)	1,15 °	≤ 12°	MPZP 3MN [W-035]	✓ spełnia
7.	Miejsca postojowe (garaż 2 + naziemne 2)	4 szt.	≥ 2 na lokal mieszkalny	MPZP 3MN; WT §18 ust. 2 [W-036]	✓ spełnia

Lp.	Parametr	Wartość	Wymaganie	Podstawa	Wynik
8.	Nieprzekraczalna linia zabudowy — element najbliższy linii	0,95 m przed linią (7,00 m od linii)	rozgraniczającej; brak przekroczeń	MPZP 3MN (fikcyjny) — nieprzekraczalna linia zabudowy od 1KDD; żaden element jej nie przekracza [W-006]	✓ spełnia
9.	Wysokość ogrodzenia od drogi (ażurowe)	1,50 m	≤ 1,60 m	MPZP 3MN (ażurowe, bez prefabrykatów betonowych) [W-038]	✓ spełnia

Ustalenia MPZP przykładowe [DANE PRZYKŁADOWE – FIKCYJNE]; wartości wymagań z docs/10_podstawy_prawne/wymagania.yaml.
Wysokość zabudowy wg upzp art. 2 pkt 30 lit. a: $H = z_{top} - t_{śr} = 111,65 - 101,38 \text{ m n.p.m.}$ ($H = z_{top} - t_{śr}$; z_{top} — najwyższy punkt budynku na dachu/ścianie/attyce (wyłączenia zamknięte: komin, nadbudówka maszynowni dźwigu lub innego pomieszczenia technicznego, wyjście z klatki; czerpnia, wyrzutnia, wywiewka, PV, wylaz, świetlik — wliczane); $t_{śr} = (t_{min} + t_{max}) / 2$ na obwodzie rzutu ścian zewnętrznych, w każdym punkcie niższa z rzędnych terenu istniejącego/projektowanego).

5. Informacje o ograniczeniach, zabytkach, wpływie eksploatacji górniczej i zagrożeniach

§ 14 pkt 5 RPB

5.1. Ograniczenia i zakazy wynikające z aktów prawa miejscowego

§ 14 pkt 5 lit. a

Działka leży na terenie objętym miejscowym planem zagospodarowania przestrzennego — uchwała nr XII/123/2024 Rady Gminy Przykładowo z 21.03.2024 — teren 3MN (fikcyjny), przeznaczenie: zabudowa mieszkaniowa jednorodzinna wolnostojąca [DANE PRZYKŁADOWE – FIKCYJNE] [DO UZUPEŁNIENIA: wypis i wyrys z MPZP (E-02)]. Ustalenia istotne dla zagospodarowania: nieprzekraczalna linia zabudowy 6,00 m od linii rozgraniczającej drogi 1KDD; wskaźniki powierzchni zabudowy, powierzchni biologicznie czynnej, intensywności, wysokości, liczby kondygnacji, geometrii dachów i liczby miejsc postojowych (sprawdzenie — pkt 4); kolorystyka elewacji: biele, szarości, grafit, naturalne drewno, beton architektoniczny (MPZP 3MN); ogrodzenie od drogi ażurowe, bez prefabrykatów betonowych; wody opadowe zagospodarowane w granicach działki; ogrzewanie ze źródeł niskoemisyjnych lub OZE (pompa ciepła powietrze–woda, budynek bez przyłącza gazowego).

5.2. Ochrona konserwatorska

§ 14 pkt 5 lit. b

Działka nie jest wpisana do rejestru zabytków ani do gminnej ewidencji zabytków i nie leży na obszarze objętym ochroną konserwatorską (MPZP bez ustaleń ochrony konserwatorskiej) [DANE PRZYKŁADOWE – FIKCYJNE].

5.3. Wpływ eksploatacji górniczej

§ 14 pkt 5 lit. c

Nie dotyczy — działka nie leży w granicach terenu górniczego [DANE PRZYKŁADOWE – FIKCYJNE].

5.4. Zagrożenia dla środowiska oraz higieny i zdrowia

§ 14 pkt 5 lit. d

Zamierzenie nie jest przedsięwzięciem mogącym znacząco oddziaływać na środowisko (rozporządzenie Rady Ministrów, Dz.U. 2019 poz. 1839 ze zm., § 3 ust. 1 pkt 55 lit. a — progi powierzchni zabudowy mieszkaniowej nieosiągnięte [W-026]) — decyzja o środowiskowych uwarunkowaniach nie jest wymagana. Charakterystyka oddziaływań:

Tabela 9. Oddziaływania i zagrożenia

Lp.	Oddziaływanie	Charakterystyka	Ocena
1.	Hałas — jednostka zewnętrzna pompy ciepła	PC-R290-09 (przykład), $L_{WA} = 58 / 53 \text{ dB(A)}$ (dzień / tryb nocny) [ZAŁ]; odległość od granicy (działka sąsiednia 123/5) 7,60 m; poziom na granicy: noc 27,4 dB(A), dzień 32,4 dB(A)	≤ 40 dB noc, ≤ 50 dB dzień (rozp. MŚ t.j. Dz.U. 2014 poz. 112, tab. 1 lp. 2a (22:00–6:00, 1 h)); cel ≤ 35 dB [W-024] — spełnia

Lp.	Oddziaływanie	Charakterystyka	Ocena
2.	Emisje do powietrza	budynek bez źródeł spalania (ogrzewanie i c.w.u. — pompa ciepła, energia elektryczna, PV)	brak emisji z instalacji spalania
3.	Ścieki i wody opadowe	ścieki bytowe do sieci; wody opadowe na działce; wody z podjazdu i garażu przez separator	brak zrzutu do wód i na teren sąsiedni (pkt 3 lit. b, pkt 7)
4.	Odpady	odpady komunalne segregowane w stanowisku pojemników przy ogrodzeniu	odbiór wg regulaminu gminy
5.	Zieleń	drzewa do usunięcia: brak; drzewa istniejące zachowane	zezwolenie / zgłoszenie usunięcia drzew nie dotyczy (u.o.p. art. 83f [W-023])
6.	Grunty rolne	klasy gruntów [ZAL] — mineralne RIVb/RV [DO UZUPEŁNIENIA: wypis z EGiB (E-03)]	decyzja o wyłączeniu z produkcji nie dotyczy przy klasach IV–VI mineralnych [W-025]
7.	Czynnik chłodniczy R290 (propan)	strefa bezpieczeństwa wokół jednostki zewnętrznej bez otworów, wpustów, studzienek i źródeł zapłonu	elementy w strefie: brak — spełnia [W-156]

Źródło danych: lamela.obliczenia.sanitarne.ogrzewanie (hałas: PORT PC p. 4.4); audyt A1; model/działka.yaml

6. Dane dotyczące warunków ochrony przeciwpożarowej

§ 14 pkt 6 RPB

Budynek mieszkalny jednorodzinny, kategoria zagrożenia ludzi **ZL IV** (WT §209 ust. 2 pkt 4), grupa wysokości **N** — budynek niski (wysokość wg WT § 6: 9,97 m; WT §8 pkt 1). Odległość od najbliższego budynku sąsiedniego (dz. 123/5): 13,72 m ≥ 8,0 m (WT §271 ust. 1; W-010) — ściany zewnętrzne i dach nierozprzestrzeniające ognia (PAB).

Droga pożarowa — nie jest wymagana: budynek ZL IV niski nie należy do obiektów, dla których wymaga się drogi pożarowej (rozporządzenie MSWiA w sprawie przeciwpożarowego zaopatrzenia w wodę oraz dróg pożarowych, Dz.U. 2009 nr 124 poz. 1030, § 12 ust. 1). Dojście od drogi publicznej 1KDD — przez furtkę utwardzonym dojściem długości ok. 7,0 m do wejścia głównego (rys. PZT-01).

Przeciwpożarowe zaopatrzenie w wodę — wymagana wydajność ≥ 10 dm³/s (rozp. Dz.U. 2009 nr 124 poz. 1030 §3 ust. 2 (5 dm³/s wg ust. 3); W-217) z sieci wodociągowej w drodze 1KDD: najbliższy hydrant zewnętrzny DN80 (ul. Lipowa), w odległości ok. 40 m od budynku [DANE PRZYKŁADOWE – FIKCYJNE] [DO UZUPEŁNIENIA: potwierdzenie lokalizacji i wydajności hydrantu przez gestora sieci]. Przeciwpożarowy wyłącznik prądu — przy złączu kablowo-pomiarowym / wejściu (PT-4 IE).

7. Dane dotyczące ochrony ludności

§ 14 pkt 6a RPB

Nie dotyczy. Informacje i dane dotyczące warunków ochrony ludności podaje się w przypadku obiektu zbiorowej ochrony (§ 14 pkt 6a RPB, dodany Dz.U. 2026 poz. 597). Budynek mieszkalny jednorodzinny bez kondygnacji podziemnych nie jest obiektem, dla którego ustawa z dnia 5 grudnia 2024 r. o ochronie ludności i obronie cywilnej (Dz.U. 2024 poz. 1907 ze zm.) przewiduje budowlę ochronną lub miejsce doraźnego schronienia (art. 93–95 tej ustawy).

8. Inne dane wynikające ze specyfiki zamierzenia

§ 14 pkt 7 RPB

8.1. Retencja i zagospodarowanie wód opadowych

§ 14 pkt 7; W-143...W-145

Metoda bilansowa Aquanet (2024), opad PANDa 2050 (C = 10 lat) [ZAL]; współczynnik filtracji gruntu $k_f = 1,0 \cdot 10^{-4}$ m/s [ZAL] [DO UZUPEŁNIENIA: k_f z badań podłoża (E-04)]. Wyniki (lamela.obliczenia.sanitarne.deszczowa):

Tabela 10. Retencja wód opadowych (wariant bazowy: zbiornik szczelny + niecka)

Lp.	Parametr	Wartość	Wymaganie	Podstawa	Wynik
1.	Powierzchnia zredukowana zlewni (dachy)	210,01 m ²	—	Aquanet 2024 tab. 2	—
2.	Pojemność szczelnego zbiornika retencyjnego	5,00 m ³	≤ 5,0 m ³	PB art. 29 ust. 2 pkt 36 (5–15 m ³ — zgłoszenie, ust. 1 pkt 38) [W-145]	✓ spełnia
3.	Niecka chłonna 28,0 m ² × 0,30 m — pojemność	8,40 m ³	≥ V_min = 1,2 · V_obl = 5,71 m ³	Aquanet 2024 zał. C (1,1 przy przelewie awaryjnym)	✓ spełnia
4.	Czas opróżniania niecki	1,63 h	≤ 24 h	Aquanet 2024 zał. C	✓ spełnia
5.	Lokalizacja — zbiornik: odl. od granic / od budynku	min 10,60 / 5,70 m	≥ 2,0 / ≥ 3,0	R8 3.5 [W-144] [W-144, W-145]	✓ spełnia
6.	Lokalizacja — rozsączanie: odl. od granic / od budynku	min 8,10 / 12,70 m	≥ 2,0 / ≥ 3,0	R8 3.5 [W-144] [W-144, W-145]	✓ spełnia

Zbiornik ≤ 5 m³ nie wymaga pozwolenia ani zgłoszenia (PB art. 29 ust. 2 pkt 36); rozsączanie skrzynkowe — wyłącznie po stanowisku PGW Wody Polskie (rejestr D-05, E-07).

8.2. Warunki gruntowe i pozostałe dane

Kategoria geotechniczna: II (opinia geotechniczna + dokumentacja badań podłoża (≥ 3 sondowania do 6 m) + projekt geotechniczny (W-280...W-282)); grunt: piasek średni (MSa), średniozagęszczony, zwierciadło wody gruntowej ok. 3,8 m p.p.t. [DANE PRZYKŁADOWE – FIKCYJNE] [DO UZUPEŁNIENIA: opinia geotechniczna (E-04)]. Instalacja fotowoltaiczna na dachach: 15 modułów, 6,45 kWp ≤ 6,5 kWp (PB art. 29 ust. 4 pkt 3 lit. c; W-194).

9. Informacja o obszarze oddziaływania obiektu

§ 14 pkt 8, § 18 RPB

Obszar oddziaływania obiektu (PB art. 3 pkt 20 — teren wyznaczony w otoczeniu obiektu na podstawie przepisów odrębnych, wprowadzających związane z tym obiektem ograniczenia w zabudowie tego terenu) określono na podstawie przepisów wymienionych w tabeli (§ 18 pkt 1 RPB) oraz: WT § 23 (miejsca gromadzenia odpadów — dla zabudowy jednorodzinnej odległości nieustalone), WT § 28 (wody opadowe — zagospodarowane na działce), ustawy – Prawo wodne (t.j. Dz.U. 2025 poz. 960 ze zm.) art. 234 ust. 1 (zakaz zmiany kierunku i natężenia odpływu wód opadowych ze szkodą dla gruntów sąsiednich i odprowadzania wód na grunty sąsiednie), ustaleń MPZP (linia zabudowy, wskaźniki — pkt 4). Wartości — minimum dla wszystkich elementów budynku i granic niedrogowych (audyt A1).

Tabela 11. Przepisy wyznaczające obszar oddziaływania i sprawdzenie

Przepis	Ograniczenie	Projekt	Wymaganie	Ocena	Element
WT § 12 ust. 1 pkt 1	ściany z oknami/drzwiami od granicy	5,73 m	≥ 4,00 m	spełnia	S0-03
WT § 12 ust. 1 pkt 2	ściany bez otworów od granicy	11,18 m	≥ 3,00 m	spełnia	S2-06
WT § 12 ust. 6 pkt 1	okapy, płyty wysunięte, daszki od granicy	5,18 m	≥ 1,50 m	spełnia	OB-A
WT § 13	przesłanianie budynków sąsiednich: odległość ≥ wysokość przesłaniania	13,72 m	≥ 10,36 m (z_top – t_min)	spełnia	budynki sąsiednie
WT § 60	nasłonecznienie budynków sąsiednich w dniach równonocy (ocena uproszczona)	10,0 h	≥ 3 h	spełnia	cień budynku
WT § 19 ust. 2	stanowiska postojowe naziemne od granicy	6,30 m	≥ 3,00 m	spełnia	MP3, MP4
WT § 271 ust. 1	odległość ścian budynków ZL od budynków sąsiednich	13,72 m	≥ 8,00 m	spełnia	—

Przepis	Ograniczenie	Projekt	Wymaganie	Ocena	Element
u.d.p. art. 43 ust. 1	budynek od zewnętrznej krawędzi jezdni drogi gminnej 1KDD	9,88 m	≥ 6,00 m	spełnia	—
POŚ art. 144 ust. 2; Dz.U. 2014 poz. 112	hałas instalacji (PC) na granicy — pora nocy	27,4 dB(A)	≤ 40 dB(A)	spełnia	działka sąsiednia 123/5

WT §12 ust. 1 pkt 1 i część wspólna (Dz.U. 2023 poz. 2442, 2024 poz. 726); każdy uskok = odrębna ściana [W-001]; WT §12 ust. 6 pkt 1 (płyty wysunięte traktowane jak okapy — interpretacja); WT §60 ust. 1 (równonoc) — 21.03.2027, 23.09.2026, godz. 7–17

Obszar oddziaływania obiektu mieści się w całości na działce nr ewid. 123/4, na której obiekt został zaprojektowany (§ 18 pkt 2 RPB).

CZĘŚĆ RYSUNKOWA

§ 7 ust. 1 pkt 4, § 15–17 RPB


OBIEKT	Budynek mieszkalny jednorodzinny wolnostojący „Dom LAMELA”
ELEMENT PROJEKTU	PZT — Projekt zagospodarowania działki
AUTORZY RYSUNKÓW	[DO UZUPEŁNIENIA: imię i nazwisko] — architektoniczna bez ograniczeń, nr upr. [DO UZUPEŁNIENIA: nr uprawnień budowlanych] [DO UZUPEŁNIENIA: imię i nazwisko] — instalacyjna (cieplne, wentylacyjne, gazowe, wod.-kan.) bez ograniczeń, nr upr. [DO UZUPEŁNIENIA: nr uprawnień budowlanych] [DO UZUPEŁNIENIA: imię i nazwisko] — instalacyjna (elektryczne i elektroenergetyczne) bez ograniczeń, nr upr. [DO UZUPEŁNIENIA: nr uprawnień budowlanych]
SPRAWDZAJĄCY	nie dotyczy (art. 20 ust. 3 pkt 2 PB)
DATA	25 września 2026 r.
LICZBA RYSUNKÓW	3 rysunki
POSTAĆ	PDF wektorowy (RPB § 2b ust. 2); arkusze w formatach oryginalnych wg PN-EN ISO 5457. W postaci papierowej arkusze składa się do formatu A4 „do wpięcia” (RPB § 2a) — tabliczka na wierzchu.
NUMERACJA	rysunki identyfikuje numer rysunku w metryce (RPB § 6 ust. 3, § 10 ust. 1)

Tabela 12. Wykaz rysunków

Lp.	Nr rysunku	Tytuł rysunku	Skala	Format	Wymiary [mm]	Uwagi
1.	PZT-01	PLAN ZAGOSPODAROWANIA DZIAŁKI	1:500	A2	594×420	podkład: mapa przykładowa (fikcyjna) — [DO UZUPEŁNIENIA: mapa do celów projektowych z klauzulą lub oświadczeniem geodety (E-01)]
2.	PZT-02	PLAN SZCZEGÓŁOWY — WYMIARY I RZĘDNE	1:200	A2	594×420	
3.	PZT-03	RYSUNEK KOORDYNACYJNY UZBROJENIA TERENU	1:200	A2	594×420	

MAPA DO CELÓW PROJEKTOWYCH — PODKŁAD PRZYKŁADOWY

PODKŁAD PRZYKŁADOWY — mapa do celów projektowych fikcyjna [DANE PRZYKŁADOWE – FIKCYJNE], narysowana z modelu działki (działka.yaml); w projekcie rzeczywistym — aktualna mapa do celów projektowych wg art. 34 ust. 3 pkt 1 PB (z klauzulą urzędową lub oświadczeniem geodety — art. 34b PB), treść i opis mapy wg § 32–33 rozp. w sprawie standardów technicznych (t.j. Dz.U. 2022 poz. 1670), znaki wg zał. 4 rozp. w sprawie BDOT500 i mapy zasadniczej (Dz.U. 2021 poz. 1385; oba akty zweryfikowane w ELI 25.09.2026 — status: obowiązujące).

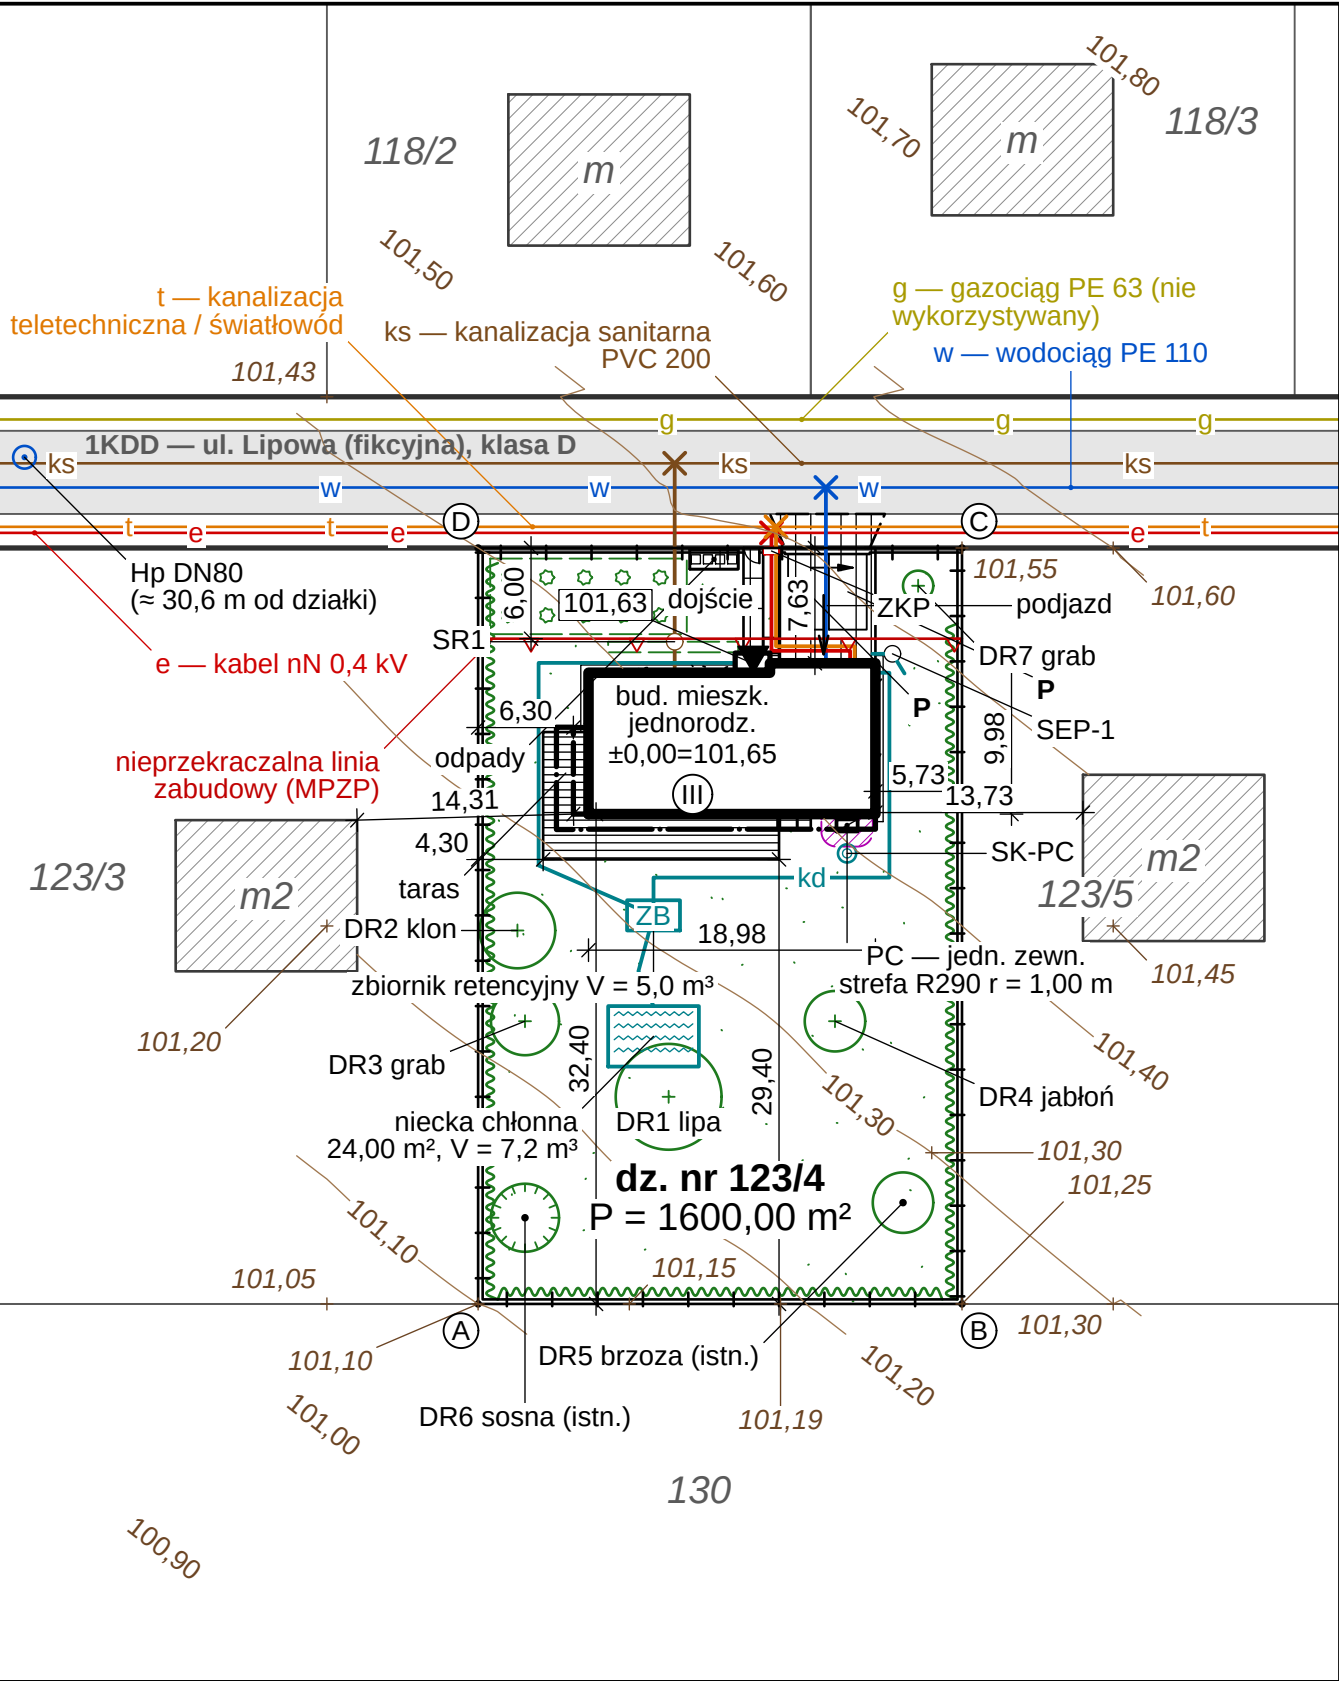

PLAN ZAGOSPODAROWANIA DZIAŁKI 1:500

ZESTAWIENIE POWIERZCHNI I WSKAŹNIKÓW ZAGOSPODAROWANIA (RPB § 14 pkt 4, MPZP)

Wskaźnik / element	Projekt	MPZP / wymaganie	Zgodność
Powierzchnia działki nr 123/4	1600,00 m ²	—	
Pow. zabudowy (upzp art. 2 pkt 35)	187,50 m ²	≤ 480,00 m ²	TAK
Udział pow. zabudowy	11,72%	≤ 30%	TAK
– z płytami i okapami (kontrolnie)	218,08 m ² (13,63%)	informacyjnie	TAK
Drogi, dojścia, place	64,87 m ²	—	
Tarasы наземные, подесты	67,27 m ²	—	
Opaska żwirowa	13,13 m ²	—	
PBC (upzp art. 2 pkt 28)	1269,84 m ² (79,36%)	≥ 800,00 m ² (50%)	TAK
– z 50 % dachu ziel. D4 (rezerwa)	1299,37 m ² (81,21%)	informacyjnie	
Pow. kondygnacji nadz. (P0+P1+P2)	396,39 m ²	80,00 m ² –1280,00 m ²	TAK
Nadziemna intensywność zabudowy	0,248	0,05–0,80	TAK
Wysokość zabudowy (art. 2 pkt 30)	10,28 m	≤ 11,00 m	TAK
Wysokość budynku (WT § 6)	9,94 m	N: ≤ 12,00 m	TAK
Kondygnacje nadziemne	3	≤ 3	TAK
Miejsca postojowe (garaż + zewn.)	2 + 2	≥ 2	TAK
Dach — kąt nachylenia	1,1° (płaski)	płaski ≤ 12° lub 30–45°	TAK
Lico ścian od linii zabudowy	1,63 m	nie przekraczać	TAK
Elementy poza linią zabudowy	brak	—	

MPZP: uchwała nr XII/123/2024 Rady Gminy Przykładowo z 21.03.2024 — teren 3MN (fikcyjny). Limity: konfiguracja arkuszy (brief § 3) — BRAK W MODELU [DO UZUPEŁNIENIA]. Wartości z modułu lamela.wskazniki (jedyne źródło; definicje upzp art. 2 pkt 28–35, t.j. Dz.U. 2026 poz. 538): PBC bez nawierzchni ażurowych, opaski, pojemników i terenu nad zbiornikiem; dach zielony (≥ 10 m²) w 50 % — tylko rezerwa. Wysokość zabudowy = z_{top} 111,68 (wywiewka kanalizacyjna 1 (z = pokrycie + 0,50 m — ZAŁOŻENIE, brak rzędnej w modelu)) – t_{śr} 101,40 (t_{min} 101,32, t_{max} 101,48 na obwodzie rzutu ścian zewn.); w każdym punkcie niższa z rzędnych terenu istniejącego/projektowanego; bez założenia: 10,25 m (czterpnia wentylacji (dachowa)). WT § 6: od terenu przy wejściu O0-O4 (101,33) do wierzchu stropodachu D1 (bez attyki) — grupa N.

ODLEGŁOŚCI OD GRANIC DZIAŁKI (WT § 12)

Granica	Element (płaszczyzna ściany)	Odl. [m]	Wymagana [m]	Zgodność
S (130)	ściana P0 z otworami	32,40	≥ 4,00	TAK
S (130)	T1 — okap/płyta/taras	29,40	≥ 1,50	TAK
E (123/5)	ściana P0 z otworami	5,73	≥ 4,00	TAK
E (123/5)	ściana P2 bez otworów	15,60	≥ 3,00	TAK
E (123/5)	PL-D — okap/płyta/taras	5,73	≥ 1,50	TAK
N (1KDD)	ściana P0 z otworami	7,63	nie dot. (ust. 10)	—
N (1KDD)	ściana P2 bez otworów	11,88	nie dot. (ust. 10)	—
N (1KDD)	PL-DA — okap/płyta/taras	6,95	nie dot. (ust. 10)	—
W (123/3)	ściana P2 z otworami	6,30	≥ 4,00	TAK
W (123/3)	ściana P2 bez otworów	11,18	≥ 3,00	TAK
W (123/3)	T1 — okap/płyta/taras	4,30	≥ 1,50	TAK

WT § 12 ust. 1: 4,00 m — ściana z oknami/drzwiami, 3,00 m — bez otworów (każda płaszczyzna ściany osobno); ust. 6: 1,50 m — okap, taras, daszek; ust. 10: od działki drogowej — nie dotyczy. Odległość w poziomie w miejscu najmniejszego oddalenia (§ 9). WT stosowane na podstawie art. 102a PB.


LEGENDA

OBSZAR ODDZIAŁYWANIA OBIEKTU (PB art. 3 pkt 20; RPB § 14 pkt 8)


Obszar oddziaływania obiektu mieści się w całości w granicach działki 123/4 (PB art. 3 pkt 20); odległości od granic ≥ 4,0 m (ściany z otworami ≥ 5,70 m, płyty ≥ 5,20 m), przesłanianie i nasłonecznienie sąsiednich budynków (≥ 8 m od granic) bez ograniczeń (WT §13, §60), hałas PC ≤ 40 dB(A) nocą na granicy (W-024), wody opadowe zagospodarowane na działce (PW art. 234), brak odprowadzania na drogę. Podstawa ustalenia (RPB § 18 pkt 1): WT § 12, 13, 19, 23, 28–29, 60, 271 (art. 102a PB); u.d.p. art. 43; POŚ art. 144 ust. 2 i rozp. MŚ w sprawie dopuszczalnych poziomów hałasu (Dz.U. 2014 poz. 112); PW art. 234; ustalenia MPZP.

OBJAŚNIENIA I UWAGI

- Wymiary i odległości w m (dokładność 0,01 m), rzędne w m n.p.m. (PL-EVRF2007-NH).
- Układ współrzędnych: lokalny układ działki (x → wschód, y → północ, początek w narożniku A); w projekcie rzeczywistym — układ PL-2000 strefa 6 z mapy do celów projektowych.
- Obrys budynku — lico zewnętrzne ścian parteru na wys. 1,0 m nad terenem; wspornik bryły A (II piętro) — obrys wyższych kondygnacji; płyty wspornikowe, okapy i daszki — przewieszenia (PN-B-01027 poz. 1.6).
- Wody opadowe zagospodarowane w granicach działki: rury spustowe → kolektory KD → zbiornik retencyjny szczelny → przelew do niecki chłonnej; odwodnienie liniowe przed bramą — brak spływu na drogę (MPZP; u.d.p. art. 39 ust. 1 pkt 9; WT § 28–29).
- Wymiary i rzędne szczegółowe — rys. PZT-02; uzbrojenie i koordynacja sieci — rys. PZT-03.
- Zjazd z drogi 1KDD pokazano jako przedłużenie bramy do krawędzi jezdni — geometria zastępcza [DO UZUPEŁNIENIA]: szerokość, skosy/łuki, nawierzchnia i przepust wg zezwolenia zarządcy drogi (u.d.p. art. 29 ust. 3a).
- Braki danych modelu (9 poz.) oznaczono [DO UZUPEŁNIENIA]; wykaz: projekt/02_PZT/BRAKI_DANYCH.mxd.
- Rysunek wygenerowany automatycznie z modelu model/budynek.yaml (wersja 1.0, 2026-09-25) — generatory lamela.views.

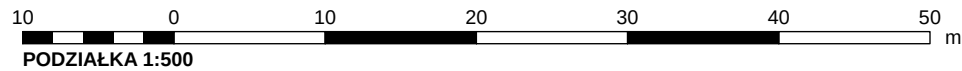

REW.	OPIS ZMIANY	DATA
0	Wydanie — rysunek wygenerowany z modelu	2026-09-25
PRACOWNIA PROJEKTOWA	PRACOWNIA PROJEKTOWA — nazwa do uzupełnienia	STADIUM
adres pracowni do uzupełnienia		PB
BRANŻA	ZAGOSPODAROWANIE TERENU	
INWESTOR (do uzupełnienia)	OBJEKT / NAZWA ZAMIERZENIA BUDOWLANEGO	
Budynek mieszkalny jednorodzinny wolnostojący „Dom LAMELA” z zagospodarowaniem działki		
ADRES / LOKALIZACJA (NR DZIAŁKI, OBRĘB, JEDN. EWIDENCYJNA)		KAT. OBIEKTU
ul. Lipowa (fikcyjna), dz. nr ewid. 123/4, obręb 0005 Przykładowo, gm. Przykładowo (fikcyjna)		I
FUNKCJA	IMIĘ I NAZWISKO	SPECJALNOŚĆ, NR UPRAWNIENI
Projektant		DATA
Projektant (wsp.)		PODPIS
Sprawdzający		
Opracował		
TYTUŁ RYSUNKU		
PLAN ZAGOSPODAROWANIA DZIAŁKI		
SKALA	FORMAT	DATA WYDANIA
1:500	A2	2026-09-25
RODZAJ DOK.	NR RYSUNKU	ARKUSZ
plan zagospodarowania	PZT-01	1/3
REW.	0	

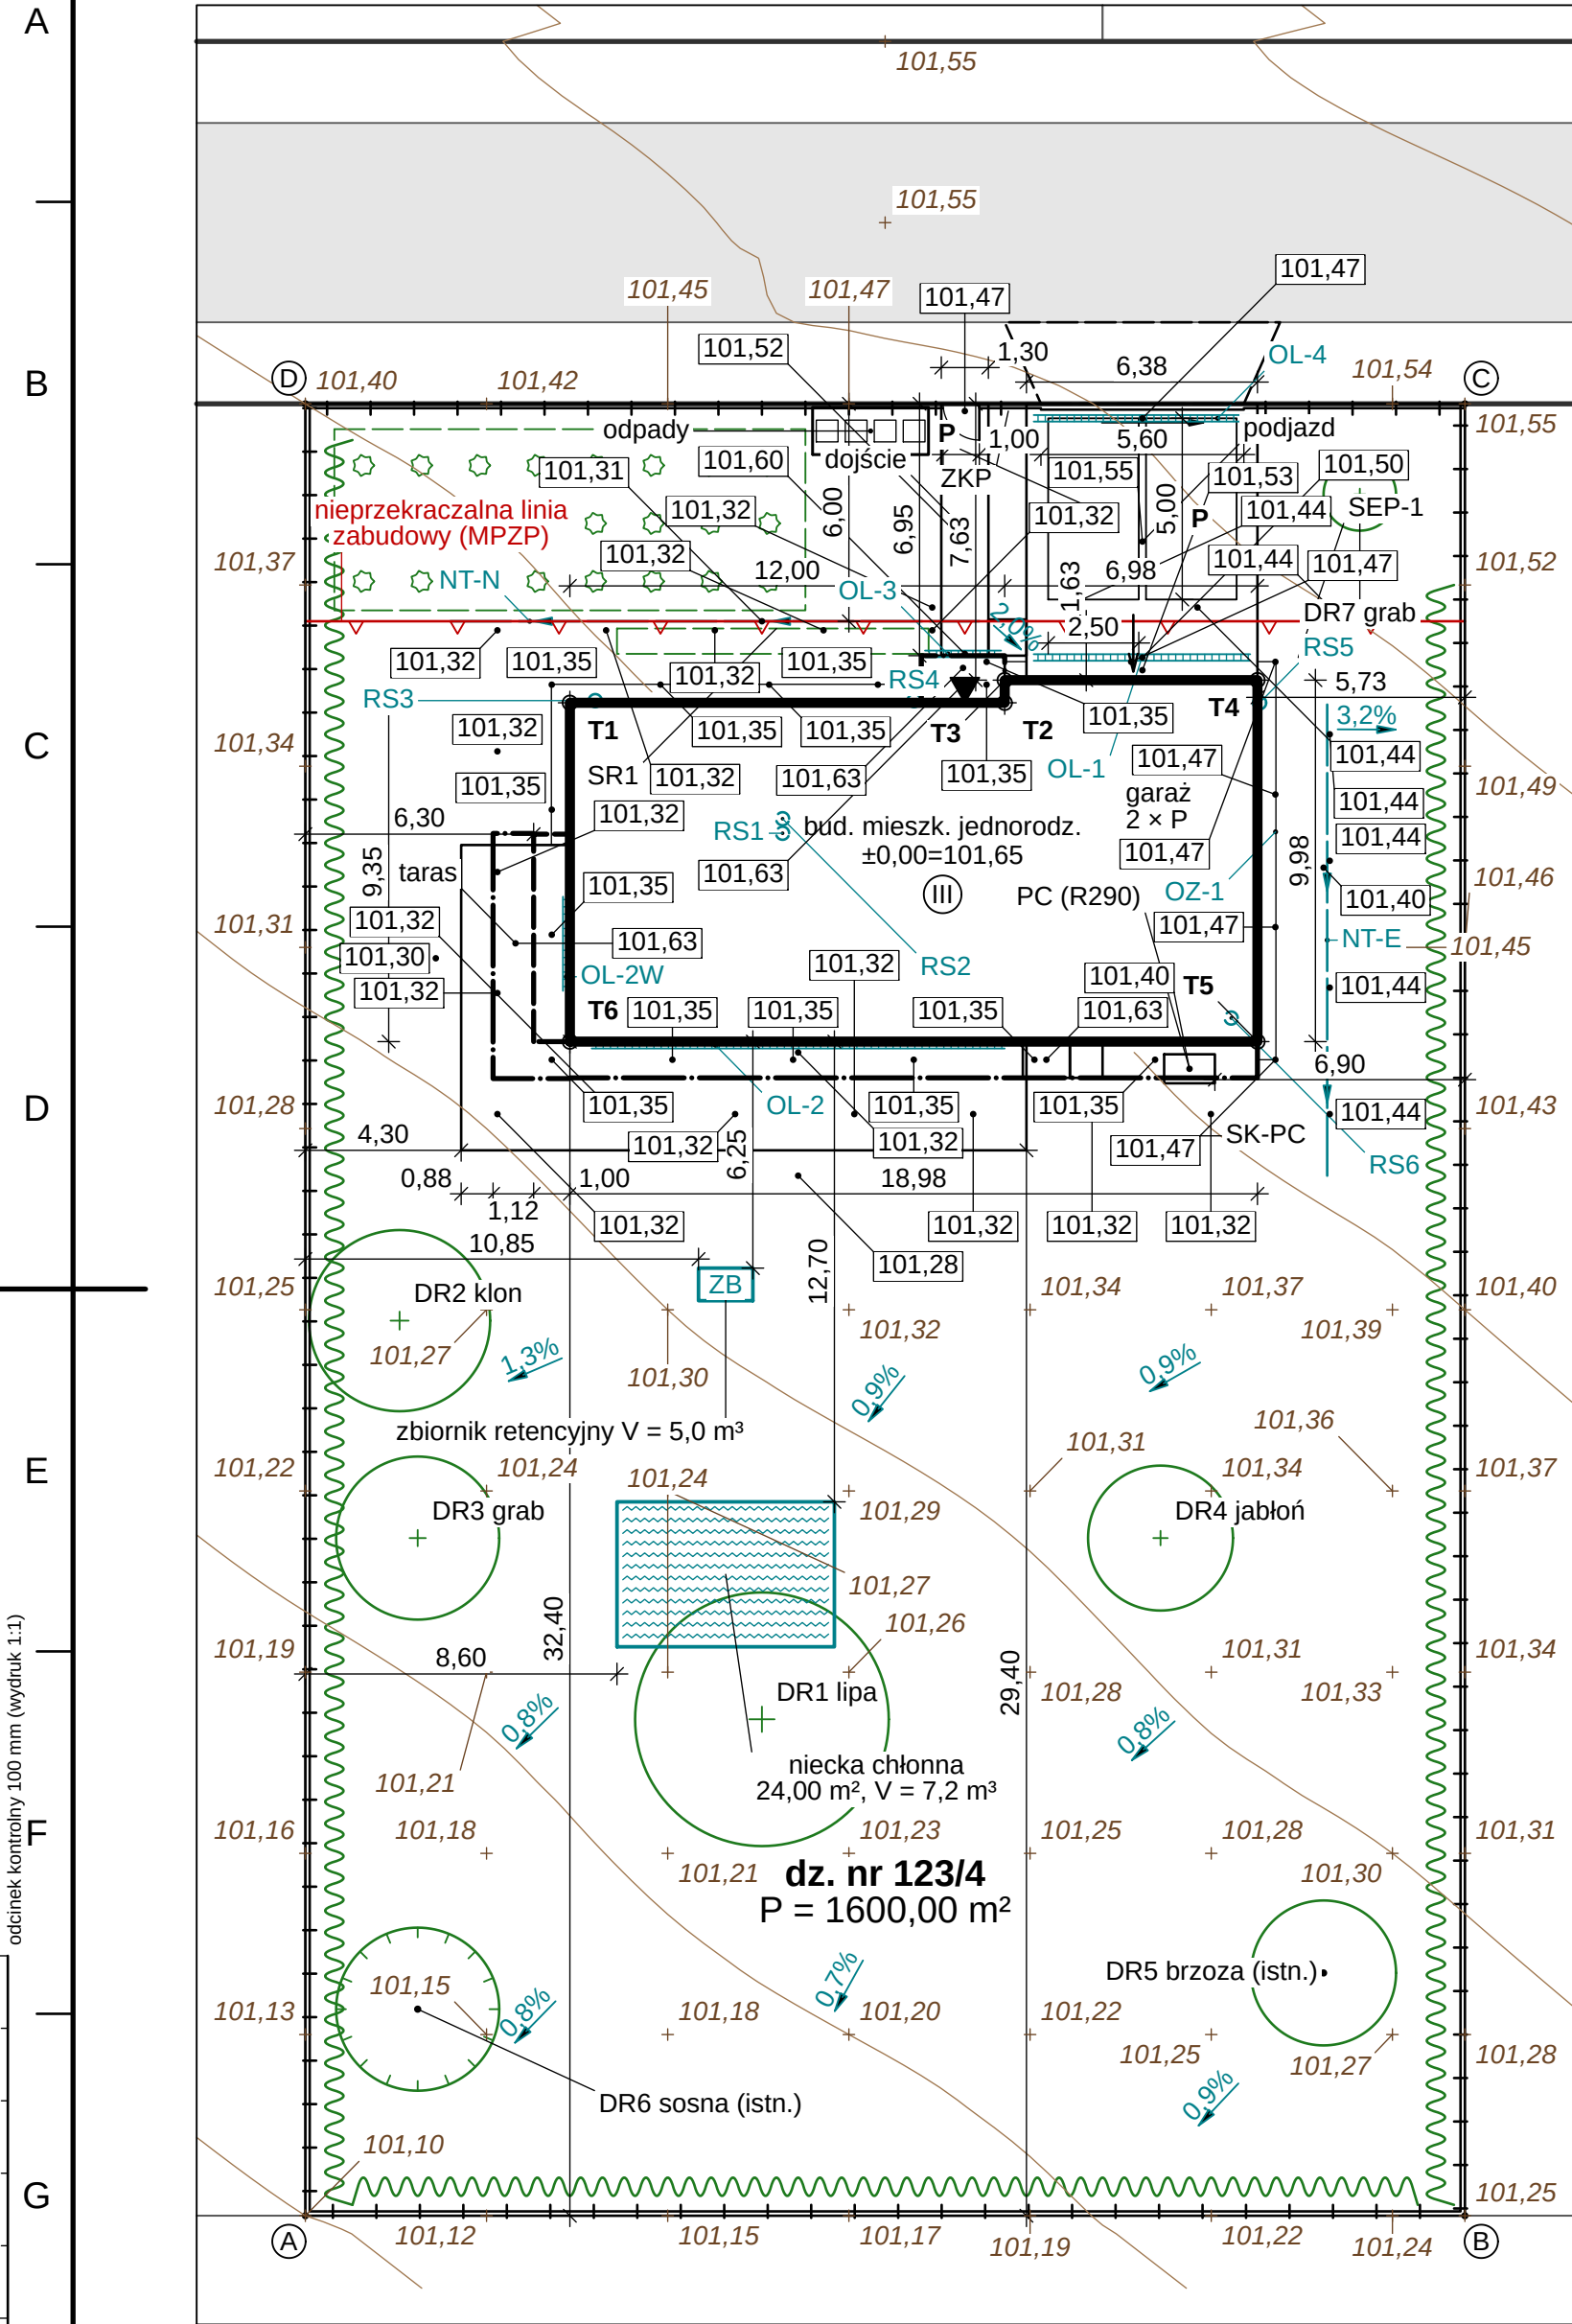

PLAN SZCZEGÓŁOWY — WYMIARY I RZĘDNE 1:200

WYKAZ PUNKTÓW TYCZENIA I GRANICZNYCH

Pkt	x [m]	y [m]	Opis
T1	7,30	41,75	narożnik obrysu parteru
T2	19,30	41,75	narożnik obrysu parteru
T3	19,30	42,38	narożnik obrysu parteru
T4	26,28	42,38	narożnik obrysu parteru
T5	26,28	32,40	narożnik obrysu parteru
T6	7,30	32,40	narożnik obrysu parteru
A	0,00	0,00	punkt graniczny działki
B	32,00	0,00	punkt graniczny działki
C	32,00	50,00	punkt graniczny działki
D	0,00	50,00	punkt graniczny działki

Układ lokalny działki: początek — narożnik A, x → wschód, y → północ. W projekcie rzeczywistym współrzędne w układzie PL-2000 (X — północ, Y — wschód) z mapy do celów projektowych; tyczenie — geodeta uprawniony (PB art. 43 ust. 1).

RZĘDNE CHARAKTERYSTYCZNE [m n.p.m.]

Poziom	Rzędna
±0,00 — posadzka parteru	101,65
T1 — deska kompozytowa...	101,63
T2 — płyty betonowe 60...	101,63
T3 — płyty betonowe 60...	101,63
teren proj. przy wejściu głównym	101,63
teren na obwodzie ścian — min.	101,32
teren na obwodzie ścian — maks.	101,48
najwyższy punkt budynku	111,68
zwierciadło wody gruntowej (ZWG)	97,60

Rzędne projektowane terenu: spadek $\geq 2\%$ od budynku; na granicach działki rzędne istniejące (bez zmiany spływu na działki sąsiednie — WT § 29, PW art. 234).

ODWODNIENIE POWIERZCHNIOWE

Ozn.	Typ	Wymiar	Spadek	Odbiornik
OL-1	liniowe	L = 5,98 m	0,5 %	SEP-1 → NT-E
OL-2	liniowe	L = 11,40 m	0,5 %	opaska / KD-W
OL-2W	liniowe	L = 2,60 m	0,5 %	KD-W
OL-3	liniowe	L = 2,10 m	0,5 %	KD-W
OL-4	liniowe	L = 5,98 m	0,5 %	SEP-1 → NT-E
OZ-1	opaska żwir.	b = 0,50 m	—	—
NT-N	niecka	L = 14,60 m	0,5 %	KD-W
NT-E	niecka	L = 13,00 m	0,6 %	ogród pd.
NCH-1	niecka	A = 24,00 m ²	—	grunt (piaski, ZWG...

DR-0: NIE PROJEKTUJE SIĘ — piaski przepuszczalne, ZWG $\approx 3,8$ m p.p.t., posadowienie $\approx 0,5$ m p.p.t. (W-285); ochrona płyty: XPS + membrana SBS, opaska żwirowa i spadki terenu

NAWIERZCHNIE UTWARDZONE I TARASY

Ozn.	Nawierzchnia	Pow.	Spadek
U1	podjazd	48,61 m ²	1,5 %
U2	dojście	9,04 m ²	2,0 %
U3	łącznik dojście–podjazd	1,05 m ²	2,0 %
U4	stanowisko pojemników	4,16 m ²	2,0 %
U5	fundament jednostki zewn....	1,12 m ²	—
U6	ścieżka gospodarcza	0,90 m ²	2,0 %
T1	deska kompozytowa na lega...	63,08 m ²	rz. 101,63
T2	płyty betonowe 60×60 na p...	2,99 m ²	rz. 101,63
T3	płyty betonowe 60×60, spa...	1,30 m ²	rz. 101,63

Kierunek spadku — strzałki na rysunku (od budynku, do odwodnień liniowych i niecek).

ODLEGŁOŚCI URZĄDZEŃ RETENCJI I PC

Element	Od	d [m]	min [m]	Zgodność
zbiornik	budynek	6,70	3,00	TAK
zbiornik	granica	11,60	2,00	TAK
zbiornik	drzewo	9,06	1,00	TAK
niecka	budynek	12,70	3,00	TAK
niecka	granica	8,60	2,00	TAK
niecka	drzewo	2,00	1,00	TAK
strefa R290	otwory, wpusty, studzienki	—	r = 1,00	TAK

Wymagania retencji — założenia projektowe (R8 pkt 3.5, W-144/W-145; nie przepis); zbiornik — odległość od środka (brak wymiarów w modelu); strefa R290 — W-156 (wytyczne producenta).

LEGENDA


	granica działki budowlanej, punkt graniczny, narożnik (PN-B-01027 poz. 2.7)		żywoplot projektowany (poz. 7.6)
	linia rozgraniczająca drogi publicznej (PN-B-01027 poz. 2.5)		drzewo liściaste projektowane (poz. 7.1)
	jezdnia drogi publicznej (wg mapy)		drzewo istniejące — zachowane (poz. 7.2)
	nieprzekraczalna linia zabudowy wg MPZP (PN-B-01027 poz. 2.2)		ogrodzenie projektowane (poz. 2.8; na granicy — odsunięte graficznie)
	budynek projektowany — obrys ścian parteru 1,0 m nad terenem (poz. 1.1)		brama przesuwana (poz. 2.9)
	obrys wyższych kondygnacji poza obrysem parteru (poz. 1.6 d)		furtka otwierana do wewnątrz działki (WT § 42)
	budynek płyt wspornikowych, okapów i daszku — przewieszenia (poz. 1.6 c)		zbiornik retencyjny szczelny (ZB)
	rzędna ±0,00 (posadzka parteru) w m n.p.m.; w kółku liczba kondygnacji nadziemnych		niecka chłonna — ogród deszczowy (przelew zbiornika)
	wejście główne do budynku (poz. 1.7)		odwodnienie liniowe
	wjazd do garażu		niecka trawiasta — grot w kierunku spływu
	zjazd z drogi publicznej — wg zezwolenia zarządcy drogi (DO UZUPEŁNIENIA)		rura spustowa: zewnętrzna / w szachcie (RS)
	nawierzchnia z kostki betonowej (poz. 7.10)		warstwa terenu istniejącego (PN-B-01027 poz. 5.2)
	nawierzchnia z płyt betonowych (poz. 7.11)		rzędna terenu istniejącego [m n.p.m.]
	płyty w trawie (ażur) — poza PBC		rzędna terenu projektowanego [m n.p.m.]
	taras naziemny — deska kompozytowa na legarach		spadek nawierzchni [%] — grot w kierunku spadku
	opaska żwirowa 16/32 na geowłókninie		kierunek spływu wód opadowych, spadek terenu [%]
	stanowisko postojowe 2,50 × 5,00 m (WT § 21)		wymiar / odległość w m z dokładnością 0,01 m
	osłona pojemników na odpady — segregacja (WT § 22)		punkt tyczenia (narożnik obrysu parteru) — wykaz współrzędnych
	rabata z krzewami		

OBJAŚNIENIA I UWAGI

- Wymiary i odległości w m (dokładność 0,01 m), rzędne w m n.p.m. (PL-EVRF2007-NH).
- Wymiary obrysu — lico zewnętrzne ścian parteru (1,0 m nad terenem); odległości od granic w miejscu najmniejszego oddalenia (WT § 9), z dokładnością 0,01 m (RPB § 15 ust. 3 w brzmieniu Dz.U. 2026 poz. 597, od 5.11.2026 — stosowane).
- Rzędne terenu istniejącego — z mapy (przykładowej); projektowanego — z modelu (działka.yaml: teren.punkty_projektowane); spadki nawierzchni wg modelu, kierunek wg terenu projektowanego; kierunki spływu na trawnikach — wg spadku terenu projektowanego (interpolacja).
- Wody opadowe z nawierzchni i dachów — na teren własny, do niecek i zbiornika (WT § 28 ust. 2); zakaz zmiany spływu w kierunku działek sąsiednich (WT § 29) i odprowadzania na drogę (u.d.p. art. 39).
- Punkty tyczenia — narożniki obrysu zewnętrznego ścian parteru; współrzędne w wykazie obok rysunku.
- Zjazd — geometria zastępcza [DO UZUPEŁNIENIA] (wg zezwolenia zarządcy drogi).
- Braki danych modelu oznaczono [DO UZUPEŁNIENIA]; wykaz: projekt/02_PZT/BRAKI_DANYCH.md.
- Rysunek wygenerowany automatycznie z modelu model/budynek.yaml (wersja 1.0, 2026-09-25) — generatory lamela.views.



REW.	OPIS ZMIANY	DATA
0	Wydanie — rysunek wygenerowany z modelu	2026-09-25
PRACOWNIA PROJEKTOWA	PRACOWNIA PROJEKTOWA — nazwa do uzupełnienia	STADIUM
adres pracowni do uzupełnienia		PB
BRANŻA	ZAGOSPODAROWANIE TERENU	
INWESTOR (do uzupełnienia)	OBIEKT / NAZWA ZAMIERZENIA BUDOWLANEGO	
	Budynek mieszkalny jednorodzinny wolnostojący „Dom LAMELA” z zagospodarowaniem działki	
ADRES / LOKALIZACJA (NR DZIAŁKI, OBRĘB, JEDN. EWIDENCYJNA)	ul. Lipowa (fikcyjna), dz. nr ewid. 123/4, obręb 0005 Przykładowo, gm. Przykładowo (fikcyjna)	KAT. OBIEKTU
		I
FUNKCJA	IMIĘ I NAZWISKO	SPECJALNOŚĆ, NR UPRAWNIENI
		DATA
Projektant		
Projektant (wsp.)		
Sprawdzający		
Opracował		
TYTUŁ RYSUNKU	PLAN SZCZEGÓŁOWY — WYMIARY I RZĘDNE	
SKALA	FORMAT	DATA WYDANIA
1:200	A2	2026-09-25
RODZAJ DOK.	NR RYSUNKU	ARKUSZ
plan szczegółowy	PZT-02	2/3
REW.	0	

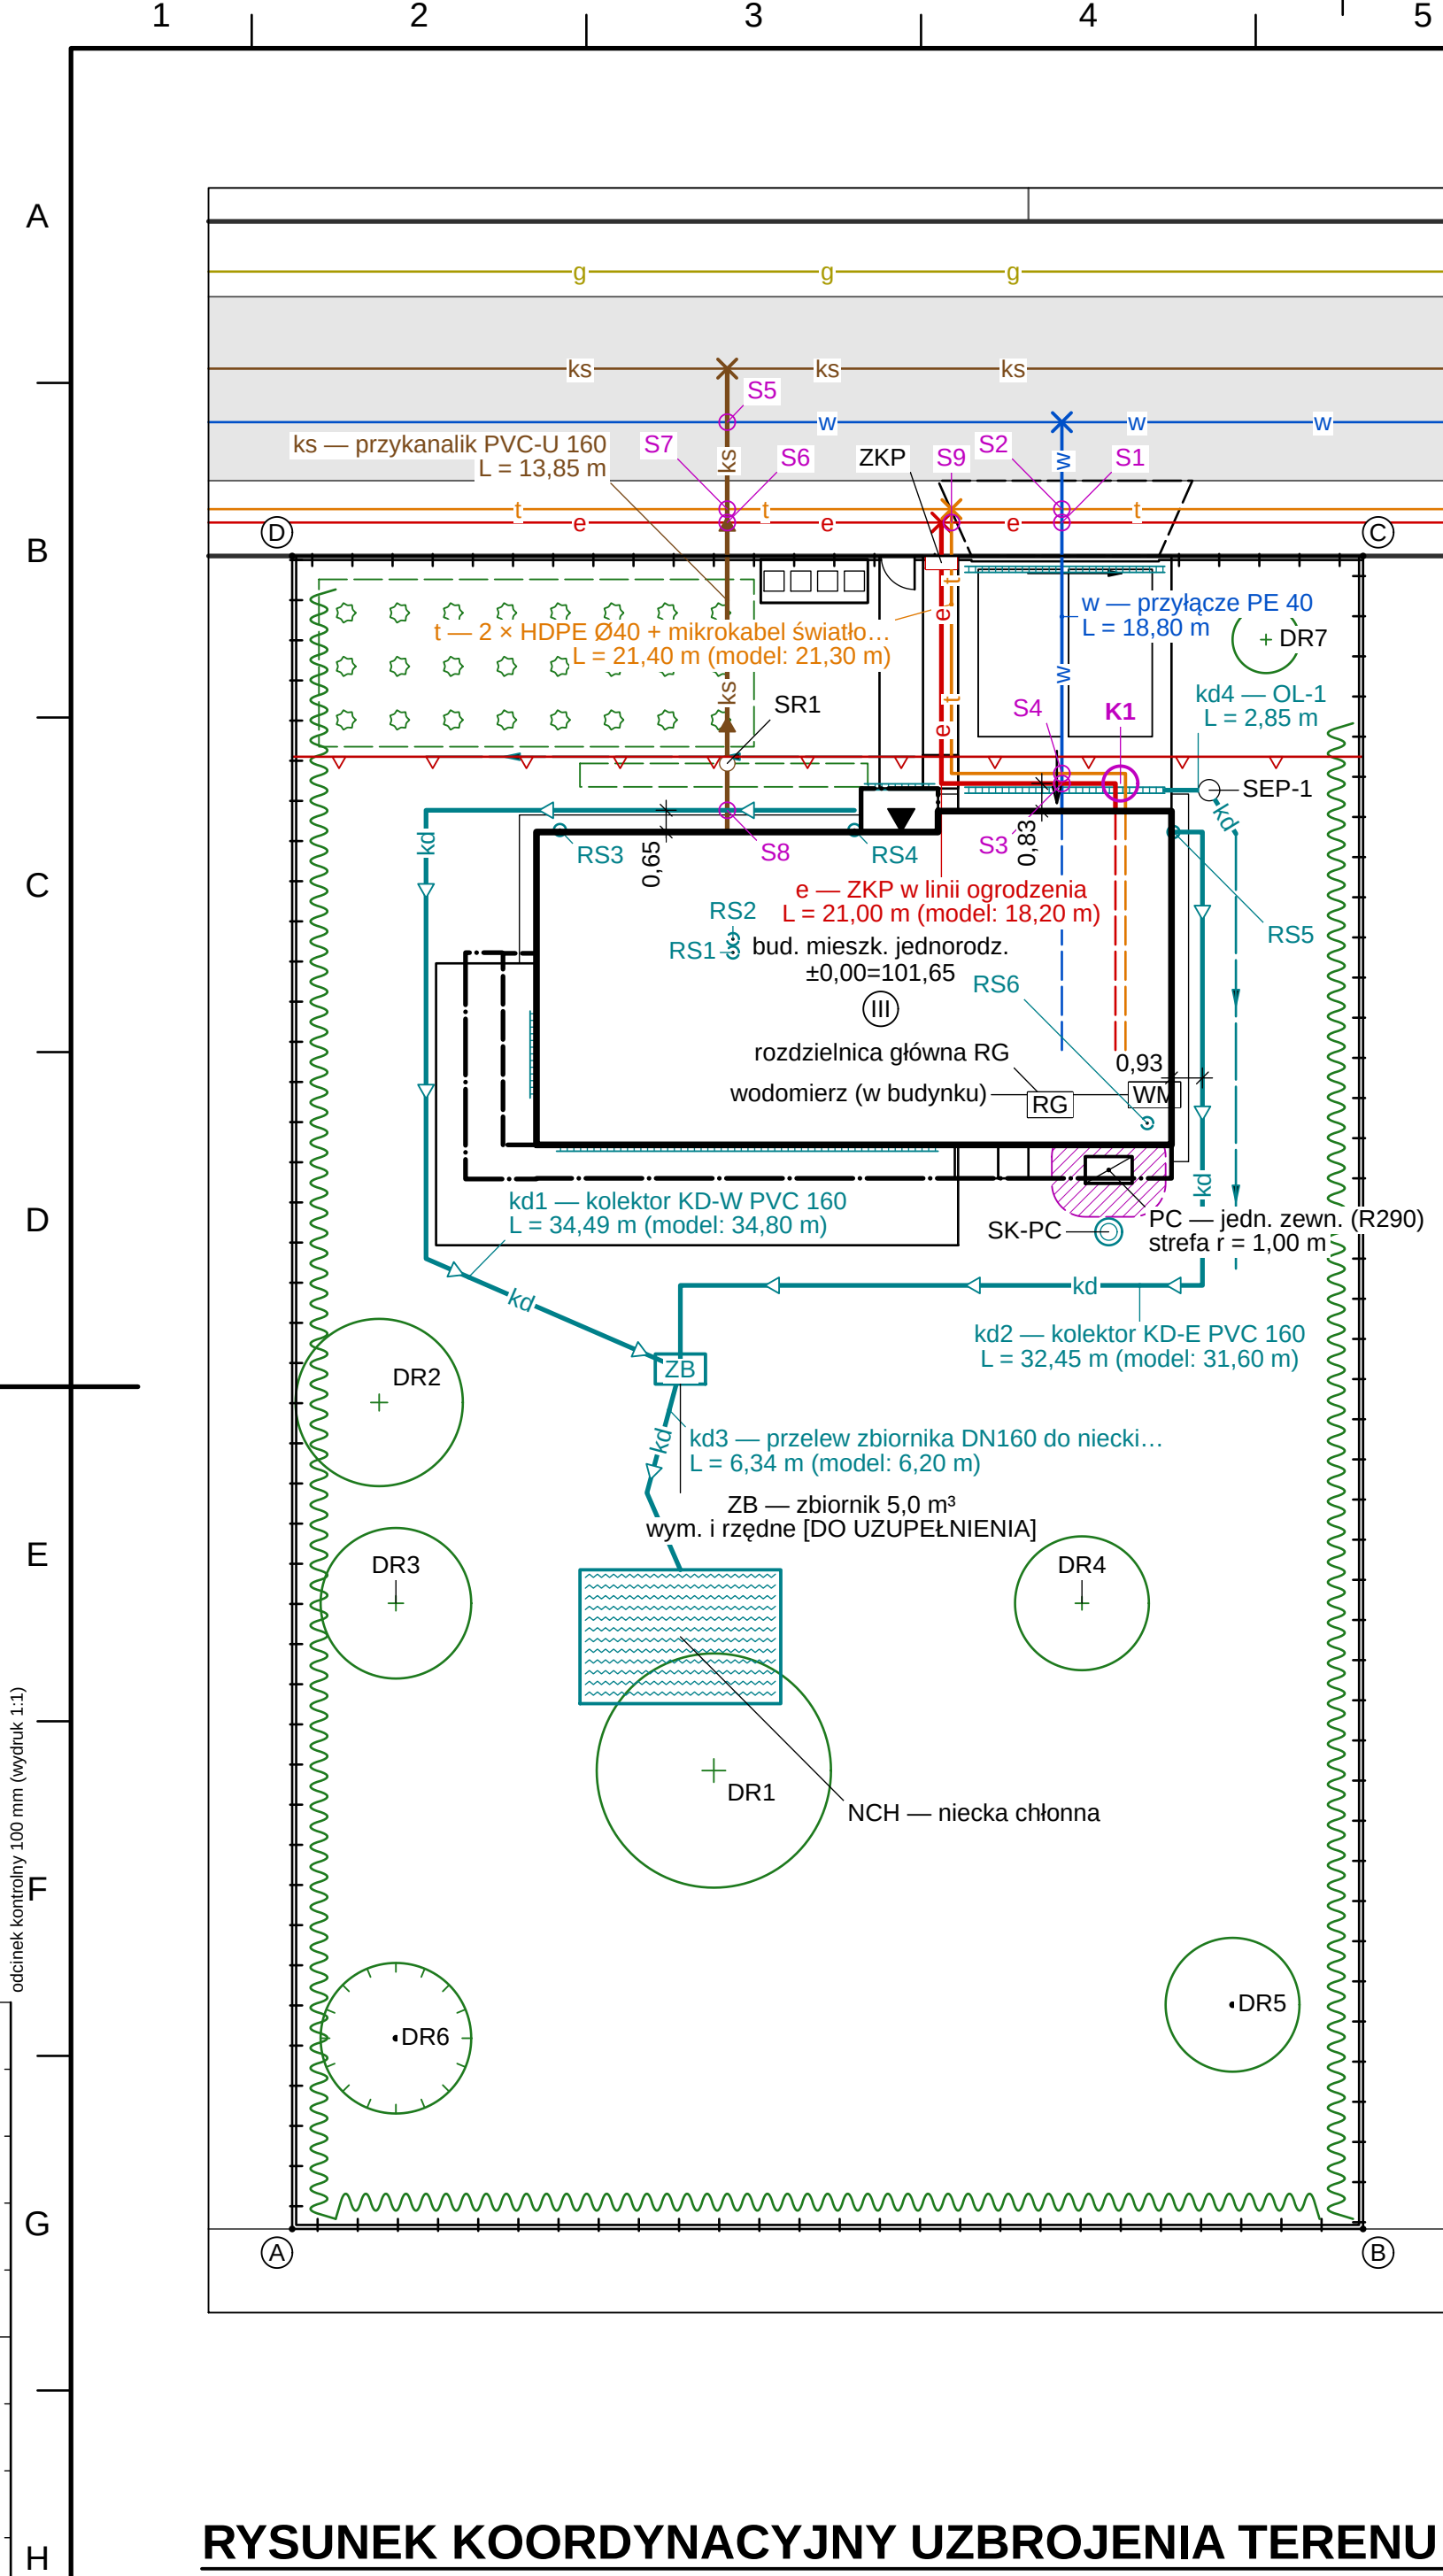

SIECI I PRZYŁĄCZA — PROJEKTOWANE I ISTNIEJĄCE

Ozn.	Sieć	Opis	L [m]	L model [m]
w	przyłłącze wodociągowe	przyłłącze PE 40	18,80	18,80
ks	kanalizacja sanitarna	przykanalik PVC-U 160	13,85	13,90
e	elektroenergetyczna nN (kabel)	ZKP w linii ogrodzenia	21,00	18,20
t	telekomunikacyjna (światłowód)	2 × HDPE Ø40 + mikrokabel świ...	21,40	21,30
kd1	kanalizacja deszczowa	kolektor KD-W PVC 160	34,49	34,80
kd2	kanalizacja deszczowa	kolektor KD-E PVC 160	32,45	31,60
kd3	kanalizacja deszczowa	przelew zbiornika DN160 do ni...	6,34	6,20
kd4	kanalizacja deszczowa	OL-1	2,85	2,90
w ist.	istniejąca (mapa)	wodociąg PE 110	—	—
ks ist.	istniejąca (mapa)	kanalizacja sanitarna PVC 200	—	—
e ist.	istniejąca (mapa)	kabel nN 0,4 kV	—	—
t ist.	istniejąca (mapa)	kanalizacja teletechniczna /...	—	—
g ist.	istniejąca (mapa)	gazociąg PE 63 (nie wykorzyst...	—	—

L — długość trasy w rzucie (z częścią pod budynkiem, linia kreskowa); średnice, spadki i rzędne dna przewodów [DO UZUPEŁNIENIA] (RPB § 15 ust. 2 pkt 11 — brak w modelu).

OBIEKTY UZBROJENIA I ODWODNIENIA

Ozn.	Opis
ZKP	złącze kablowo-pomiarowe we wnęce ogrodzenia
SR1	studzienka rewizyjna kanalizacji Ø425
PC-JZ	jednostka zewn. PC monoblok R290 w osłonie lamelowe...
SEP-1	osadnik z separatorem substancji ropopochodnych
SK-PC	studnia chłonna skroplin PC
HYDR	najbliższy hydrant zewnętrzny DN80
RS1	rura spustowa DN100 (w szachcie) z dachu D1
RS2	rura spustowa DN100 (w szachcie) z dachu D1
RS3	rura spustowa DN100 (zewn.) z dachu D2
RS4	rura spustowa DN100 (zewn.) z dachu D3
RS5	rura spustowa DN100 (zewn.) z dachu D4
RS6	rura spustowa DN100 (w szachcie) z dachu D4

KOORDYNACJA — ODLEGŁOŚCI POZIOME MIĘDZY SIECIAMI

Para sieci	d [m]	min [m]	Źródło wymagania	Zgodność
w – ks ist.	3,15	1,50	praktyka proj. (COBRTI INSTAL z. 3)*	TAK
w – kd2	3,40	1,50	praktyka proj. (COBRTI INSTAL z. 3)*	TAK
w – kd4	3,08	1,50	praktyka proj. (COBRTI INSTAL z. 3)*	TAK
e – t ist.	1,02	0,50	N SEP-E-004:2014*	TAK
e – t	0,30	0,50	N SEP-E-004:2014*	warunk.
e – kd1	2,72	0,50	N SEP-E-004:2014*	TAK
e – kd2	1,80	0,50	N SEP-E-004:2014*	TAK
e – kd4	1,48	0,50	N SEP-E-004:2014*	TAK
t – kd2	1,50	0,50	praktyka proj.*	TAK
t – kd4	1,18	0,50	praktyka proj.*	TAK
e – budynek	0,83	—	informacyjnie (lico ściany)	—
kd1 – budynek	0,65	—	informacyjnie (lico ściany)	—
kd2 – budynek	0,93	—	informacyjnie (lico ściany)	—

* wartości minimalne wg zasad wiedzy technicznej (N SEP-E-004, praktyka projektowa) — NIE są przepisem: WT § 26–28 określają tylko wymagania ogólne uzbrojenia działki; do potwierdzenia w warunkach przyłączenia gestorów [SPRAWDŹ]. „warunk.” — dopuszczalne przy rurach osłonowych.

SKRZYŻOWANIA SIECI

Nr	Sieci	x [m]	y [m]
S1	w × e ist.	23,00	51,00
S2	w × t ist.	23,00	51,40
S3	w × e	23,00	43,20
S4	w × t	23,00	43,50
S5	ks × w ist.	13,00	54,00
S6	ks × e ist.	13,00	51,00
S7	ks × t ist.	13,00	51,40
S8	ks × kd1	13,00	42,40
S9	t × e ist.	19,70	51,00

Odstępny pionowe na skrzyżowaniach — wg warunków gestorów sieci [DO UZUPEŁNIENIA] (brak rzędnych przewodów w modelu); kable w rurach osłonowych w obrębie skrzyżowań.

KOLIZJE I ZBLIŻENIA

Nr	Rodzaj	Opis	Ocena
K1	zbliżenie sieci	e–t: 0,30 m < 0,50 m	warunk.


K1: dopuszczalne przy ułożeniu w rurach osłonowych — uzgodnić z gestorami

LEGENDA

	granica działki budowlanej, punkt graniczny, narożnik (PN-B-01027 poz. 2.7)
	linia rozgraniczająca drogi publicznej (PN-B-01027 poz. 2.5)
	jezdnia drogi publicznej (wg mapy)
	nieprzekraczalna linia zabudowy wg MPZP (PN-B-01027 poz. 2.2)
	budynek projektowany — obrys ścian parteru 1,0 m nad terenem (poz. 1.1)
	obrys wyższych kondygnacji poza obrysem parteru (poz. 1.6 d)
	obrys płyt wspornikowych, okapów i daszku — przewieszenia (poz. 1.6 c)
	rzędna ±0,00 (posadzka parteru) w m n.p.m.; w kółku liczba kondygnacji nadziemnych
	wejście główne do budynku (poz. 1.7)
	wjazd do garażu
	zjazd z drogi publicznej — wg zezwolenia zarządcy drogi (DO UZUPEŁNIENIA)
	nawierzchnia z kostki betonowej (poz. 7.10)
	nawierzchnia z płyt betonowych (poz. 7.11)
	płyty w trawie (ażur) — poza PBC
	taras naziemny — deska kompozytowa na legarach
	opaska żwirowa 16/32 na geowłókninie
	stanowisko postojowe 2,50 × 5,00 m (WT § 21)
	osłona pojemników na odpady — segregacja (WT § 22)
	rabata z krzewami
	żywopłot projektowany (poz. 7.6)
	drzewo liściaste projektowane (poz. 7.1)
	drzewo istniejące — zachowane (poz. 7.2)
	ogrodzenie projektowane (poz. 2.8; na granicy — odsunięte graficznie)
	brama przesuwna (poz. 2.9)
	furta otwierana do wewnątrz działki (WT § 42)
	jednostka zewn. pompy ciepła (fundament) i strefa czynnika R290
	zbiornik retencyjny szczelny (ZB)
	niecka chłonna — ogród deszczowy (przelew zbiornika)
	odwodnienie liniowe
	niecka trawiasta — grot w kierunku spływu
	rura spustowa: zewnętrzna / w szachcie (RS)
	miejsce włączenia przyłącza do sieci (PN-B-01027 poz. 6)
	złącze kablowo-pomiarowe ZKP (w linii ogrodzenia)
	studzienka rewizyjna kanalizacji
	studnia chłonna skroplin pompy ciepła
	skrzyżowanie sieci — zachować odstęp pionowy (tabela)
	zbliżenie / kolizja sieci (nr w tabeli koordynacji)
	w — sieć wodociągowa istniejąca (mapa)
	w — przyłącze wodociągowe projektowane
	ks — sieć kanalizacji sanitarnej istniejąca (mapa)
	ks — przykanalik sanitarny projektowany
	kd — kanalizacja deszczowa projektowana (kolektory, przelewy)
	e — linia kablowa nN istniejąca (mapa)
	e — kabel nN projektowany (ZKP → RG)
	t — sieć telekomunikacyjna istniejąca (mapa)
	t — przyłącze telekomunikacyjne projektowane
	g — sieć gazowa istniejąca (mapa)

OBJAŚNIENIA I UWAGI

- Wymiary i odległości w m (dokładność 0,01 m), rzędne w m n.p.m. (PL-EVRF2007-NH).
- Oznaczenia sieci — kolory i litery wg mapy zasadniczej (zał. 4 rozp. w sprawie BDOT500 i mapy zasadniczej, Dz.U. 2021 poz. 1385): w — wodociąg, ks — kanalizacja sanitarna, kd — kanalizacja deszczowa, e — elektroenergetyczna, t — telekomunikacyjna, g — gazowa; istniejące — linia cienka (wg mapy), projektowane — gruba; w budynku/pod płytą — kreskowa; „x” — włączenie do sieci.
- Przyłącza w granicach działki nie podlegają narzędziu koordynacyjnej ZUD (PGiK art. 28b); roboty w pasie drogowym 1KDD — za zezwoleniem zarządcy drogi (u.d.p. art. 40).
- Skrzyżowań: 9; zbliżeń poniżej wartości minimalnych: 1 (tabela „Kolizje i zbliżenia”).
- Wody opadowe: rury spustowe RS → kolektory kd → zbiornik ZB → przelew do niecki chłonnej NCH; odwodnienia liniowe OL → kolektory kd (WT § 28 ust. 2).
- Drenaż opaskowy DR-0: NIE PROJEKTUJE SIĘ — piaski przepuszczalne, ZWG = 3,8 m p.p.t., posadowienie = 0,5 m p.p.t. (W-285); ochrona płyty: XPS + membrana SBS, opaska żwirowa i spadki terenu
- Braki danych modelu (9 poz.) — [DO UZUPEŁNIENIA]; wykaz: projekt/02_PZT/BRAKI_DANYCH.md.
- Rysunek wygenerowany automatycznie z modelu model/budynek.yaml (wersja 1.0, 2026-09-25) — generatory lamela.views.

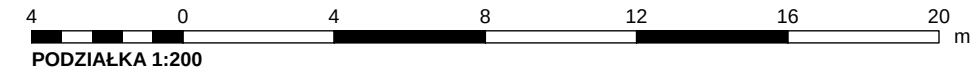

REW.		OPIS ZMIANY		DATA			
0		Wydanie — rysunek wygenerowany z modelu		2026-09-25			
PRACOWNIA PROJEKTOWA PRACOWNIA PROJEKTOWA — nazwa do uzupełnienia adres pracowni do uzupełnienia			STADIUM PB	BRANŻA ZAGOSPODAROWANIE TERENU			
INWESTOR (do uzupełnienia)							
OBIEKT / NAZWA ZAMIERZENIA BUDOWLANEGO Budynek mieszkalny jednorodzinny wolnostojący „Dom LAMELA” z zagospodarowaniem działki							
ADRES / LOKALIZACJA (NR DZIAŁKI, OBRĘB, JEDN. EWIDENCYJNA) ul. Lipowa (fikcyjna), dz. nr ewid. 123/4, obręb 0005 Przykładowo, gm. Przykładowo (fikcyjna)				KAT. OBIEKTU I			
FUNKCJA		IMIĘ I NAZWISKO		SPECJALNOŚĆ, NR UPRAWNIENI	DATA	PODPIS	
Projektant							
Projektant (wsp.)							
Sprawdzający							
Opracował							
TYTUŁ RYSUNKU							
RYSUNEK KOORDYNACYJNY UZBROJENIA TERENU							
SKALA 1:200		FORMAT A2	DATA WYDANIA 2026-09-25	RODZAJ DOK. rysunek koordynacyjny	NR RYSUNKU PZT-03	ARKUSZ 3/3	REW. 0