



A
B
C
D
E
F
G
H

1 2 3 4 5 6 7 8 9 10 11 12 13

OBJAŚNIENIA I UWAGI (cd.)

6. Rozmieszczenie modułów wyznaczono algorytmicznie w polu użytkowym dachu (odsunięcie $\geq 1,0$ m od krawędzi, odstępy od otworów, wpustów, czepni, wyrzutni i wywiewek), konstrukcja balastowa niskoprofilowa — górna krawędź s wierzchu attyki; obciążenia i balast wg PN-EN 1991-1-4 (projekt konstrukcji).
7. Konstrukcję wsporczą PV połączyć z GSU przewodem wyrównawczym ≥ 6 mm² Cu (712.444.5.5.101); odstęp separacyjny od ewentualnych zwodów wg PN-EN IEC 62305-3.
8. Rysunek wygenerowany automatycznie z modelu model/budynek.yaml (wersja 1.0, 2026-09-25) — generatory lamela.views.

1 0 1 2 3 4 5 m
PODZIAŁKA 1:50

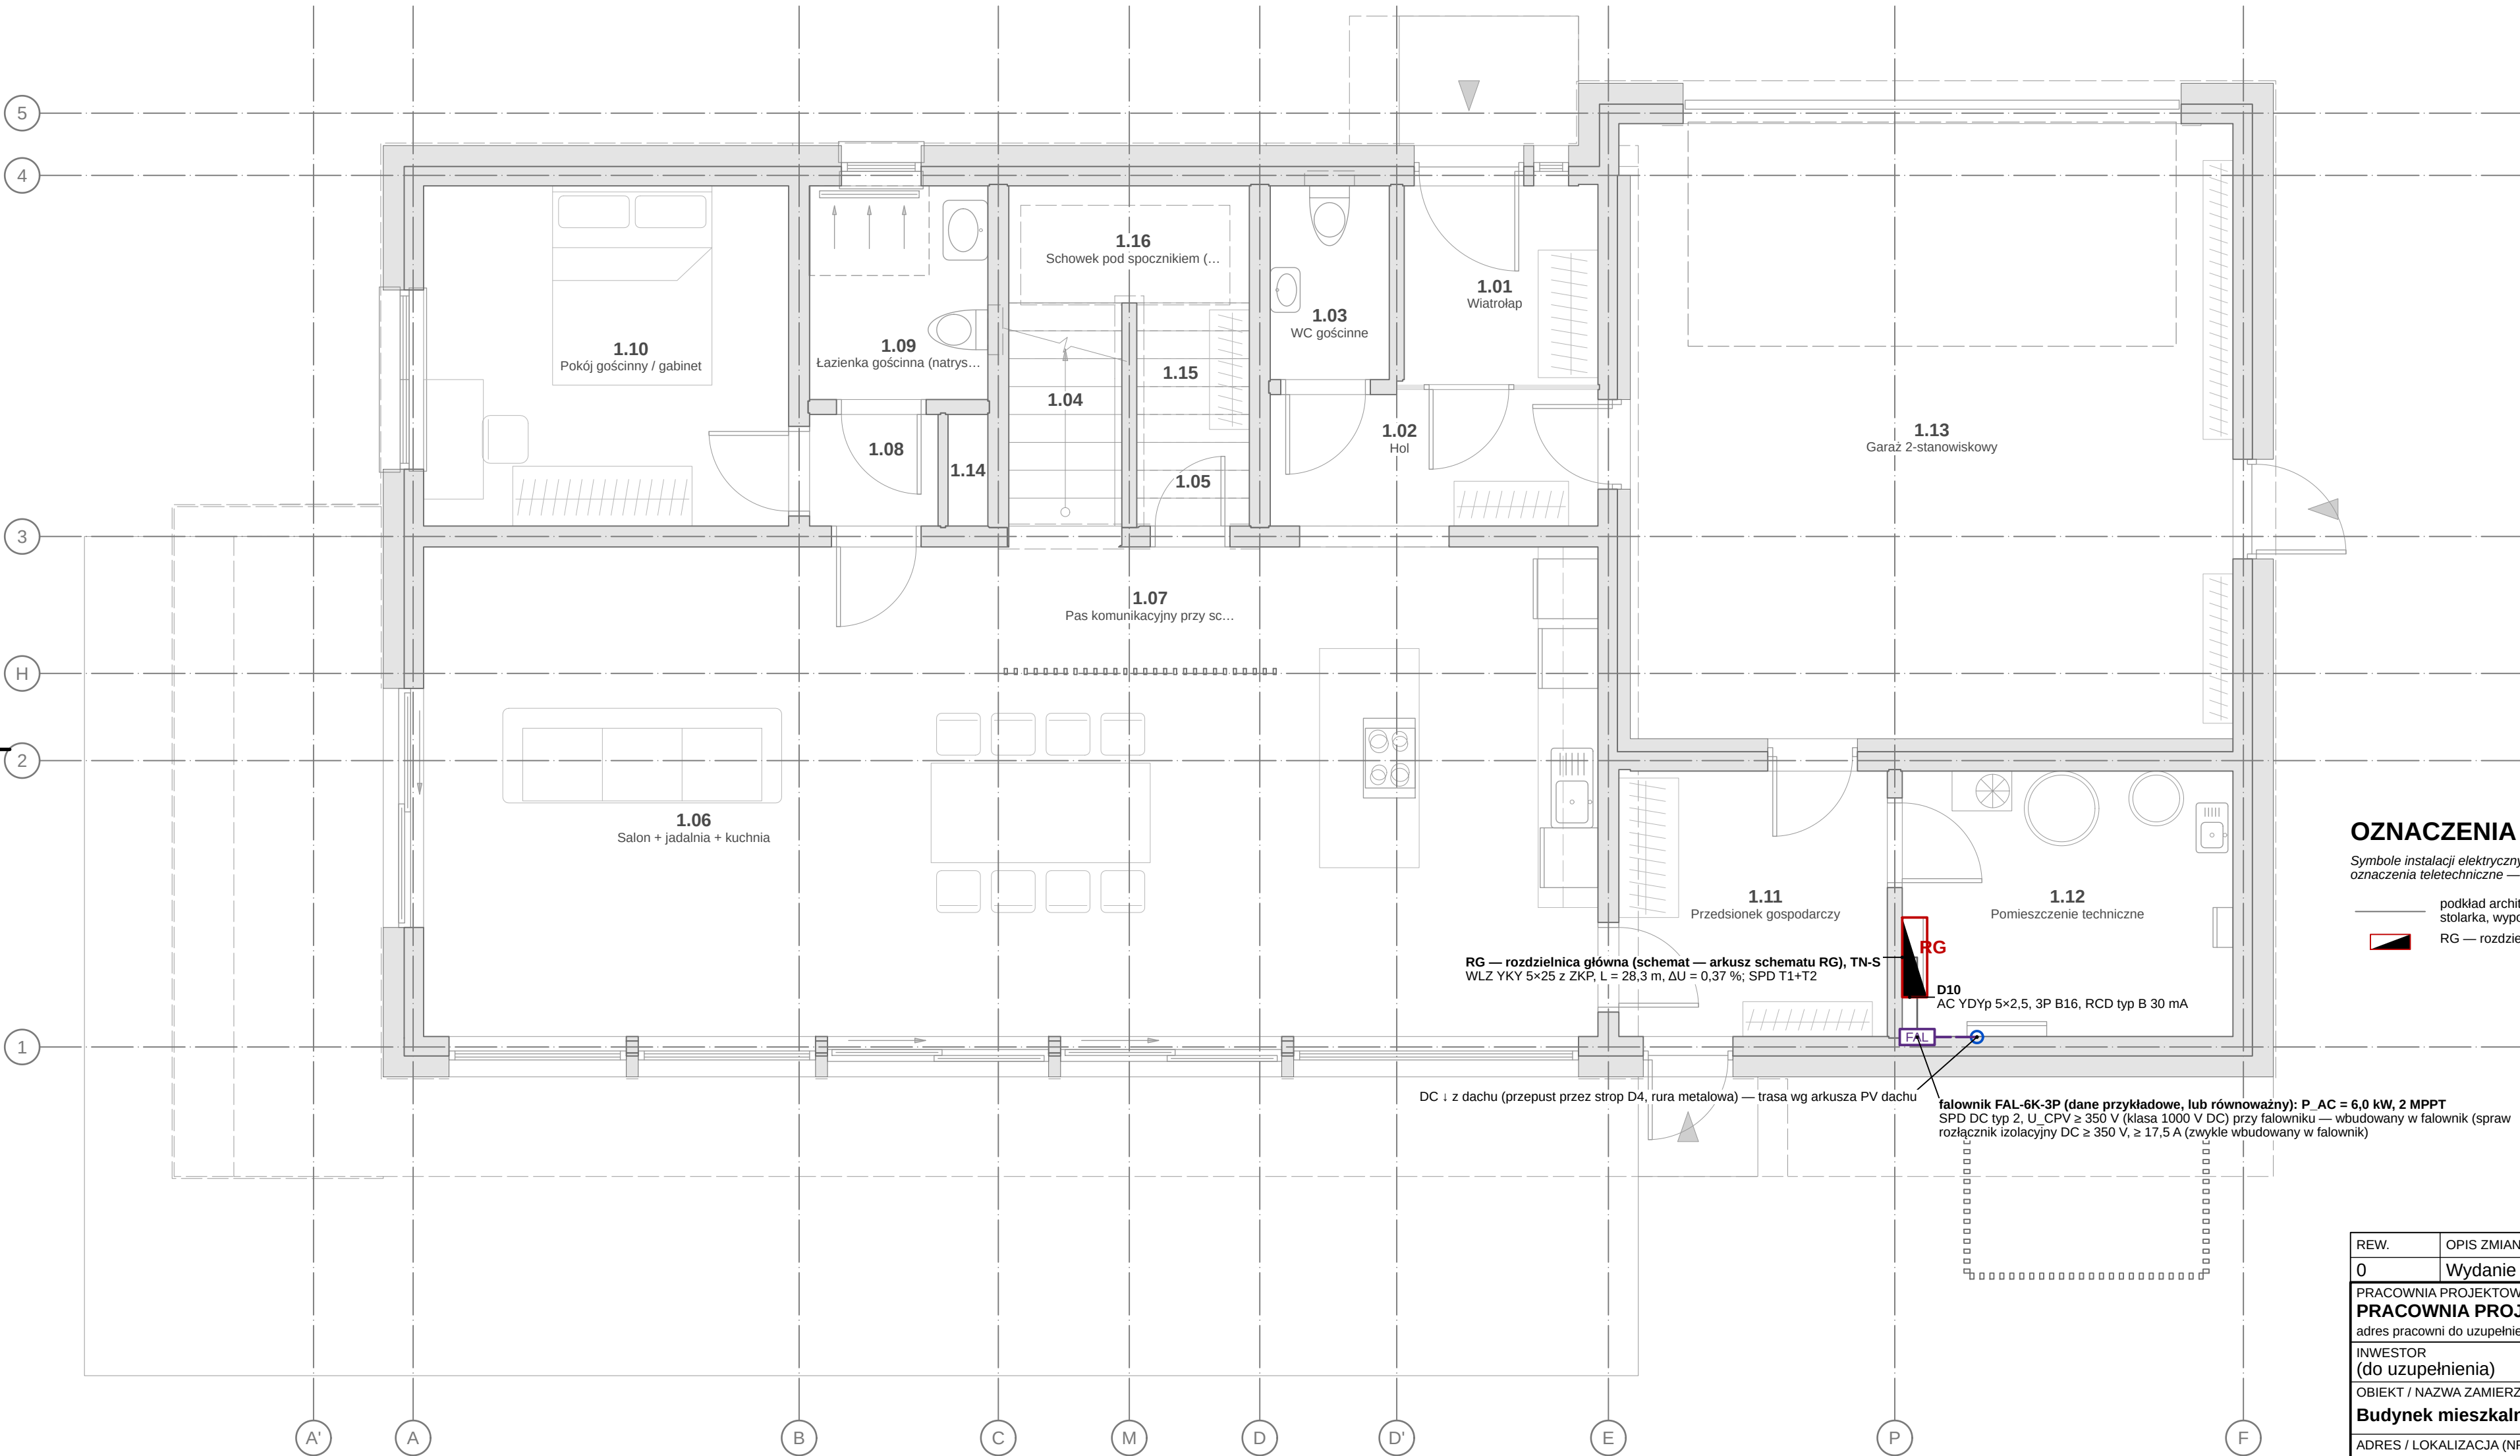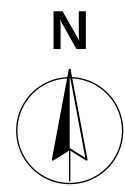

OZNACZENIA — LEGENDA SYMBOLI

Symboly instalacji elektrycznych wg IEC 60617 (baza IEC; PN-EN 60617 — wycofana, stosowana jako praktyka branżowa) i PN-EN ISO 14617; oznaczenia teletechniczne — praktyka branżowa. Obowiązuje legenda na arkuszu.

- podkład architektoniczny (rzut AR — ściany przecięte, stolarka, wyposażenie) — linie cienkie szare
- RG — rozdzielnica główna (PN-EN IEC 61439-3)
- FAL — falownik PV (SPD DC typ 2, rozłącznik DC)
- przepust / pion przewodów DC

INSTALACJA FOTOWOLTAICZNA — RZUT PARTERU (FALOWNIK, SPD) 1:50

OBJAŚNIENIA I UWAGI

1. Średnice przewodów w mm (d_zxs — rury wielowarstwowe, Ø/DN — kanalizacja, kanały wentylacyjne), przekroje żył w mm², odległości i rzędne w m; $\pm 0,000 \approx 101,650$ m n.p.m. (PL-EVRP2007-NH).
2. Rysunki instalacji na podkładzie rzutów architektury (PB-AR); podkład — linie cienkie szare (warstwy I-PODKŁAD*).
3. Przy RG, przycisku PWP i falowniku — tabliczki ostrzegawcze: „Instalacja PV — strona DC pod napięciem po wyłączeniu PWP” (WT § 183, PN-HD 60364-7-712).
4. Instalacja fotowoltaiczna wg PN-HD 60364-7-712, PN-EN 62446-1 (dokumentacja, badania), WT § 184 i art. 29 ust. 4 pkt 3 lit. c PB (moc $\leq 6,5$ kWp): 15×430 Wp = 6,45 kWp, układ EW10, E = 5610 kWh/a (PVGIS; obliczenia lamela.obliczenia.elektryka.py).
5. Łańcuchy: 2 x do 8 modułów; U_oc,max = 350 V, U_mpp 196–298 V, I_sc = 14,0 A (obliczenia) — sprawdzić z DTR wybranych modułów i falownika (dane przykładowe, lub równoważne).

REW.	OPIS ZMIANY			DATA		
0	Wydanie — rysunek wygenerowany z modelu			2026-09-25		
PRACOWNIA PROJEKTOWA PRACOWNIA PROJEKTOWA — nazwa do uzupełnienia adres pracowni do uzupełnienia				STADIUM PT	BRANŻA INSTALACJE ELEKTRYCZNE (IE)	
INWESTOR (do uzupełnienia)						
OBIEKT / NAZWA ZAMIERZENIA BUDOWLANEGO Budynek mieszkalny jednorodzinny wolnostojący „Dom LAMELA”						
ADRES / LOKALIZACJA (NR DZIAŁKI, OBREB, JEDN. EWIDENCYJNA) ul. Lipowa (fikcyjna), dz. nr ewid. 123/4, obręb 0005 Przykładowo, gm. Przykładowo (fikcyjna)					KAT. OBIEKTU I	
FUNKCJA	IMIĘ I NAZWISKO		SPECJALNOŚĆ, NR UPRAWNIENI		DATA	PODPIS
Projektant	[DO UZUPEŁNIENIA]		[DO UZUPEŁNIENIA]			
Projektant (wsp.)	[DO UZUPEŁNIENIA]		[DO UZUPEŁNIENIA]			
Sprawdzający	nie dotyczy (art. 20 ust. 3 pkt 2 PB)		—			
Opracował	[DO UZUPEŁNIENIA]		[DO UZUPEŁNIENIA]			
TYTUŁ RYSUNKU INSTALACJA FOTOWOLTAICZNA — RZUT PARTERU (FALOWNIK, SPD)						
SKALA 1:50	FORMAT 690x420	DATA WYDANIA 2026-09-25	RODZAJ DOK. rzut instalacji	NR RYSUNKU PT-IE-11	ARKUSZ 11/14	REW. 0

1 2 3 4 5 6 7 8 9 10 11 12 13 13^{st.} 690x420