






ELEWACJA POŁUDNIOWA (OGRODOWA) 1:50

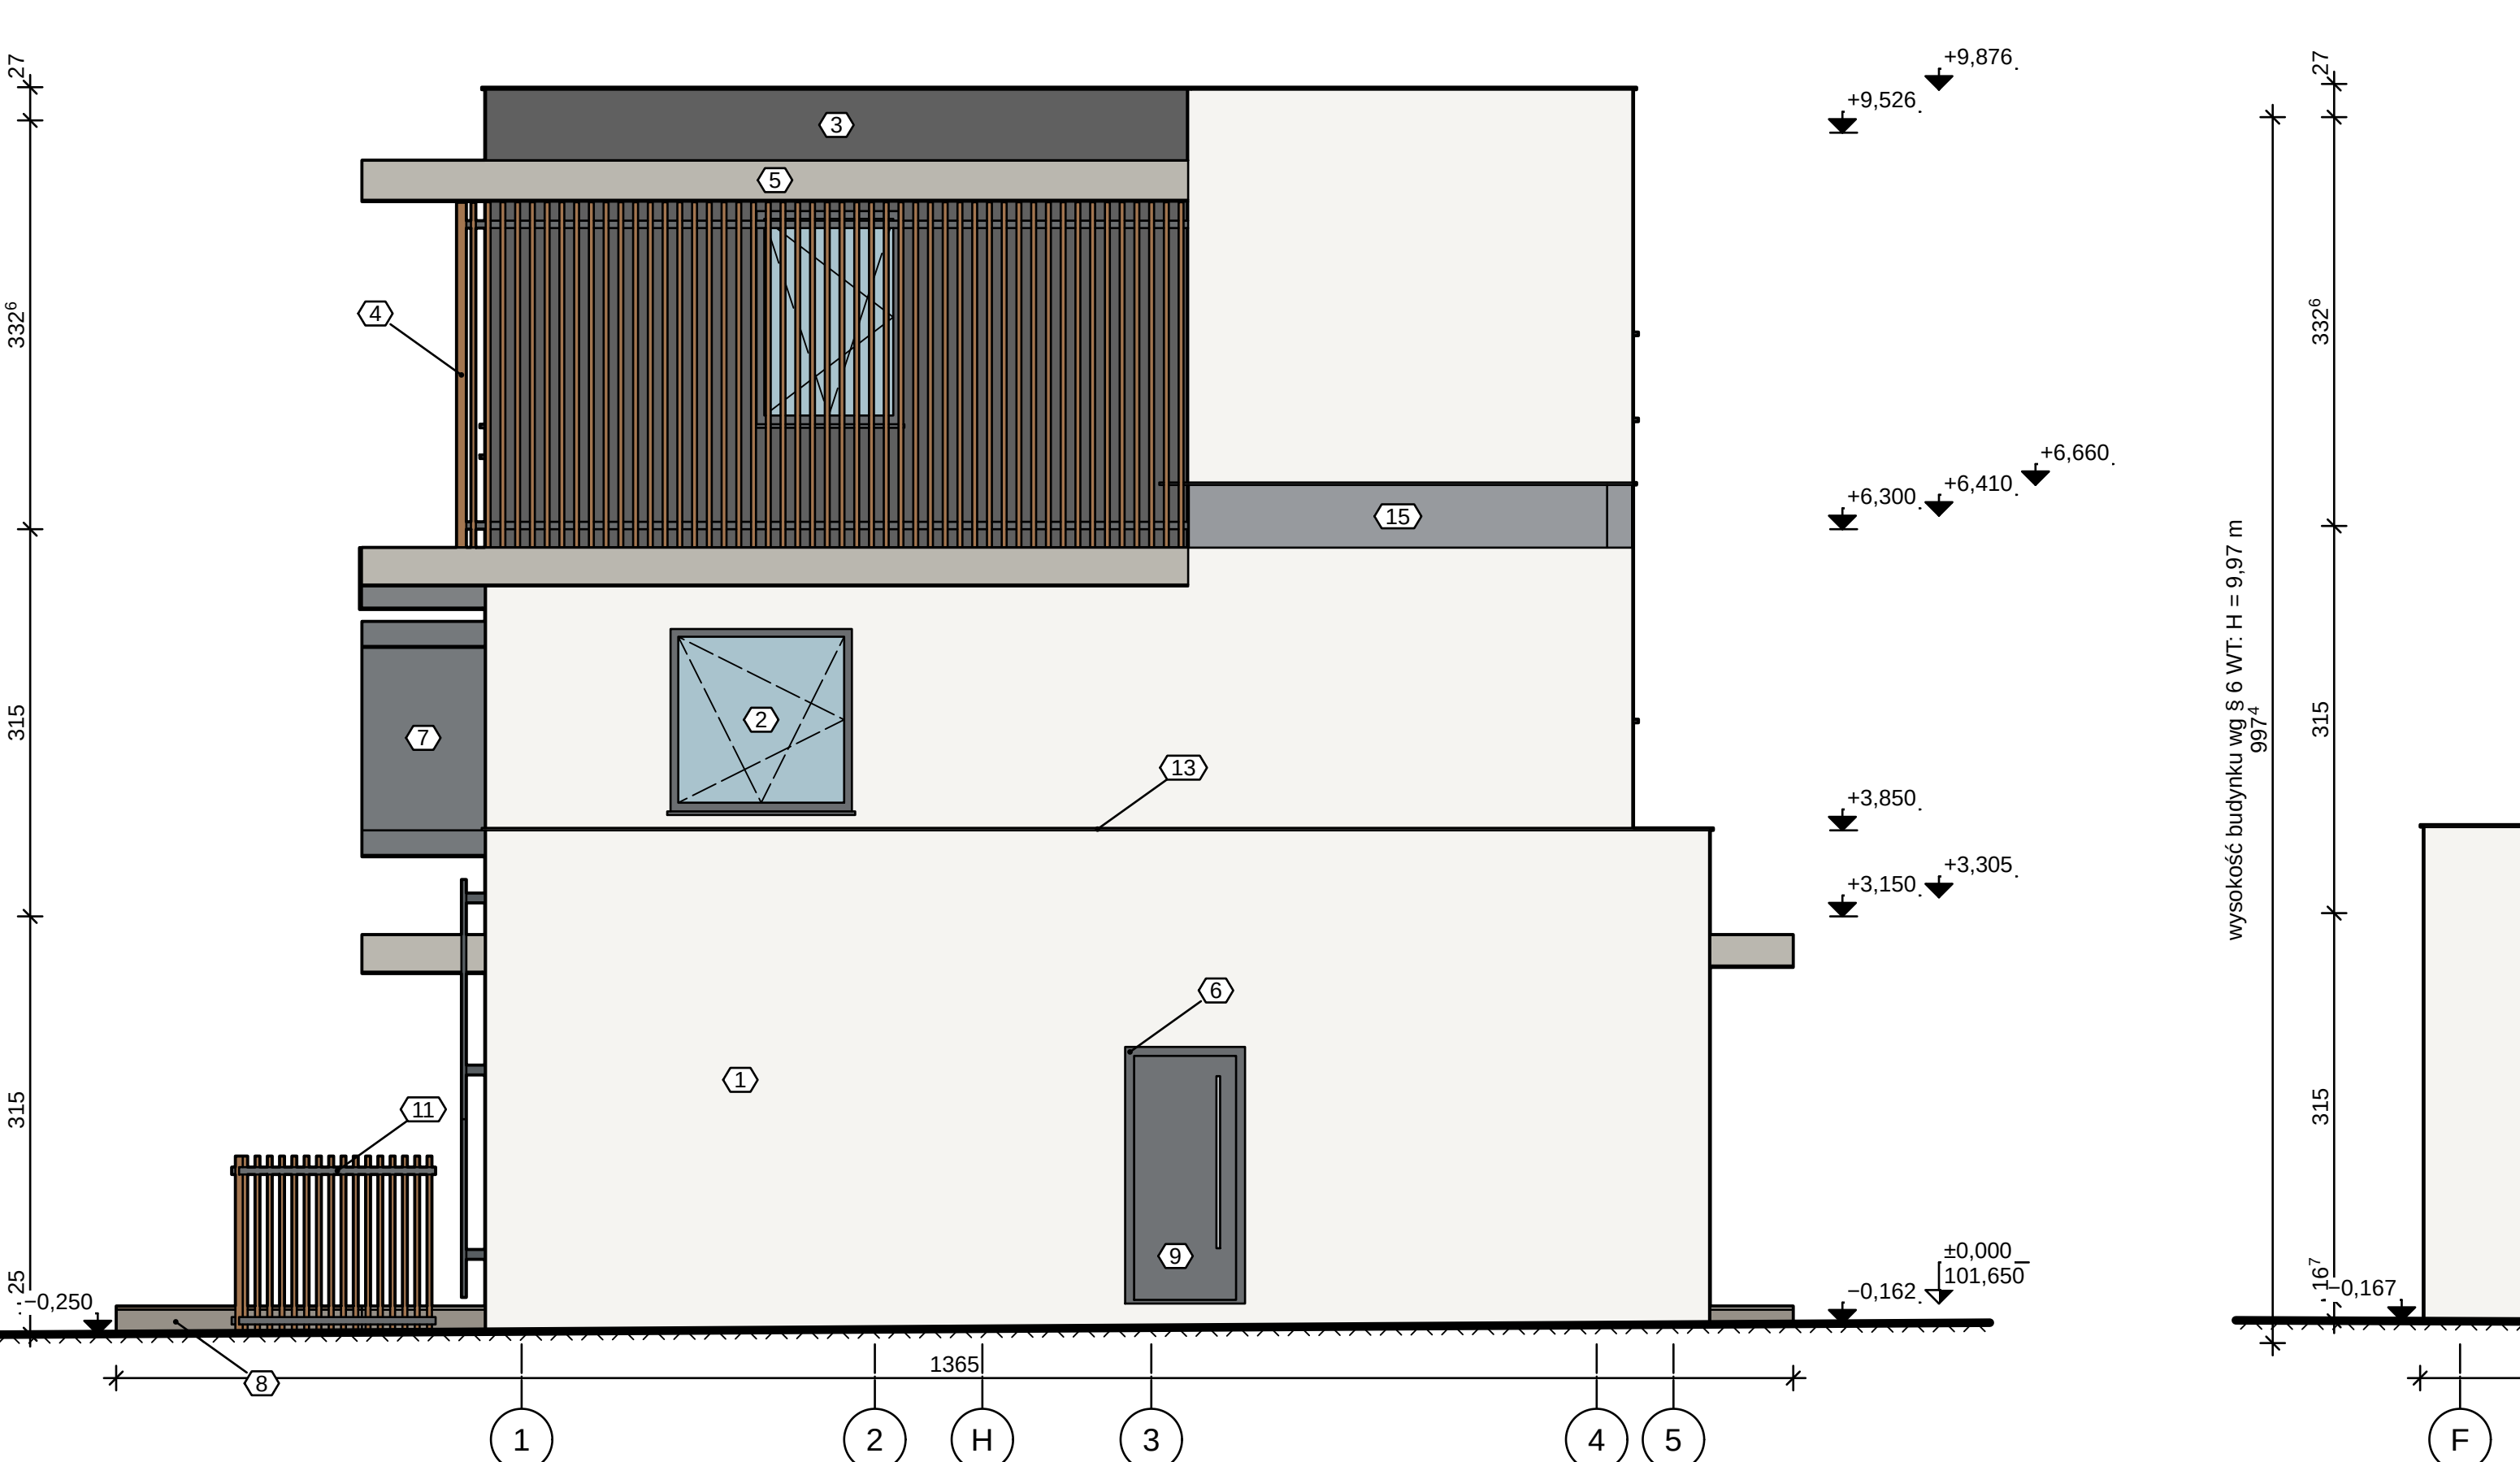

ELEWACJA WSCHODNIA 1:50

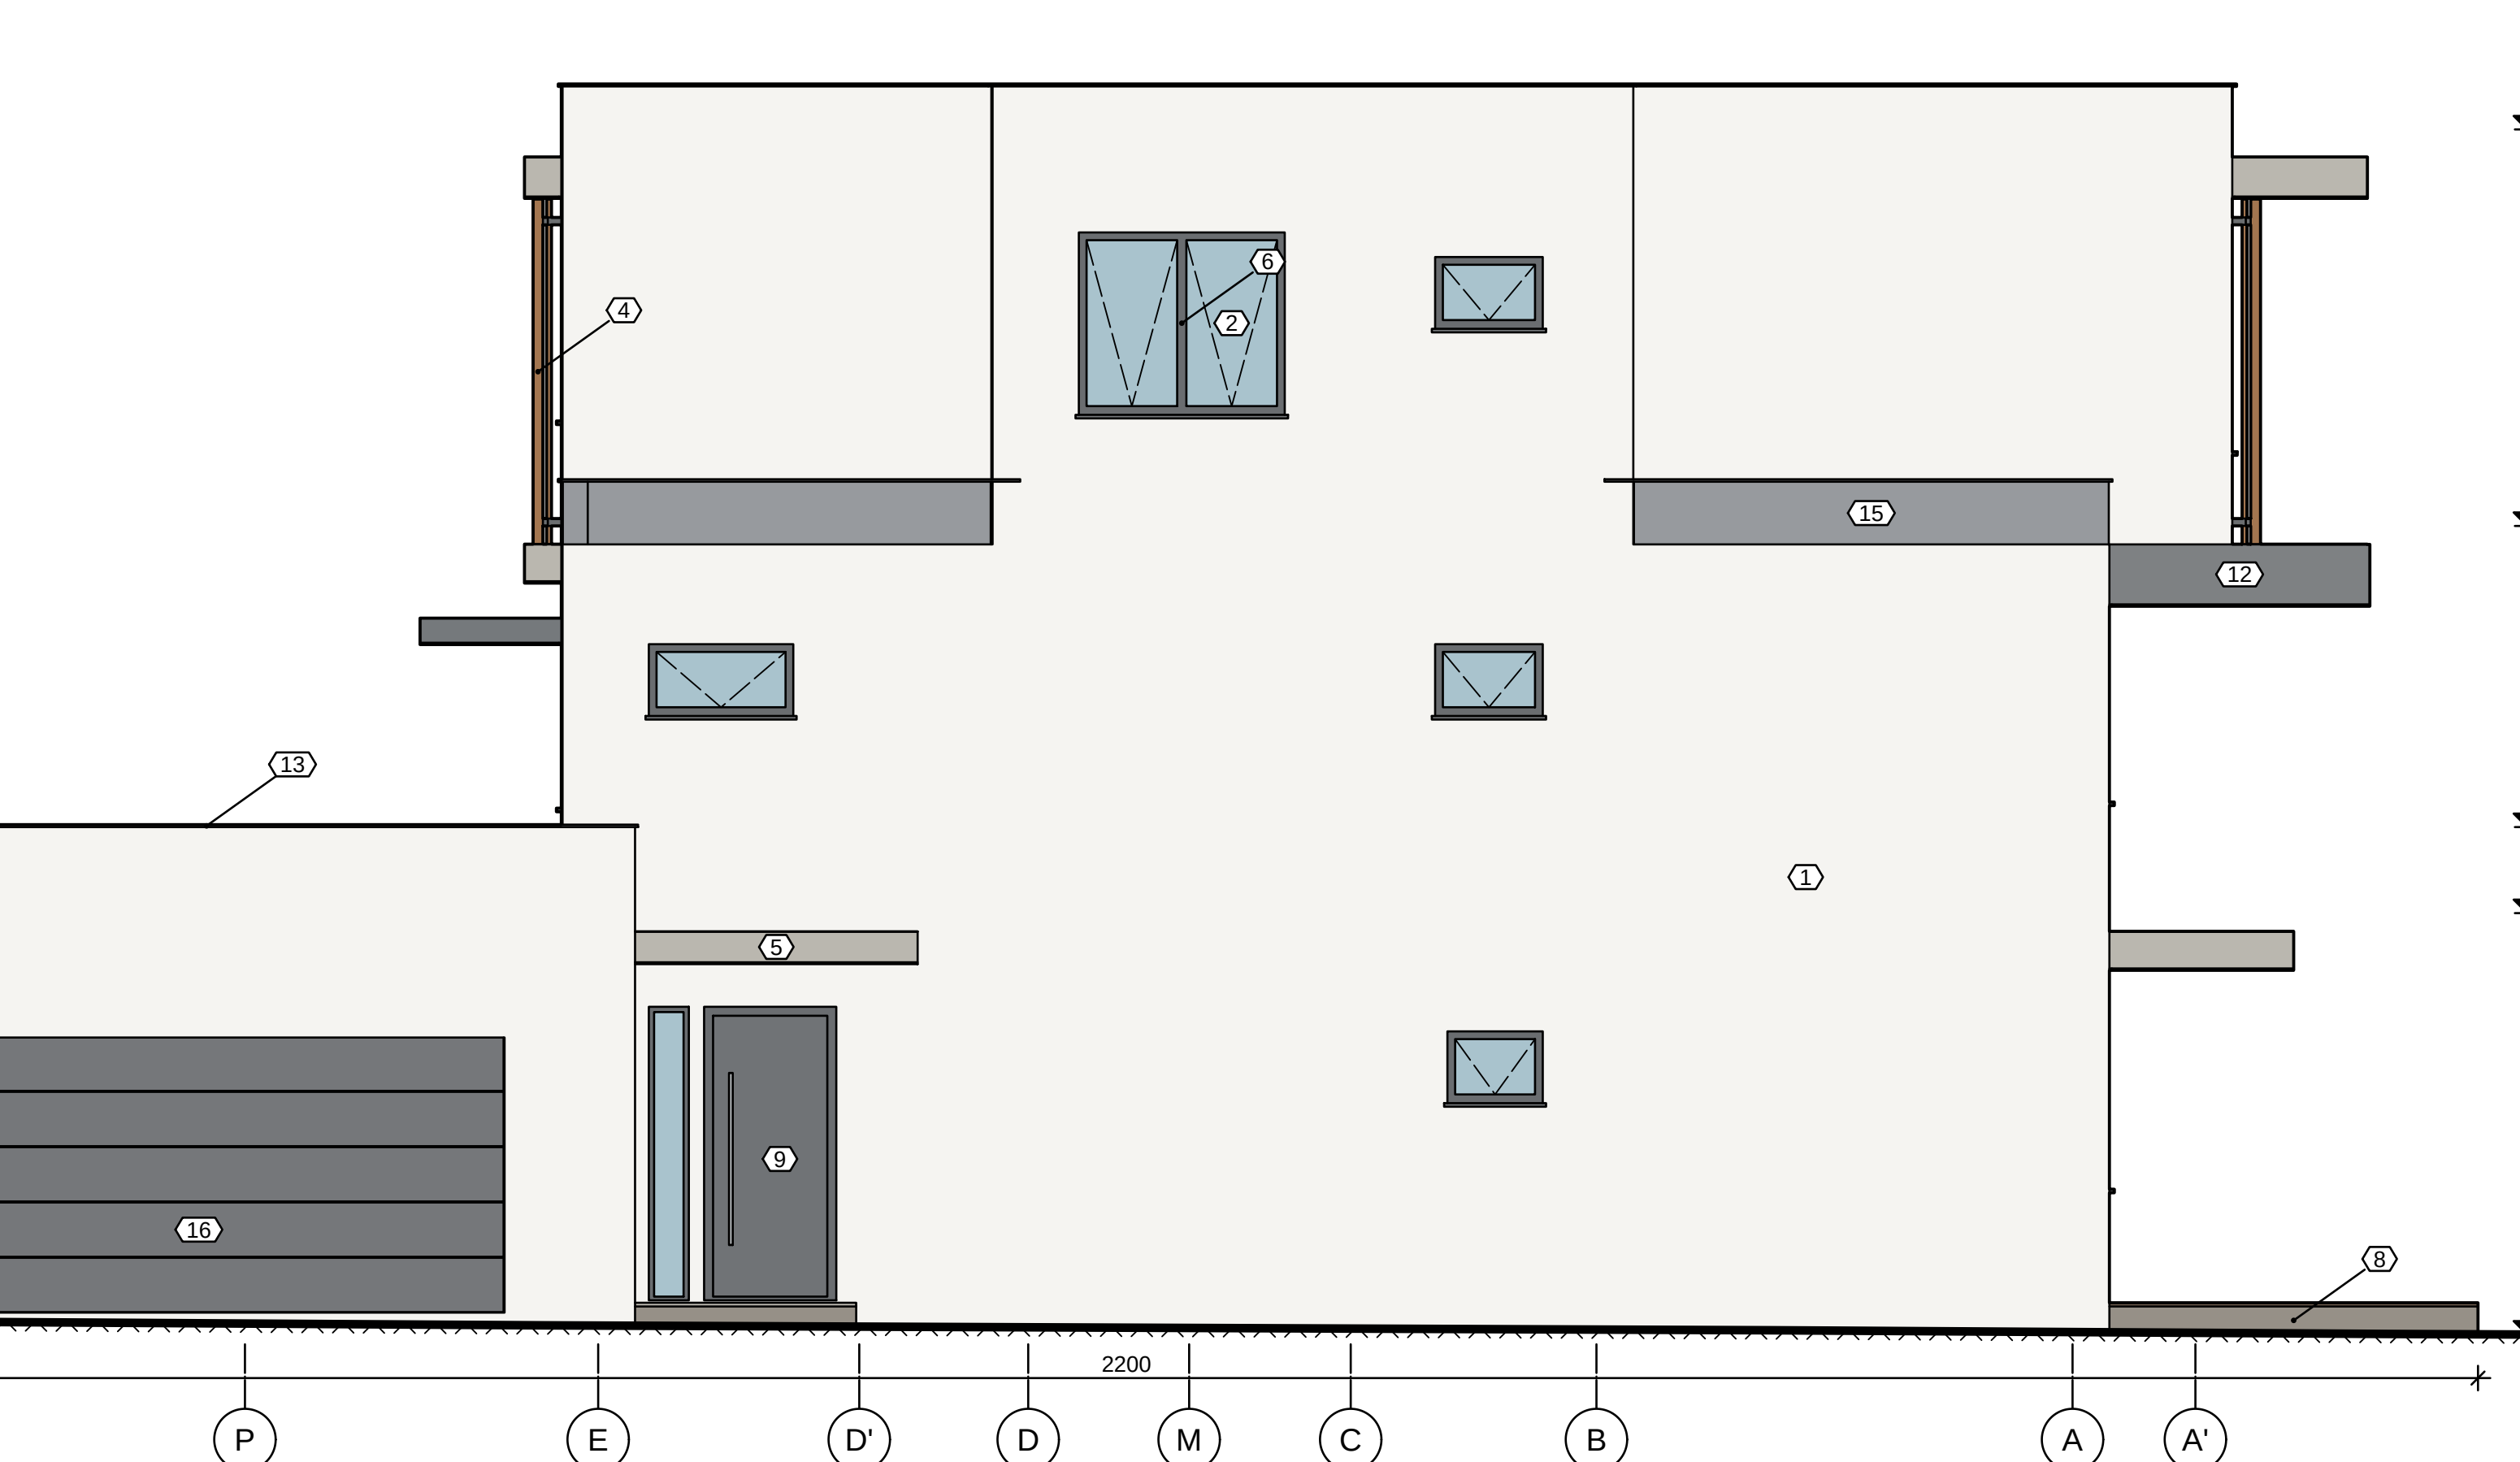

ELEWACJA PÓŁNOCNA (OD ULICY) 1:50

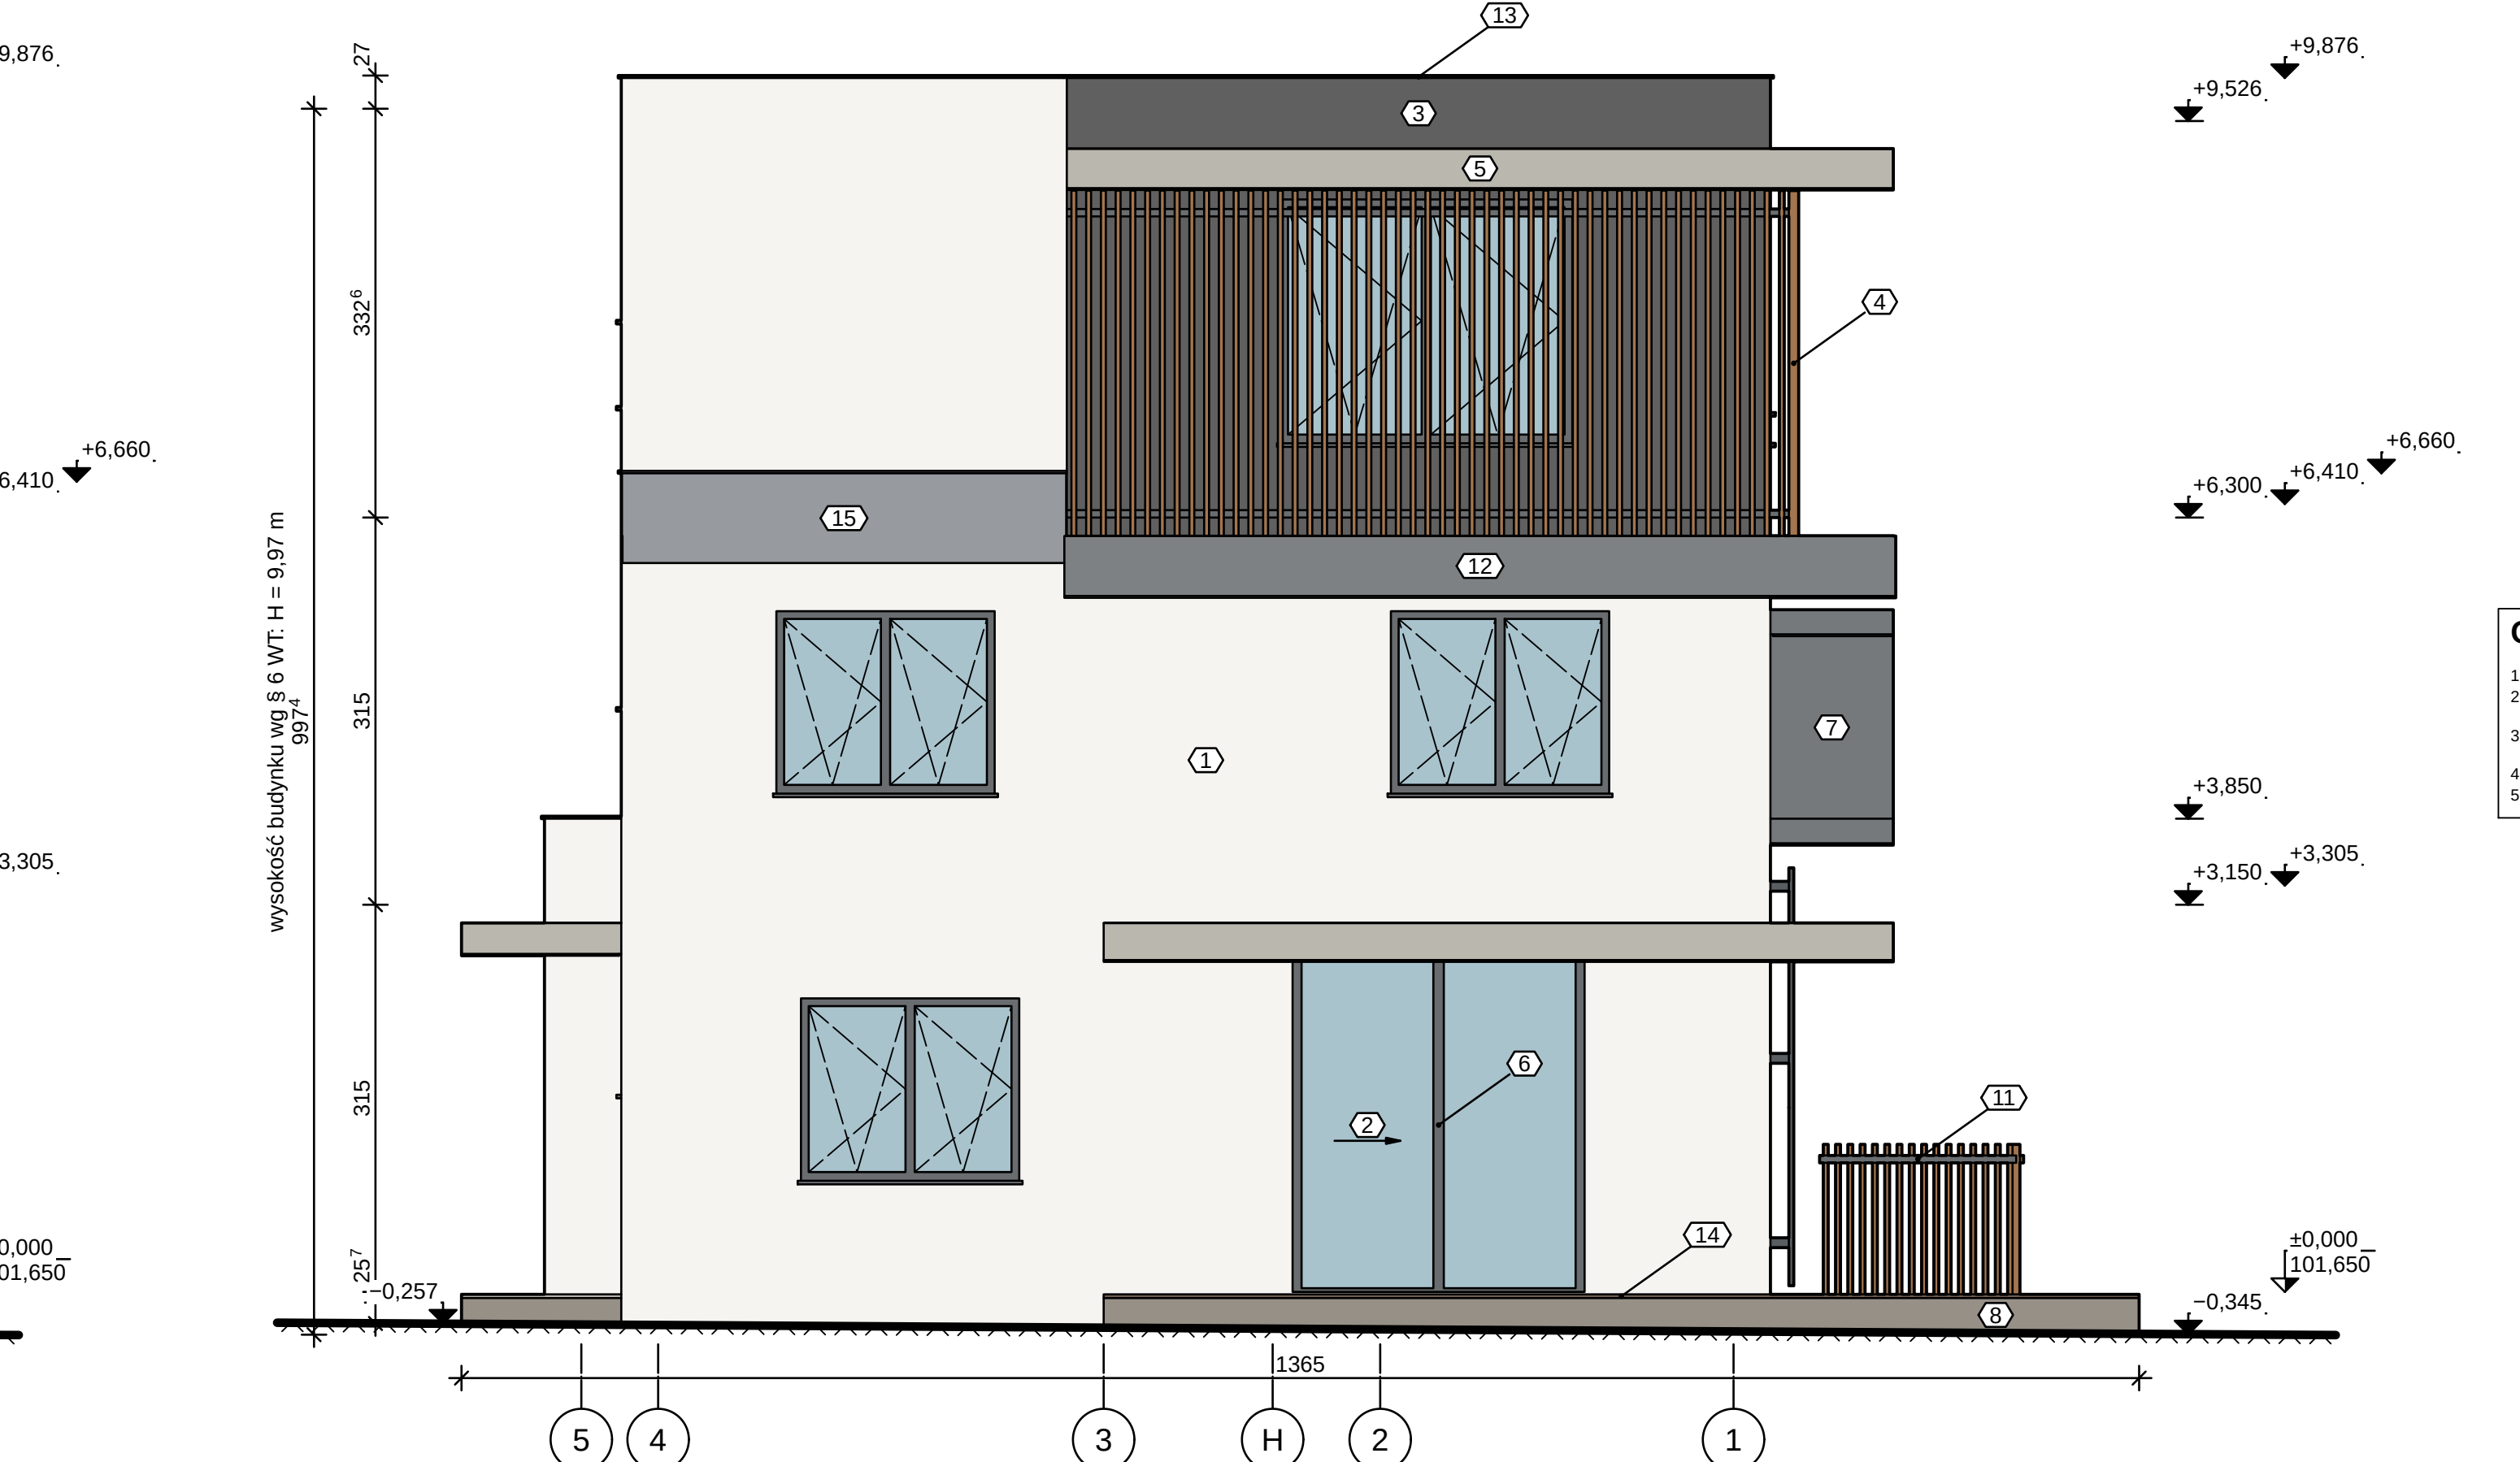

ELEWACJA ZACHODNIA 1:50

KOLORYSTYKA I MATERIAŁY ELEWACJI

1	ETICS: warstwa zbrojona + tynk silikonowy 1,5 mm (biały) / jasnoszary NCS S 1500-N [TYNK_SIL]	#F5F4D0
2	Szkoło (szyby zespolone) [SZKLO]	#A9C3D3
3	Membrana fasadowa wiatroizolacyjna UV-stabilna, czarna (sd = 0,02 m) [MEMB_WIATR]	#1D1D1D
4	Lamele elewacyjne 40x80 mm, drewno termoojone (klasa 1 trwałość), olejowane [DREWNO_TERMO]	#96B4D1
5	Żelbet C30/37 XC4XF1 (krawędzie płyt wysuniętych, atyki, belki) [ZB_C30]	#B4B1A9
6	Stolarka — profile aluminiowe, antracyt [RAMA_ALU]	#2B2B33
7	Rama boku C: ruszt stalowy ocynkowany w okładzinie z blachy aluminiowej RAL 7016 (pusta w środku) [RAMA_C]	#3B4044
8	Podbudowa nawierzchni (kusztywo) [NAW_PODBUDOWA]	#8B877D
9	Drzwi zewnętrzne, płycina aluminiowa [DRZWI_ZEWNI]	#343B3C
10	Stal S235 ocynkowana ogniochrona, malowana proszkowo RAL 7016 — kratownica prężąca (pręty Ø12 w siatce 0,30 m, rama 40x40) [STAL_OCYNK]	#A8A055
11	Stal malowana proszkowo (balustrady, rylce) [STAL_BAL]	#2C3034
12	Podsiłkita zewnętrzna: płyta włóknocementowa 12 mm na ruszcie, RAL 7016 [PODSUF]	#474B4F
13	Obróbki blacharskie (blacha powlekana) [OBRÓBKA_BLACH]	#3B3433
14	Deska tarasowa [NAW_DESKA]	#6D5847
15	Styropian grafitowy EPS 031 (ETICS, NRO w systemie) [EPS031]	#8B2956
16	Brama garażowa segmentowa [BRAMA_GAR]	#3A3E42

OBJAŚNIENIA I UWAGI

- Wymiary w cm (mm w indeksie górnym, np. 24" = 24,5 cm), rzędne w m względem ±0,000 = 101,650 m n.p.m. (PL-EVRF2007-NH).
- Rzędne: trójką zaczerniony — poziom wykończenia, niezaczerzony — konsurkacja, w pokoiu zaczerniony — poziom ±0,000 z rzędną bezwzględna (PN-B-01025).
- Wysokość budynku wg § 6 WT: H = 9,97 m od terenu przy najniższym położonym wejściu (-0,348) do wierzchu stropodachu D1 (+9,626) — H = 9,97 m (bez atyki).
- Kolorystyka orientacyjna wg kolorów materiałów w modelu (do potwierdzenia wzornikiem RAL/NCs).
- Rysunek wygenerowany automatycznie z modelu model/budynki.yam (wersja 1.0, 2026-09-25) — generatory lamele.views.

REW.	OPIS ZMIANY	DATA
0	Wydanie — rysunek wygenerowany z modelu	2026-09-25

PRACOWNIA PROJEKTOWA — nazwa do uzupełnienia	PB	ARCHITEKTURA (AR)
adres pracowni do uzupełnienia		

INWESTOR (do uzupełnienia)			
Budynek mieszkalny jednorodzinny wolnostojący „Dom LAMELA”			
ADRES / LOKALIZACJA (NR DZIAŁKI, OBREB, JEDN. EWIDENCYJNA)		KAT. OBIEKTU	
ul. Lipowa (fikcyjna), dz. nr ewid. 123/4, obręb 0005 Przykładowo, gm. Przykładowo (fikcyjna)		I	

FUNKCJA	IMIĘ I NAZWISKO	SPECJALNOŚĆ, NR UPRAWNIEN	DATA	PODPIS
Projektant	[DO UZUPEŁNIENIA]	[DO UZUPEŁNIENIA]		
Projektant (wsp.)	[DO UZUPEŁNIENIA]	[DO UZUPEŁNIENIA]		
Sprawdzający	nie dotyczy (art. 20 ust. 3 pkt 2 PB)	—		
Opracował	[DO UZUPEŁNIENIA]	[DO UZUPEŁNIENIA]		

TYTUŁ RYSUNKU				
ELEWACJE				
SKALA	FORMAT	DATA WYDANIA	RODZAJ DOK.	NR RYSUNKU
1:50	2050x297	2026-09-25	elewacja	PB-AR-05
ARKUSZ			REW.	
5/5			0	