

PROJEKT ARCHITEKTONICZNO-BUDOWLANY — RYSUNKI

Lp.	Nr rys.	Tytuł rysunku	Skala	Format
1	PB-AR-01	RZUT PARTERU	1:50	620×594
2	PB-AR-02	RZUT I PIĘTRA	1:50	594×480
3	PB-AR-03	RZUT II PIĘTRA I RZUT DACHU	1:50	590×891
4	PB-AR-04	PRZEKROJE A-A I B-B	1:50	1150×420
5	PB-AR-05	ELEWACJE	1:50	2050×297

PRACOWNIA PROJEKTOWA PRACOWNIA PROJEKTOWA — nazwa do uzupełnienia		STADIUM PB	BRANŻA ARCHITEKTURA (AR)			
INWESTOR (do uzupełnienia)						
OBIEKT / NAZWA ZAMIERZENIA BUDOWLANEGO Budynek mieszkalny jednorodzinny wolnostojący „Dom LAMELA”						
ADRES / LOKALIZACJA (NR DZIAŁKI, OBRĘB, JEDN. EWIDENCYJNA) ul. Lipowa (fikcyjna), dz. nr ewid. 123/4, obręb 0005 Przykładowo, gm. Przykładowo (fikcyjna)				KAT. OBIEKTU I		
FUNKCJA	IMIĘ I NAZWISKO	SPECJALNOŚĆ, NR UPRAWNIENI	DATA	PODPIS		
Projektant	[DO UZUPEŁNIENIA]	[DO UZUPEŁNIENIA]				
Projektant (wsp.)	[DO UZUPEŁNIENIA]	[DO UZUPEŁNIENIA]				
Sprawdzający	nie dotyczy (art. 20 ust. 3 pkt 2 PB)	—				
Opracował	[DO UZUPEŁNIENIA]	[DO UZUPEŁNIENIA]				
TYTUŁ RYSUNKU SPIS RYSUNKÓW						
SKALA —	FORMAT A4	DATA WYDANIA 2026-09-25	RODZAJ DOK. spis	NR RYSUNKU PB-AR-00	ARKUSZ —	REW.

RZUT PARTERU 1:50

ZESTAWIENIE POMIESZCZEŃ

Nr	Nazwa pomieszczenia	Posadzka	Kat.	Wys. [m]	Pow. [m²]
1.06	Salon + jadalnia + kuchnia	Deska warstwowa dębowa 15 mm, klejona	podst.	2,77	54,44
1.13	Garaż 2-stanowiskowy	Posadzka żywiczna epoksydowa antypoślizgowa R11 (garaż)	pomoc.	2,76	37,42
1.10	Pokój gościnny / gabinet	Deska warstwowa dębowa 15 mm, klejona	podst.	2,77	12,52
1.12	Pomieszczenie techniczne	Płytki gresowe 60×120 na kleju C2TE S1	techn.	2,76	8,85
1.11	Przedśionek gospodarczy	Płytki gresowe 60×120 na kleju C2TE S1	ruchu	2,76	7,18
1.02	Hol	Płytki gresowe 60×120 na kleju C2TE S1	ruchu	2,77	4,44
1.01	Wiatrołap	Płytki gresowe 60×120 na kleju C2TE S1	ruchu	2,77	3,89
1.09	Łazienka gościnna (natrysk)	Płytki gresowe 60×120 na kleju C2TE S1	pomoc.	2,77	3,84
1.07	Pas komunikacyjny przy schodach	Deska warstwowa dębowa 15 mm, klejona	ruchu	2,77	3,51
1.16	Schowek pod spocznikiem (h < 1,40)	Płytki gresowe 60×120 na kleju C2TE S1	pomoc.	1,37	2,91
1.04	Klatka schodowa	Deska warstwowa dębowa 15 mm, klejona	ruchu	2,77	2,78
1.03	WC gościnne	Płytki gresowe 60×120 na kleju C2TE S1	pomoc.	2,77	2,32
1.15	Schowek pod schodami (h 1,40–2,20)	Płytki gresowe 60×120 na kleju C2TE S1	pomoc.	1,80	1,45
1.08	Przedpokój gościnny	Deska warstwowa dębowa 15 mm, klejona	ruchu	2,77	1,44
1.05	Spizarnia	Płytki gresowe 60×120 na kleju C2TE S1	pomoc.	2,77	1,02
1.14	Szacht instalacyjny SI		techn.	2,77	0,45
RAZEM powierzchnia netto					148,45
w tym podstawowa + pomocnicza					115,91

OZNACZENIA MATERIAŁÓW (PN-B-01030 + przyjęte)


	Wełna mineralna 035 (szkielet, docieplenia, ściana dom–garaż) — meander „UUU”		Stal konstrukcyjna S355 (słupy RK, rama boksu C), cynkowana ogniowo + malowana proszkowo RAL 7016 — zaczemienie
	Styropian grafitowy EPS 031 (ETICS, NRO w systemie) — sygnak „VVV”		Ścianka szklana VSG 2 × 8 mm w ramie aluminiowej (wiatrołap / hol)
	Błoczek wapienno-piaskowy 12 cm, kl. 15 (ścianki działowe, łcowy w klatce); Błoczek wapienno-piaskowy (silikat) 18 cm, kl. 20, gr. 1, na zaprawie cienkowarstwowej — kratka ukośna 45°/135°		Żelbet C25/30, B500SP (stropy, płyta fundamentowa, ściany); Żelbet C30/37 XC4/XF1 (krawędzie płyt wysuniętych, attyki, belki) — 45° na przemian ciągle i przerywane

OZNACZENIA LINII

—	elementy nad płaszczyzną cięcia (obrys płyt, wsporników, brył wyższych kondygnacji)
—	elementy poniżej płaszczyzny cięcia (widok z góry)
- -	osie konstrukcyjne; linia punktowa z pogrubionymi końcami — ślad przekroju


OBJAŚNIENIA I UWAGI

- Wymiary w cm (mm w indeksie górnym, np. 24^o = 24,5 cm), rzędne w m względem ±0,000 = 101,650 m n.p.m. (PL-EVRF2007-NH).
- Rzuty: płaszczyzna cięcia +1,10 m nad posadzką kondygnacji. Linia kreskowa — elementy nad płaszczyzną cięcia (obrys płyt i wsporników, brył wyższych kondygnacji, otwory w stropie nad, belki); linia cienką — elementy poniżej (widok).
- Otwory, licznik — szerokość, mianownik — wysokość w świetle muru, w nawiasie wysokość parapetu; symbol stolarki wg zestawienia stolarki.
- Numeracja pomieszczeń wg PN-B-01025 / PN-EN ISO 4157-2: <nr kondygnacji (parter = 1)><nr>; identyfikator w modelu: <kond>-<nr> (parter = 0).
- Drzwi: strona otwierania (lewej/prawej) wg modelu — patrząc od strony, w którą otwiera się skrzydło.
- Rysunek wygenerowany automatycznie z modelu model/budynk.yam1 (wersja 1.0, 2026-09-25) — generatory lamela.views.

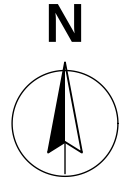

REW.	OPIS ZMIANY			DATA
0	Wydanie — rysunek wygenerowany z modelu			2026-09-25
PRACOWNIA PROJEKTOWA PRACOWNIA PROJEKTOWA — nazwa do uzupełnienia adres pracowni do uzupełnienia			STADIUM PB	BRANŻA ARCHITEKTURA (AR)
INWESTOR (do uzupełnienia)				
OBJEKT / NAZWA ZAMIERZENIA BUDOWLANEGO Budynek mieszkalny jednorodzinny wolnostojący „Dom LAMELA”				
ADRES / LOKALIZACJA (NR DZIAŁKI, OBREB, JEDN. EWIDENCYJNA) ul. Lipowa (fikcyjna), dz. nr ewid. 123/4, obręb 0005 Przykładowo, gm. Przykładowo (fikcyjna)				KAT. OBJEKTU I
FUNKCJA	IMIĘ I NAZWISKO	SPECJALNOŚĆ, NR UPRAWNIENI	DATA	PODPIS
Projektant	[DO UZUPEŁNIENIA]	[DO UZUPEŁNIENIA]		
Projektant (wsp.)	[DO UZUPEŁNIENIA]	[DO UZUPEŁNIENIA]		
Sprawdzający	nie dotyczy (art. 20 ust. 3 pkt 2 PB)	—		
Opracował	[DO UZUPEŁNIENIA]	[DO UZUPEŁNIENIA]		
TYTUŁ RYSUNKU RZUT PARTERU				
SKALA 1:50	FORMAT 620×594	DATA WYDANIA 2026-09-25	RODZAJ DOK. rzut	NR RYSUNKU PB-AR-01
ARKUSZ 1/5			REW. 0	

RZUT II PIĘTRA 1:50

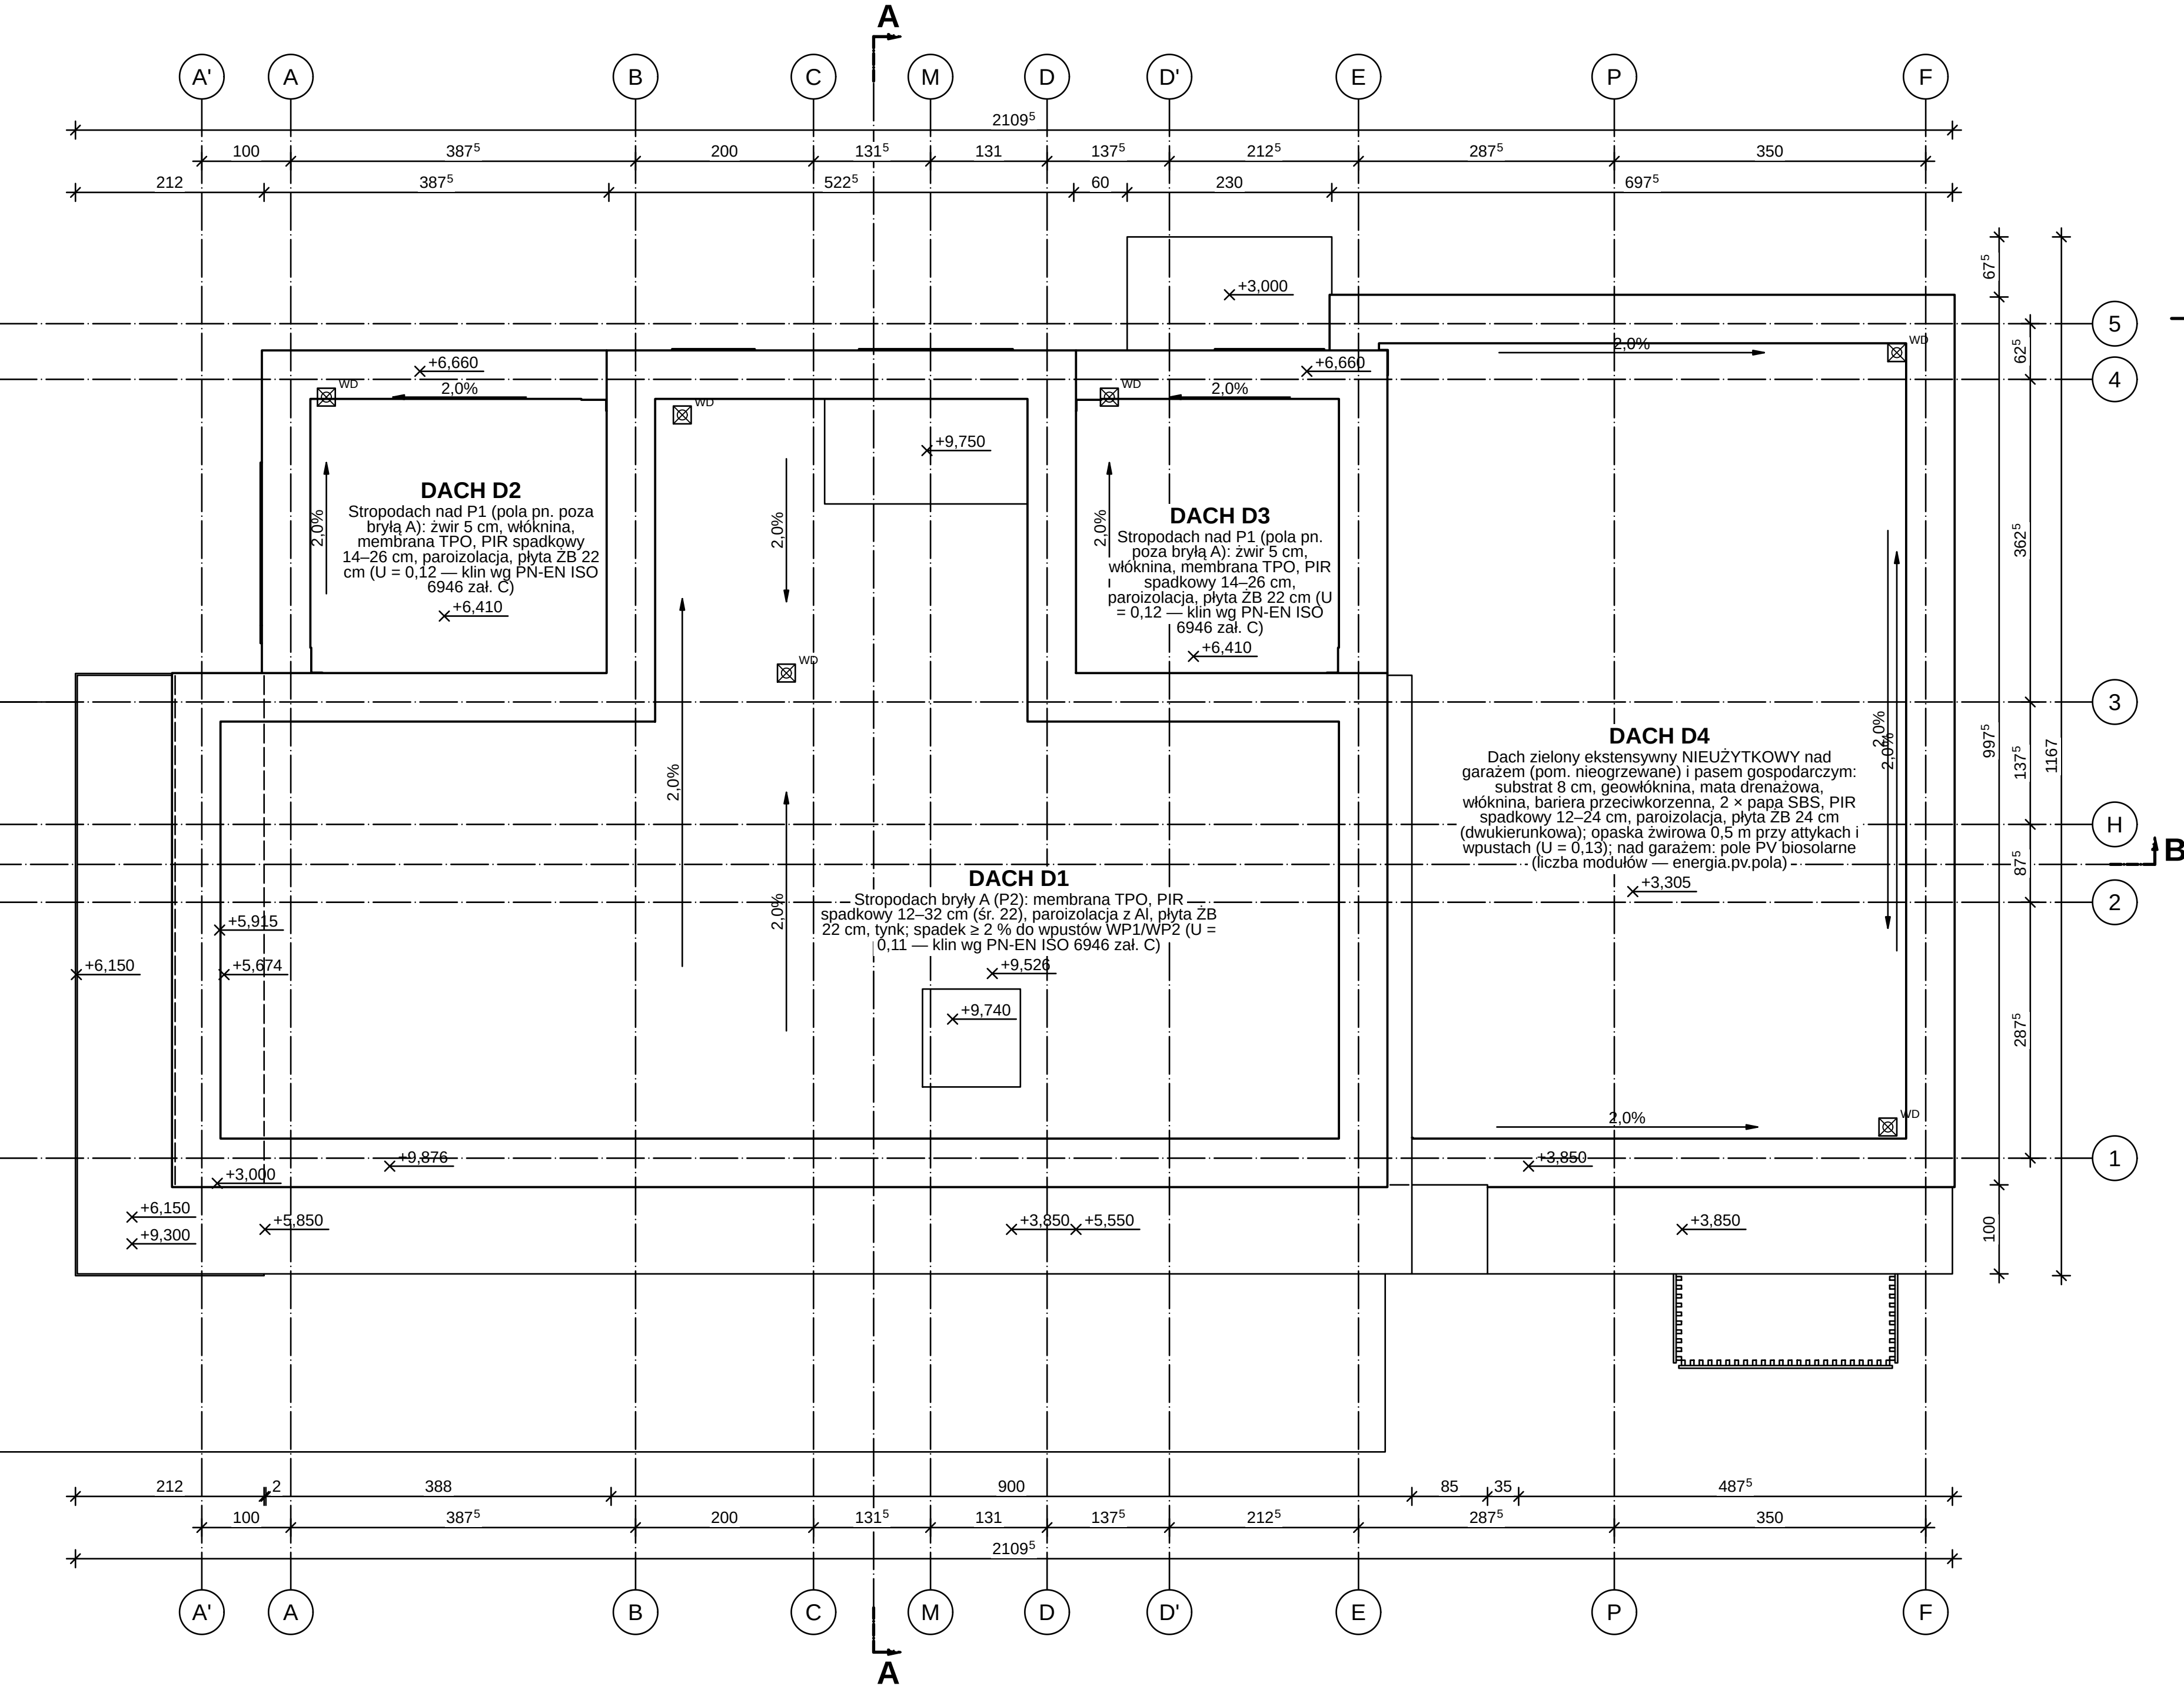

RZUT DACHU 1:50

OZNACZENIA MATERIAŁÓW (PN-B-01030 + przyjęte)

- Włókna mineralna 035 (szkielet, docieplenia, ściana dom-garaż). Włókna mineralna fasadowa (elewacja wentylowana bryły A, A1) — meander „UJU”
- Styropian grafityowy EPS 031 (ETICS, NFO w systemie) — żyrnak „VVV”
- Membrana fasadowa wiatroizolacyjna UV-stabilna, czarna (sd = 0,02 m)
- Błoczek wapniowo-piaskowy 12 cm, kl. 15 (ścianki działowe, łocowy w klatce); Błoczek wapniowo-piaskowy (silikat) 18 cm, kl. 20, gr. 1, na zaprawie cienkowarstwowej — krawka ukośna 45°/135°
- Żelbet C25/30, B500SP (stropy, płyta fundamentowa, ściany); Żelbet C30/37 XC4/XF1 (krawędzie płyt wysuniętych, atyki, belki) — 45° na przemian ciagle i przerywane

OZNACZENIA LINII


- — — — — elementy nad płaszczyzną cięcia (obrys płyt, wsporników, brył wyższych kondygnacji)
- — — — — elementy poniżej płaszczyzny cięcia (widok z góry)
- — — — — osie konstrukcyjne; linia punktowa z pogrubionymi końcami — ślad przekroju

OBJAŚNIENIA I UWAGI

- Wymiary w cm (mm w indeksie górnym, np. 24⁵ = 24,5 cm), rzędne w m względem ±0,000 = 101,650 m n.p.m. (PL-EVRNF2007-NH).
- Rzuty: płaszczyzna cięcia +1,10 m nad posadzką kondygnacji. Linia kreskową — elementy nad płaszczyzną cięcia (obrys płyt i wsporników, brył wyższych kondygnacji, otwory w stropie nad, belki), linia cieniłą — elementy poniżej (widok).
- Ołowy: licznik — szerokość, mianownik — wysokość w świetle muru, w nawiasie wysokość parapetu; symbol stolarki wg zestawienia stolarki.
- Numeracja pomieszczeń wg PN-B-01025 / PN-EN ISO 4157-2: <nr> kondygnacji (parter = 1) > <nr> identyfikator w modelu: <kond>-<nr> (parter = 0).
- Drzwi: strona otwierania (lewe/prawe) wg modelu — patrząc od strony, w którą otwiera się skrzydło.
- Rysunek wygenerowany automatycznie z modelu model/budynki-jam1 (wersja 1.0, 2026-09-25) — generatory lamela.views.

ZESTAWIENIE POMIESZCZEŃ

Nr	Nazwa pomieszczenia	Posadzka	Kat.	Wys. [m]	Pow. [m²]
3.02	Sypialnia rodziców	Deska warstwowa dębowa 15 mm, klejona	podst.	2,77	21,43
3.05	Gabinet / pokój gościnny okazjonalny	Deska warstwowa dębowa 15 mm, klejona	podst.	2,77	16,25
3.03	Garderoba (przedpokój apartamentu)	Deska warstwowa dębowa 15 mm, klejona	pomoc.	2,77	10,49
3.07	Pom. techniczne (centrala rekuperacyjna, wentyl na dach)	Płytki gresowe 60x120 na kleju C2TE S1	techn.	2,77	5,90
3.01	Hol	Deska warstwowa dębowa 15 mm, klejona	ruchu	2,77	5,74
3.04	Łazienka rodziców	Płytki gresowe 60x120 na kleju C2TE S1	pomoc.	2,77	5,51
3.08	Szacht instalacyjny SI		techn.	2,77	0,45
3.06	Klatka schodowa (wyjście z biegu 2, pustaka)	Deska warstwowa dębowa 15 mm, klejona	ruchu	2,77	0,24
RAZEM powierzchnia netto					66,01
w tym podstawowa + pomocnicza					53,67

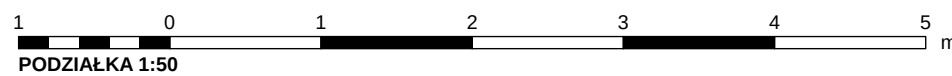

REW.	OPIS ZMIANY	DATA
0	Wydanie — rysunek wygenerowany z modelu	2026-09-25
PRACOWNIA PROJEKTOWA PRACOWNIA PROJEKTOWA — nazwa do uzupełnienia		STADIUM PB
INWESTOR (do uzupełnienia)		BRANŻA ARCHITEKTURA (AR)
OBJEKT / NAZWA ZAMIERZENIA BUDOWLANEGO Budynek mieszkalny jednorodzinny wolnostojący „Dom LAMELA”		
ADRES / LOKALIZACJA (NR DZIAŁKI, OBRĘB, JEDN. EWIDENCYJNA) ul. Lipowa (fikcyjna), dz. nr ewid. 123/4, obręb 0005 Przykładowo, gm. Przykładowo (fikcyjna)		KAT. OBJEKTU I
FUNKCJA	IMIĘ I NAZWISKO	SPECJALNOŚĆ, NR UPRAWNIENI
Projektant	[DO UZUPEŁNIENIA]	[DO UZUPEŁNIENIA]
Projektant (wsp.)	[DO UZUPEŁNIENIA]	[DO UZUPEŁNIENIA]
Sprawdzający	nie dotyczy (art. 20 ust. 3 pkt 2 PB)	—
Opracował	[DO UZUPEŁNIENIA]	[DO UZUPEŁNIENIA]
TYTUŁ RYSUNKU		

RZUT II PIĘTRA I RZUT DACHU

SKALA 1:50	FORMAT S90x891	DATA WYDANIA 2026-09-25	RODZAJ DOK. Rzut	NR RYSUNKU PB-AR-03	ARKUSZ 3/5	REW. 0
---------------	-------------------	----------------------------	---------------------	------------------------	---------------	-----------

PRZEKRÓJ A-A 1:50

SD1 — Stropodach bryły A (P2): membrana TPO, PIR spadkowy 12-32 cm (śr. 22), paroizolacja z Al, płyta ZB 22 cm, tynk; spadek z 2 % do wpustów WP1/WP2 (U = 0,11 — klin wg PN-EN ISO 6946 zał. C)
Membrana dachowa TPO 1,5 mm, mocowana mechanicznie (hydroizolacja stropodachów) 2 mm.
Płyty PIR z okładziną (izolacja spadkowa stropodachów) 22 cm
Paroizolacja bitumiczna z wkładką Al (na płycie stropodachów) 4 mm
Żelbet C25/30, B500SP (stropy, płyta fundamentowa, ściany) 22 cm
Tynk gipsowy maszynowy 1 cm

PRZEKRÓJ B-B 1:50

SD1 — Stropodach bryły A (P2): membrana TPO, PIR spadkowy 12-32 cm (śr. 22), paroizolacja z Al, płyta ZB 22 cm, tynk; spadek z 2 % do wpustów WP1/WP2 (U = 0,11 — klin wg PN-EN ISO 6946 zał. C)
Membrana dachowa TPO 1,5 mm, mocowana mechanicznie (hydroizolacja stropodachów) 2 mm.
Płyty PIR z okładziną (izolacja spadkowa stropodachów) 22 cm
Paroizolacja bitumiczna z wkładką Al (na płycie stropodachów) 4 mm
Żelbet C25/30, B500SP (stropy, płyta fundamentowa, ściany) 22 cm
Tynk gipsowy maszynowy 1 cm

OZNACZENIA MATERIAŁÓW (PN-B-01030 + przyjęte)

- Lamele dębowe 30×60 mm (ekran komunikacji P0, h 2,10 m);
Deska warstwowa dębowa 15 mm, klejona — przekrój wzdłuż;
grunt rodzimy
- Substrat ekstensywny 8 cm z matą rozchodnikową (sedum)
- Włeha mineralna fasadowa (elewacja wentylowana bryły A, A1);
Włeha mineralna 035 (szkielet, docieplenia, ściana dom-garaż)
— meander „UUU”
- Płyty PIR z okładziną (izolacja spadkowa stropodachów) —
zygzak z okładzinami
- Izolacja przeciwwilgociowa i przeciwradonowa: membrana SBS
4 mm na płycie fundamentowej — linia bardzo gruba
- Membrana dachowa TPO 1,5 mm, mocowana mechanicznie (hydroizolacja stropodachów);
Hydroizolacja 2 + papa SBS (podkładowa + wierzchniego krycia, dach zielony) — pas czarno-biały
- Styropian grafitowy EPS 031 (ETICS, NRO w systemie);
Styropian podłogowy EPS 100-038 (pod jaskrychem);
Styropian elastykowany EPS T (akustyczny, pod jaskrychem) — zygzak VVV
- Polistyren ekstrudowany XPS 300 (pod płytą fundamentową,
cokol, izolacja obwodowa) — zygzak podwójny
- Jaskrych cementowy CT-C25-F5 z węzownicą ogrzewania
podłogowego — kropki
- Membrana fasadowa wiatroizolacyjna UV-stabilna, czarna (sd = 0,02 m)
- Błoczek wapienno-piaskowy 12 cm, kl. 15 (ścianki działowe,
łzowy w klatce); Błoczek wapienno-piaskowy (silikat) 18 cm, kl. 20, gr. 1, na zaprawie cienkowarstwowej — krawka ukłosa 45°/135°
- Paroizolacja bitumiczna z wkładką Al (na płycie stropodachów)
— linia kropkowa cienka 30, po ciepłej stronie
- Podsyпка piaskowa zagęszczona (l_s ≥ 0,98)
- Płyta gipsowo-kartonowa 12,5 mm (GKB / GKBi w łazienkach);
Podsufitka zewnętrzna: płyta włóknocementowa 12 mm na ruszcie, RAL 7016
- Obrobki blacharskie (blacha powlekana); Siatarka — profile
aluminowe, antyżyr; Rama boku C: ruszt stacjonary
cynkowany w okładzinie z blachy aluminowej RAL 7016
(pusła w środku); Stal malowana proszkowo (balustrady, rygle)
— zabezpieczenie
- Szkieł (szyby zespolone); Ścianka szklana VSG 2 × 8 mm w
ramie aluminiowej (wiatrołap / hol)
- Żelbet C25/30, B500SP (stropy, płyta fundamentowa, ściany);
Żelbet C30/37 XC-4/XF1 (krawędzie płyt wysuniętych, atyki, belki)
— 45° na przemiian ciągłe i przerywane
- Podbudowa nawierzchni (kruszywo)

OBJAŚNIENIA I UWAGI

- Wymiary w cm (mm w indeksie górnym, np. 24⁵ = 24,5 cm), rzędne w m względem ±0,000 = 101,650 m n.p.m. (PL-EVRF2007-NH).
- Rzędne: trójkąt zaczerpnięty — poziom wykończenia, niezaczerpnięty — konstrukcji, w połowie zaczerpnięty — poziom ±0,000 z rzędną bezwzględną (PN-B-01025).
- Wysokość budynku wg § 6 WT: od terenu przy najbliższym położonym wejściu (~0,348) do wierzchu stropodachu D1 (+9,626) — H = 9,97 m (bez atyki).
- Opisy warstw: kod i nazwa przegrody z modelu, materiały i grubości wg modelu (od góry / od lewej).
- Przekrój A-A: opisy warstw pominięte na rysunku (brak miejsca w podziale 1:50); POD-0, STROP ST2 + POD-1 — układ warstw wg zestawienia przegród w części opisowej / przekroju 1:50.
- Przekrój B-B: opisy warstw pominięte na rysunku (brak miejsca w podziale 1:50); POD-0, STROP ST2 + POD-1, STROP ST22 + POD-1, OK1 — układ warstw wg zestawienia przegród w części opisowej / przekroju 1:50.
- Rysunek wygenerowany automatycznie z modelu modelbudynek.yam! (wersja 1.0, 2026-09-25) — generatory lamela views.




REW.	OPIS ZMIANY		DATA	
0	Wydanie — rysunek wygenerowany z modelu		2026-09-25	
PRACOWNIA PROJEKTOWA PRACOWNIA PROJEKTOWA — nazwa do uzupełnienia			STADIUM PB	BRANŻA ARCHITEKTURA (AF)
INWESTOR (do uzupełnienia)				
OBJEKT / NAZWA ZAMIERZENIA BUDOWLANEGO Budynek mieszkalny jednorodzinny wolnostojący „Dom LAMELA”				
ADRES / LOKALIZACJA (NR DZIAŁKI, OBRĘB, JEDN. EWIDENCYJNA) ul. Lipowa (fikcyjna), dz. nr ewid. 123/4, obręb 0005 Przykładowo, gm. Przykładowo (fikcyjna)				KAT. OBJEKTU I
FUNKCJA	IMIĘ I NAZWISKO	SPECJALNOŚĆ, NR UPRAWNIENI	DATA	PODPIS
Projektant	[DO UZUPEŁNIENIA]	[DO UZUPEŁNIENIA]		
Projektant (wsp.)	[DO UZUPEŁNIENIA]	[DO UZUPEŁNIENIA]		
Sprawdzający	nie dotyczy (art. 20 ust. 3 pkt 2 PB)	—		
Opracował	[DO UZUPEŁNIENIA]	[DO UZUPEŁNIENIA]		

PRZEKROJE A-A I B-B


SKALA	FORMAT	DATA WYDANIA	RODZAJ DOK.	NR RYSUNKU	ARKUSZ	REW.
1:50	1150×420	2026-09-25	przekrój	PB-AR-04	4/5	0




ELEVACJA POŁUDNIOWA (OGRODOWA) 1:50

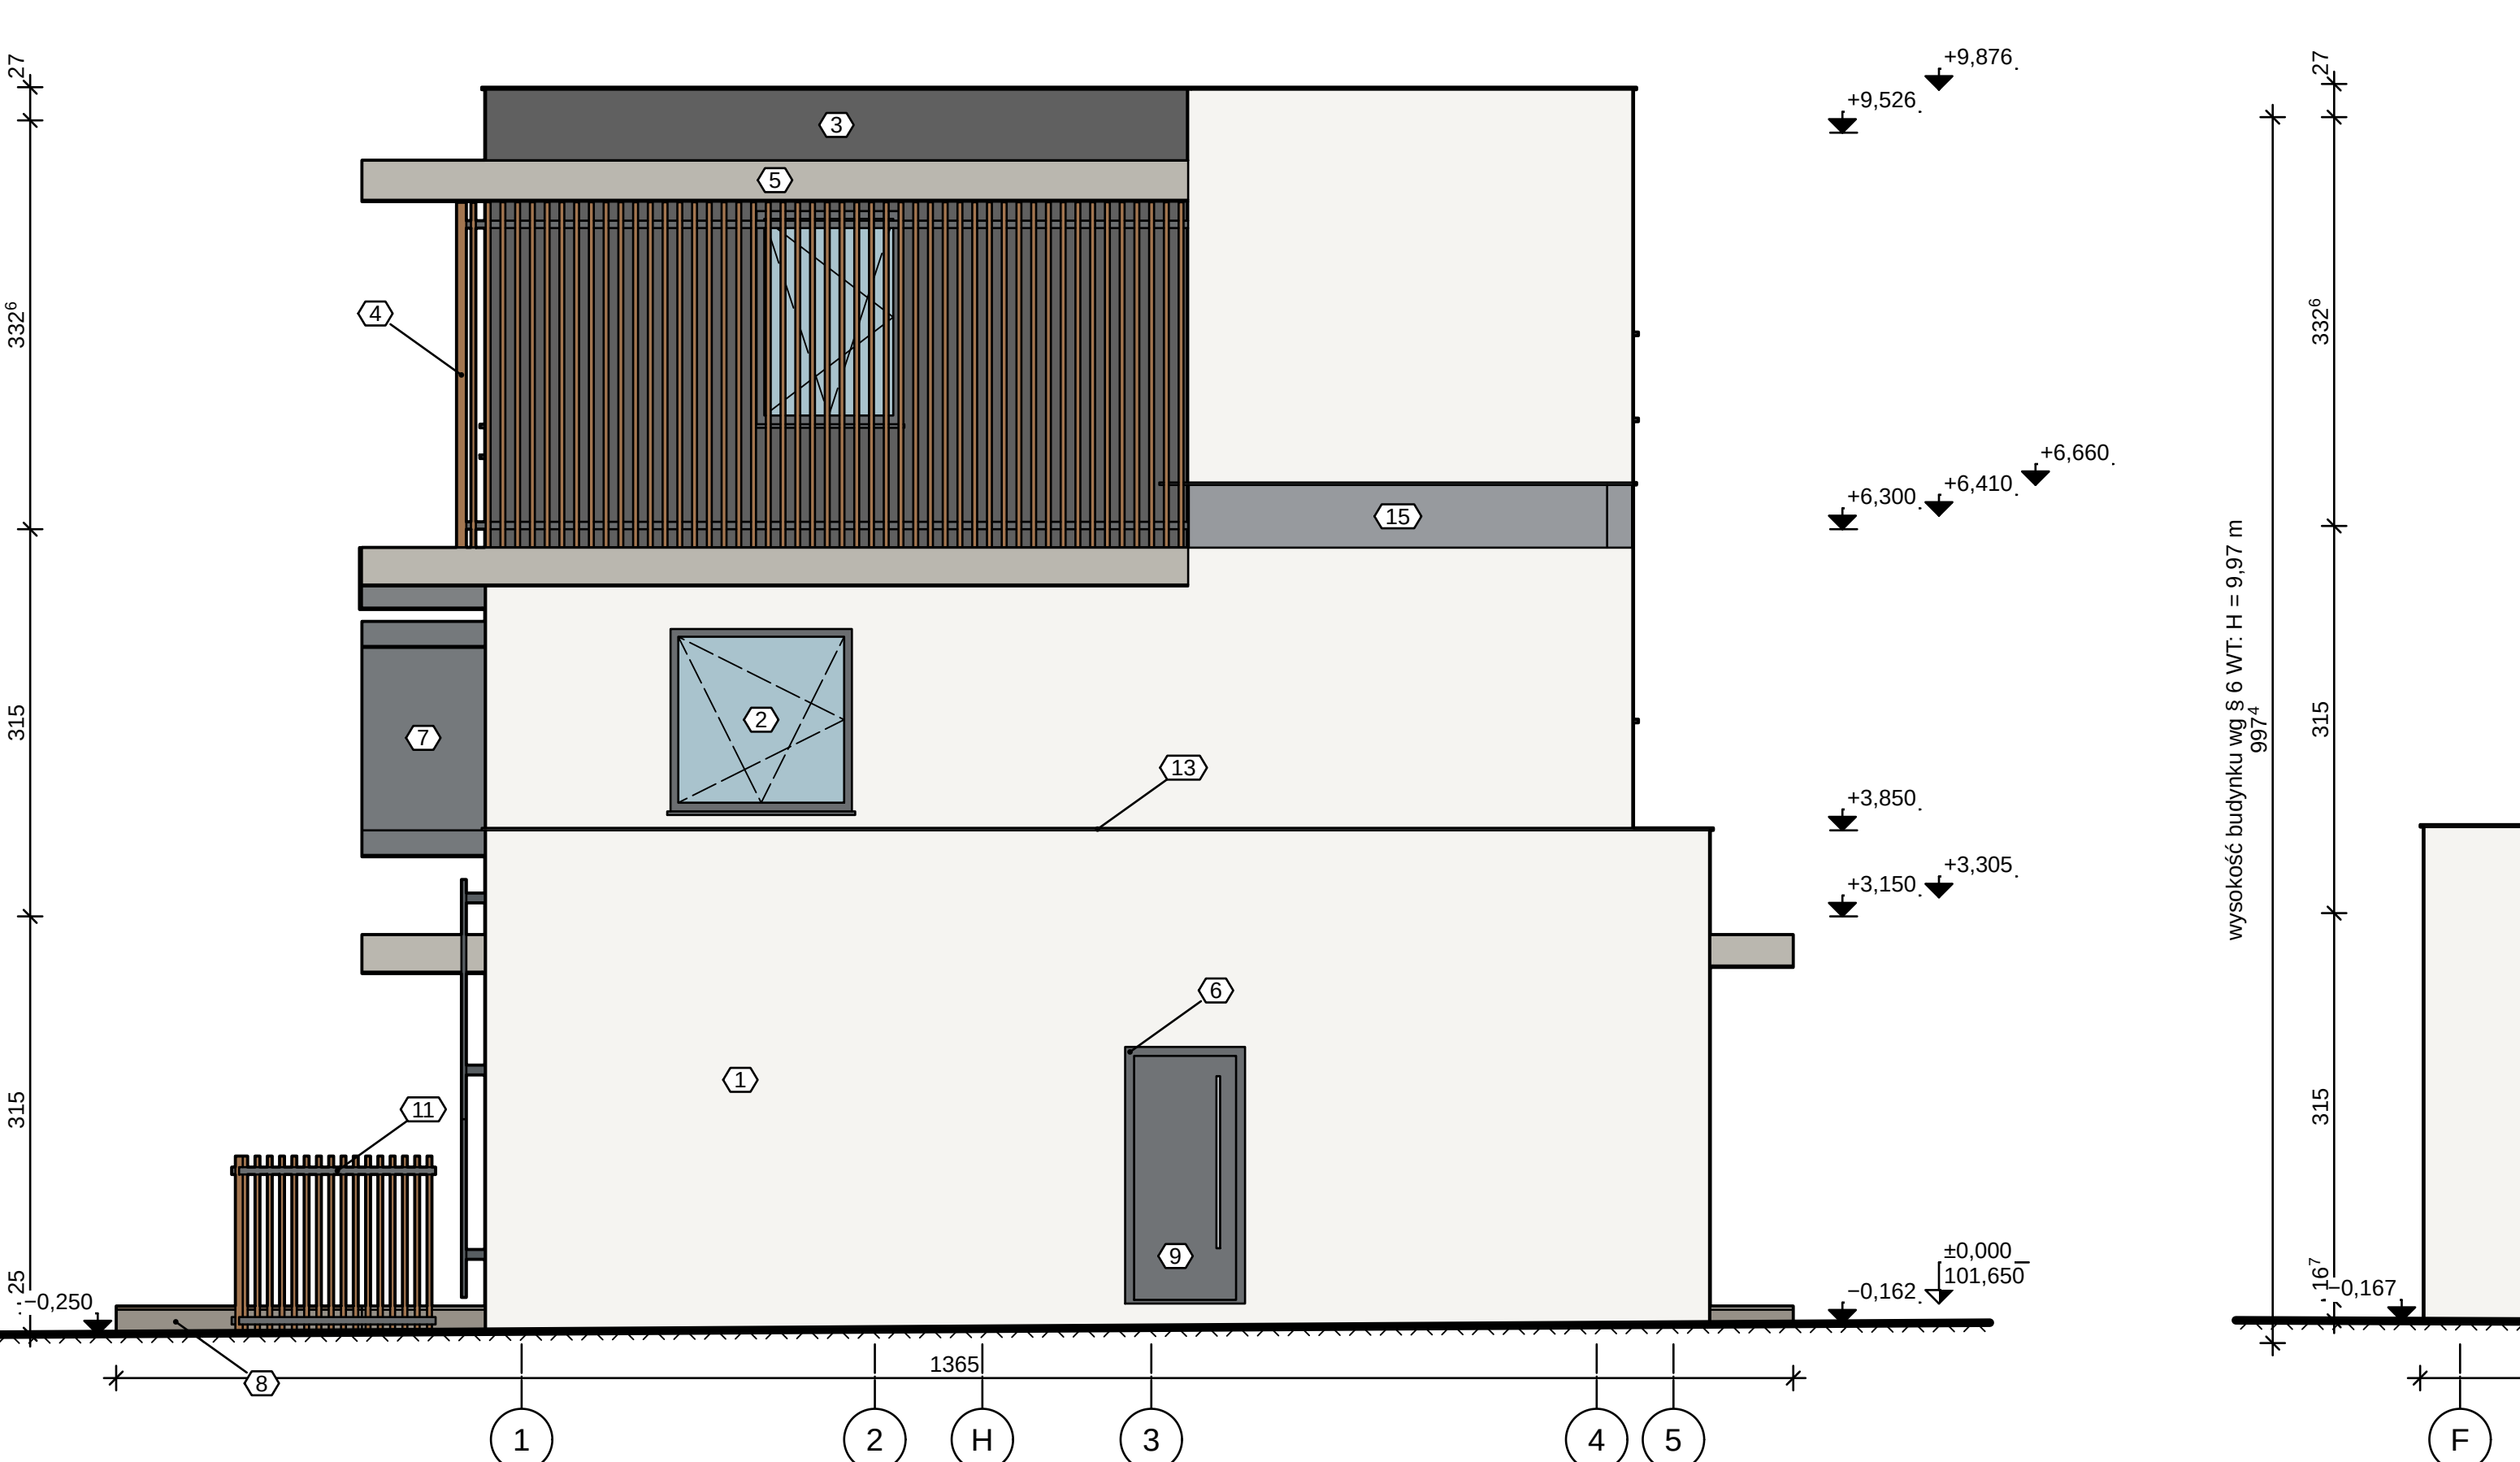

ELEVACJA WSCHODNIA 1:50

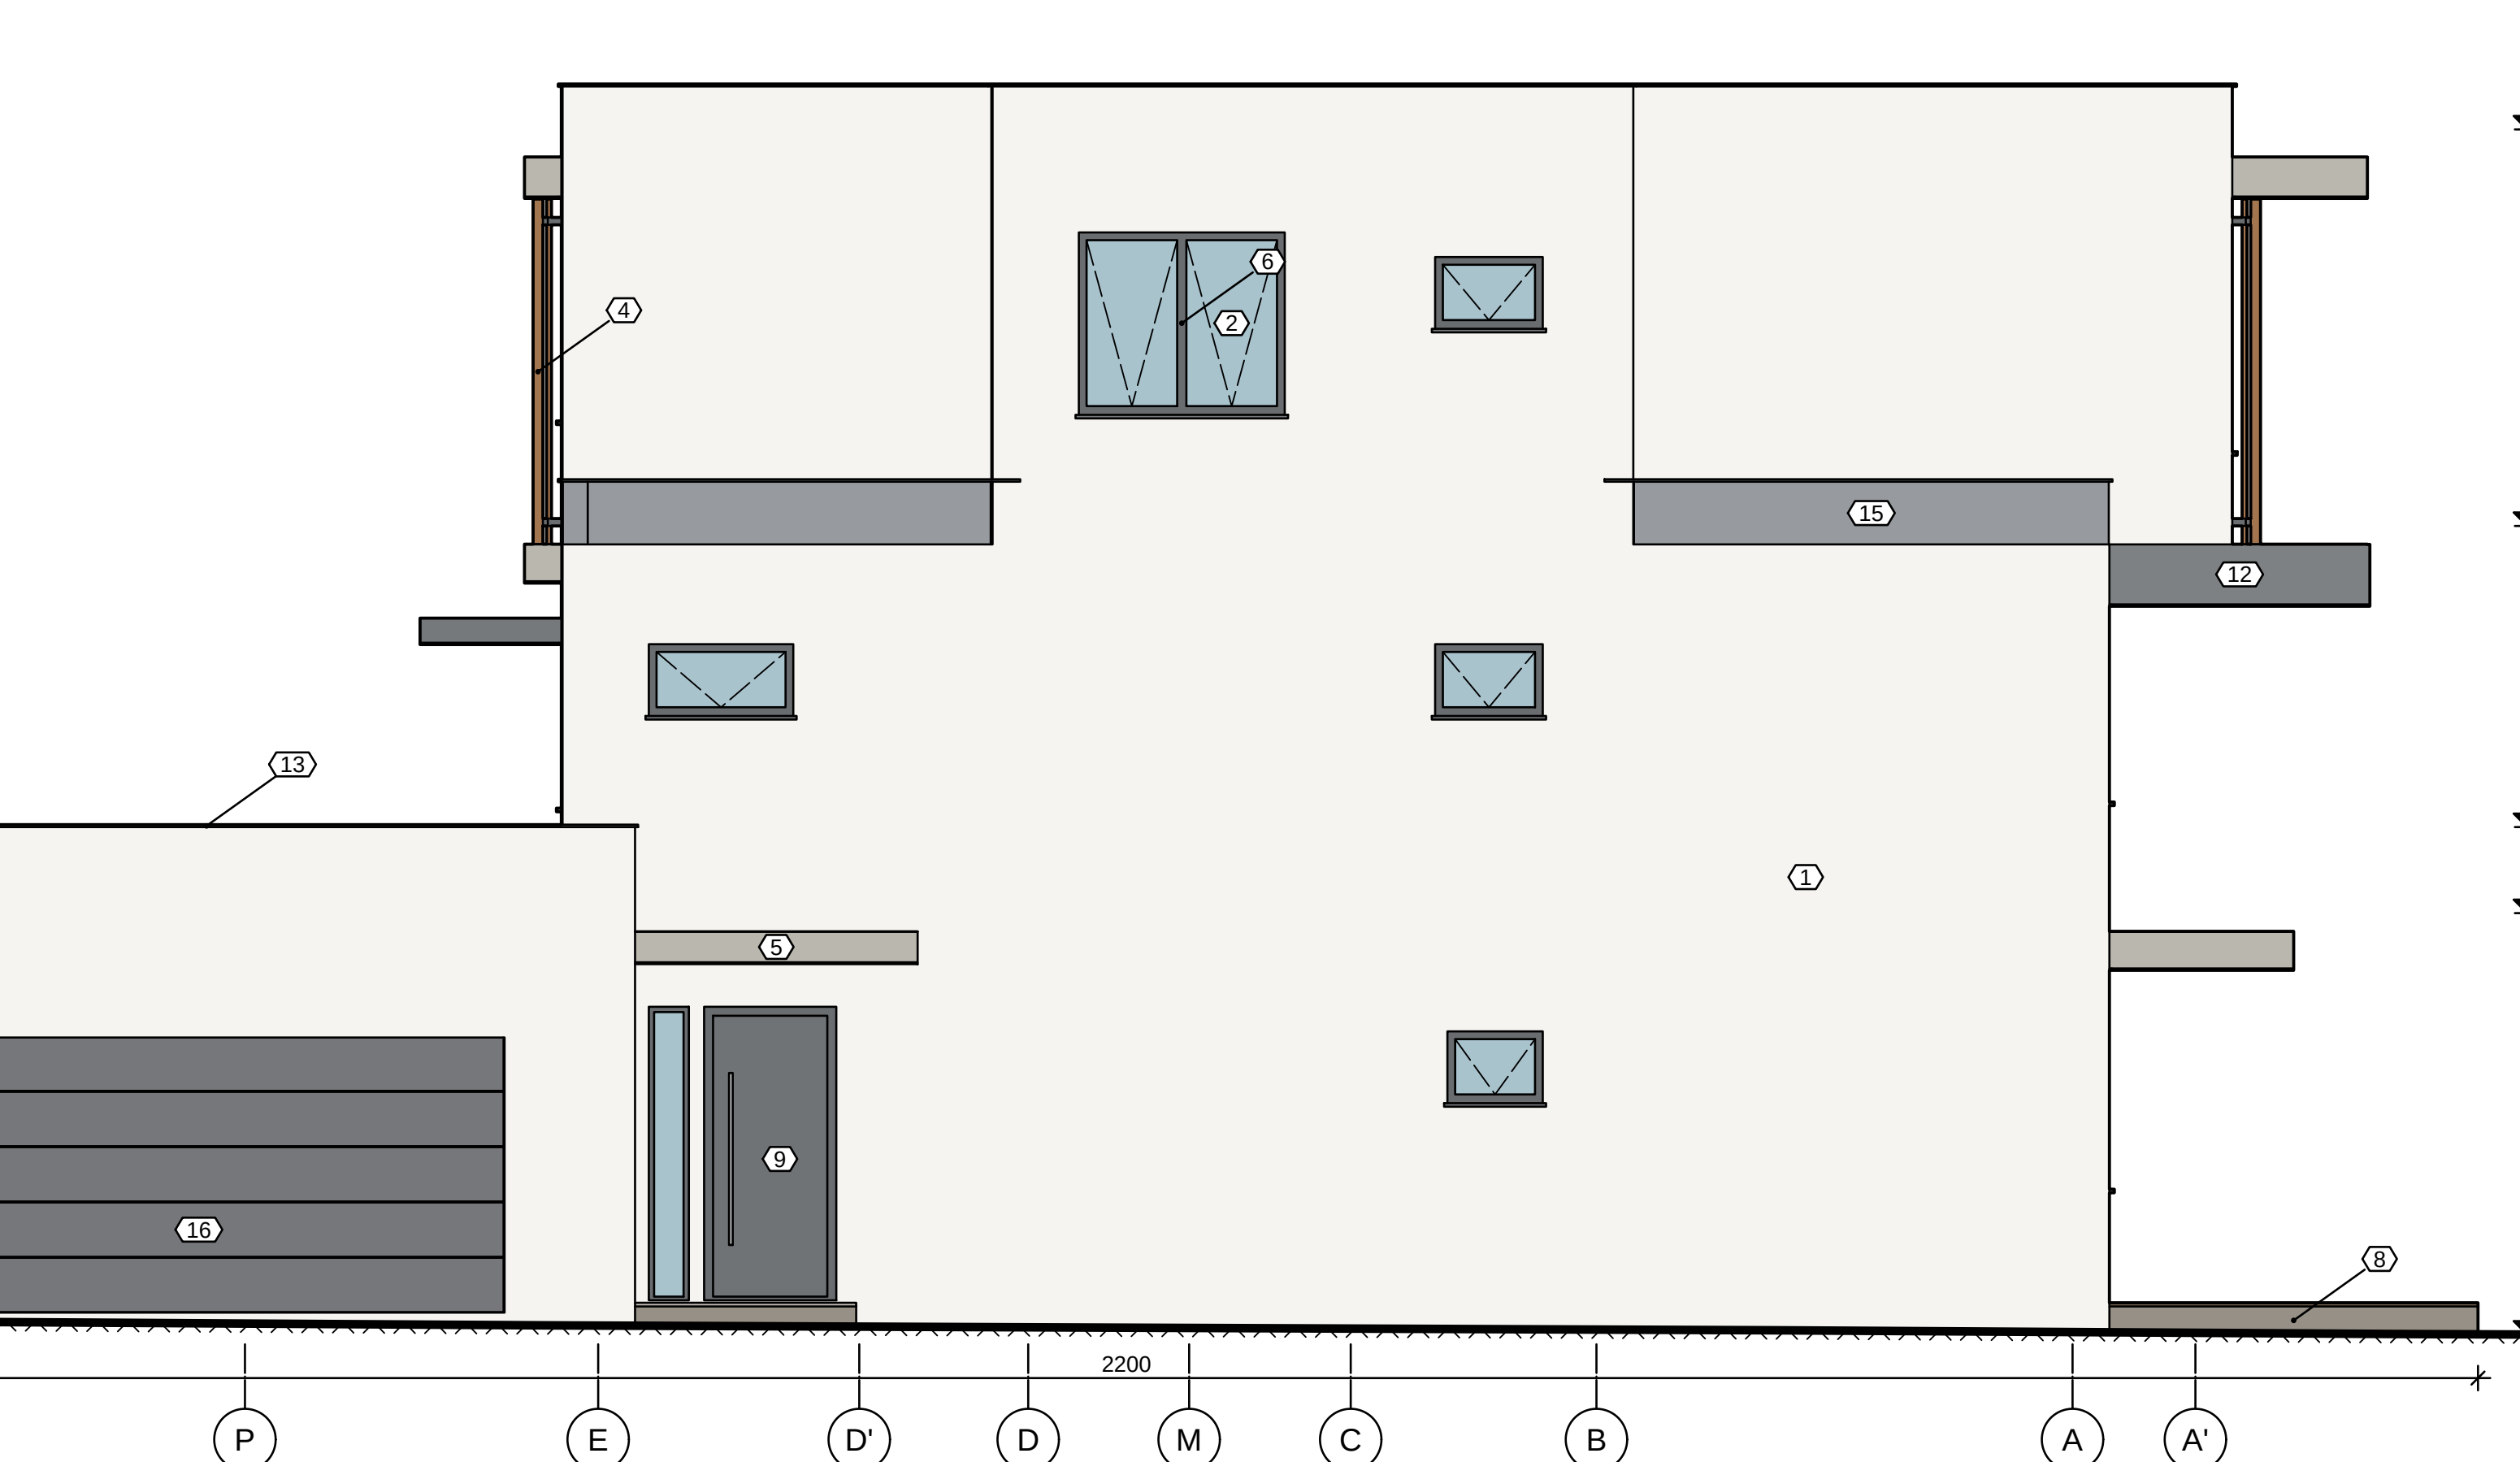

ELEVACJA PÓŁNOCNA (OD ULICY) 1:50

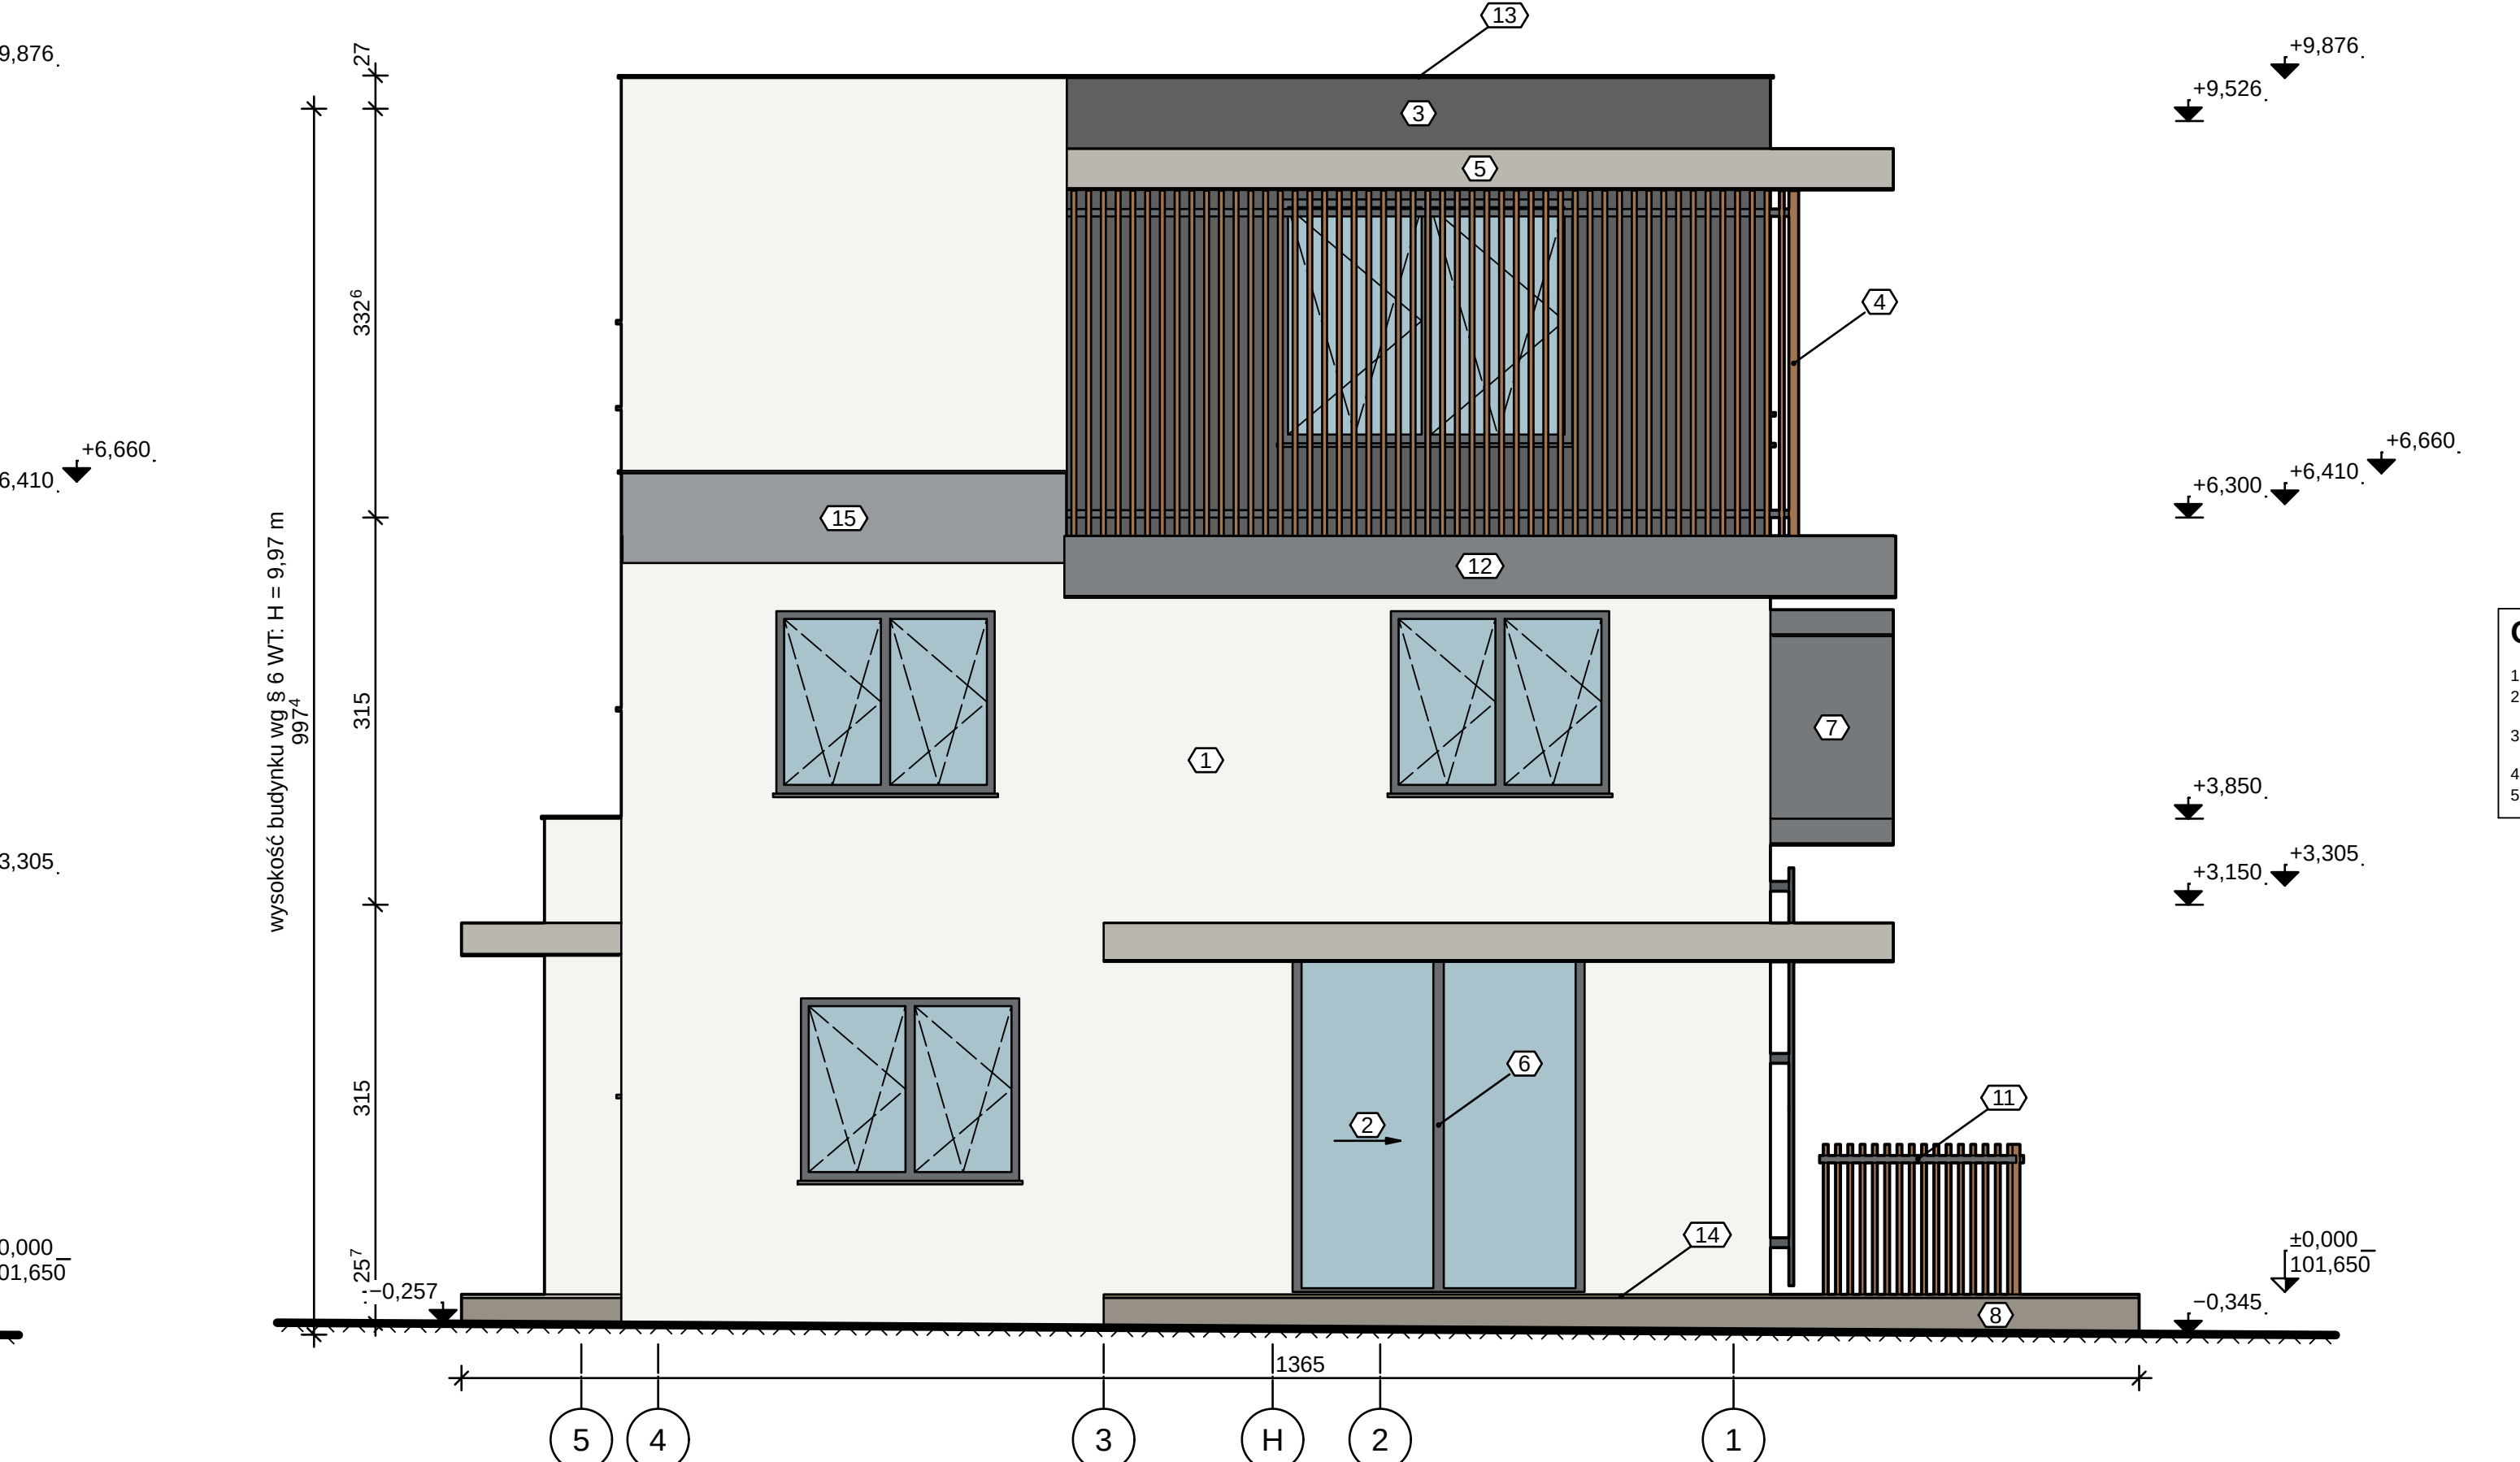

ELEVACJA ZACHODNIA 1:50

KOLORYSTYKA I MATERIAŁY ELEWACJI

1

ETICS: warstwa zbrojona + tynk silikony 1,5 mm (biały) / jasnoszary NCS S 1500-N [TYNK_SIL]

#f5f4f0

2

Szko (szyby zespolone) [SZKLO]

#a9c3cd

3

Membrana fasadowa wiatroizolacyjna UV-stabilna, czarna (sd = 0,02 m) [MEMB_WIATR]

#1d1d1d

4

Lamele elewacyjne 40x80 mm, drewno termojest (klasa 1 trwałość), olejowane [DREWNO_TERMO]

#96b4d1

5

Żelbet C30/37 XC4/F1 (krawędzie płyt wysuniętych, atyki, belki) [ZB_C30]

#b4b1a9

6

Stolarka — profile aluminiowe, antracyt [RAMA_ALU]

#2b2b33

7

Rama boku C: ruszt stalowy ocynkowany w okładzinie z blachy aluminiowej RAL 7016 (pusta w środku) [RAMA_C]

#3b4044

8

Podbudowa nawierzchni (kusztywo) [NAW_PODBUDOWA]

#8b877d

9

Drzwi zewnętrzne, płycina aluminiowa [DRZWI_ZEWNI]

#34383c

10

Stal S235 ocynkowana ogniotrwała, malowana proszkowo RAL 7016 — kratownica prążcy (pręty Ø12 w siatce 0,30 m; rama 40x40) [STAL_OCYNK]

#4a5055

11

Stal malowana proszkowo (balustrady, rylce) [STAL_BAL]

#2c3034

12

Podsiłotka zewnętrzna: płyta włóknocementowa 12 mm na ruszcie, RAL 7016 [PODSUF]

#474b4f

13

Obróbki blacharskie (blacha powlekana) [OBRÓBKA_BLACH]

#3b3b43

14

Deska tarasowa [NAW_DESKA]

#6d5847

15

Styropian grafitowy EPS 031 (ETICS, NRO w systemie) [EPS031]

#8b9296

16

Brama garażowa segmentowa [BRAMA_GAR]

#3a3e42

OBJAŚNIENIA I UWAGI

1. Wymiary w cm (mm w indeksie górnym, np. 24" = 24,5 cm), rzędne w m względem ±0,000 = 101,650 m n.p.m. (PL-EVRF2007-NH).

2. Rzędne: trójką zaczerniony — poziom wykończenia, niezaczerzony — konsuracja, w pokwie zaczerniony — poziom ±0,000 z rzędną bezwzględna (PN-B-01025).

3. Wysokość budynku wg § 6 WT: H = 9,97 m od terenu przy najniższym położonym wejściu (-0,348) do wierzchu stropodachu D1 (+9,626) — H = 9,97 m (bez atyki).

4. Kolorystyka orientacyjna wg kolorów materiałów w modelu (do potwierdzenia wzornikiem RAL/NCs).

5. Rysunek wygenerowany automatycznie z modelu model/budynki.yam (wersja 1.0, 2026-09-25) — generatory lamele.views.

1 0 1 2 3 4 5 m

PODZIAŁKA 1:50

REW.	OPIS ZMIANY	DATA
0	Wydanie — rysunek wygenerowany z modelu	2026-09-25

PRACOWNIA PROJEKTOWA — nazwa do uzupełnienia

PB

ARCHITEKTURA (AR)

INWESTOR (do uzupełnienia)

ADRES / LOKALIZACJA (NR DZIAŁKI, OBREB, JEDN. EWIDENCYJNA)

ul. Lipowa (fikcyjna), dz. nr ewid. 123/4, obręb 0005 Przykładowo, gm. Przykładowo (fikcyjna)

KAT. OBIEKTU

I

FUNKCJA	IMIĘ I NAZWISKO	SPECJALNOŚĆ, NR UPRAWNIEN	DATA	PODPIS
Projektant	[DO UZUPEŁNIENIA]	[DO UZUPEŁNIENIA]		
Projektant (wsp.)	[DO UZUPEŁNIENIA]	[DO UZUPEŁNIENIA]		
Sprawdzający	nie dotyczy (art. 20 ust. 3 pkt 2 PB)	—		
Opracował	[DO UZUPEŁNIENIA]	[DO UZUPEŁNIENIA]		

TYTUŁ RYSUNKU

ELEVACJE

SKALA	FORMAT	DATA WYDANIA	RODZAJ DOK.	NR RYSUNKU	ARKUSZ	REW.
1:50	2050x297	2026-09-25	elewacja	PB-AR-05	5/5	0