



PRZEKRÓJ A-A 1:50

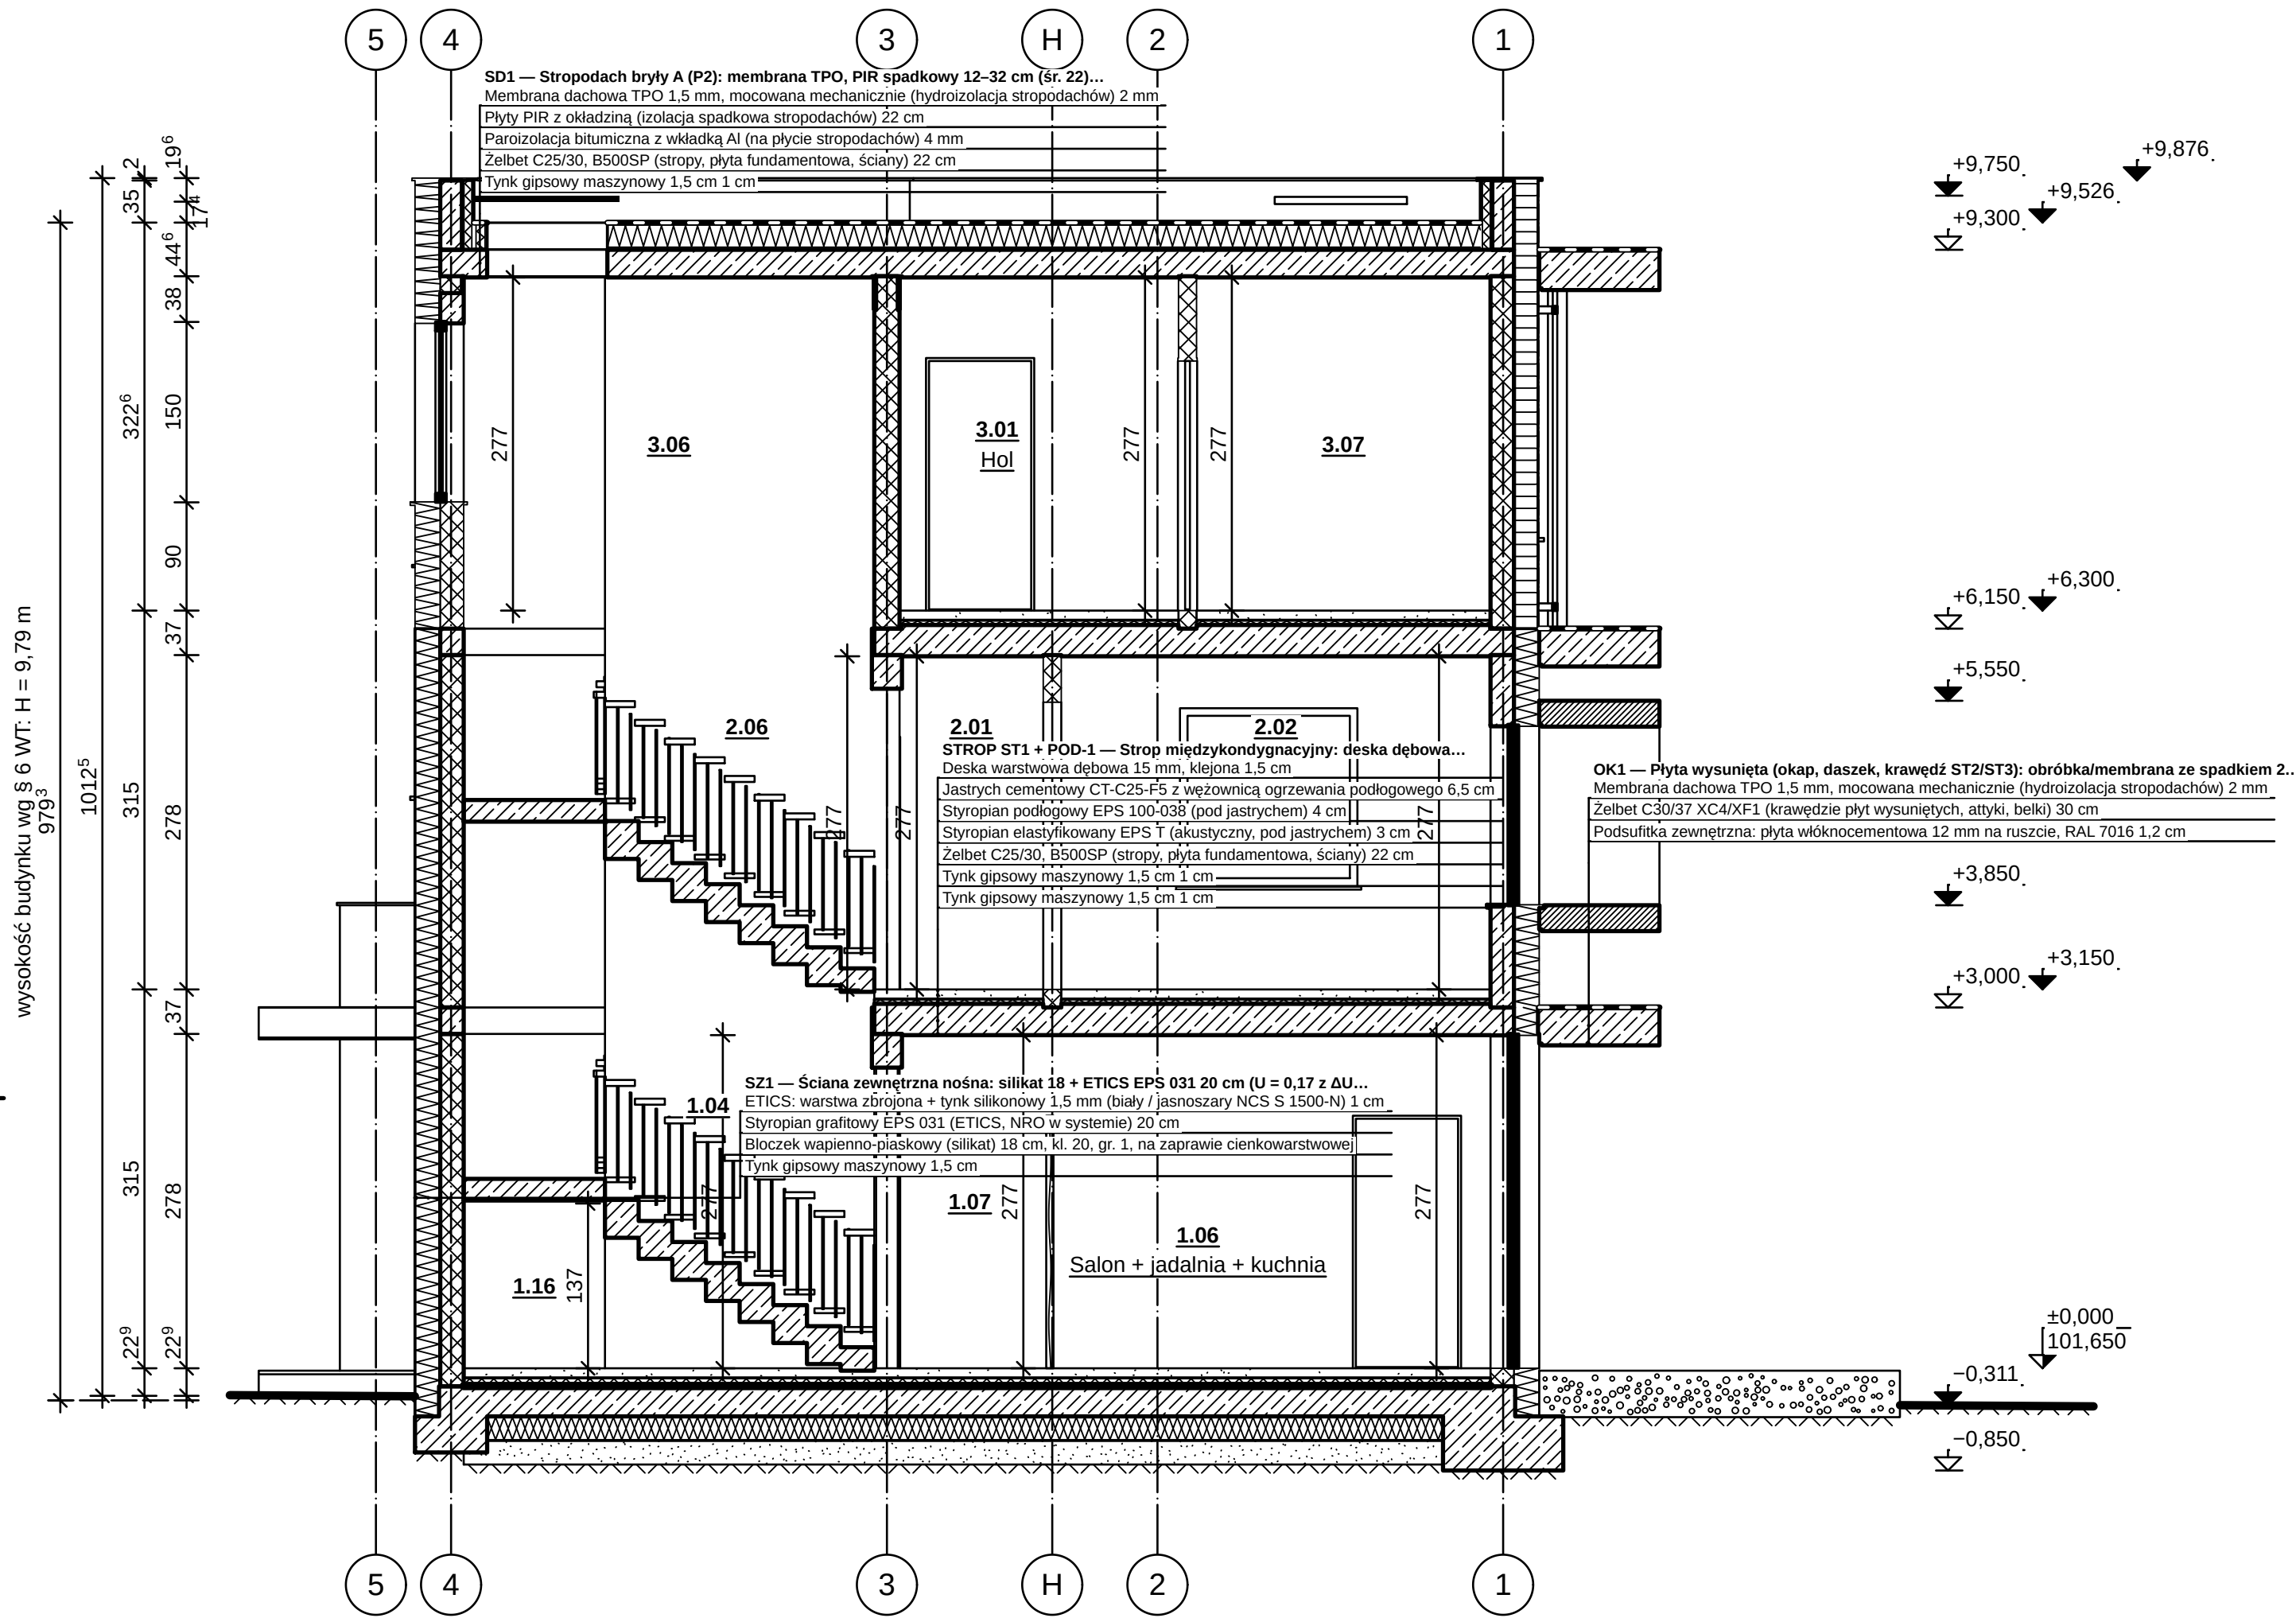

PRZEKRÓJ B-B 1:50

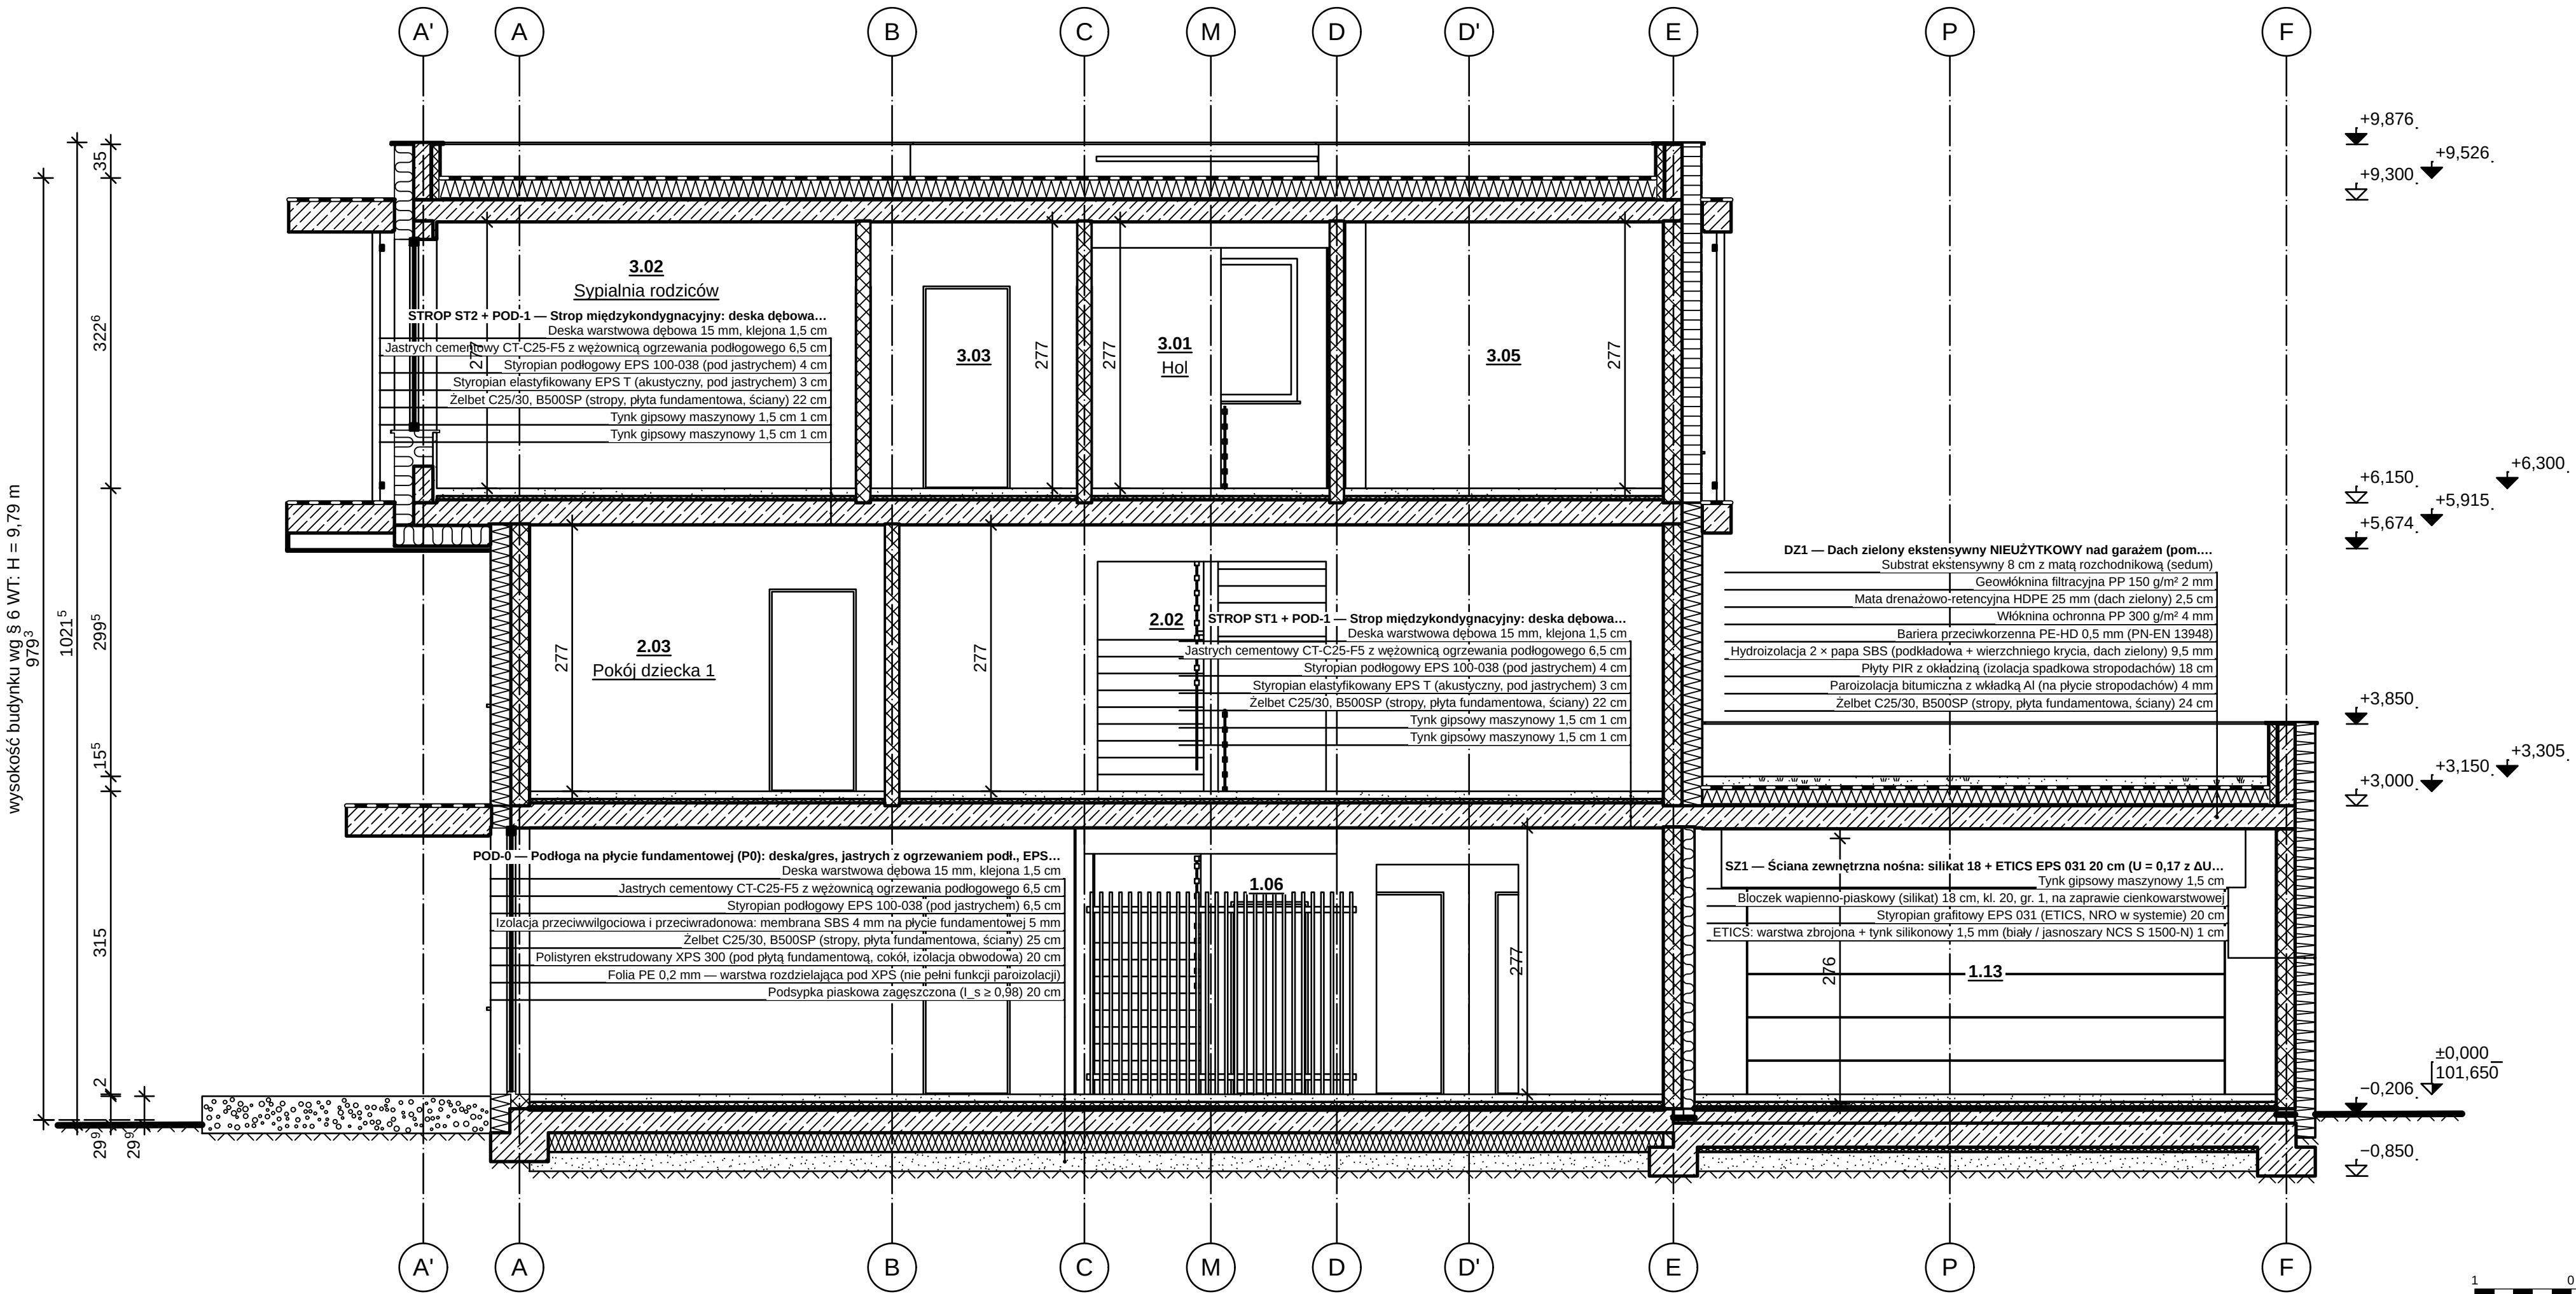


OBJAŚNIENIA I UWAGI

- Wymiary w cm (mm w indeksie górnym, np. 24" = 24,5 cm), rzędne w m względem ±0,000 = 101,650 m n.p.m. (PL-EVRF2007-NH).
- Rzędne: trójkąt zaczerpnięty — poziom wykończenia, niezaczerpnięty — konstrukcji, w polowie zaczerpnięty — poziom ±0,000 z rzędnej bezwzględnej (PN-B-01025).
- Wysokość budynku wg § 6 WT: od terenu przy najniższej podłożonej wejściu (-0,267) do wierzchu stropodachu D1 (+9,526) — H = 9,79 m (bez attyki).
- Opisy warstw: kod i nazwa przegrody z modelu, materiały i grubości wg modelu (od góry / od lewej).
- Opisy warstw pominięte na rysunku (brak miejsca w podziale 1:50): STROP ST2 + POD-1, SD1, OK1 — układ warstw wg zestawienia przegród w części opisowej / przekroju 1:50.
- Opisy warstw pominięte na rysunku (brak miejsca w podziale 1:50): STROP ST22 + POD-1, SD1, OK1 — układ warstw wg zestawienia przegród w części opisowej / przekroju 1:50.
- Rysunek wygenerowany automatycznie z modelu model/budynki.yamli (wersja 1.0, 2026-09-25) — generatory lamela.views.

OZNACZENIA MATERIAŁÓW (PN-B-01030 + przyjęte)

- Lamele dębowe 30×60 mm (ekran komunikacji P0, h 2,10 m; 0,02 m).
- Deska warstwowa dębowa 15 mm, klejona — przekrój wzdłuż włókien.
- grunt rodzimy
- Substrat ekstensywny 8 cm z małą rozchodnikową (sedum)
- Wełna mineralna fasadowa (elewacja wentylowana bryły A, A1); Wełna mineralna OSB (szkielet, docieplenia, ściana dom-garaż) — meander „UUU”
- Płyty PIR z okładziną (izolacja spadkowa stropodachów) — zygzak z okładzinami
- Izolacja przeciwwilgociowa i przeciwdrażna: membrana SBS 4 mm na płycie fundamentowej — linia bardzo gruba
- Membrana dachowa TPO 1,5 mm, mocowana mechanicznie (hydroizolacja stropodachów); Hydroizolacja 2 × papa SBS (podkładowa + wierzchniego krycia, dach zielony) — pas czarno-biały
- Syroplan gąflowy EPS 031 (ETICS, NRO w systemie); Syroplan podłogowy EPS 100-038 (pod jastrychem); Syroplan elastykowany EPS T (akustyczny, pod jastrychem) — zygzak „VVV”
- Polistyren ekstrudowany XPS 300 (pod płytą fundamentową, cokoł, izolacja obwodowa) — zygzak podwójny
- Jastrych cementowy CT-C25-F5 z wężownicą ogrzewania podłogowego — kropki
- Membrana fasadowa wiatroizolacyjna UV-stabilna, czarna (sd = 0,02 m)
- Błoczek wapienno-piaskowy 12 cm, kl. 15 (ścianki działowe, łocowy w klatce); Błoczek wapienno-piaskowy (silikat) 18 cm, kl. 20, gr. 1, na zaprawie cienkowarstwowej — kratka ukośna 45°/135°
- Paroizolacja bitumiczna z wkładką Al (na płycie stropodachów) — linia kreskowa cienka 3/1 po ciepłej stronie
- Podsyłka piaskowa zagęszczona (L s ≥ 0,98)
- Płyta gipsowo-kartonowa 12,5 mm (GKB / GKB1 w łazienkach); Syroplan podłogowy EPS 100-038 (pod jastrychem); RAL 7015 (pusta w środku); Słal malowana proszkowo (balustrady, rygle) — zaznaczenie
- Szkło (szyby zespolone); Ścianka szklana VSG 2 × 8 mm w ramie aluminiowej (wiatrąpek / hoi)
- Żelbet C25/30, B500SP (stropy, płyta fundamentowa, ściany); Żelbet C30/37 XC4/XF1 (krawędzie płyt wysuniętych, attyki, belki) — 45° na przemian ciągłe i przerywane
- Podbudowa nawierzchni (kruszywo)

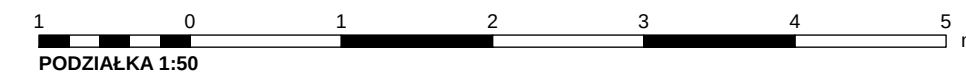

REW.	OPIS ZMIANY		DATA	
0	Wydanie — rysunek wygenerowany z modelu		2026-09-25	
PRACOWNIA PROJEKTOWA PRACOWNIA PROJEKTOWA — nazwa do uzupełnienia			STADIUM PB	BRANŻA ARCHITEKTURA (AR)
adres pracowni do uzupełnienia				
INWESTOR (do uzupełnienia)				
OBIEKT / NAZWA ZAMIERZENIA BUDOWLANEGO				
Budynek mieszkalny jednorodzinny wolnostojący „Dom LAMELA”				
Adres / LOKALIZACJA (NR DZIAŁKI, OBRĘB, JEDN. EWIDENCYJNA)				KAT. OBIEKTU
ul. Lipowa (fikcyjna), dz. nr ewid. 1234, obręb 0005 Przykładowo, gm. Przykładowo (fikcyjna)				I
FUNKCJA	IMIĘ I NAZWISKO	SPECJALNOŚĆ, NR UPRAWNIENI	DATA	PODPIS
Projektant				
Projektant (wsp.)				
Sprawdzający				
Opracował				
TYTUŁ RYSUNKU				
PRZEKROJE A-A I B-B				
SKALA 1:50	FORMAT 1130x420	DATA WYDANIA 2026-09-25	RODZAJ DOK. przekrój	NR RYSUNKU PB-AR-04
ARKUSZ 4/5	REW. 0			