




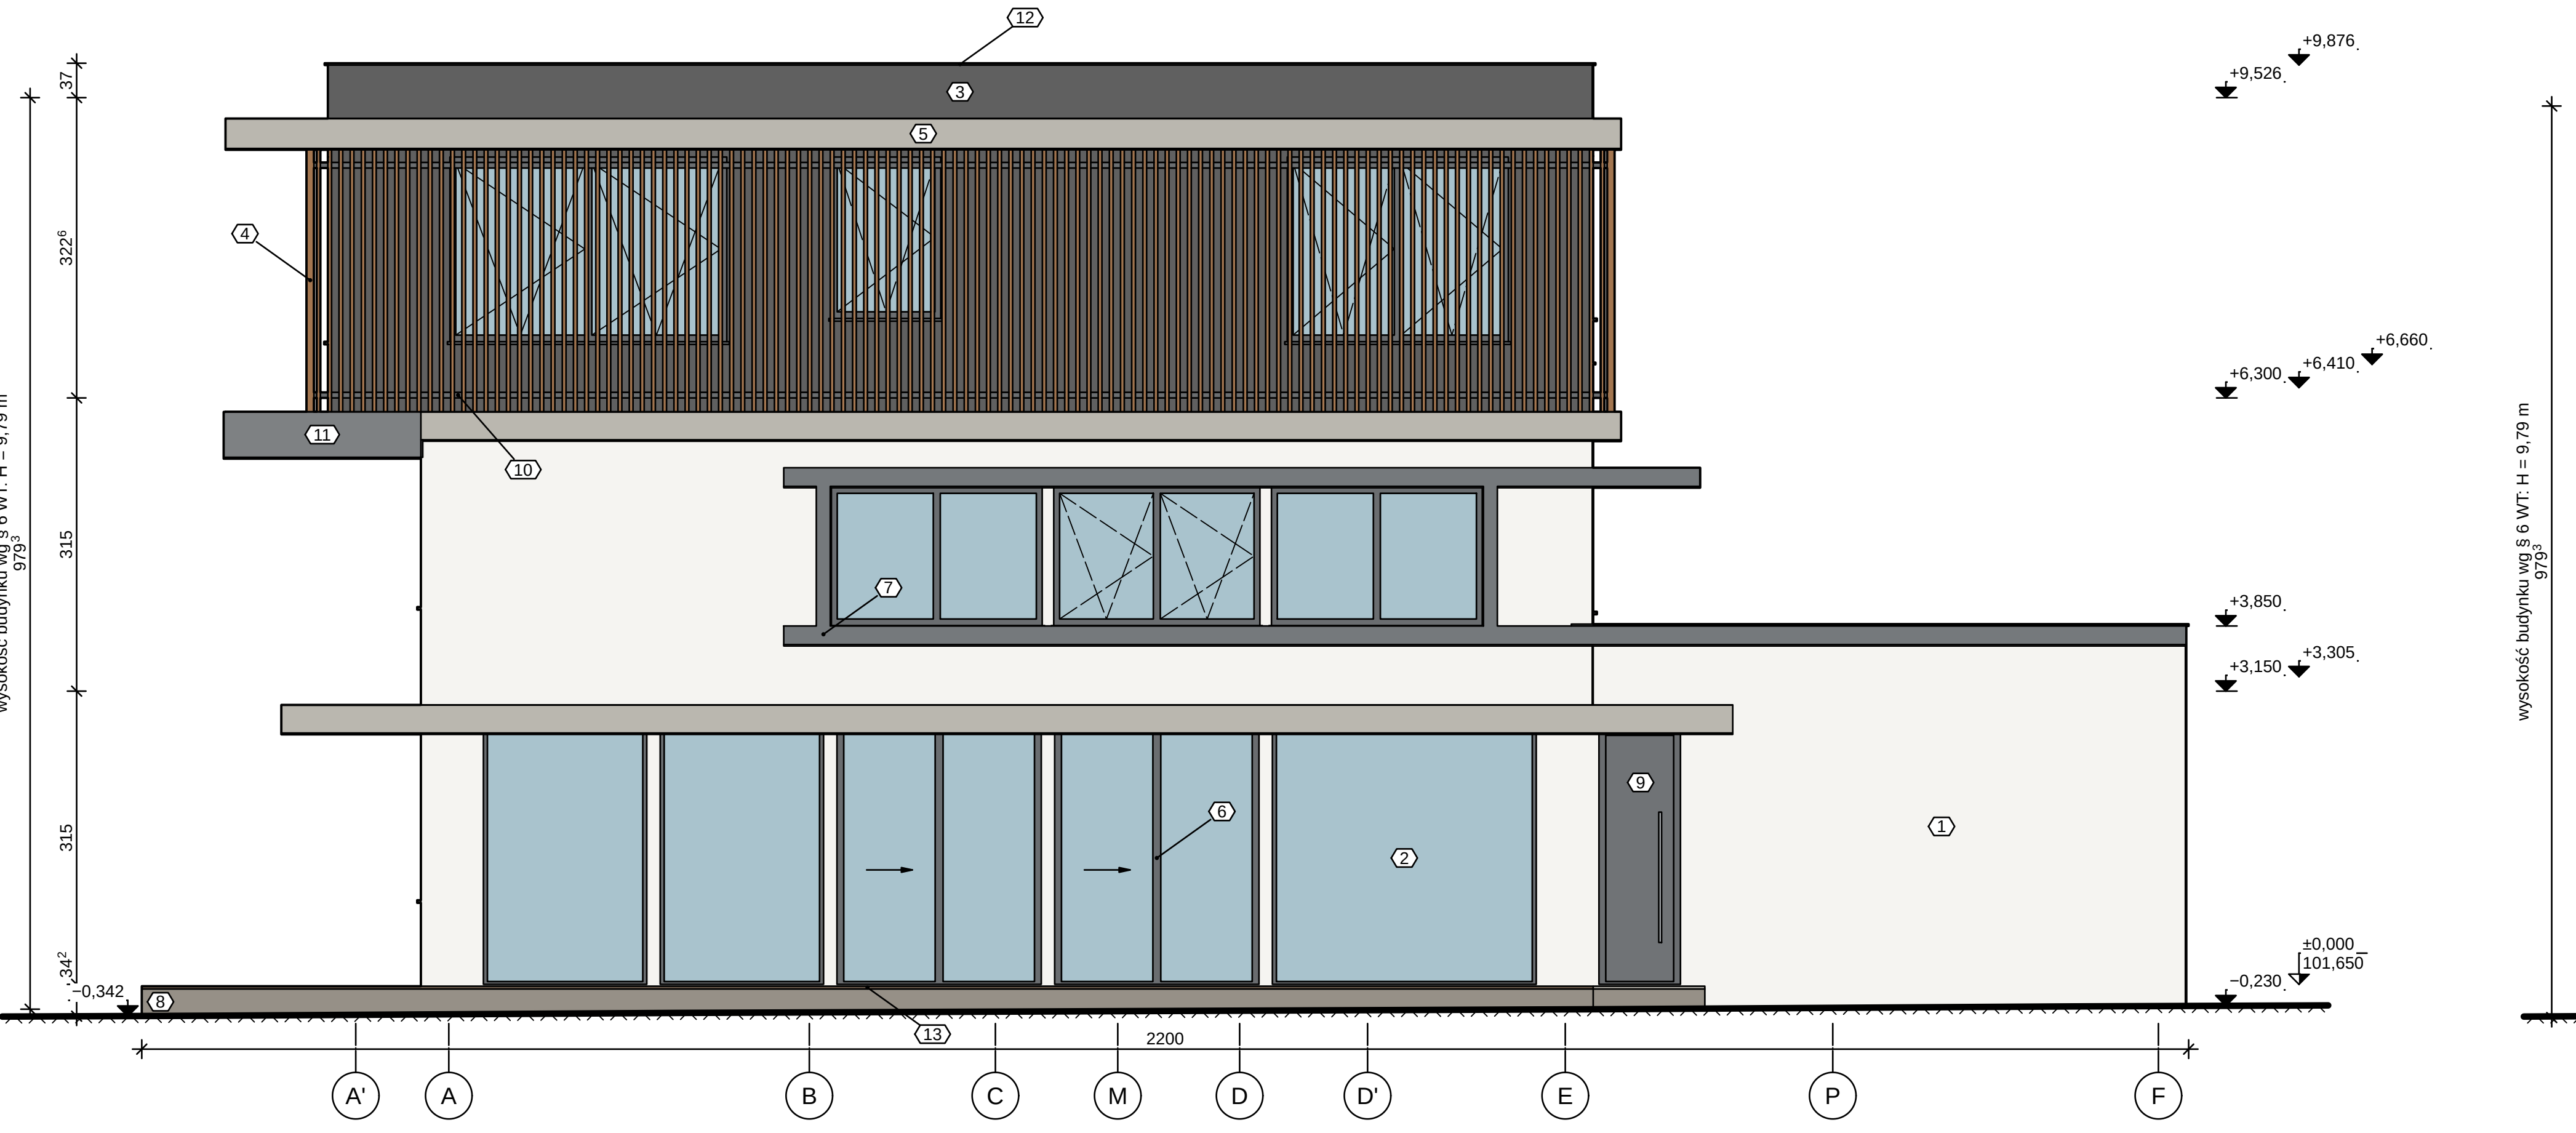


ELEWACJA POŁUDNIOWA (OGRODOWA) 1:50

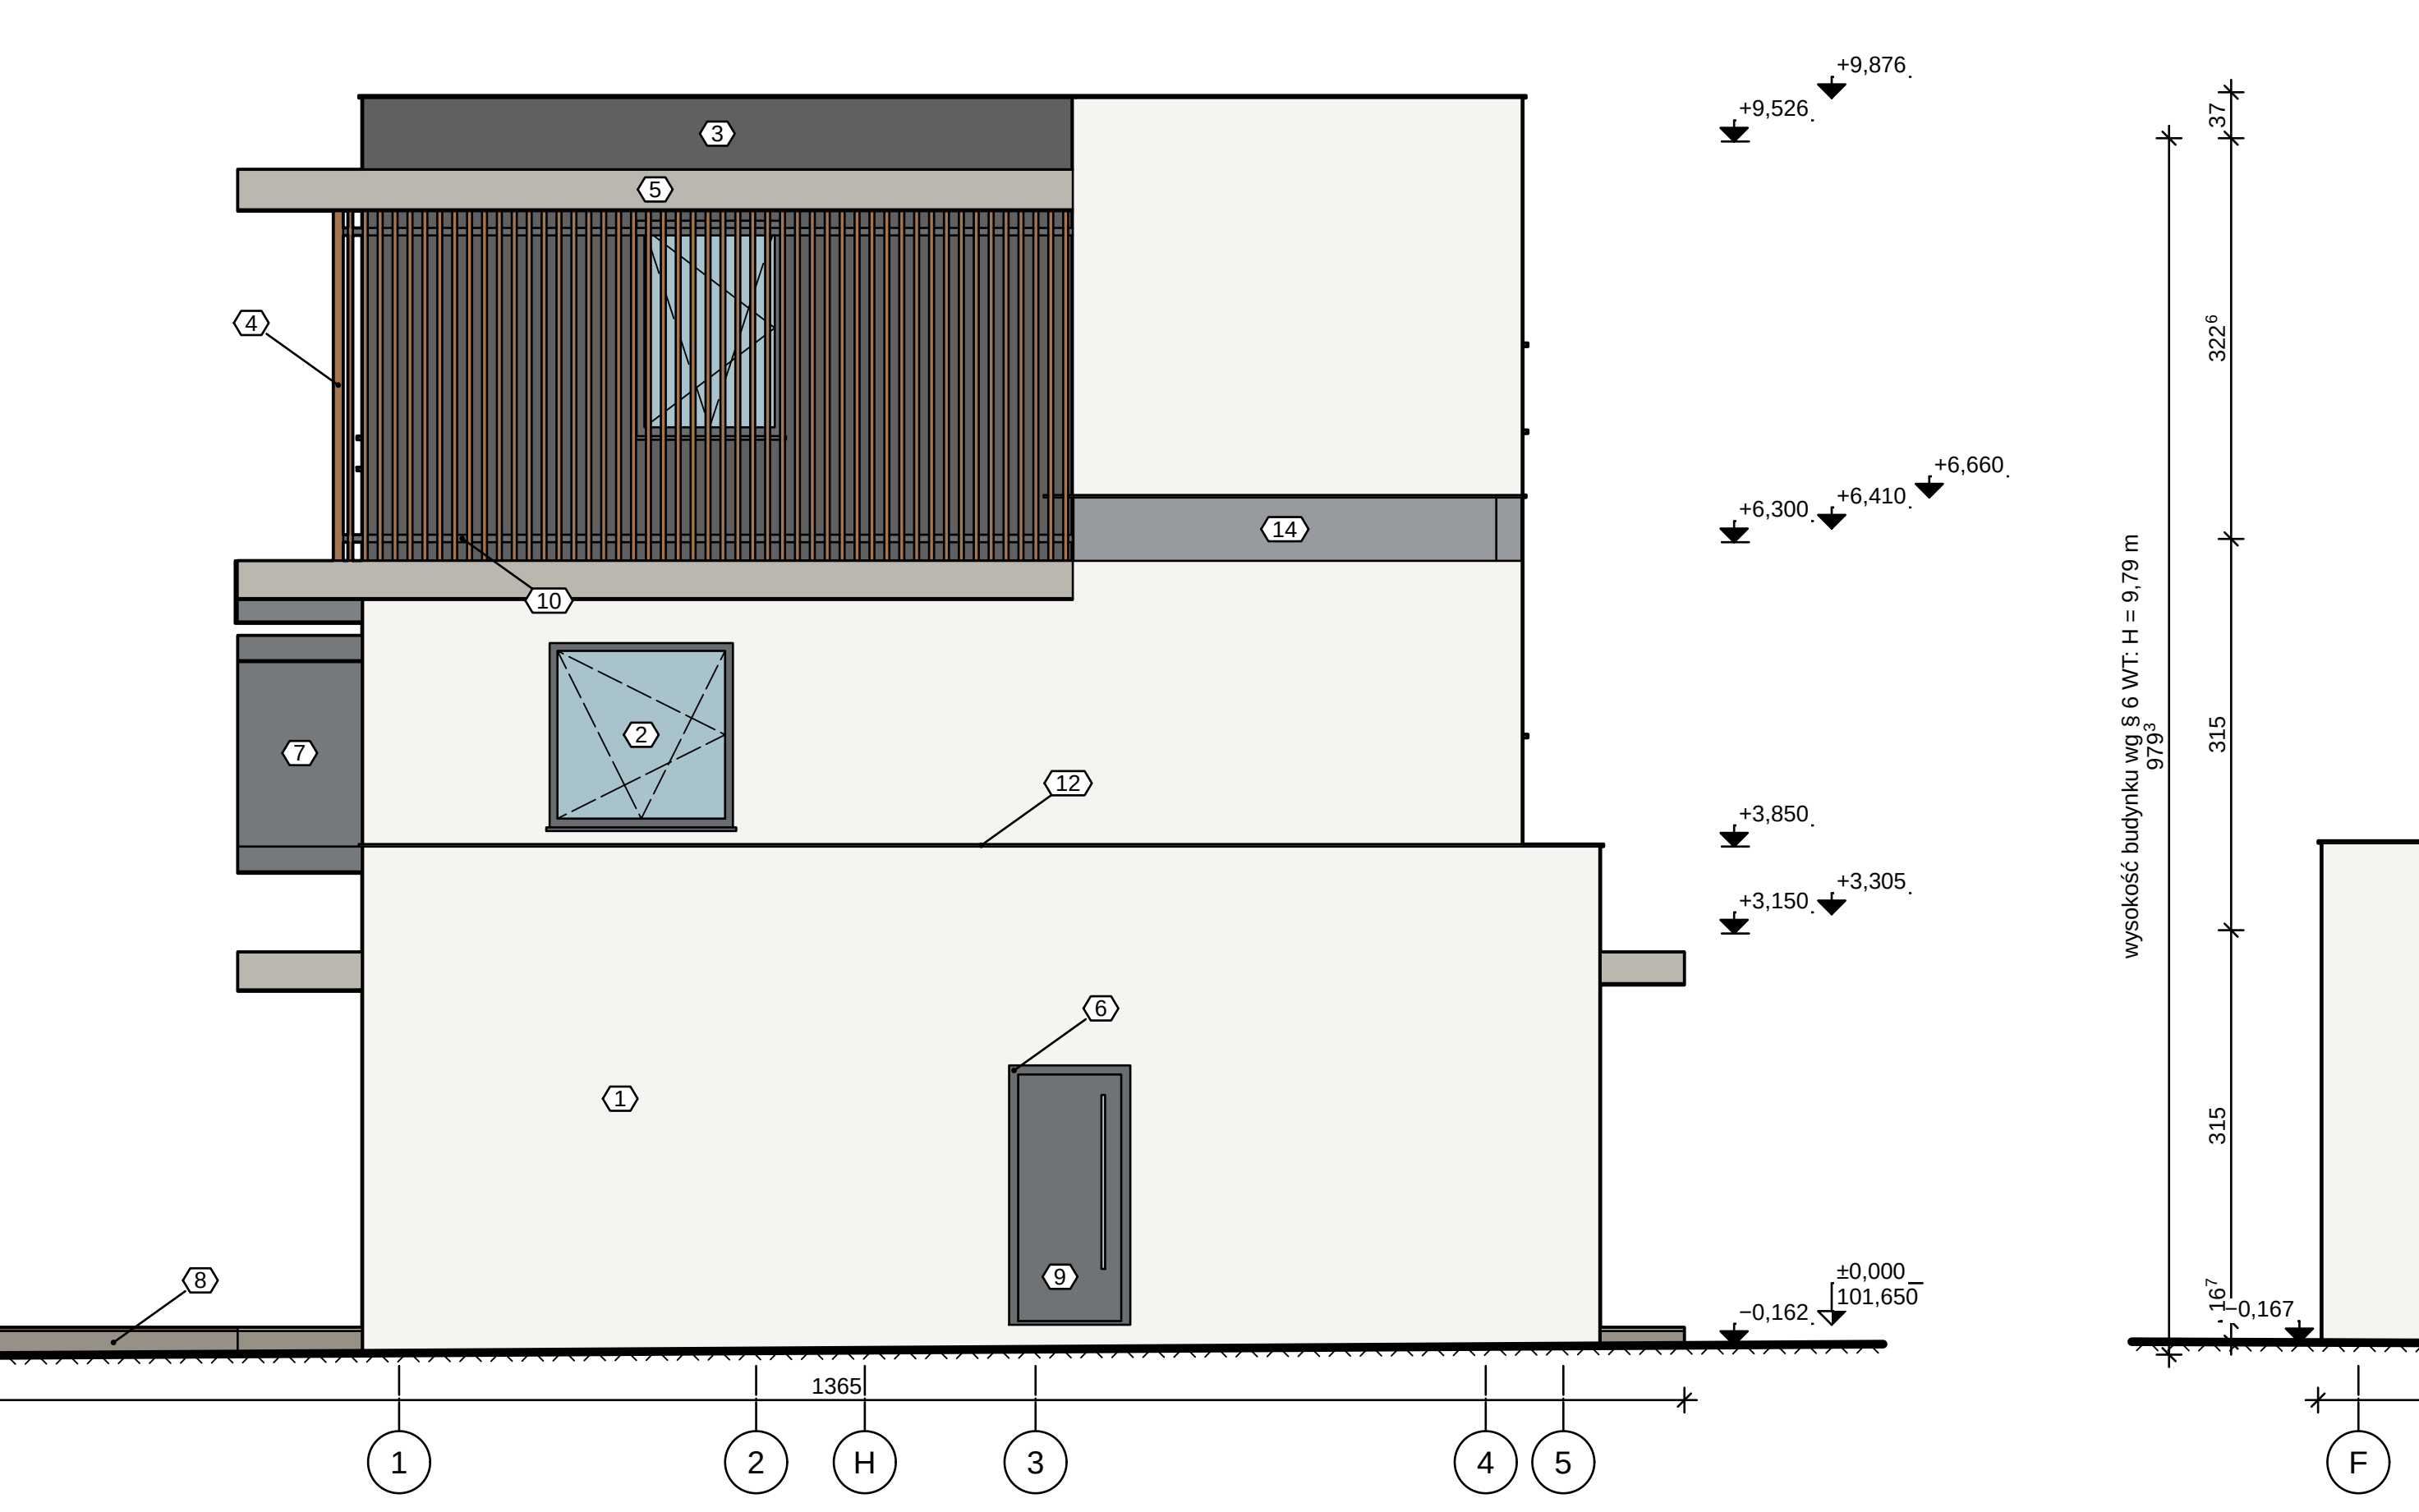

ELEWACJA WSCHODNIA 1:50

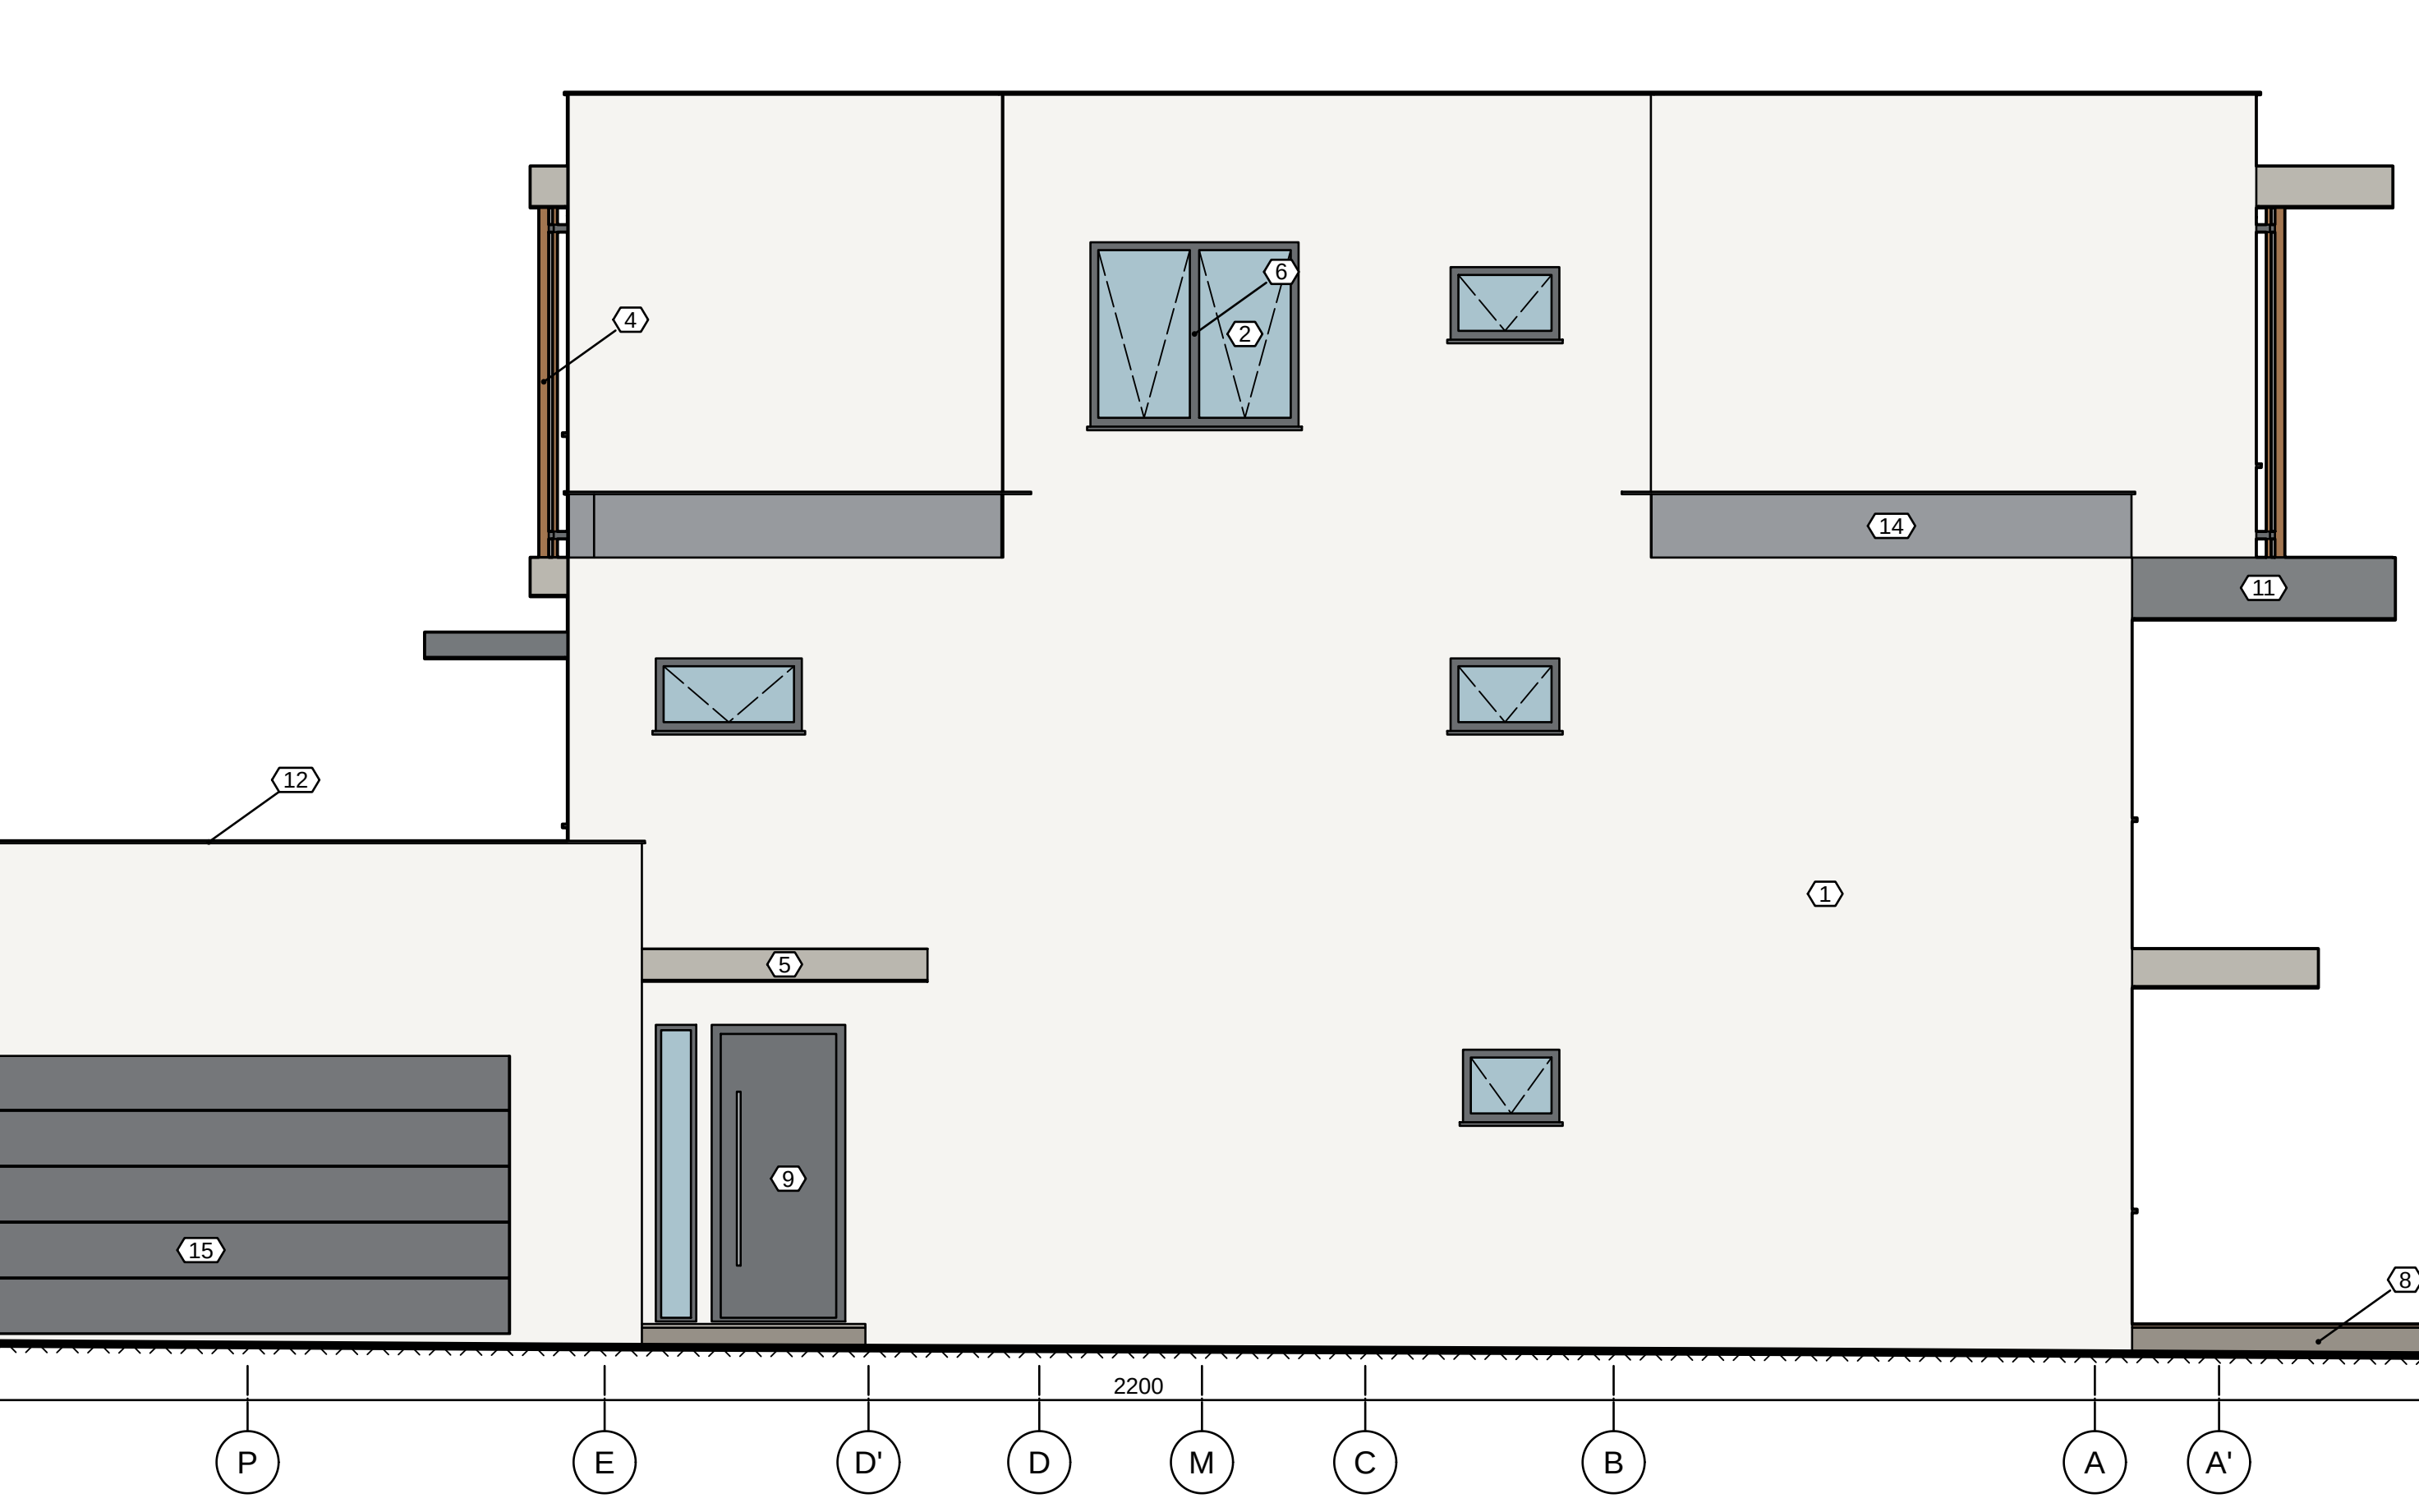

ELEWACJA PÓŁNOCNA (OD ULICY) 1:50

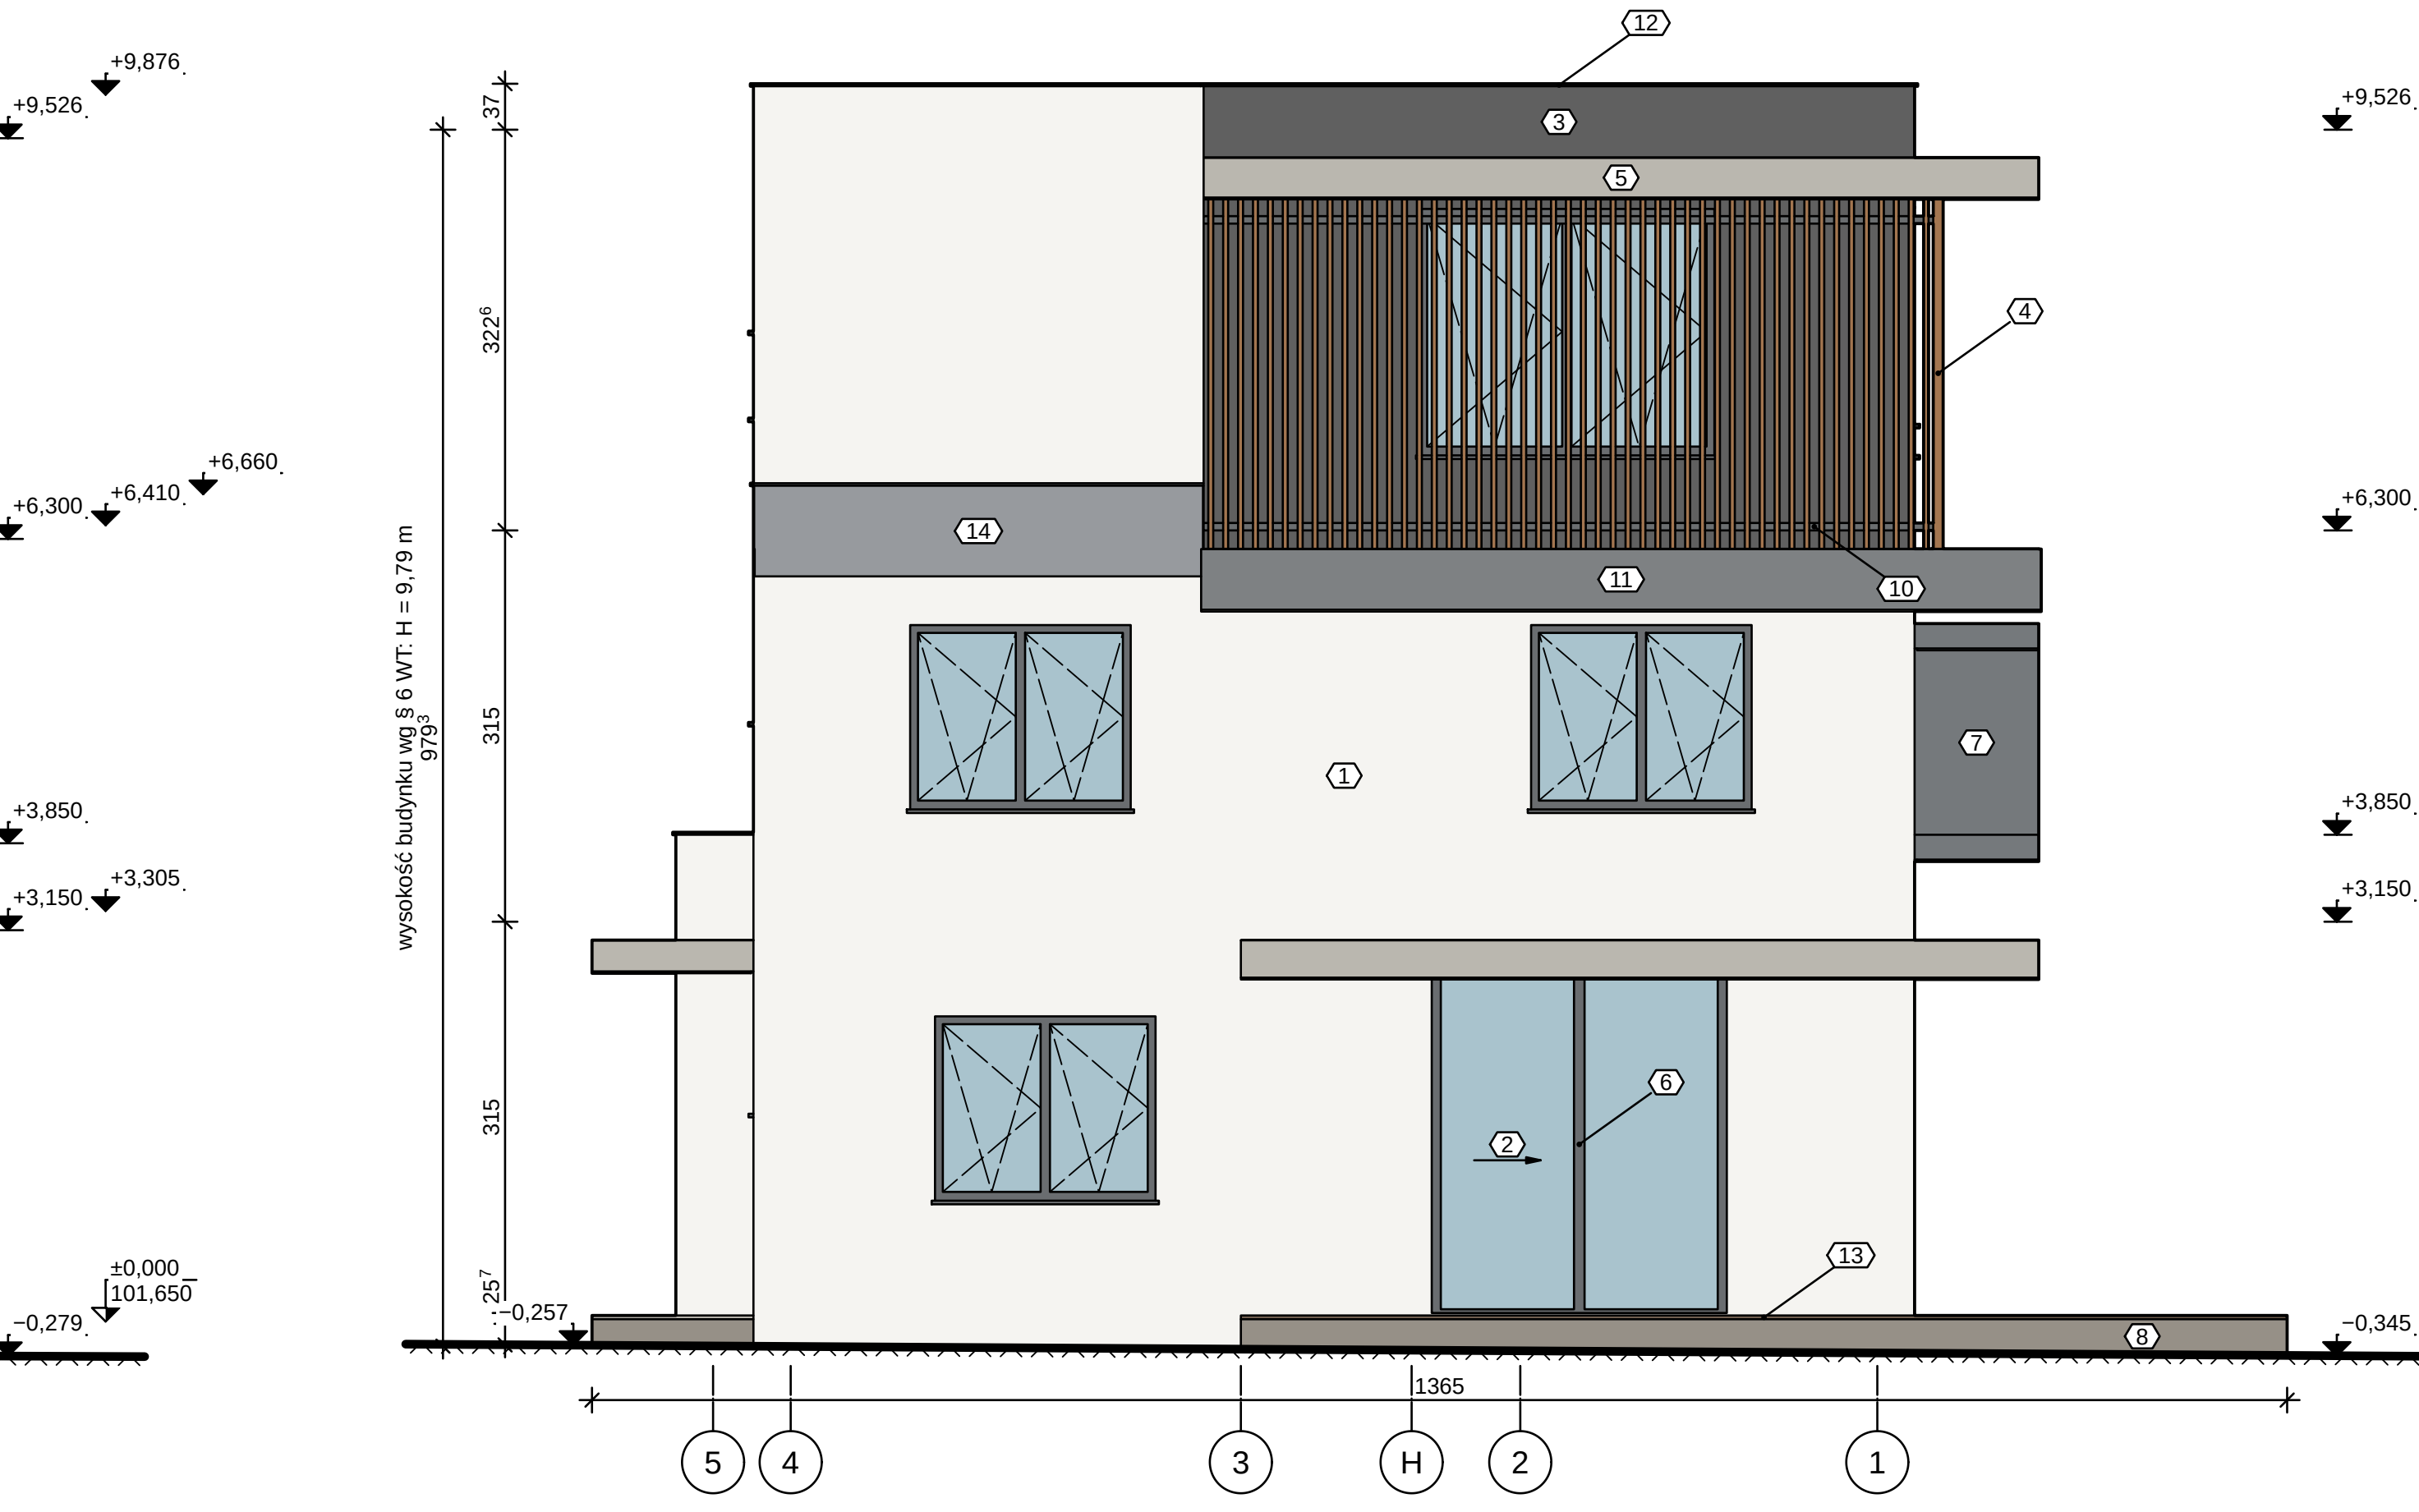

ELEWACJA ZACHODNIA 1:50

KOLORYSTYKA I MATERIAŁY ELEWACJI

1

ETICS: warstwa zbrojona + tynk silikonowy 1,5 mm (biały) / jasnoszary NCS S 1500-N [TYNK_SIL]

#f5f4f0

2

Szkoło (szyby zespolone) [SZKŁO]

#a9c3cd

3

Membrana fasadowa wiatrozłaczająca UV-stabilna, czarna (sd = 0,02 m) [MEMB_WIATR]

#1d1d1d

4

Lamele elewacyjne 40x80 mm, drewno termoofer (klasa 1 trwałości), olejowane [DREWNO_TERMO]

#6b6b41

5

Żelbet C30/37 XC4XF1 (krawędzie płyt wysuniętych, atyki, belki) [ZB_C30]

#b4b1a9

6

Stołarka — profile aluminiowe, antracyt [RAMA_ALU]

#2b2b33

7

Rama boku C: ruszt stalowy ocynkowany w okładzinie z blachy aluminiowej RAL 7016 (pusta w środku) [RAMA_C]

#3b4044

8

Podbudowa nawierzchni (kuszyno) [NAW_PODBUDOWA]

#34383c

9

Drzwi zewnętrzne, płytina aluminiowa [DRZWI_ZEWNI]

#8d877d

10

Stal malowana proszkowo (balustrady, rygle) [STAL_BAL]

#2c3034

11

Podsiufka zewnętrzna: płyta włóknocementowa 12 mm na ruszcie, RAL 7016 [PODSUF]

#47474f

12

Obróbki blacharskie (blacha powlekana) [OBRÓBKA_BLACH]

#3b3b43

13

Deska tarasowa [NAW_DESKA]

#6d5847

14

Styropian grafitowy EPS 031 (ETICS, NRO w systemie) [EPS031]

#8f9286

15

Brama garażowa segmentowa [BRAMA_GAR]

#3a3a42

OBJAŚNIENIA I UWAGI

1. Wymiary w cm (mm w indeksie górnym, np. 24^h = 24,5 cm), rzędne w m względem ±0,000 = 101,650 m n.p.m. (PL-EVRF2007-NH).

2. Rzędne: rękót zaczerniony — poziom wykończenia, niezaczerniony — konstrukcji, w połowie zaczerniony — poziom ±0,000 z rzędną bezwzględną (PN-8-01029).

3. Wysokość budynku wg § 6 WT: H = 9,79 m od wierzchu stropodachu D1 (+9,526) — H = 9,79 m (bez atyki).

4. Kolorystyka orientacyjna wg kolorów materiałów w modelu (do potwierdzenia wzorkiem RAL/NCS).

5. Rysunek wygenerowany automatycznie z modelu model/budynki/ym (wersja 1.0, 2026-09-25) — generatory lamela.views.

1 0 1 2 3 4 5 m

PODZIAŁKA 1:50

REW.	OPIS ZMIANY	DATA
0	Wydanie — rysunek wygenerowany z modelu	2026-09-25
PRACOWNIA PROJEKTOWA — nazwa do uzupełnienia		PB
adres pracowni do uzupełnienia		ARCHITEKTURA (AR)
INWESTOR (do uzupełnienia)		
OBIEKT / NAZWA ZAMIERZENIA BUDOWLANEGO		
Budynek mieszkalny jednorodzinny wolnostojący „Dom LAMELA”		
ADRES / LOKALIZACJA (NR DZIAŁKI, OBRĘB. JEDN. EWIDENCYJNA)		KAT. OBIEKTU
ul. Lipowa (fikcyjna), dz. nr ewid. 123/4, obręb 0005 Przykładowo, gm. Przykładowo (fikcyjna)		I
FUNKCJA	IMIĘ I NAZWISKO	SPECJALNOŚĆ, NR UPRAWNIEN
Projektant		DATA
Projektant (wsp.)		PODPIS
Sprawdzający		
Opracował		
TYTUŁ RYSUNKU		
ELEWACJE		
SKALA	FORMAT	DATA WYDANIA
1:50	2050x297	2026-09-25
RODZAJ DOK.	NR RYSUNKU	ARKUSZ
elewacja	PB-AR-05	5/5
REW.	0	

1 2 3 4 5 6 7 8 9 10 11 12 13 14 15 16 17 18 19 20 21 22 23 24 25 26 27 28 29 30 31 32 33 34 35 36 37 38 39 40

1 2 3 4 5 6 7 8 9 10 11 12 13 14 15 16 17 18 19 20 21 22 23 24 25 26 27 28 29 30 31 32 33 34 35 36 37 38 39 40

1 2 3 4 5 6 7 8 9 10 11 12 13 14 15 16 17 18 19 20 21 22 23 24 25 26 27 28 29 30 31 32 33 34 35 36 37 38 39 40

1 2 3 4 5 6 7 8 9 10 11 12 13 14 15 16 17 18 19 20 21 22 23 24 25 26 27 28 29 30 31 32 33 34 35 36 37 38 39 40