

A

B


C

D


E

F

odcinek kontroly 100 mm (wydruk 1:1)

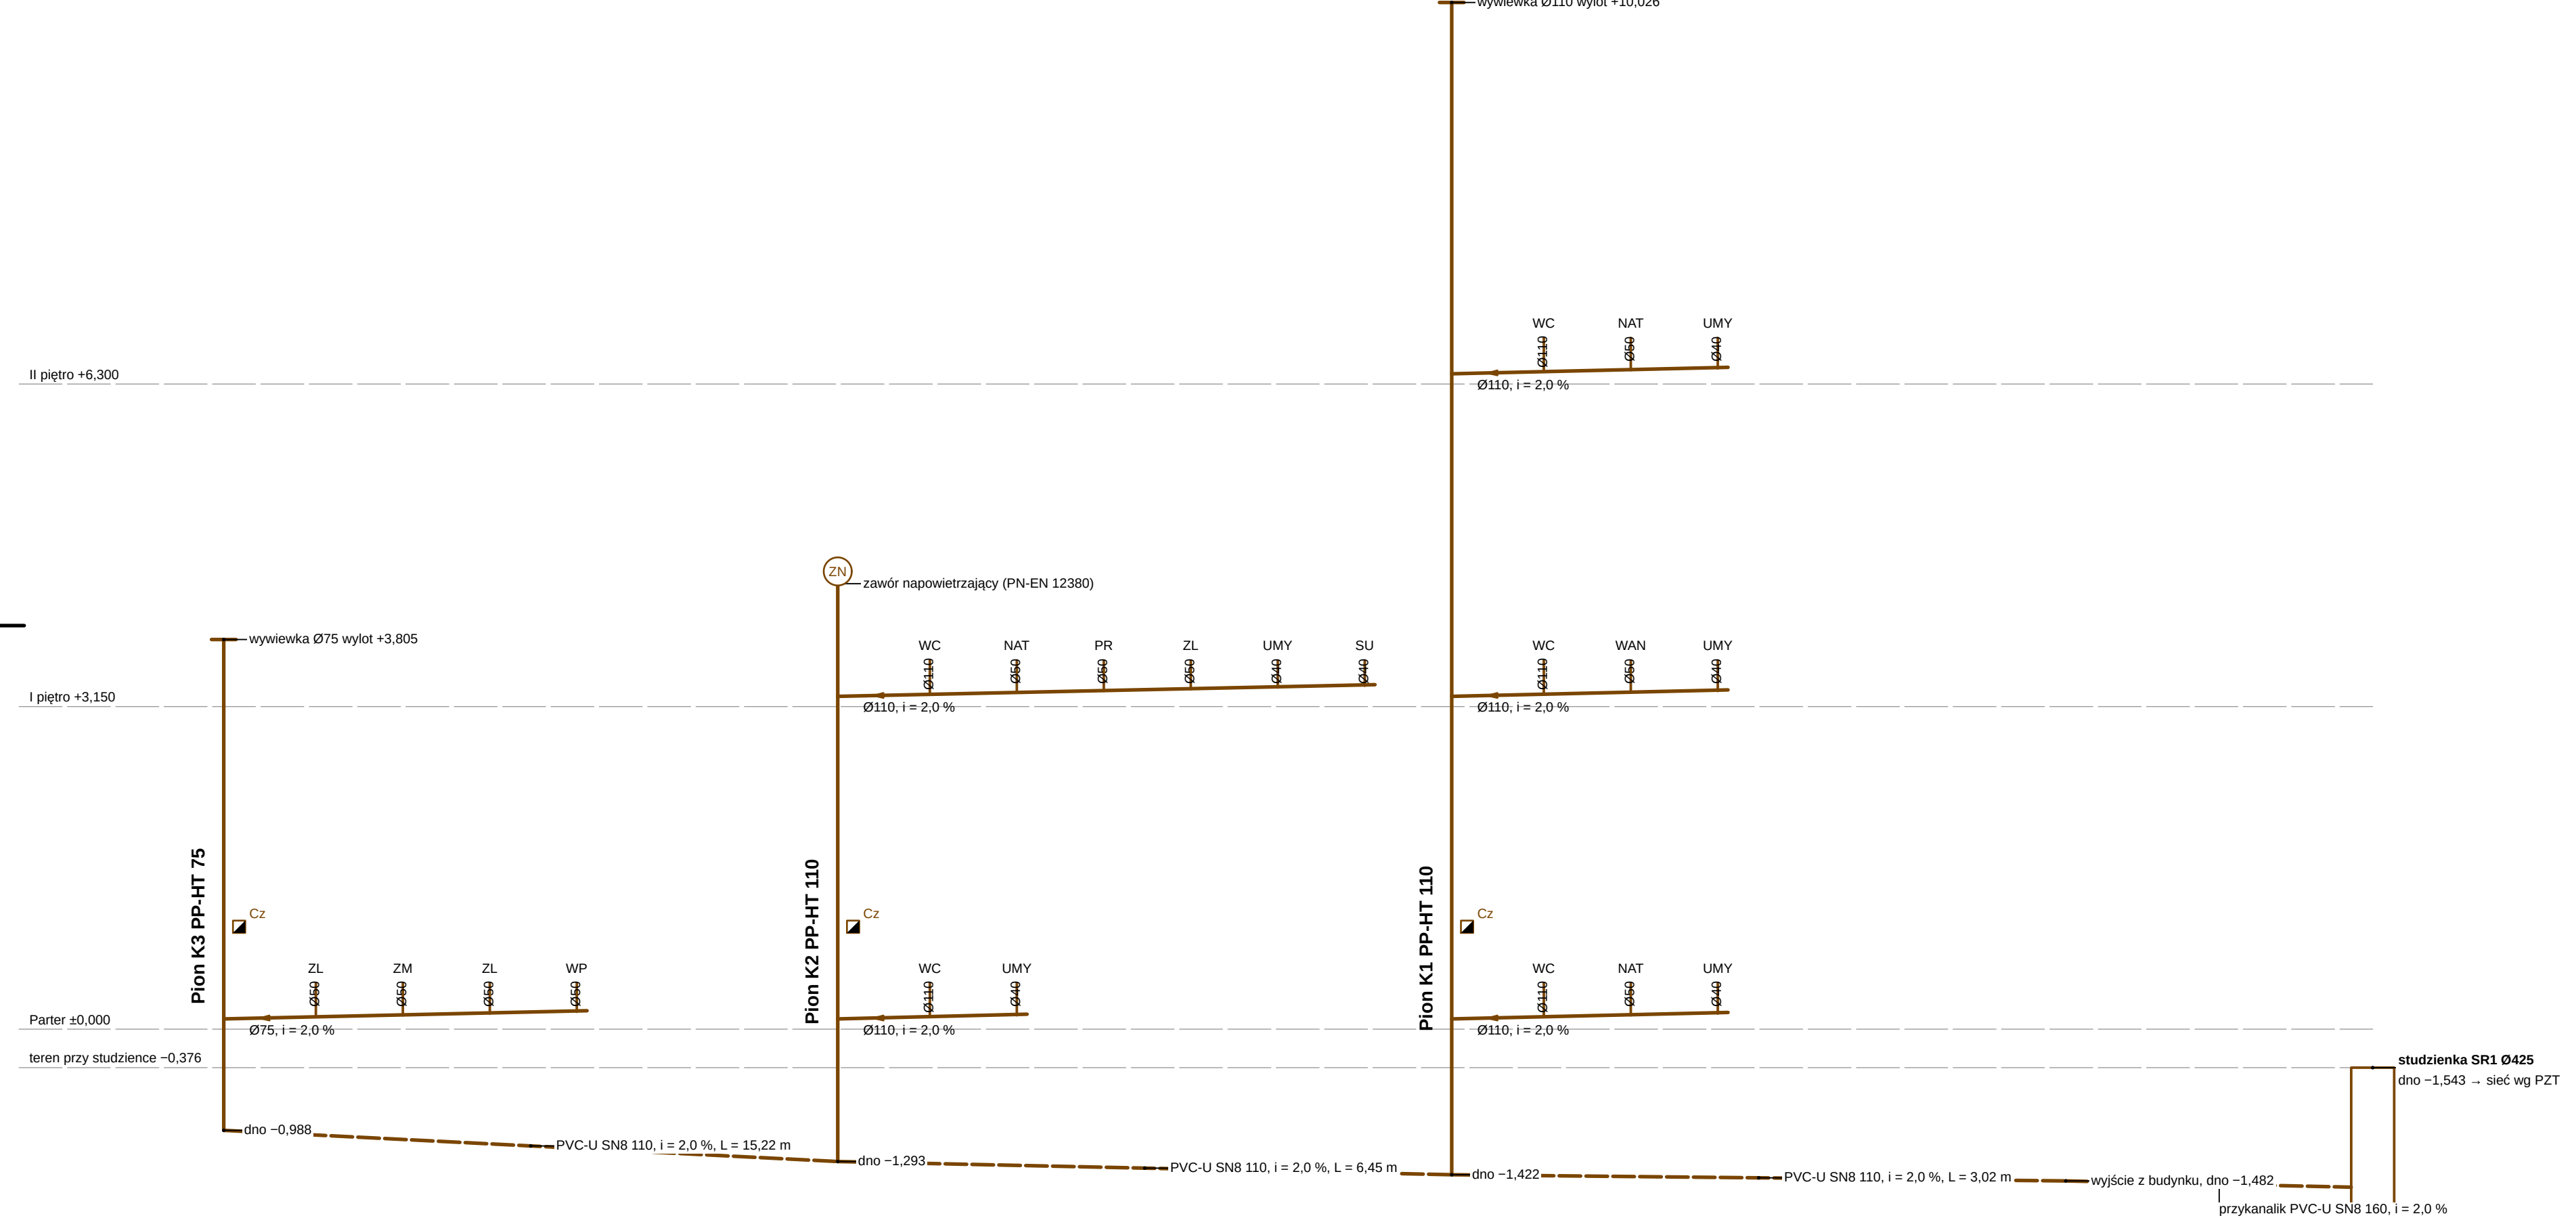

ROZWINIĘCIE KANALIZACJI SANITARNEJ (PIONY)

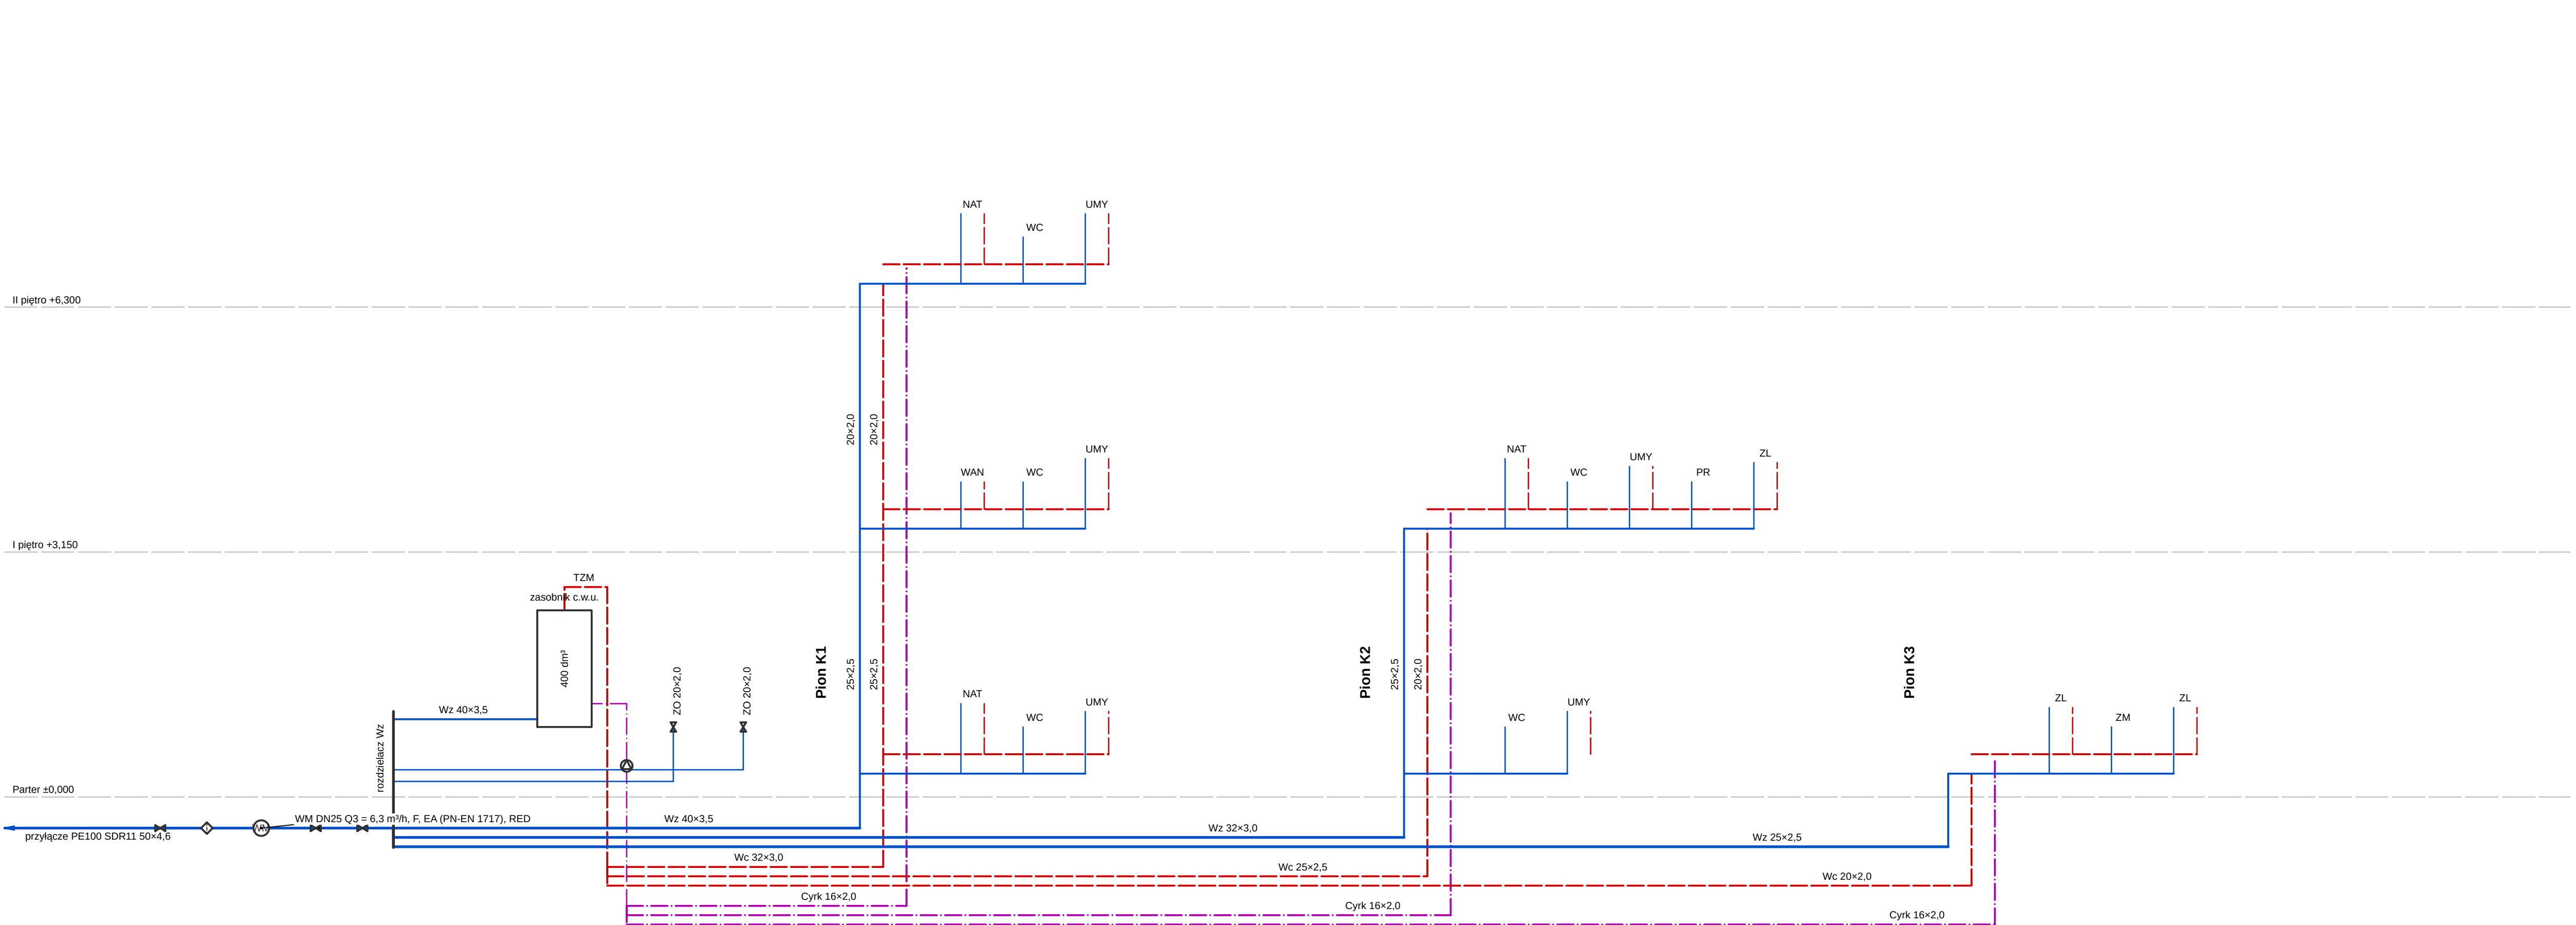

ROZWINIĘCIE INSTALACJI WODOCIĄGOWEJ

OZNACZENIA — LEGENDA SYMBOLI

- Ks — pion / podejście PP-HT (PN-EN 1451-1)
- przewód pod płytą / przykanalik PVC-U SN8 (PN-EN 1401-1)
- czyszczak na pionie (1,0 m nad posadzką)
- zawór napowietrzający pionu
- Wz — woda zimna
- Wc — ciepła woda użytkowa
- Cyrk — cyrkulacja c.w.u.
- wodomierz; F — filtr; EA — zawór antyskażeniowy (zwrtny); zawory odcinające

PIONY I PRZEWODY ODPŁYWOWE (obliczenia PN-EN 12056-2)

Odcinek	Rodzaj	DN	ZDU	Q [l/s]	L [m]
PION_K1	pion	Ø110	9,5	2,00	7,90
PION_K2	pion	Ø110	7,9	2,00	4,75
PION_K3	pion	Ø75	3,2	0,89	1,60
KOL1	poziom	Ø110	3,2	0,89	15,22
KOL2	poziom	Ø110	11,1	2,00	6,45
KOL3	poziom	Ø110	20,6	2,27	3,02
PRZ	przykanalik	Ø160	20,6	2,27	3,05

OBJAŚNIENIA I UWAGI

- Schemat bez skali: rzędne w m względem ±0,000 (posadzka parteru), średnice w mm.
- Rysunki instalacji na podkładzie rzutów architektury (PB-AR); podkład — linie cienkie szare (warstwy i-PODKŁAD*).
- Rozwinięcie kanalizacji: os pionowa w skali rzędnych (1:50), os pozioma umowna. Podejścia pokazano schematycznie (kolejność przyborów wg średnic), rzędne dna przewodów pod płytą z obliczeń (lamela.obliczenia.sanitarne.kanalizacja).
- Wentylacja pionów: K1 — wywiewka ponad dach; K2 — zawór napowietrzający PN-EN 12380 (dozwolony); K3 — wywiewka ponad dach.
- Rozwinięcie instalacji wodociągowej: os pionowa w skali rzędnych, os pozioma umowna; wysokości wypływów wg PN-92/B-01706 (praktyka projektowa). Średnice z obliczeń (lamela.obliczenia.sanitarne.woda); punkt krytyczny PRY18 (c.w.u.), p. wym = 325 kPa.
- Oznaczenia przyborów: WC — miska ustępowa, UMY — umywalka, NAT — natrysk, WAN — wanna, ZL — zlewomyywak, ZLG — zlew gospodarczy, ZM — zmywarka, PR — pralka, ZO — zawór ogrodowy.
- Rysunek wygenerowany automatycznie z modelu modelibudynek.yamli (wersja 1.0, 2026-09-25) — generatory lamela.views.

REW.		OPIS ZMIANY			DATA	
0		Wydanie — rysunek wygenerowany z modelu			2026-09-25	
PRACOWNIA PROJEKTOWA PRACOWNIA PROJEKTOWA — nazwa do uzupełnienia adres pracowni do uzupełnienia				STADIUM PT	BRANŻA INSTALACJE SANITARNE (IS)	
INWESTOR (do uzupełnienia)						
OBIEKT / NAZWA ZAMIERZENIA BUDOWLANEGO						
Budynek mieszkalny jednorodzinny wolnostojący „Dom LAMELA”						
ADRES / LOKALIZACJA (NR DZIAŁKI, OBRĘB, JEDN. EWIDENCYJNA)					KAT. OBIEKTU	
ul. Lipowa (fikcyjna), dz. nr ewid. 123/4, obręb 0005 Przykładowo, gm. Przykładowo (fikcyjna)					I	
FUNKCJA		IMIĘ I NAZWISKO		SPECJALNOŚĆ, NR UPRAWNIEŃ	DATA	PODPIS
Projektant		[DO UZUPEŁNIENIA]		[DO UZUPEŁNIENIA]		
Projektant (wsp.)		[DO UZUPEŁNIENIA]		[DO UZUPEŁNIENIA]		
Sprawdzający		nie dotyczy (art. 20 ust. 3 pkt 2 PB)		—		
Opracował		[DO UZUPEŁNIENIA]		[DO UZUPEŁNIENIA]		
TYTUŁ RYSUNKU						
KANALIZACJA I WODOCIĄG — ROZWINIĘCIA						
SKALA	FORMAT	DATA WYDANIA	RODZAJ DOK.	NR RYSUNKU	ARKUSZ	REW.
—	1410×297	2026-09-25	schemat instalacji	PT-IS-10	10/11	0