


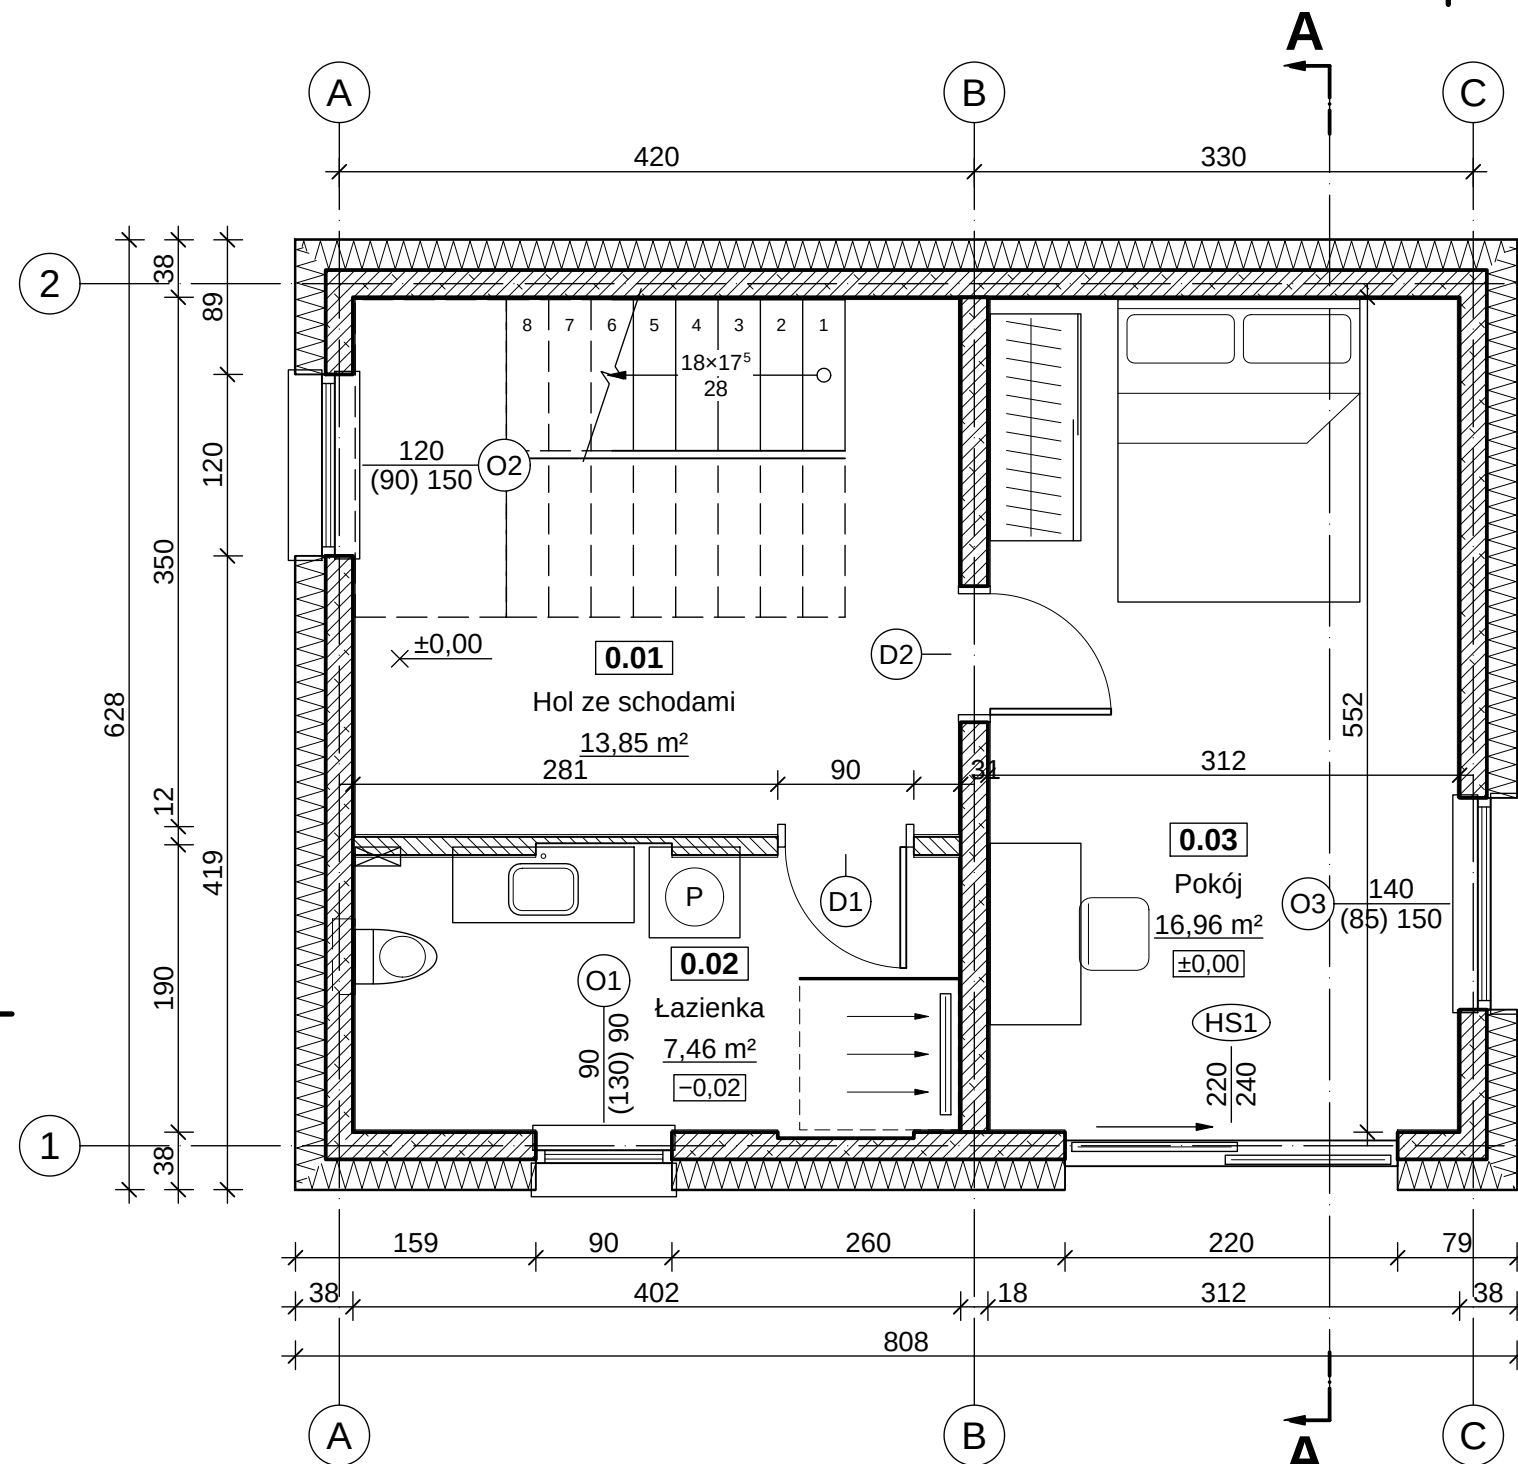

RZUT PARTERU — FRAGMENT 1:50

ZESTAWIENIE POMIESZCZEŃ

Nr	Nazwa pomieszczenia	Posadzka	Pow. [m²]
0.01	Hol ze schodami	gres	13,85
0.02	Łazienka	gres	7,46
0.03	Pokój	deska	16,96
RAZEM			38,27

ZESTAWIENIE OTWORÓW (w świetle muru)


Symbol	Szer. [cm]	Wys. [cm]	Parapet [cm]
O1	90	90	130
HS1	220	240	0
O2	120	150	90
O3	140	150	85
D1	90	205	—
D2	90	205	—

OZNACZENIA MATERIAŁÓW

	Mur z bloczków wapienno-piaskowych (silikatowych)		Izolacja termiczna twarda (EPS) — zygzak
	Mur z cegieł i pustaków ceramicznych		Tynk, zaprawa

UWAGI

- Wymiary w cm (mm w indeksie górnym), rzędne w m. Rzędna $\pm 0,00$ = posadzka parteru = 101,65 m n.p.m.
- Wymiary otworów w świetle muru: licznik — szerokość, mianownik — wysokość, w nawiasie wysokość parapetu.
- Rysunek testowy silnika — dane nie stanowią projektu.

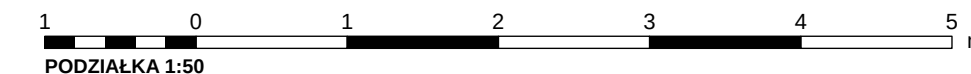

REW.	OPIS ZMIANY	DATA
0	Wydanie do weryfikacji silnika rysunkowego	2026-09-25
PRACOWNIA PROJEKTOWA	STADIUM	BRANŻA
PRACOWNIA PROJEKTOWA — nazwa do uzupełnienia	PB	ARCHITEKTURA
adres pracowni do uzupełnienia		
INWESTOR		
(do uzupełnienia)		
OBIEKT / NAZWA ZAMIERZENIA BUDOWLANEGO		
Budynek mieszkalny jednorodzinny „Dom LAMELA” — PRÓBA SILNIKA RYSUNKOWEGO (rysunek testowy)		
ADRES / LOKALIZACJA (NR DZIAŁKI, OBRĘB, JEDN. EWIDENCYJNA)		KAT. OBIEKTU
dz. nr ewid. 123/4, obręb 0005 Przykładowo, jedn. ewid. Przykładowo (dane fikcyjne)		I
FUNKCJA	IMIĘ I NAZWISKO	SPECJALNOŚĆ, NR UPRAWNIEN
		DATA
Projektant		PODPIS
Projektant (wsp.)		
Sprawdzający		
Opracował		
TYTUŁ RYSUNKU		
RZUT PRÓBNY — FRAGMENT PARTERU		
SKALA	FORMAT	DATA
1:50	A3	09.2026
	NR RYSUNKU	DEM0-01
	REWIZJA	0