

TOM RYSUNKÓW ARCHITEKTURY — WIDOKI Z MOD

Lp.	Nr rys.	Tytuł rysunku	Skala	Format
1	PB-AR-01	RZUT PARTERU	1:50	A1
2	PB-AR-02	RZUT I PIĘTRA	1:50	A3×3
3	PB-AR-03	RZUT II PIĘTRA	1:50	A3×3
4	PB-AR-04	RZUT DACHU	1:50	A2×3
5	PB-AR-05	PRZEKRÓJ A-A	1:50	A3×3
6	PB-AR-06	PRZEKRÓJ B-B	1:50	A3×3
7	PB-AR-07	ELEWACJA POŁUDNIOWA (OGRODOWA)	1:50	A3×3
8	PB-AR-08	ELEWACJA PÓŁNOCNA (OD ULICY)	1:50	A3×3
9	PB-AR-09	ELEWACJA WSCHODNIA	1:50	A2
10	PB-AR-10	ELEWACJA ZACHODNIA	1:50	A2

PRACOWNIA PROJEKTOWA PRACOWNIA PROJEKTOWA — nazwa do uzupełnienia		STADIUM PB	BRANŻA ARCHITEKTURA (AR)			
INWESTOR (do uzupełnienia)						
OBIEKT / NAZWA ZAMIERZENIA BUDOWLANEGO Budynek mieszkalny jednorodzinny wolnostojący „Dom LAMELA”						
ADRES / LOKALIZACJA (NR DZIAŁKI, OBRĘB, JEDN. EWIDENCYJNA) ul. Lipowa (fikcyjna), dz. nr ewid. 123/4, obręb 0005 Przykładowo, gm. Przykładowo (fikcyjna)				KAT. OBIEKTU I		
FUNKCJA	IMIĘ I NAZWISKO	SPECJALNOŚĆ, NR UPRAWNIEŃ	DATA	PODPIS		
Projektant						
Projektant (wsp.)						
Sprawdzający						
Opracował						
TYTUŁ RYSUNKU SPIS RYSUNKÓW						
SKALA —	FORMAT A4	DATA WYDANIA 2026-09-25	RODZAJ DOK. spis	NR RYSUNKU PB-AR-00	ARKUSZ —	REW.

odcinek kontury 100 mm (wydruk 1:1)

RZUT PARTERU 1:50

REW.	OPIS ZMIANY		DATA	
0	Wydanie — rysunek wygenerowany z modelu		2026-09-25	
PRACOWNIA PROJEKTOWA		STADIUM	BRANŻA	
PRACOWNIA PROJEKTOWA — nazwa do uzupełnienia		PB	ARCHITEKTURA (AR)	
adres pracowni do uzupełnienia				
INWESTOR				
(do uzupełnienia)				
OBJEKT / NAZWA ZAMIERZENIA BUDOWLANEGO				
Budynek mieszkalny jednorodzinny wolnostojący „Dom LAMELA”				
ADRES / LOKALIZACJA (NR DZIAŁKI, OBRĘB, JEDN. EWIDENCYJNA)				KAT. OBJEKTU
ul. Lipowa (fikcyjna), dz. nr ewid. 1234, obręb 0005 Przykładowo, gm. Przykładowo (fikcyjna)				I
FUNKCJA	IMIĘ I NAZWISKO	SPECJALNOŚĆ, NR UPRAWNIEN	DATA	PODPIS
Projektant				
Projektant (wsp.)				
Sprawdzający				
Opracował				
TYTUŁ RYSUNKU				
RZUT PARTERU				
SKALA	FORMAT	DATA WYDANIA	RODZAJ DOK.	NR RYSUNKU
1:50	A1	2026-09-25	Izot	PB-AR-01
ARKUSZ		REW.		
1/10		0		

ZESTAWIENIE POMIESZCZEŃ

Nr	Nazwa pomieszczenia	Posadzka	Kat.	Wys. [m]	Pow. [m²]
1.06	Salon + jadalnia + kuchnia	Deska warstwowa dębowa 15 mm, klejona	podst.	2,77	54,44
1.13	Garaż 2-stanowiskowy	Posadzka żywiczna epoksydowa antypoślizgowa	podst. (garaż)	2,76	37,42
1.10	Pokój gościnny / gabinet	Deska warstwowa dębowa 15 mm, klejona	podst.	2,77	12,52
1.12	Pomieszczenie techniczne	Płytki gresowe 60×120 na kleju C2TE S1 techn.	podst.	2,76	8,85
1.11	Przedśionek gospodarczy	Płytki gresowe 60×120 na kleju C2TE S1 techn.	podst.	2,76	7,18
1.05	Śpiżarnia (pod schodami)	Płytki gresowe 60×120 na kleju C2TE S1 pomoc.	podst.	1,90	5,40
1.02	Hol	Płytki gresowe 60×120 na kleju C2TE S1 techn.	podst.	2,77	4,44
1.01	Wiatrołap	Płytki gresowe 60×120 na kleju C2TE S1 techn.	podst.	2,77	3,89
1.09	Łazienka gościnna (natrysk)	Płytki gresowe 60×120 na kleju C2TE S1 pomoc.	podst.	2,77	3,84
1.07	Pas komunikacyjny przy schodach	Deska warstwowa dębowa 15 mm, klejona	podst.	2,77	3,51
1.04	Klatka schodowa	Deska warstwowa dębowa 15 mm, klejona	podst.	2,77	2,82
1.03	WC gościnne	Płytki gresowe 60×120 na kleju C2TE S1 pomoc.	podst.	2,77	2,32
1.08	Przedpokój gościnny	Deska warstwowa dębowa 15 mm, klejona	podst.	2,77	1,44
1.14	Szacht instalacyjny SI		techn.	2,77	0,45
RAZEM powierzchnia netto					148,52
w tym użytkowa (podst. + pomoc.)					115,94

OZNACZENIA MATERIAŁÓW (PN-B-01030 + przyjęte)



	Wełna mineralna 035 (szkielet, docieplenia, ściana dom–garaż)		Ściarka szklana VSG 2 × 8 mm w ramie aluminiowej (wiatrołap / hol)
	— meander „UUU”		Żelbet C25/30, B500SP (stropy, płyta fundamentowa, ściany) —
	Styropian grafitylowy EPS 031 (ETICS, NRO w systemie) —		żyzgak „VVV”
	Bloczek wapienno-piaskowy 12 cm, kl. 15 (ściarki działowe, licowy w klatce)		Bloczek wapienno-piaskowy (silikat) 19 cm, kl. 20, gr. 1. na zaprawie cienkowarstwowej — kratka ukośna 45°/135°

OZNACZENIA LINII

—	elementy nad płaszczyzną cięcia (obrys płyt, wsporników, brył wyższych kondygnacji)
—	elementy poniżej płaszczyzny cięcia (widok z góry)
—	osie konstrukcyjne; linia punktowa z pogrubionymi końcami — ślad przekroju

OBJAŚNIENIA I UWAGI

- Wymiary w cm (mm w indeksie górnym, np. 24⁵ = 24,5 cm), rzędne w m względem ±0,000 = 101,650 m n.p.m. (PL-EVRF2007-NH).
- Rzuty: płaszczyzna cięcia +1,10 m nad posadzką kondygnacji. Linia kreskowa — elementy nad płaszczyzną cięcia (obrys płyt i wsporników, brył wyższych kondygnacji, otwory w stropie nad, belki); linia cienioka — elementy poniżej (widok).
- Otwory: licznik — szerokość, mianownik — wysokość w świetle muru, w nawiasie wysokość parapetu; symbol stolarki wg zestawienia stolarki.
- Numeracja pomieszczeń wg PN-B-01025 / PN-EN ISO 4157-2: <nr kondygnacji> (partier = 1)> <nr>, identyfikator w modelu: <skond> <nr> (partier = 0).
- Drzwi: strona otwierania (lewe/prawe) wg modelu — patrząc od strony, w którą otwiera się skrzydło.
- Rysunek wygenerowany automatycznie z modelu /home/user/alhouse/model/budynek.yaml (wersja 1.0, 2026-09-25) — generatory lamela.views.

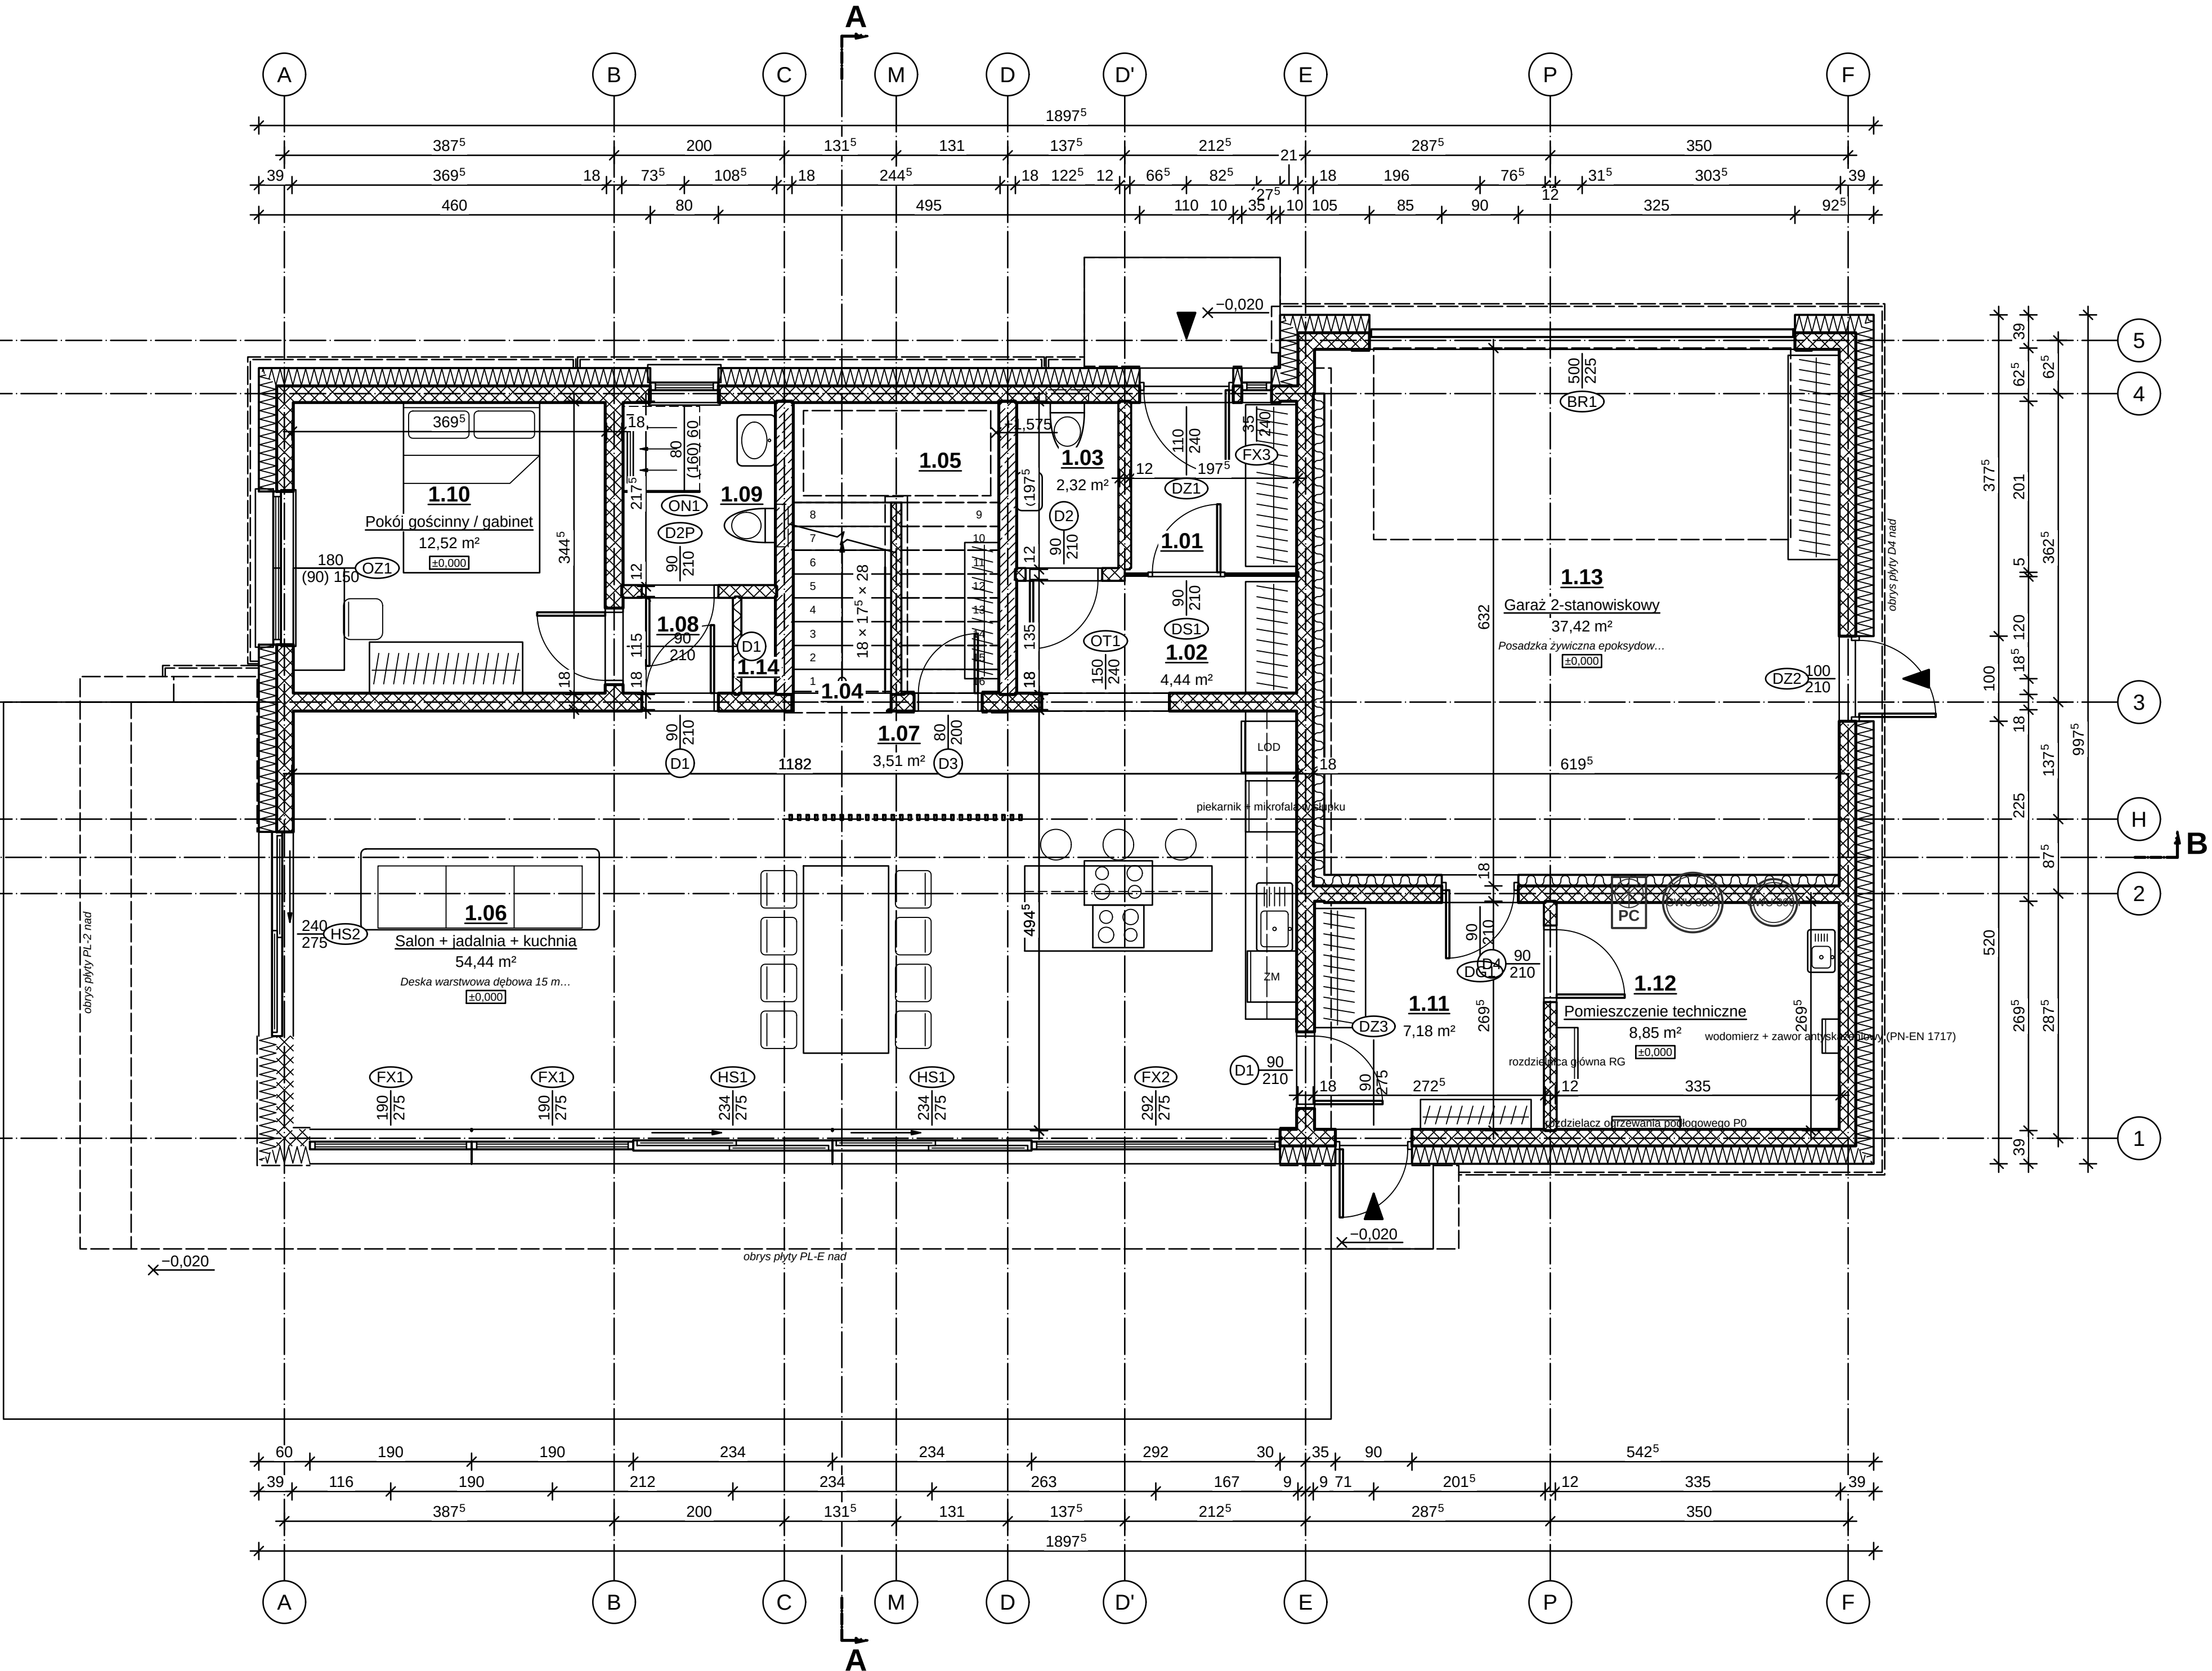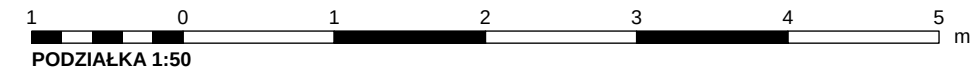

odcinek kontynuacji 100 mm (wydruk 1:1)

RZUT I PIĘTRA 1:50

ZESTAWIENIE POMIESZCZEŃ

Nr	Nazwa pomieszczenia	Posadzka	Kat.	Wys. [m]	Pow. [m²]
2.02	Pokój rodzinny / biblioteka (boks C)	Deska warstwowa dębowa 15 mm, klejona	podst.	2,77	28,36
2.01	Hol	Deska warstwowa dębowa 15 mm, klejona	naruchu	2,77	14,09
2.03	Pokój dziecka 1	Deska warstwowa dębowa 15 mm, klejona	podst.	2,77	13,19
2.04	Pokój dziecka 2	Deska warstwowa dębowa 15 mm, klejona	podst.	2,77	12,52
2.08	Pralnia z suszarnią	Płytki gresowe 60×120 na kleju C2TE \$1	pomoc.	2,77	6,64
2.05	Łazienka dzieci (wanna)	Płytki gresowe 60×120 na kleju C2TE \$1	pomoc.	2,77	5,50
2.07	WC z natryskiem	Płytki gresowe 60×120 na kleju C2TE \$1	pomoc.	2,77	4,08
2.06	Klatka schodowa	Deska warstwowa dębowa 15 mm, klejona	naruchu	2,77	0,49
2.09	Szacht instalacyjny SI		techn.	2,77	0,45
RAZEM powierzchnia netto					85,33
w tym użytkowa (podst. + pomoc.)					70,30

OZNACZENIA MATERIAŁÓW (PN-B-01030 + przyjęte)


	Wełna mineralna 035 (szkielet, docieplenia, ściana dom-garaż)		Blocek wapienno-piaskowy 12 cm, kl. 15 (ścianki działowe, licowy w klatce); Blocek wapienno-piaskowy (silikat) 18 cm, kl. 20, gr. 1, na zaprawie cienkowarstwowej — kratka ukośna 45°/135°
	meander „UUU”		Styropian grafitowy EPS 031 (ETICS, NRO w systemie) —
	zygzak „VVV”		Rama boksu C: ruszt stalowy ocynkowany w układzinie z blachy aluminiowej RAL 7016 (pusta w środku); Stal konstrukcyjna S355 (słupy RK, rama boksu C); cynkowana ognioowo + malowana proszkowo RAL 7016 — zabezpieczenie

OZNACZENIA LINII


- elementy nad płaszczyzną cięcia (obrysy płyt, wsporników, brył wyższych kondygnacji)
- elementy poniżej płaszczyzny cięcia (widok z góry)
- osie konstrukcyjne; linia punktowa z pogrubionymi końcami — ślad przekroju

OBJAŚNIENIA I UWAGI

- Wymiary w cm (mm w indeksie górnym, np. 24^h = 24,5 cm), rzędne w m względem ±0,000 = 101,650 m n.p.m. (PL-EVRF2007-NH).
- Rzuty: płaszczyzna cięcia +1,10 m nad posadzką kondygnacji. Linia kreskową — elementy nad płaszczyzną cięcia (obrysy płyt i wsporników, brył wyższych kondygnacji, otwory w stropie nad, belki); linią cieniłą — elementy poniżej (widok).
- Otwory: licznik — szerokość, mianownik — wysokość w świetle muru, w nawiasie wysokość parapetu; symbol stolarki wg zestawienia stolarki.
- Numeracja pomieszczeń wg PN-B-01025 / PN-EN ISO 4157-2: <nr kondygnacji (partier = 1)> <nr>; identyfikator w modelu: <kond>.<nr> (partier = 0).
- Drzwi: strona otwierania (lewej/prawej) wg modelu — patrząc od strony, w którą otwiera się skrzydło.
- Rysunek wygenerowany automatycznie z modelu /home/user/ai/aihouse/model/budynek.yaml (wersja 1.0, 2026-09-25) — generatory lamela.views.

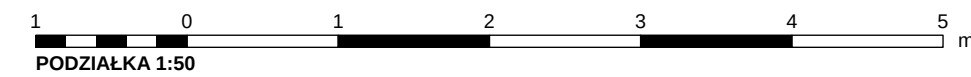

REW.	OPIS ZMIANY			DATA	
0	Wydanie — rysunek wygenerowany z modelu			2026-09-25	
PRACOWNIA PROJEKTOWA				STADIUM	BRANŻA
PRACOWNIA PROJEKTOWA — nazwa do uzupełnienia				PB	ARCHITEKTURA (AR)
adres pracowni do uzupełnienia					
INWESTOR					
(do uzupełnienia)					
OBIEKT / NAZWA ZAMIERZENIA BUDOWLANEGO					
Budynek mieszkalny jednorodzinny wolnostojący „Dom LAMELA”					
ADRES / LOKALIZACJA (NR DZIAŁKI, OBRĘB, JEDN. EWIDENCYJNA)					KAT. OBIEKTU
ul. Lipowa (fikcyjna), dz. nr ewid. 123/4, obręb 0005 Przykładowo, gm. Przykładowo (fikcyjna)					I
FUNKCJA	IMIĘ I NAZWISKO		SPECJALNOŚĆ, NR UPRAWNIENI		DATA
Projektant					
Projektant (wsp.)					
Sprawdzający					
Opracował					
TYTUŁ RYSUNKU					
RZUT I PIĘTRA					
SKALA	FORMAT	DATA WYDANIA	RODZAJ DOK.	NR RYSUNKU	ARKUSZ
1:50	A3×3	2026-09-25	rzut	PB-AR-02	2/10
					REW. 0

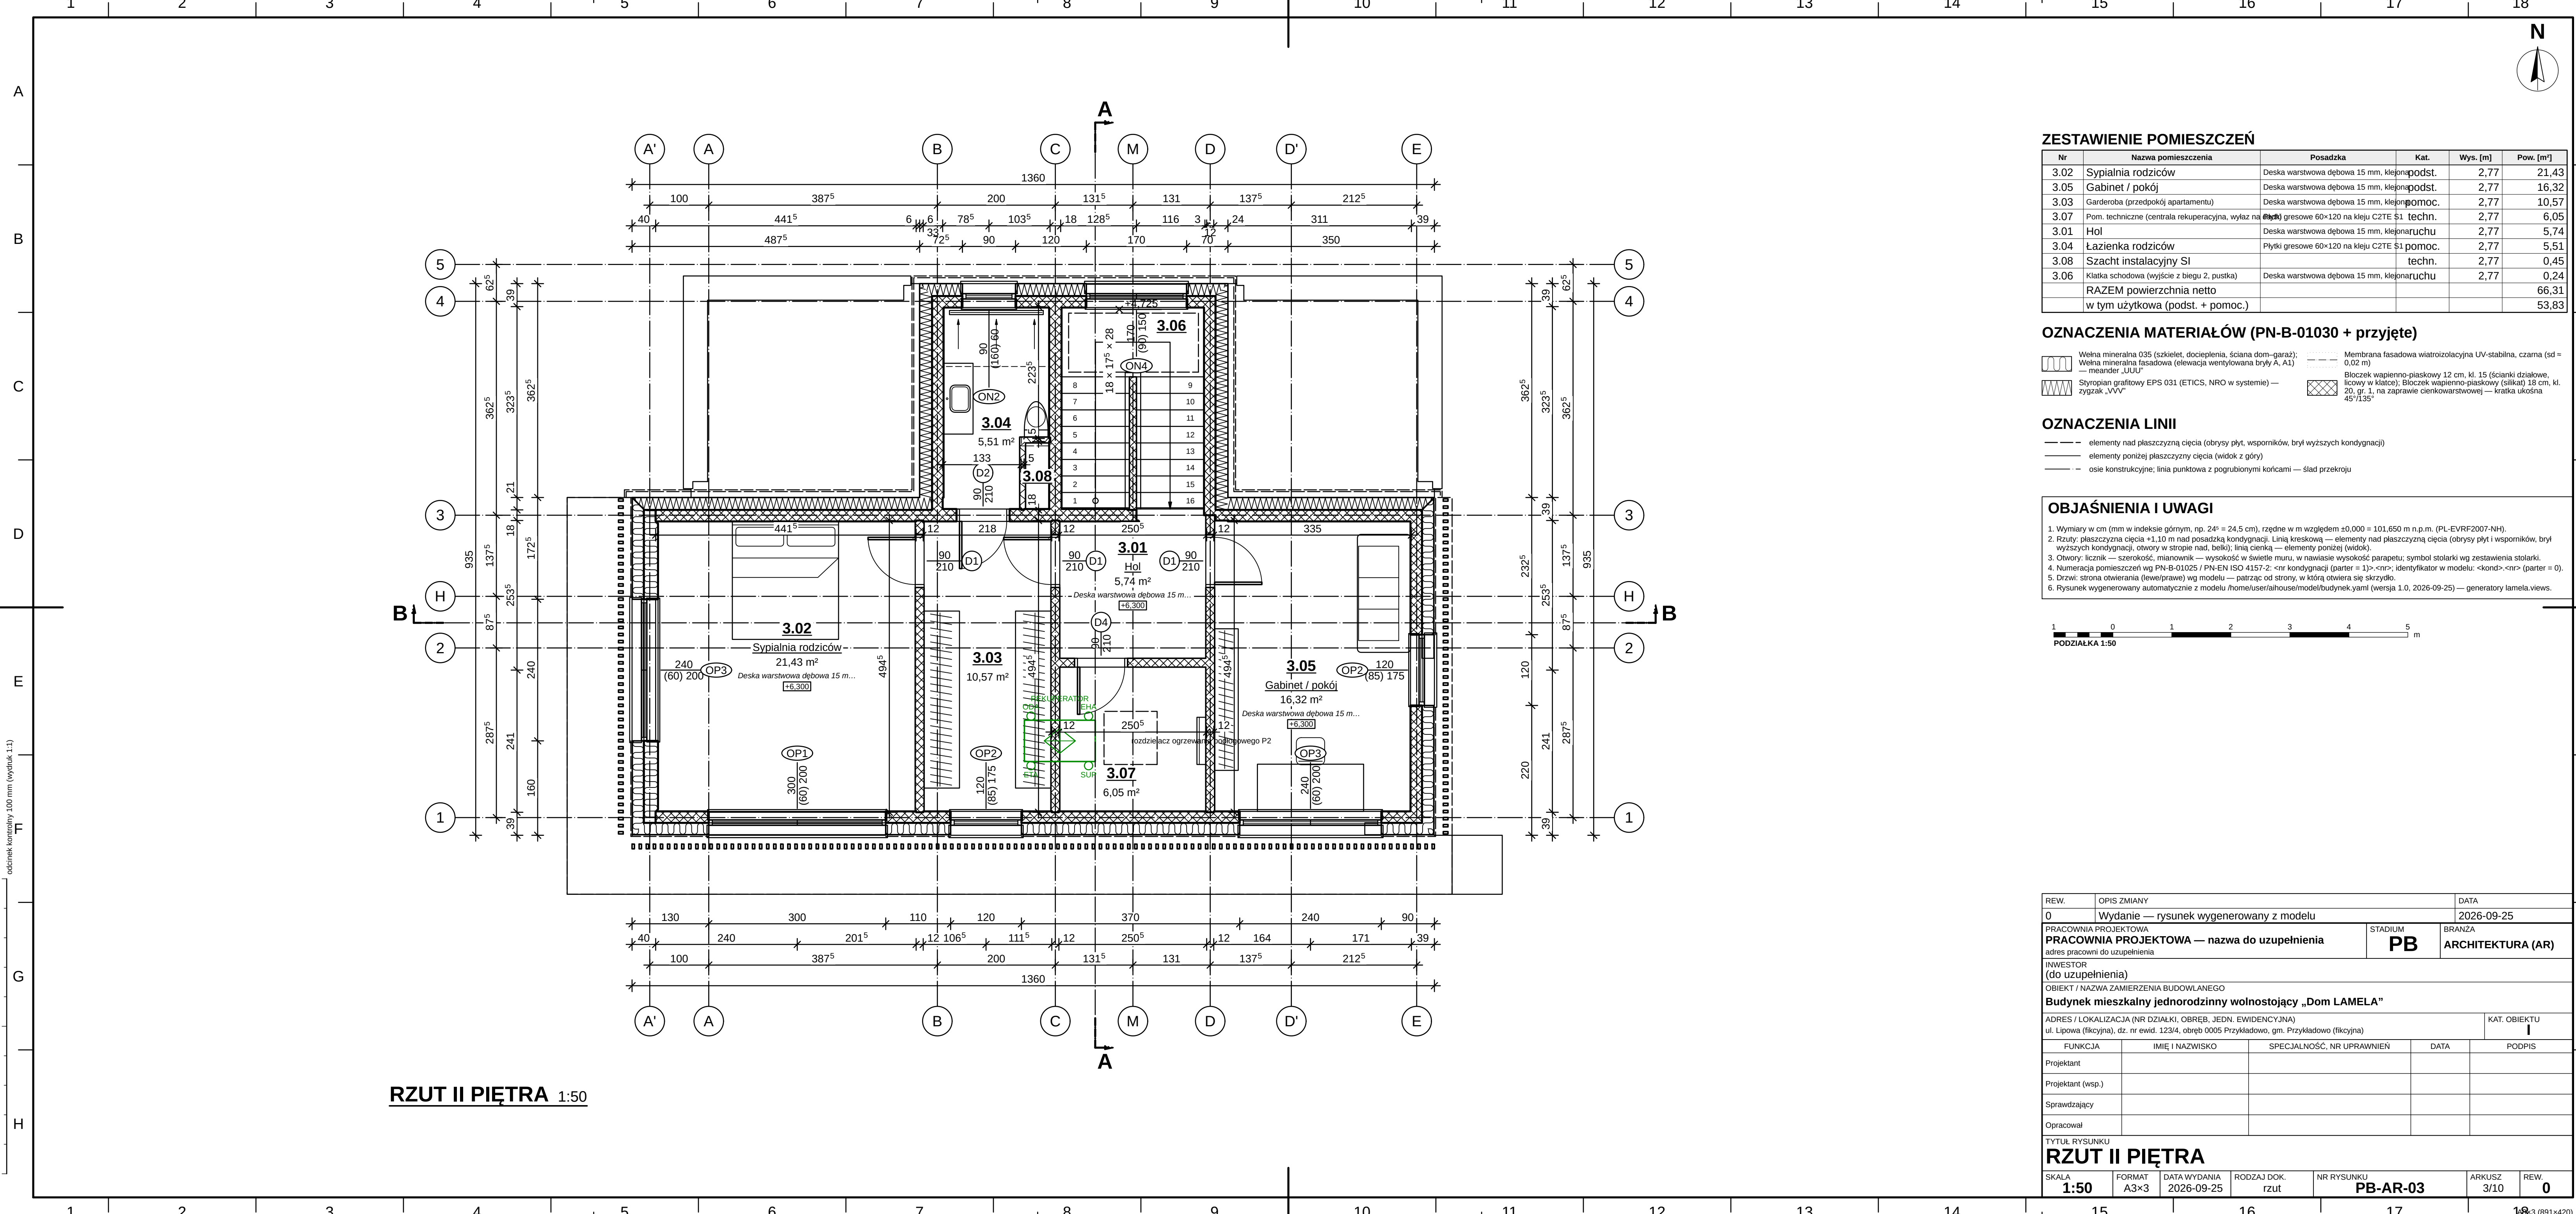

ZESTAWIENIE POMIESZCZEŃ

Nr	Nazwa pomieszczenia	Posadzka	Kat.	Wys. [m]	Pow. [m²]
3.02	Sypialnia rodziców	Deska warstwowa dębowa 15 mm, klejona	podst.	2,77	21,43
3.05	Gabinet / pokój	Deska warstwowa dębowa 15 mm, klejona	podst.	2,77	16,32
3.03	Garderoba (przedpokój apartamentu)	Deska warstwowa dębowa 15 mm, klejona	pomoc.	2,77	10,57
3.07	Pom. techniczne (centrala rekuperacyjna, wylaz na dach)	Płytki gresowe 60×120 na kleju C2TE \$1	techn.	2,77	6,05
3.01	Hol	Deska warstwowa dębowa 15 mm, klejona	aruchu	2,77	5,74
3.04	Łazienka rodziców	Płytki gresowe 60×120 na kleju C2TE \$1	pomoc.	2,77	5,51
3.08	Szacht instalacyjny SI		techn.	2,77	0,45
3.06	Klatka schodowa (wyjście z biegu 2, pustka)	Deska warstwowa dębowa 15 mm, klejona	aruchu	2,77	0,24
RAZEM powierzchnia netto					66,31
w tym użytkowa (podst. + pomoc.)					53,83

OZNACZENIA MATERIAŁÓW (PN-B-01030 + przyjęte)


	Włna mineralna 035 (szkielet, docieplenia, ściana dom-garaż); Włna mineralna fasadowa (elewacja wentylowana bryły A, A1) — meander „UJU”		Membrana fasadowa wiatroizolacyjna UV-stabilna, czarna (sd = 0,02 m)
	Styropian grafitowy EPS 031 (ETICS, NRO w systemie) — zygzak „VVV”		Błoczek wapienno-piaskowy 12 cm, kl. 15 (ścianki działowe, licowy w klatce); Błoczek wapienno-piaskowy (silikat) 18 cm, kl. 20, gr. 1, na zaprawie cienkowarstwowej — kratka ukośna 45°/135°

OZNACZENIA LINII


---	elementy nad płaszczyzną cięcia (obrys płyt, wsporników, brył wyższych kondygnacji)
---	elementy poniżej płaszczyzny cięcia (widok z góry)
---	osie konstrukcyjne; linia punktowa z pogrubionymi końcami — ślad przekroju

OBJAŚNIENIA I UWAGI

- Wymiary w cm (mm w indeksie górnym, np. 24⁵ = 24,5 cm), rzędne w m względem ±0,000 = 101,650 m n.p.m. (PL-EVRF2007-NH).
- Rzuty: płaszczyzna cięcia +1,10 m nad posadzką kondygnacji. Linia kreskowa — elementy nad płaszczyzną cięcia (obrys płyt i wsporników, brył wyższych kondygnacji), otwory w stropie nad, belki; linia cienką — elementy poniżej (widok).
- Otwory: licznik — szerokość, mianownik — wysokość w świetle muru, w nawiasie wysokość parapetu; symbol stolarki wg zestawienia stolarki.
- Numeracja pomieszczeń wg PN-B-01025 / PN-EN ISO 4157-2: <nr kondygnacji (partier = 1)>. <nr>; identyfikator w modelu: <kond>-<nr> (partier = 0).
- Drzwi: strona otwierania (lewe/prawe) wg modelu — patrząc od strony, w którą otwiera się skrzydło.
- Rysunek wygenerowany automatycznie z modelu /home/user/ai/house/model/budynek.yaml (wersja 1.0, 2026-09-25) — generatory lamela.views.

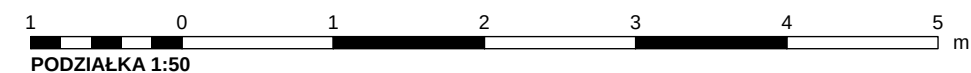

REW.	OPIS ZMIANY			DATA	
0	Wydanie — rysunek wygenerowany z modelu			2026-09-25	
PRACOWNIA PROJEKTOWA				STADIUM	BRANŻA
PRACOWNIA PROJEKTOWA — nazwa do uzupełnienia				PB	ARCHITEKTURA (AR)
adres pracowni do uzupełnienia					
INWESTOR					
(do uzupełnienia)					
OBIEKT / NAZWA ZAMIERZENIA BUDOWLANEGO					
Budynek mieszkalny jednorodzinny wolnostojący „Dom LAMELA”					
ADRES / LOKALIZACJA (NR DZIAŁKI, OBRĘB, JEDN. EWIDENCYJNA)					KAT. OBIEKTU
ul. Lipowa (fikcyjna), dz. nr ewid. 123/4, obręb 0005 Przykładowo, gm. Przykładowo (fikcyjna)					I
FUNKCJA	IMIĘ I NAZWISKO	SPECJALNOŚĆ, NR UPRAWNIENI	DATA	PODPIS	
Projektant					
Projektant (wsp.)					
Sprawdzający					
Opracował					
TYTUŁ RYSUNKU					
RZUT II PIĘTRA					
SKALA	FORMAT	DATA WYDANIA	RODZAJ DOK.	NR RYSUNKU	ARKUSZ
1:50	A3×3	2026-09-25	rzut	PB-AR-03	3/10
					REW.
					0

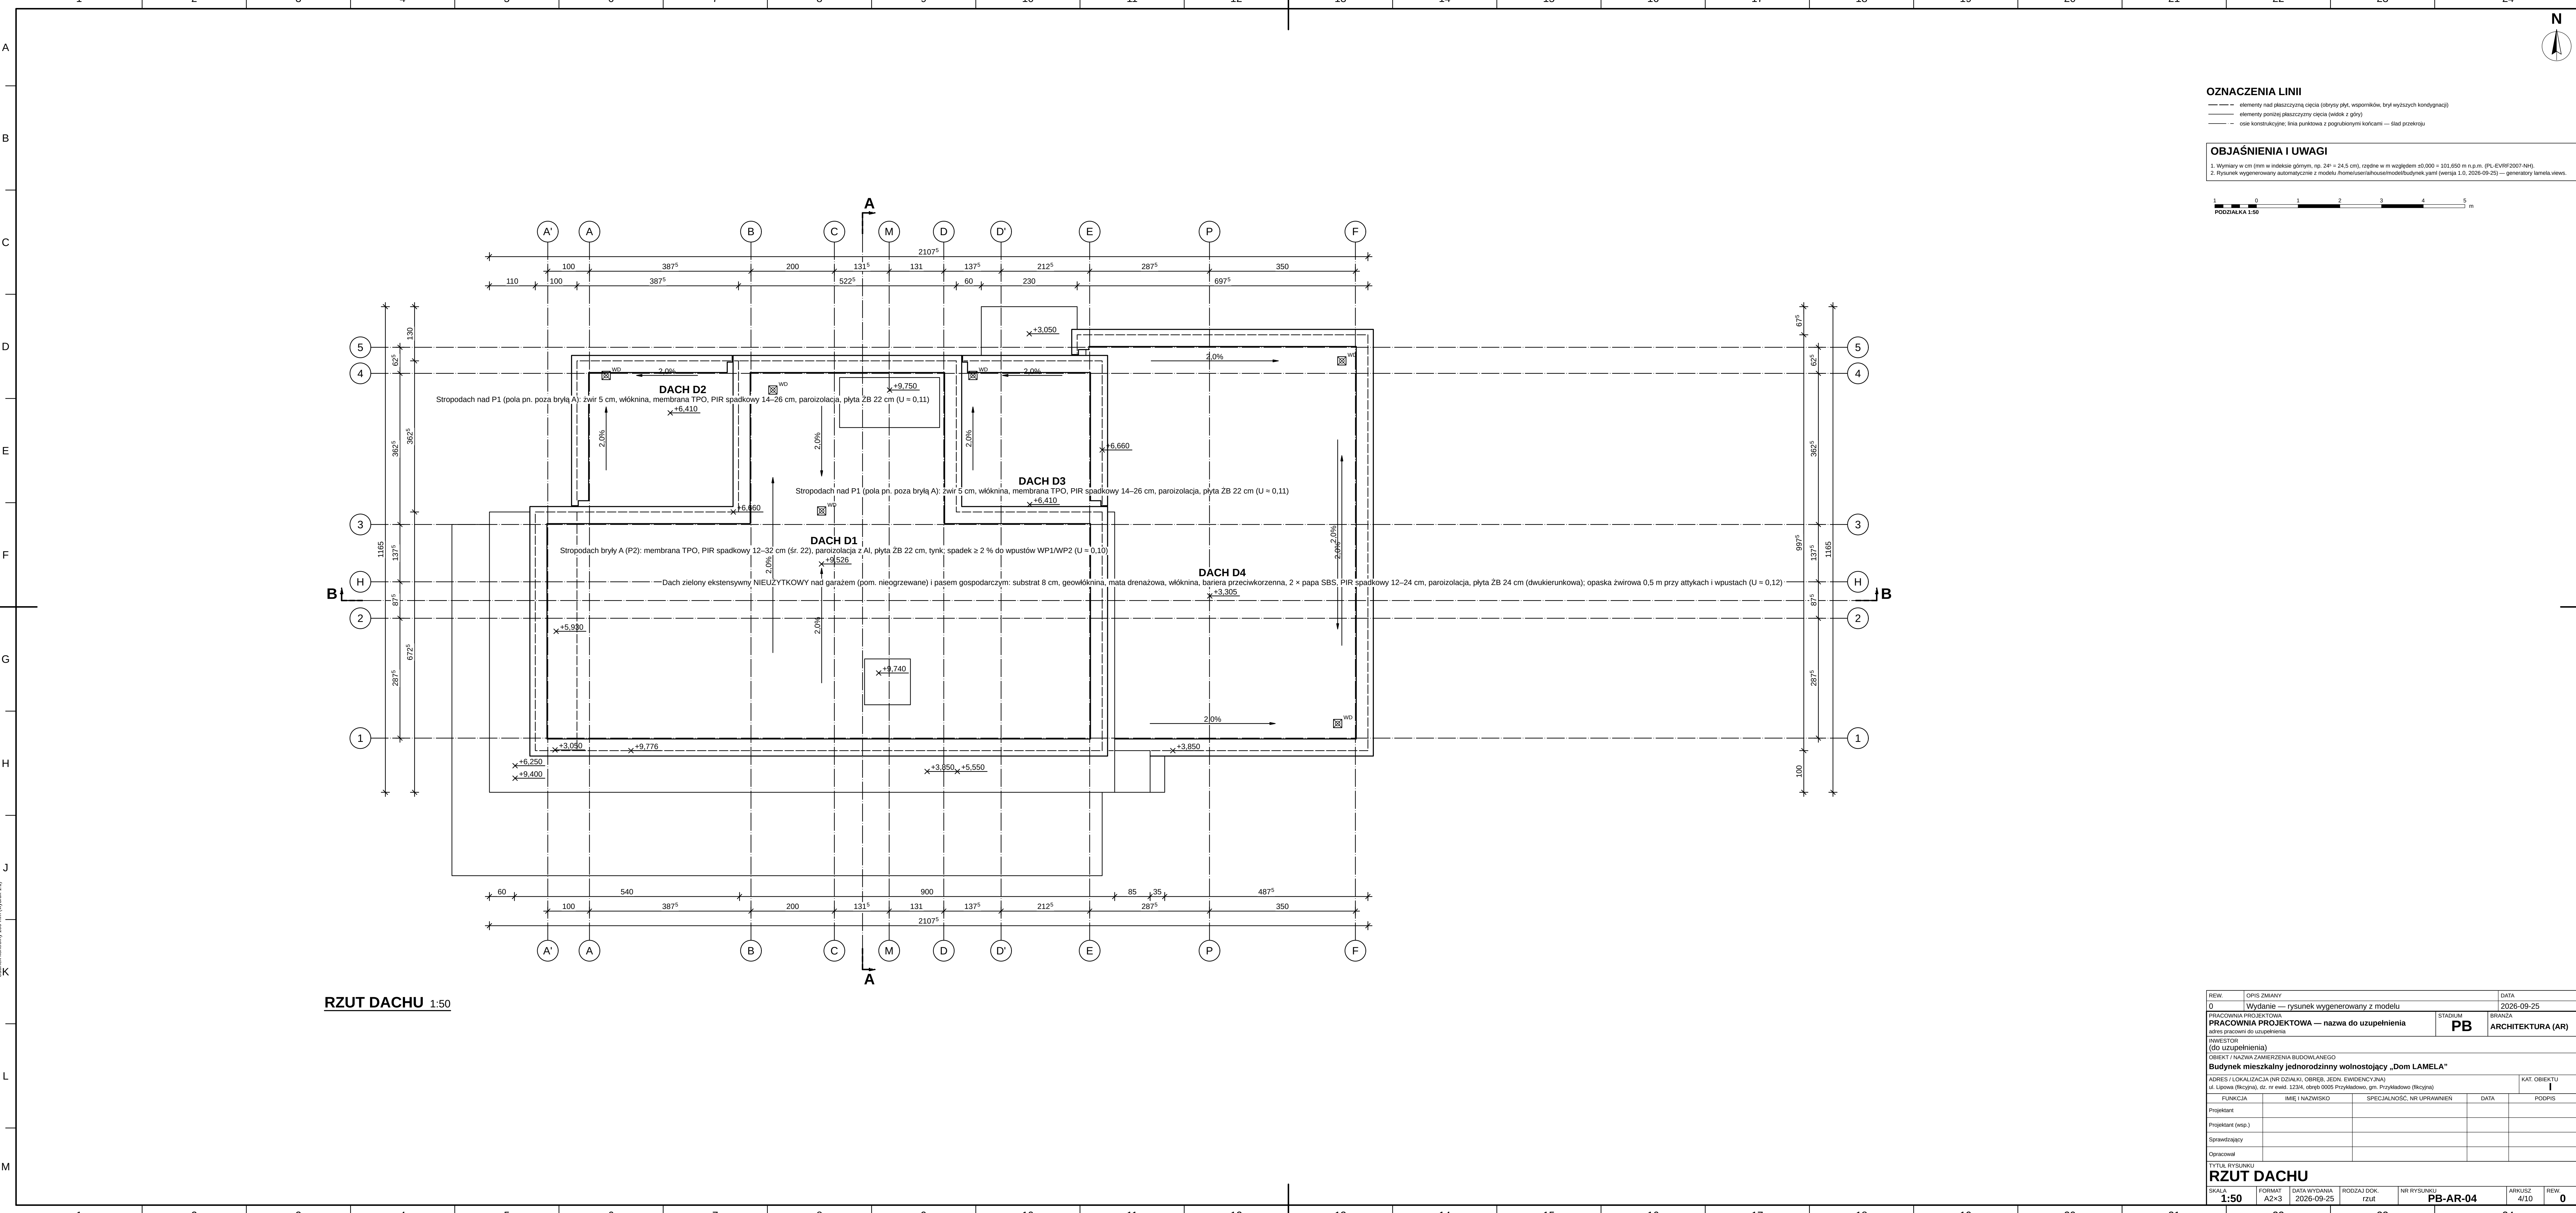

RZUT DACHU 1:50


OZNACZENIA LINII

- elementy nad płaszczyznę cięcia (obryszy płyt, wspomników, brył wyższych kondygnacji)
- elementy poniżej płaszczyzny cięcia (wielok z góry)
- osie konstrukcyjne; linia punktowa z pogrubionymi końcami — ślad przekroju

OBJAŚNIENIA I UWAGI

1. Wymiary w cm (mm w indeksie górnym, np. 24⁵ = 24,5 cm), rzędy w m względem s.0.000 = 101.650 m n.p.m. (PL-EVRP2007-NH).

2. Rysunek wygenerowany automatycznie z modelu /modeluser/housemodel/budynek-yarni (wersja 1.0, 2026-09-25) — generatory lamela.views.

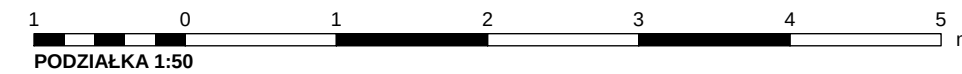

REW.	OPIS ZMIANY			DATA	
0	Wydanie — rysunek wygenerowany z modelu			2026-09-25	
PRACOWNIA PROJEKTOWA			STADIUM	BRANŻA	
PRACOWNIA PROJEKTOWA — nazwa do uzupełnienia			PB	ARCHITEKTURA (AR)	
adres pracowni do uzupełnienia					
INWESTOR					
(do uzupełnienia)					
OBIEKT (nazwa zamierzenia budowlanego)					
Budynek mieszkalny jednorodzinny wolnostojący „Dom LAMELA”					
ADRES / LOKALIZACJA (nr działki, obręb, jedn. ewidencyj. mapy)					KAT. OBIEKTU
ul. Lipowa (Racjonal), dz. nr ewid. 1234, obręb 0005 Przykładowo, gm. Przykładowo (Racjonal)					I
FUNKCJA	IMIE I NAZWISKO	SPECJALNOŚĆ, NR UPRAWNIEN	DATA	PODOPIS	
Projektant					
Projektant (wsp.)					
Sprawdzający					
Opracował					
TYTUŁ RYSUNKU					
RZUT DACHU					
SKALA	FORMAT	DATA WYDANIA	RODZAJ DOK.	NR RYSUNKU	REW.
1:50	A2x3	2026-09-25	rzut	PB-AR-04	0
				ARKUSZ	
				4/10	

PRZEKRÓJ B-B 1:50

wysokość budynku wg § 6 WT: H = 9,79 m

odcinek kantyliny 100 mm (wydruk 1:1)

SD1 — Stropodach bryły A (P2): membrana TPO, PIR spadkowy 12–32 cm (śr. 22)...
Membrana dachowa TPO 1,5 mm, mocowana mechanicznie (hydroizolacja stropodachów) 2 mm
Płyty PIR z okładziną (izolacja spadkowa stropodachów) 22 cm
Paroizolacja bitumiczna z wkładką Al (na płycie stropodachów) 4 mm
Żelbet C25/30, B500SP (stropy, płyta fundamentowa, ściany) 22 cm
Tynk gipsowy maszynowy 1,5 cm 1 cm

3.02
Sypialnia rodziców

STROP ST2 + POD-1 — Strop międzykondygnacyjny: deska dębowa...
Deska warstwowa dębowa 15 mm, klejona 1,5 cm
Jasnych cementowy CT-C25-F5 z węzownicą ogrzewania podłogowego 6,5 cm
Styropian podłogowy EPS 100-038 (pod jasnym) 4 cm
Styropian elastyczny EPS T (akustyczny, pod jasnym) 3 cm
Żelbet C25/30, B500SP (stropy, płyta fundamentowa, ściany) 22 cm
Tynk gipsowy maszynowy 1,5 cm 1 cm

2.03
Pokój dziecka 1

2.02 STROP ST1 + POD-1 — Strop międzykondygnacyjny: deska dębowa...
Deska warstwowa dębowa 15 mm, klejona 1,5 cm
Jasnych cementowy CT-C25-F5 z węzownicą ogrzewania podłogowego 6,5 cm
Styropian podłogowy EPS 100-038 (pod jasnym) 4 cm
Styropian elastyczny EPS T (akustyczny, pod jasnym) 3 cm
Żelbet C25/30, B500SP (stropy, płyta fundamentowa, ściany) 22 cm
Tynk gipsowy maszynowy 1,5 cm 1 cm

POD-0 — Podłoga na płycie fundamentowej (P0): deska/gres, jasnych z ogrzewaniem podł., EPS...
Deska warstwowa dębowa 15 mm, klejona 1,5 cm
Jasnych cementowy CT-C25-F5 z węzownicą ogrzewania podłogowego 6,5 cm
Styropian podłogowy EPS 100-038 (pod jasnym) 6,5 cm
Izolacja przeciwwilgociowa i przeciwradonowa: membrana SBS 4 mm na płycie fundamentowej 5 mm
Żelbet C25/30, B500SP (stropy, płyta fundamentowa, ściany) 25 cm
Polistyren ekstrudowany XPS 300 (pod płytą fundamentową, cokół, izolacja obwodowa) 20 cm
Folia PE 0,2 mm — warstwa rozdzielająca pod XPS (nie pełni funkcji paroizolacji)
Podsyłka piaskowa zagęszczona (l_s ≥ 0,58) 20 cm

1.06

DZ1 — Dach zielony ekstensywny NIEUŻYTKOWY nad garażem (pom...
Substrat ekstensywny 8 cm z matą rozchodnikową (sedum)
Geowłóknina filtracyjna PP 150 g/m² 2 mm
Mata drenażowo-retencyjna HDPE 25 mm (dach zielony) 2,5 cm
Włóknina ochronna PP 300 g/m² 4 mm
Bariera przeciwwodna PE-HD 0,5 mm (PN-EN 13948)
Hydroizolacja 2 × papa SBS (podkładowa + wierzchniego krycia, dach zielony) 9,5 mm
Płyty PIR z okładziną (izolacja spadkowa stropodachów) 18 cm
Paroizolacja bitumiczna z wkładką Al (na płycie stropodachów) 4 mm
Żelbet C25/30, B500SP (stropy, płyta fundamentowa, ściany) 24 cm

SZ1 — Ściana zewnętrzna nośna: silikat 18 + ETICS EPS 031 20 cm (U = 0,15)
Tynk gipsowy maszynowy 1,5 cm
Błoczek wapienno-piaskowy (silikat) 18 cm, kl. 20, gr. 1, na zaprawie cienkowarstwowej
Styropian grafitowy EPS 031 (ETICS, NRO w systemie) 20 cm
ETICS: warstwa zbrojona + tynk silikonowy 1,5 mm (biały / jasnoszary NCS S 1500-N) 1 cm

1.13

OZNACZENIA MATERIAŁÓW (PN-B-01030 + przyjęte)


	grunt rodzimy		Membrana fasadowa wiatroizolacyjna UV-stabilna, czarna (sd = 0,02 m)
	Substrat ekstensywny 8 cm z matą rozchodnikową (sedum)		Błoczek wapienno-piaskowy 12 cm, kl. 15 (ścianki działowe, licowy w klatce); Błoczek wapienno-piaskowy (silikat) 18 cm, kl. 20, gr. 1, na zaprawie cienkowarstwowej — krata ukośna 45°/135°
	Welna mineralna 035 (szkielet, docieplenia, ściana dom-garaż); Welna mineralna fasadowa (elewacja wentylowana bryły A, A1) — meander „UUU”		Paroizolacja bitumiczna z wkładką Al (na płycie stropodachów) — linia kreskowa cienka 3/1 po ciepłej stronie
	Płyty PIR z okładziną (izolacja spadkowa stropodachów) — zygzak z okładzinami		Podsyłka piaskowa zagęszczona (l _s ≥ 0,98)
	Izolacja przeciwwilgociowa i przeciwradonowa: membrana SBS 4 mm na płycie fundamentowej — linia bardzo gruba		Obróbki blacharskie (blacha powlekana); Stolarka — profile aluminiowe, antracyt; Stal malowana proszkowo (balustrady, rygle) — zaczerpnięcie
	Membrana dachowa TPO 1,5 mm, mocowana mechanicznie (hydroizolacja stropodachów); Hydroizolacja 2 × papa SBS (podkładowa + wierzchniego krycia, dach zielony) — pas czarno-biały		Tynk cementowo-wapienny 1,5 cm (garaż, pom. techniczne); Tynk gipsowy maszynowy 1,5 cm; ETICS: warstwa zbrojona + tynk silikonowy 1,5 mm (biały / jasnoszary NCS S 1500-N) — kropki nieregularne
	Styropian grafitowy EPS 031 (ETICS, NRO w systemie); Styropian podłogowy EPS 100-038 (pod jasnym); Styropian elastyczny EPS T (akustyczny, pod jasnym) — zygzak „VVV”		Żelbet C25/30, B500SP (stropy, płyta fundamentowa, ściany); Żelbet C50/37 XC4/XF1 (krawędzie płyt wysuniętych, atyki, belki) — 45° na przemian ciepłe i przegrzewane
	Polistyren ekstrudowany XPS 300 (pod płytą fundamentową, cokół, izolacja obwodowa) — zygzak podwójny		Podbudowa nawierzchni (kruszywo)
	Jasnych cementowych CT-C25-F5 z węzownicą ogrzewania podłogowego — kropki		

OBJAŚNIENIA I UWAGI

- Wymiary w cm (mm w indeksie górnym, np. 24° = 24,5 cm), rzędne w m względem ±0,000 = 101,650 m n.p.m. (PL-EVRF2007-NH).
- Rzędne: trójkąt zaczerpnięty — poziom wykończenia, niezaczerpnięty — konstrukcji, w pokłowie zaczerpnięty — poziom ±0,000 z rzędną bezwzględną (PN-B-01025).
- Wysokość budynku wg § 6 WT: od terenu przy najniższej położonym wejściu (−0,267) do wierzchu stropodachu D1 (+9,526) — H = 9,79 m (bez atyki).
- Opisy warstw: kod i nazwa przegrody z modelu, materiały i grubości wg modelu (od góry / od lewej).
- Opisy warstw pominięte na rysunku (brak miejsca w podziale 1:50): STROP ST22 + POD-1, OK1 — układ warstw wg zestawienia przegród w części opisowej / przekroju 1:50.
- Rysunek wygenerowany automatycznie z modelu /home/user/aihouse/model/budynki.yaml (wersja 1.0, 2026-09-25) — generatory lamela.views.

1 0 1 2 3 4 5 m
PODZIAŁKA 1:50

REW.	OPIS ZMIANY	DATA
0	Wydanie — rysunek wygenerowany z modelu	2026-09-25
PRACOWNIA PROJEKTOWA PRACOWNIA PROJEKTOWA — nazwa do uzupełnienia		STADIUM PB
adres pracowni do uzupełnienia		BRANŻA ARCHITEKTURA (AR)
INWESTOR (do uzupełnienia)		
OBIEKT / NAZWA ZAMIERZENIA BUDOWLANEGO Budynek mieszkalny jednorodzinny wolnostojący „Dom LAMELA”		
ADRES / LOKALIZACJA (NR DZIAŁKI, OBRĘB, JEDN. EWIDENCYJNA) ul. Lipowa (fikcyjna), dz. nr ewid. 123/4, obręb 0005 Przykładowo, gm. Przykładowo (fikcyjna)		KAT. OBIEKTU I
FUNKCJA	IMIĘ I NAZWISKO	SPECJALNOŚĆ, NR UPRAWNIEN
Projektant		DATA
Projektant (wsp.)		PODPIS
Sprawdzający		
Opracował		
TYTUŁ RYSUNKU PRZEKRÓJ B-B		
SKALA 1:50	FORMAT A3×3	DATA WYDANIA 2026-09-25
RODZAJ DOK. przekrój	NR RYSUNKU PB-AR-06	ARKUSZ 6/10
		REW. 0

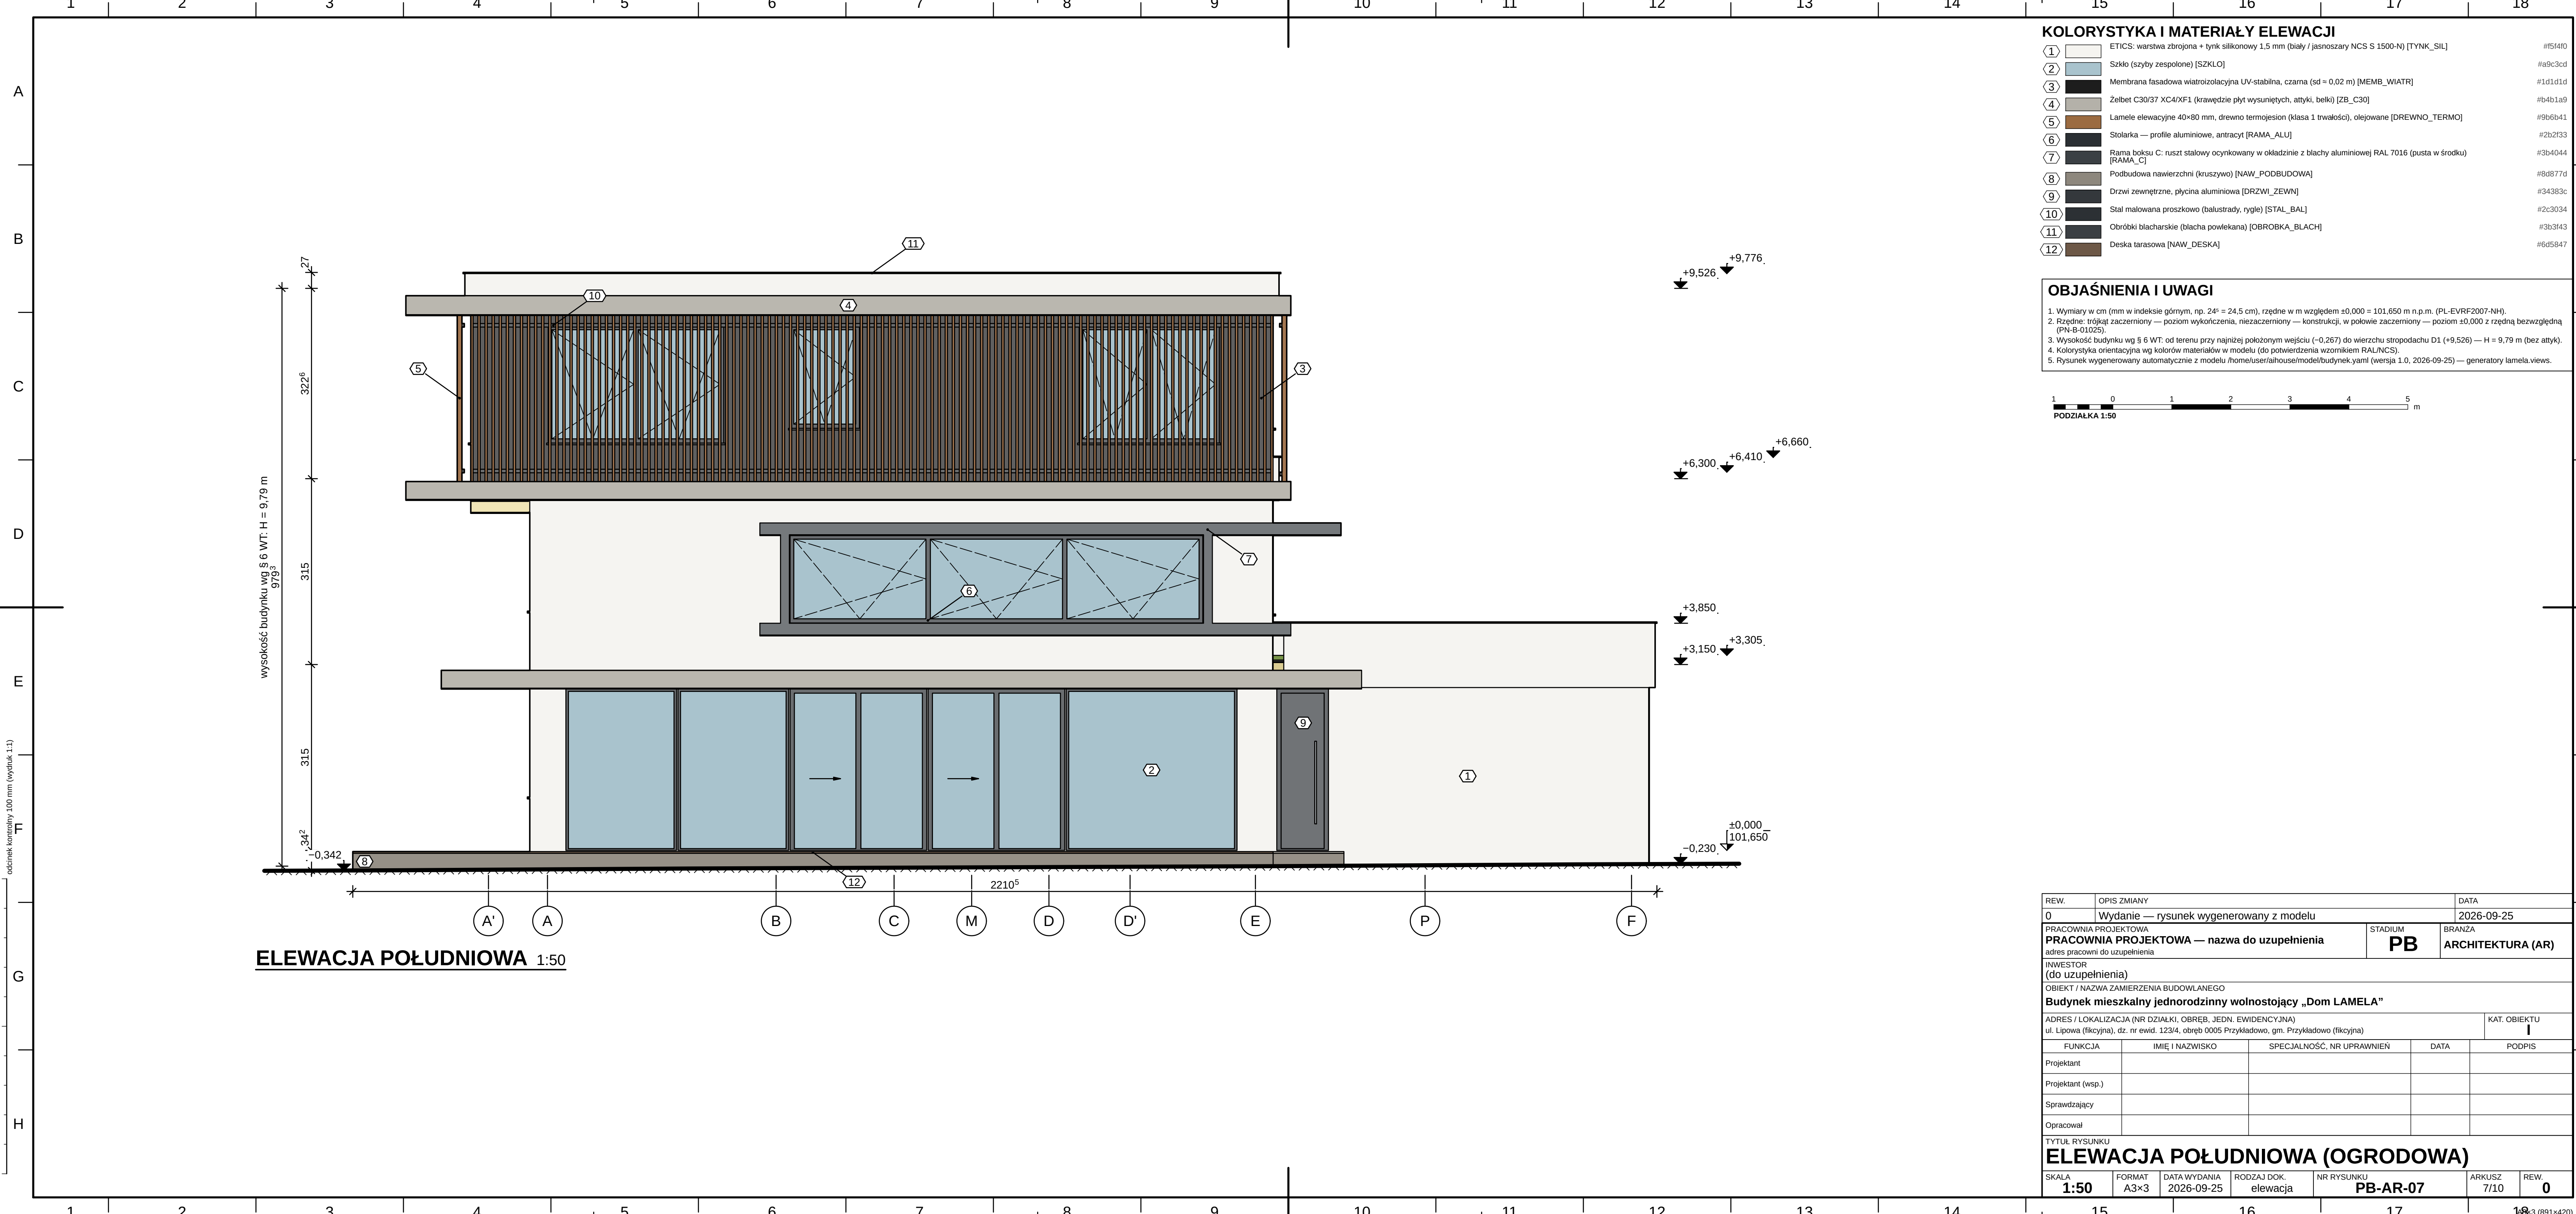


KOLORYSTYKA I MATERIAŁY ELEWACJI


1	ETICS: warstwa zbrojona + tynk silikonowy 1,5 mm (biały / jasnoszary NCS S 1500-N) [TYNK_SIL]	#f5f4f0
2	Szko (szyby zespolone) [SZKLO]	#a9c3cd
3	Membrana fasadowa wiatroizolacyjna UV-stabilna, czarna (sd = 0,02 m) [MEMB_WIATR]	#1d1d1d
4	Żelbet C30/37 XC4/XF1 (krawędzie płyt wysuniętych, attyki, belki) [ZB_C30]	#b4b1a9
5	Lamele elewacyjne 40×80 mm, drewno termojesion (klasa 1 trwałości), olejowane [DREWNO_TERMO]	#9b6b41
6	Stolarka — profile aluminiowe, antracyt [RAMA_ALU]	#2b2f33
7	Rama boksu C: ruszt stalowy ocynkowany w okładzinie z blachy aluminiowej RAL 7016 (pusta w środku) [RAMA_C]	#3b4044
8	Podbudowa nawierzchni (kruszywo) [NAW_PODBUDOWA]	#8d877d
9	Drzwi zewnętrzne, płycina aluminiowa [DRZWI_ZEWN]	#34383c
10	Stal malowana proszkowo (balustrady, rygle) [STAL_BAL]	#2c3034
11	Obróbki blacharskie (blacha powlekana) [OBROBKA_BLACH]	#3b3f43
12	Deska tarasowa [NAW_DESKA]	#6d5847

OBJAŚNIENIA I UWAGI

- Wymiary w cm (mm w indeksie górnym, np. 24² = 24,5 cm), rzędne w m względem ±0,000 = 101,650 m n.p.m. (PL-EVRF2007-NH).
- Rzędne: trójkąt zaczerpiony — poziom wykończenia, niezaczerpiony — konstrukcji, w polowie zaczerpiony — poziom ±0,000 z rzędną bezwzględną (PN-B-01025).
- Wysokość budynku wg § 6 WT: od terenu przy najniższym wejściu (-0,267) do wierzchu stropodachu D1 (+9,526) — H = 9,79 m (bez attyki).
- Kolorystyka orientacyjna wg kolorów materiałów w modelu (do potwierdzenia wzornikiem RAL/NCS).
- Rysunek wygenerowany automatycznie z modelu /home/user/aihouse/model/budynek.yaml (wersja 1.0, 2026-09-25) — generatory lamela.views.

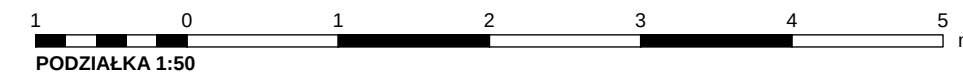

REW.	OPIS ZMIANY	DATA
0	Wydanie — rysunek wygenerowany z modelu	2026-09-25
PRACOWNIA PROJEKTOWA	PRACOWNIA PROJEKTOWA — nazwa do uzupełnienia	STADIUM PB
adres pracowni do uzupełnienia	BRANZA ARCHITEKTURA (AR)	
INWESTOR (do uzupełnienia)	OBIEKT / NAZWA ZAMIERZENIA BUDOWLANEGO Budynek mieszkalny jednorodzinny wolnostojący „Dom LAMELA”	
ADRES / LOKALIZACJA (NR DZIAŁKI, OBREB, JEDN. EWIDENCYJNA) ul. Lipowa (fikcyjna), dz. nr ewid. 123/4, obręb 0005 Przykładowo, gm. Przykładowo (fikcyjna)	KAT. OBIEKTU I	
FUNKCJA	IMIĘ I NAZWISKO	SPECJALNOŚĆ, NR UPRAWNIENI
Projektant		DATA
Projektant (wsp.)		PODPIS
Sprawdzający		
Opracował		
TYTUŁ RYSUNKU ELEVACJA POŁUDNIOWA (OGRODOWA)		
SKALA 1:50	FORMAT A3×3	DATA WYDANIA 2026-09-25
RODZAJ DOK. elewacja	NR RYSUNKU PB-AR-07	ARKUSZ 7/10
REW. 0		

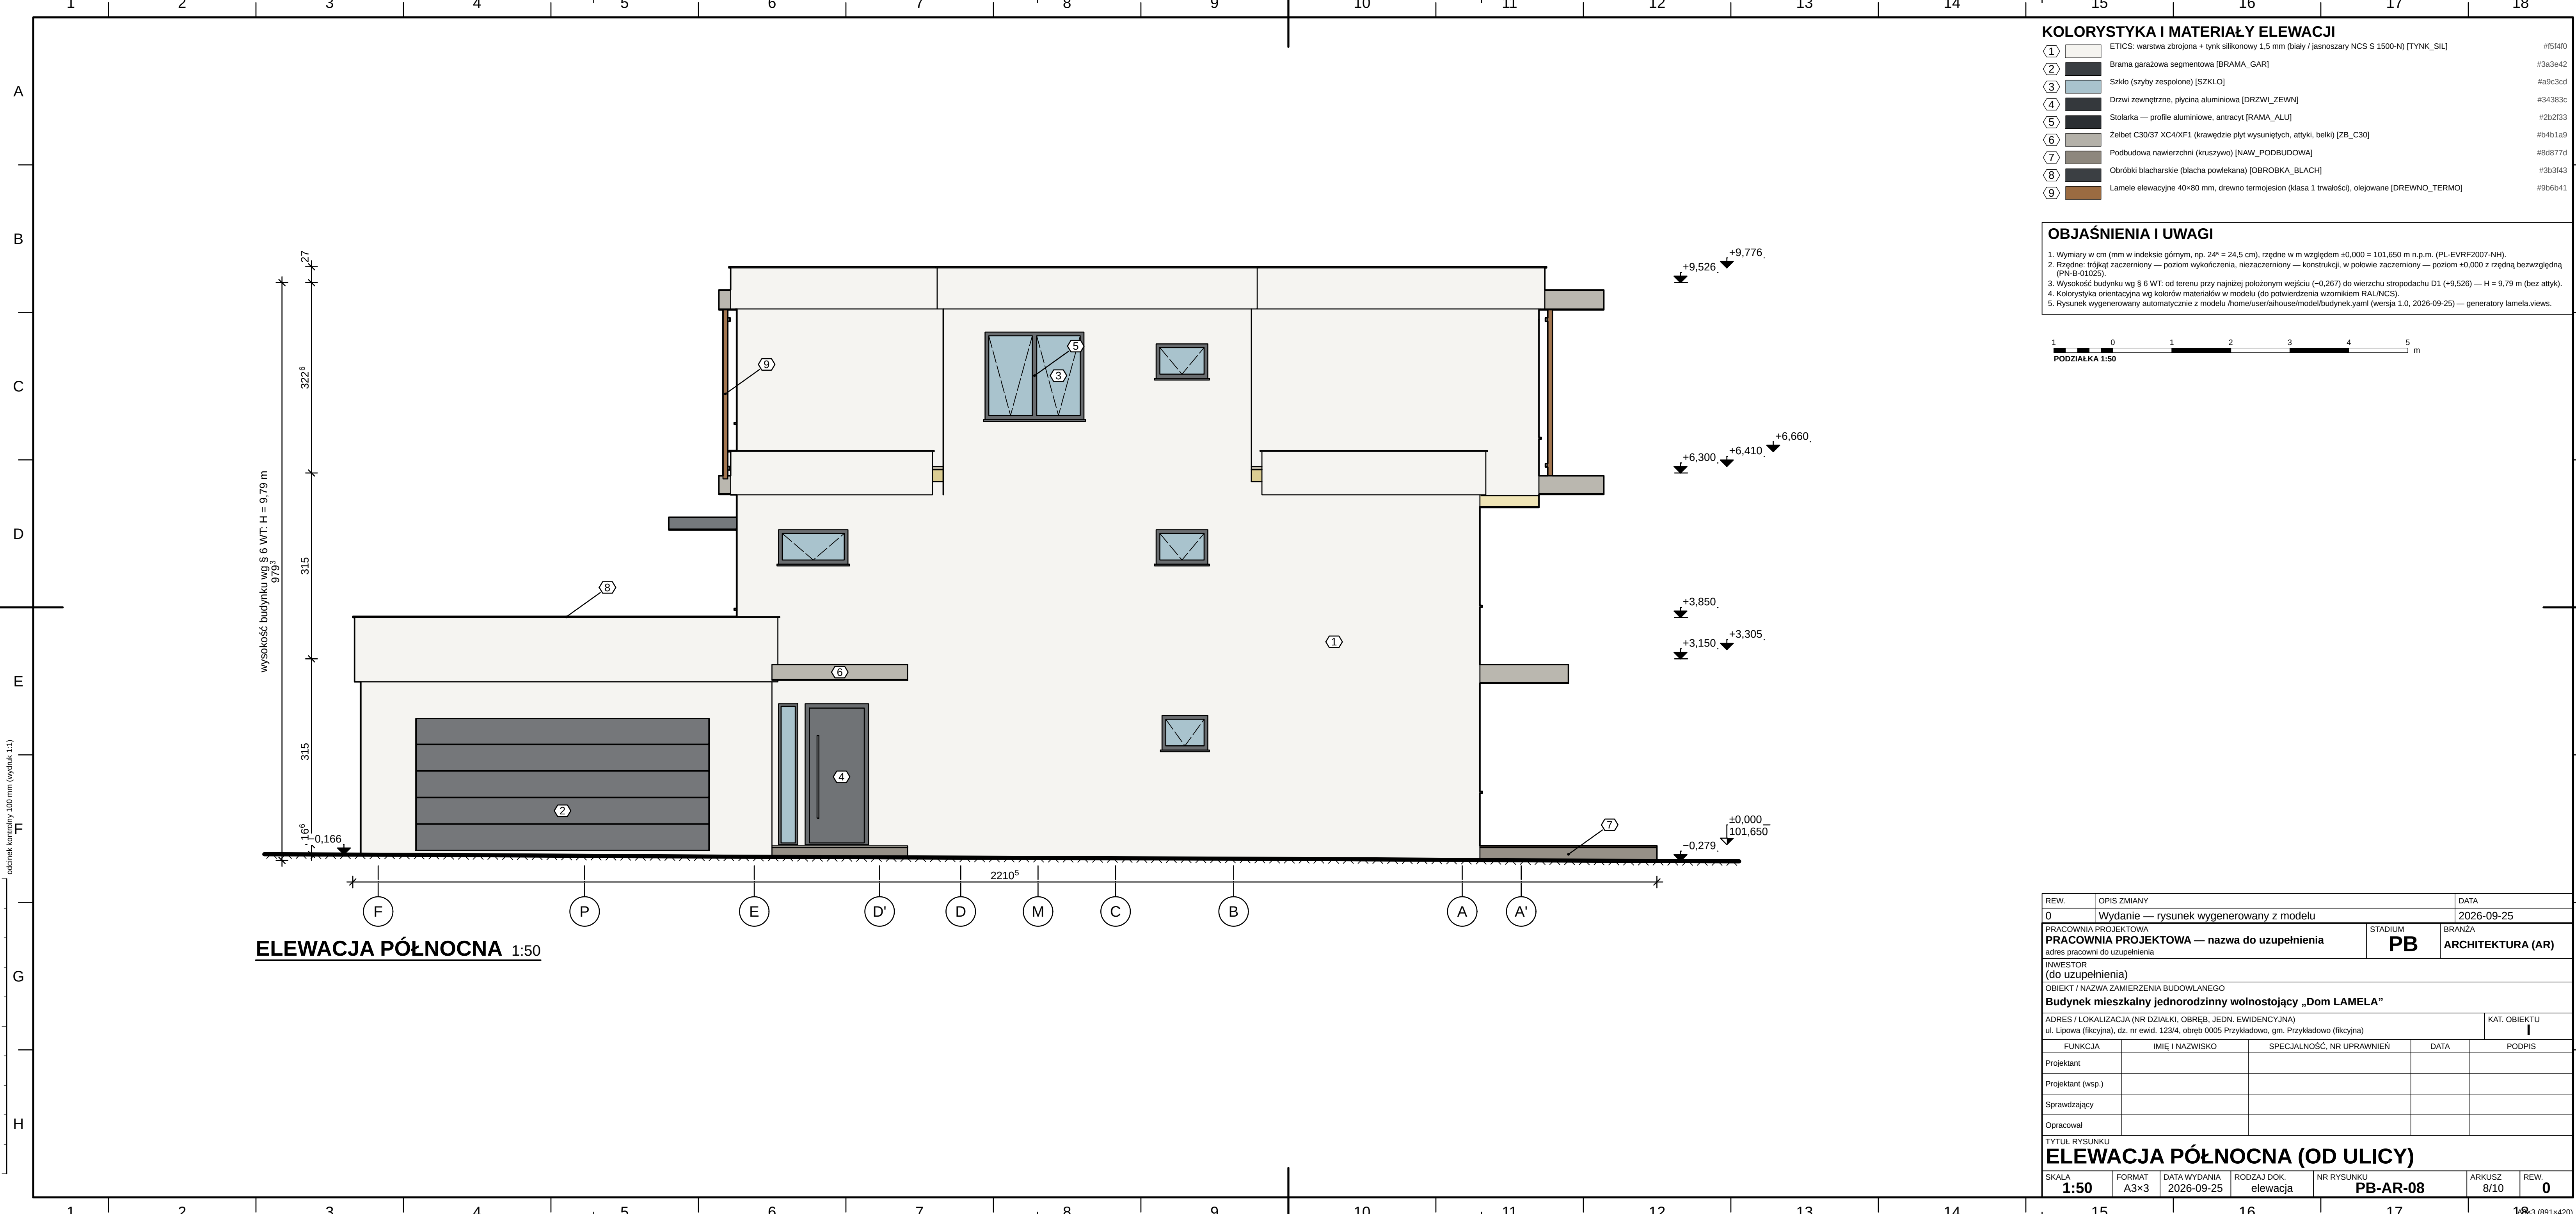

KOLORYSTYKA I MATERIAŁY ELEWACJI

1	ETICS: warstwa zbrojona + tynk silikonowy 1.5 mm (biały / jasnoszary NCS S 1500-N) [TYNK_SIL]	#f5f4f0
2	Brama garażowa segmentowa [BRAMA_GAR]	#3a3e42
3	Szkoło (szyby zespolone) [SZKLO]	#a9c3cd
4	Drzwi zewnętrzne, płycina aluminiowa [DRZWI_ZEWN]	#34383c
5	Stołarka — profile aluminiowe, antracyt [RAMA_ALU]	#2b2f33
6	Żelbet C30/37 XC4/XP1 (krawędzie płyt wysuniętych, attyki, belki) [ZB_C30]	#b4b1a9
7	Podbudowa nawierzchni (kruszywo) [NAW_PODBUDOWA]	#8d877d
8	Otróbbki blacharskie (blacha powlekana) [OBROBKA_BLACH]	#3b3f43
9	Lamele elewacyjne 40×80 mm, drewno termojesion (klasa 1 trwałości), olejowane [DREWNO_TERMO]	#9b6b41

OBJAŚNIENIA I UWAGI

- Wymiary w cm (mm w indeksie górnym, np. 24⁶ = 24,5 cm), rzędne w m względem ±0.000 = 101,650 m n.p.m. (PL-EVRF2007-NH).
- Rzędne: trójkąt zaczerpiony — poziom wykończenia, niezaczerpiony — konstrukcji, w połowie zaczerpiony — poziom ±0.000 z rzędną bezwzględną (PN-B-01025).
- Wysokość budynku wg § 6 WT: od terenu przy najniżej położonym wejściu (−0.267) do wierzchu stropodachu D1 (+9.526) — H = 9.79 m (bez attyki).
- Kolorystyka orientacyjna wg kolorów materiałów w modelu (do potwierdzenia wzornikiem RALNCS).
- Rysunek wygenerowany automatycznie z modelu /home/user/ai/house/model/budynek.yaml (wersja 1.0, 2026-09-25) — generatory lamela.views.

1 0 1 2 3 4 5 m
PODZIAŁKA 1:50

REW.	OPIS ZMIANY				DATA		
0	Wydanie — rysunek wygenerowany z modelu				2026-09-25		
PRACOWNIA PROJEKTOWA PRACOWNIA PROJEKTOWA — nazwa do uzupełnienia adres pracowni do uzupełnienia				STADIUM PB	BRANZA ARCHITEKTURA (AR)		
INWESTOR (do uzupełnienia)							
OBIEKT / NAZWA ZAMIERZENIA BUDOWLANEGO							
Budynek mieszkalny jednorodzinny wolnostojący „Dom LAMELA”							
ADRES / LOKALIZACJA (NR DZIAŁKI, OBREB, JEDN. EWIDENCYJNA) ul. Lipowa (fikcyjna), dz. nr ewid. 123/4, obręb 0005 Przykładowo, gm. Przykładowo (fikcyjna)					KAT. OBIEKTU I		
FUNKCJA		IMIĘ I NAZWISKO		SPECJALNOŚĆ, NR UPRAWNIENI		DATA	PODPIS
Projektant							
Projektant (wsp.)							
Sprawdzający							
Opracował							
TYTUŁ RYSUNKU							
ELEWACJA PÓŁNOCNA (OD ULICY)							
SKALA 1:50	FORMAT A3×3	DATA WYDANIA 2026-09-25	RODZAJ DOK. elewacja	NR RYSUNKU PB-AR-08		ARKUSZ 8/10	REW. 0

