


OZNACZENIA NA RYSUNKU


- pręt reprezentatywny grupy (warstwa górna), linia gruba
- pręt z odgięciem 90° — odgięcie (ramię) pokazane w płaszczyźnie rysunku
- linia rozkładu prętów grupy (zasieg), kółko — pręt reprezentatywny
- numer pozycji pręta (zestawienie stali)
- strefa zbrojenia narożnego (0,2·l_min) — pręty górą i dołem w 2 kierunkach
- ściany / belki / słupy pod płytą (widok zasłonięty)
- łącznik termoizolacyjny (ETA) — pręty wspornika przez izolację

OBJAŚNIENIA I UWAGI

1. Wymiary w cm (mm w indeksie górnym, np. 24⁵ = 24,5 cm), rzędne w m względem ±0,000 = 101,650 m n.p.m. (PL-EVRF2007-NH).
2. Zestawienie stali, strefy zbrojenia narożnego/na ścinanie i dozbrojenia — arkusz PT-BQ-14.
3. Strefy Z...: strzemiona zamknięte Ø8 obejmujące pręty dolne i górne (kształt 51), rozstaw podłużny wg tabeli, poprzeczny ≤ 1.5d (9.3.2(5)); pierwsze strzemie ≤ 0.5d od lica podpory; V_Ed — reakcja podpory uśredniona na 1,0 m (osobliwości MES płyty na końcach podpór) [ZaŁ].
4. Stal zbrojeniowa B500SP (klasa ciągliwości C, f_yk = 500 MPa) wg PN-H-93220:2018-02 / PN-EN 10080; pręty gięte na zimno na trzpieniach Ø_m ≥ 4φ (φ ≤ 16 mm) i ≥ 7φ (φ > 16 mm) — PN-EN 1992-1-1 tabl. 8.1N; oznaczenia prętów i kształtów wg PN-EN ISO 3766 (liczba, nr pozycji, Ø, rozstaw [cm], długość rozwinięcia l [cm]).
5. Otuliny zapewnić podkładkami dystansowymi (rozstaw ≤ 1,0 m, dla siatek górnych — podpórki „kobyłki” ≤ 1,0 m) — PN-EN 13670 p. 6.5; odchyłka wykonawcza Δc_dev = 10 mm uwzględniona w c_nom (PN-EN 1992-1-1 4.4.1.3 + NA).
6. Pręty łączyć na zakład l_v (tabela w stopce zestawienia), styki mijankowo — w jednym przekroju ≤ 50 % prętów; odstęp w świetle prętów ≥ max(φ; d_g + 5 mm; 20 mm) — PN-EN 1992-1-1 8.2(2), 8.7.2; pręty dolne w strefie podpory zakotwić ≥ 10φ za licem (9.3.1.2(1) → 9.2.1.5).
7. Betonowanie: beton wg PN-EN 206+A2 i PN-B-06265 (klasa, ekspozycja, D_max 16 mm, konsystencja S3); pielęgnacja ≥ 7 dni (klasa pielęgnacji 2 — PN-EN 13670 p. 8.5); przerwy robocze wyłącznie w miejscach uzgodnionych z projektantem.
8. Rozszalowanie i usunięcie podpór: płyty i belki po uzyskaniu ≥ 70 % f_ck (PN-EN 13670 p. 5.6 i 8.5), wsporniki — nie wcześniej niż po 28 dniach i po wykonaniu elementów dociążających zaplecze; podpory wtórne do 28 dni.
9. Zbrojenie wynika z obliczeń statycznych (projekt/04_PT_konstrukcja/obliczenia, numeracja pozycji jak na rysunku); kontrola A_s,prov ≥ A_s,req — raport kontrola_zbrojenia.md. Pozycje z niespełnionymi warunkami nośności (wynik „NIE” w raporcie) wymagają zmian przed wydaniem do realizacji.
10. Warstwa górna: pręty nad podporami — 0,3·l przesa za osią podpory (≥ l_bd), przy krawędzi płyty z odgięciem w wiercu (ramię = h – 2c); wsporniki — od krawędzi swobodnej przez łącznik termoizolacyjny do przesa zaplecza na max(l_c; l_bd) za podporą (PN-EN 1992-1-1 9.3.1.2(2), 9.3.1.4).
11. Rysunek wygenerowany automatycznie z modelu model/budynek.yaml (wersja 1.0, 2026-09-25) — generatory lamela.views.

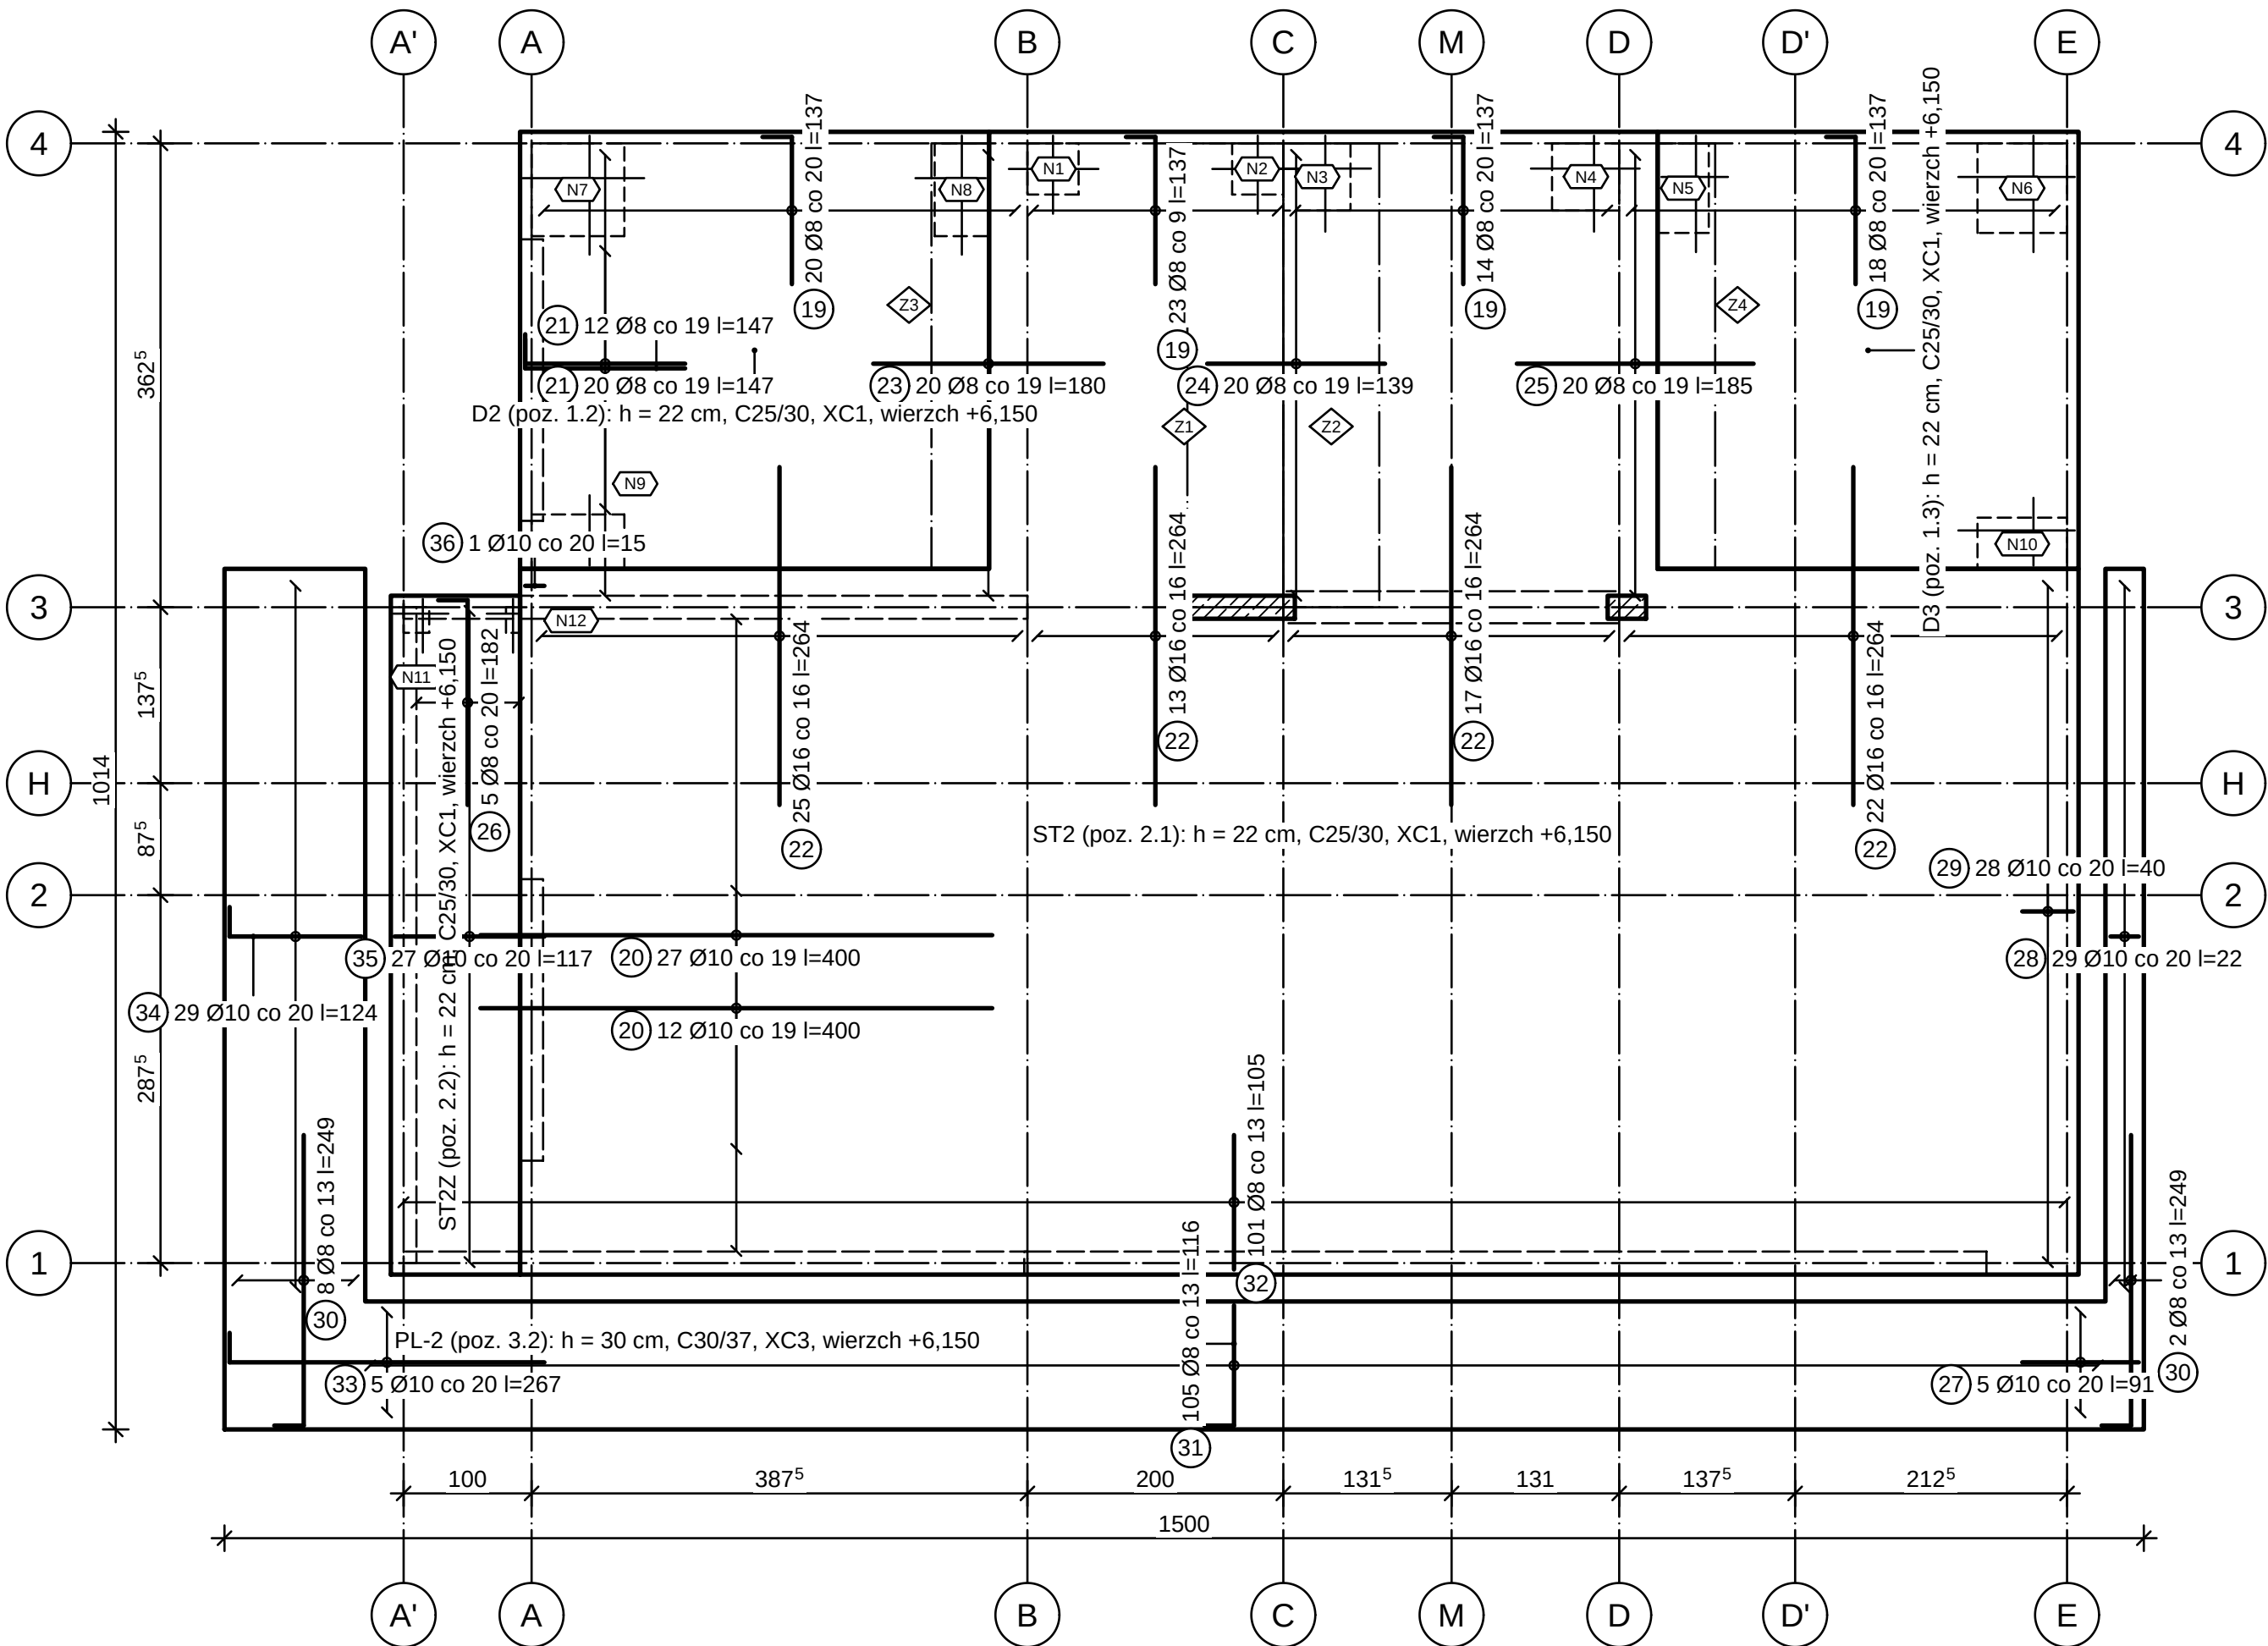

ZBROJENIE GÓRNE PŁYT ST2, ST2Z, D2, D3, PL-2 1:50

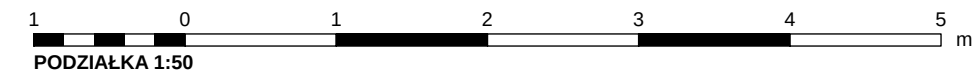

REW.	OPIS ZMIANY			DATA	
0	Wydanie — rysunek wygenerowany z modelu			2026-09-25	
PRACOWNIA PROJEKTOWA PRACOWNIA PROJEKTOWA — nazwa do uzupełnienia adres pracowni do uzupełnienia			STADIUM PT	BRANŻA KONSTRUKCJA (BO)	
INWESTOR (do uzupełnienia)					
OBIEKT / NAZWA ZAMIERZENIA BUDOWLANEGO Budynek mieszkalny jednorodzinny wolnostojący „Dom LAMELA”					
ADRES / LOKALIZACJA (NR DZIAŁKI, OBRĘB, JEDN. EWIDENCYJNA) ul. Lipowa (fikcyjna), dz. nr ewid. 123/4, obręb 0005 Przykładowo, gm. Przykładowo (fikcyjna)					KAT. OBIEKTU I
FUNKCJA		IMIĘ I NAZWISKO	SPECJALNOŚĆ, NR UPRAWNIENI	DATA	PODPIS
Projektant		[DO UZUPEŁNIENIA]	[DO UZUPEŁNIENIA]		
Projektant (wsp.)		[DO UZUPEŁNIENIA]	[DO UZUPEŁNIENIA]		
Sprawdzający		nie dotyczy (art. 20 ust. 3 pkt 2 PB)	—		
Opracował		[DO UZUPEŁNIENIA]	[DO UZUPEŁNIENIA]		
TYTUŁ RYSUNKU ZBROJENIE GÓRNE STROPU NAD I PIĘTREM					
SKALA 1:50	FORMAT 400×594	DATA WYDANIA 2026-09-25	RODZAJ DOK. rysunek zbrojenia	NR RYSUNKU PT-BO-13	ARKUSZ 13/27
					REW. 0