



Strop międzykondygnacyjny
Deska warstwowa dębowa 15 mm, klejona 1,5 cm
Jastrych cementowy CT-C25-F5 z węzownicą ogrzewania podłogowego 6,5 cm
Styropian podłogowy EPS 100-038 (pod jastrychem) 4 cm
Styropian elastyfikowany EPS T (akustyczny, pod jastrychem) 3 cm

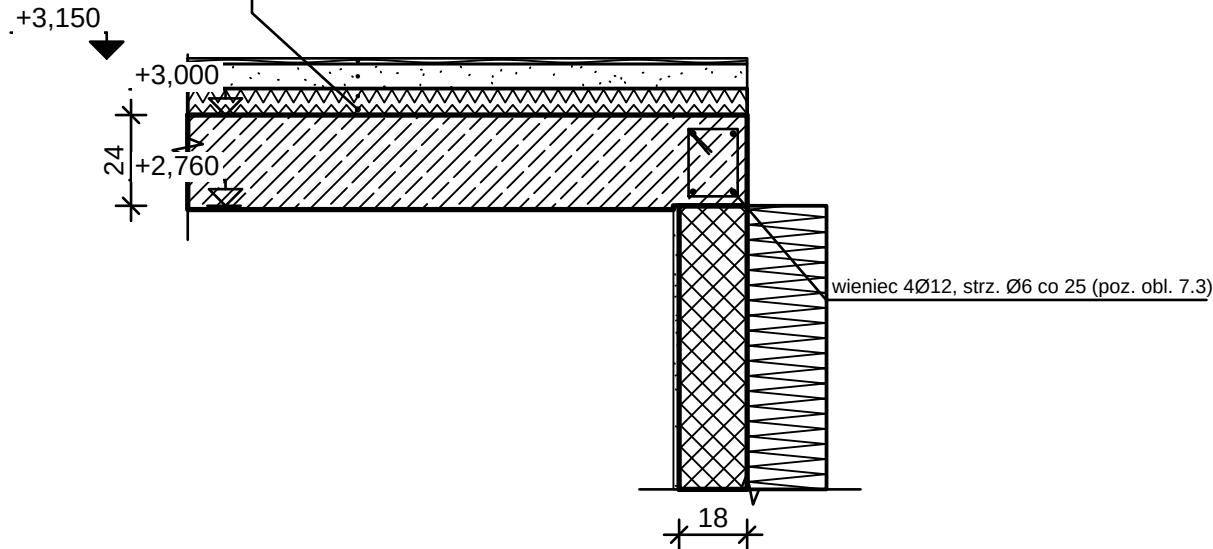

WIENIEC — KRAWĘDŹ STROPU D4 NA ŚCIANIE S0-03 1:20


Strop międzykondygnacyjny
Deska warstwowa dębowa 15 mm, klejona 1,5 cm
Jastrych cementowy CT-C25-F5 z węzownicą ogrzewania podłogowego 6,5 cm
Styropian podłogowy EPS 100-038 (pod jastrychem) 4 cm
Styropian elastyfikowany EPS T (akustyczny, pod jastrychem) 3 cm

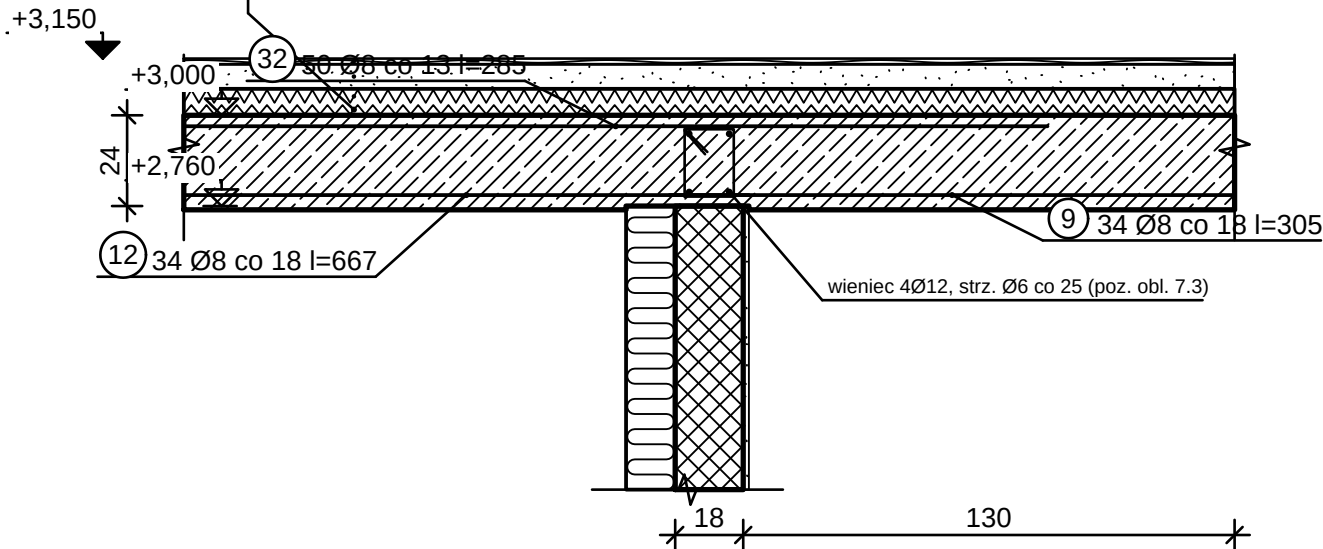

OPARCIE STROPU D4 NA ŚCIANIE S0-17 1:20

OBJAŚNIENIA I UWAGI

- Wymiary w cm (mm w indeksie górnym, np. 24⁵ = 24,5 cm), rzędne w m względem ±0,000 = 101,650 m n.p.m. (PL-EVRF2007-NH).
- Węzły stropów: warstwy wg przegród z modelu; zbrojenie — numery pozycji jak na arkuszach zbrojenia płyt poziomym (warstwa dolna/górna); wieniec wg pozycji obliczeniowej wieńców.
- Otuliny (c_{nom}) — wg klasy ekspozycji elementów (PN-EN 1992-1-1 tabl. 4.4N + NA, Δc_{dev} = 10 mm); podkładki dystansowe wg PN-EN 13670.
- Stal B500SP (PN-H-93220), beton wg arkuszy zbrojenia; oznaczenia prętów wg PN-EN ISO 3766.
- Rysunek wygenerowany automatycznie z modelu model/budynek.yaml (wersja 1.0, 2026-09-25) — generatory lamela.views.

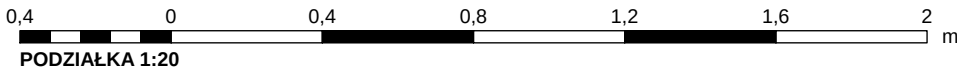

REW.	OPIS ZMIANY			DATA	
0	Wydanie — rysunek wygenerowany z modelu			2026-09-25	
PRACOWNIA PROJEKTOWA PRACOWNIA PROJEKTOWA — nazwa do uzupełnienia adres pracowni do uzupełnienia			STADIUM PT	BRANŻA KONSTRUKCJA (BO)	
INWESTOR (do uzupełnienia)					
OBIEKT / NAZWA ZAMIERZENIA BUDOWLANEGO Budynek mieszkalny jednorodzinny wolnostojący „Dom LAMELA”					
ADRES / LOKALIZACJA (NR DZIAŁKI, OBRĘB, JEDN. EWIDENCYJNA) ul. Lipowa (fikcyjna), dz. nr ewid. 123/4, obręb 0005 Przykładowo, gm. Przykładowo (fikcyjna)				KAT. OBIEKTU I	
FUNKCJA	IMIĘ I NAZWISKO	SPECJALNOŚĆ, NR UPRAWNIEŃ		DATA	PODPIS
Projektant	[DO UZUPEŁNIENIA]	[DO UZUPEŁNIENIA]			
Projektant (wsp.)	[DO UZUPEŁNIENIA]	[DO UZUPEŁNIENIA]			
Sprawdzający	nie dotyczy (art. 20 ust. 3 pkt 2 PB)	—			
Opracował	[DO UZUPEŁNIENIA]	[DO UZUPEŁNIENIA]			
TYTUŁ RYSUNKU WIENIEC I OPARCIE STROPU NA MURZE SILIKATOWYM					
SKALA 1:20	FORMAT 470×297	DATA WYDANIA 2026-09-25	RODZAJ DOK. przekrój konstrukcyjny	NR RYSUNKU PT-BO-19	ARKUSZ 19/27
					REW. 0