


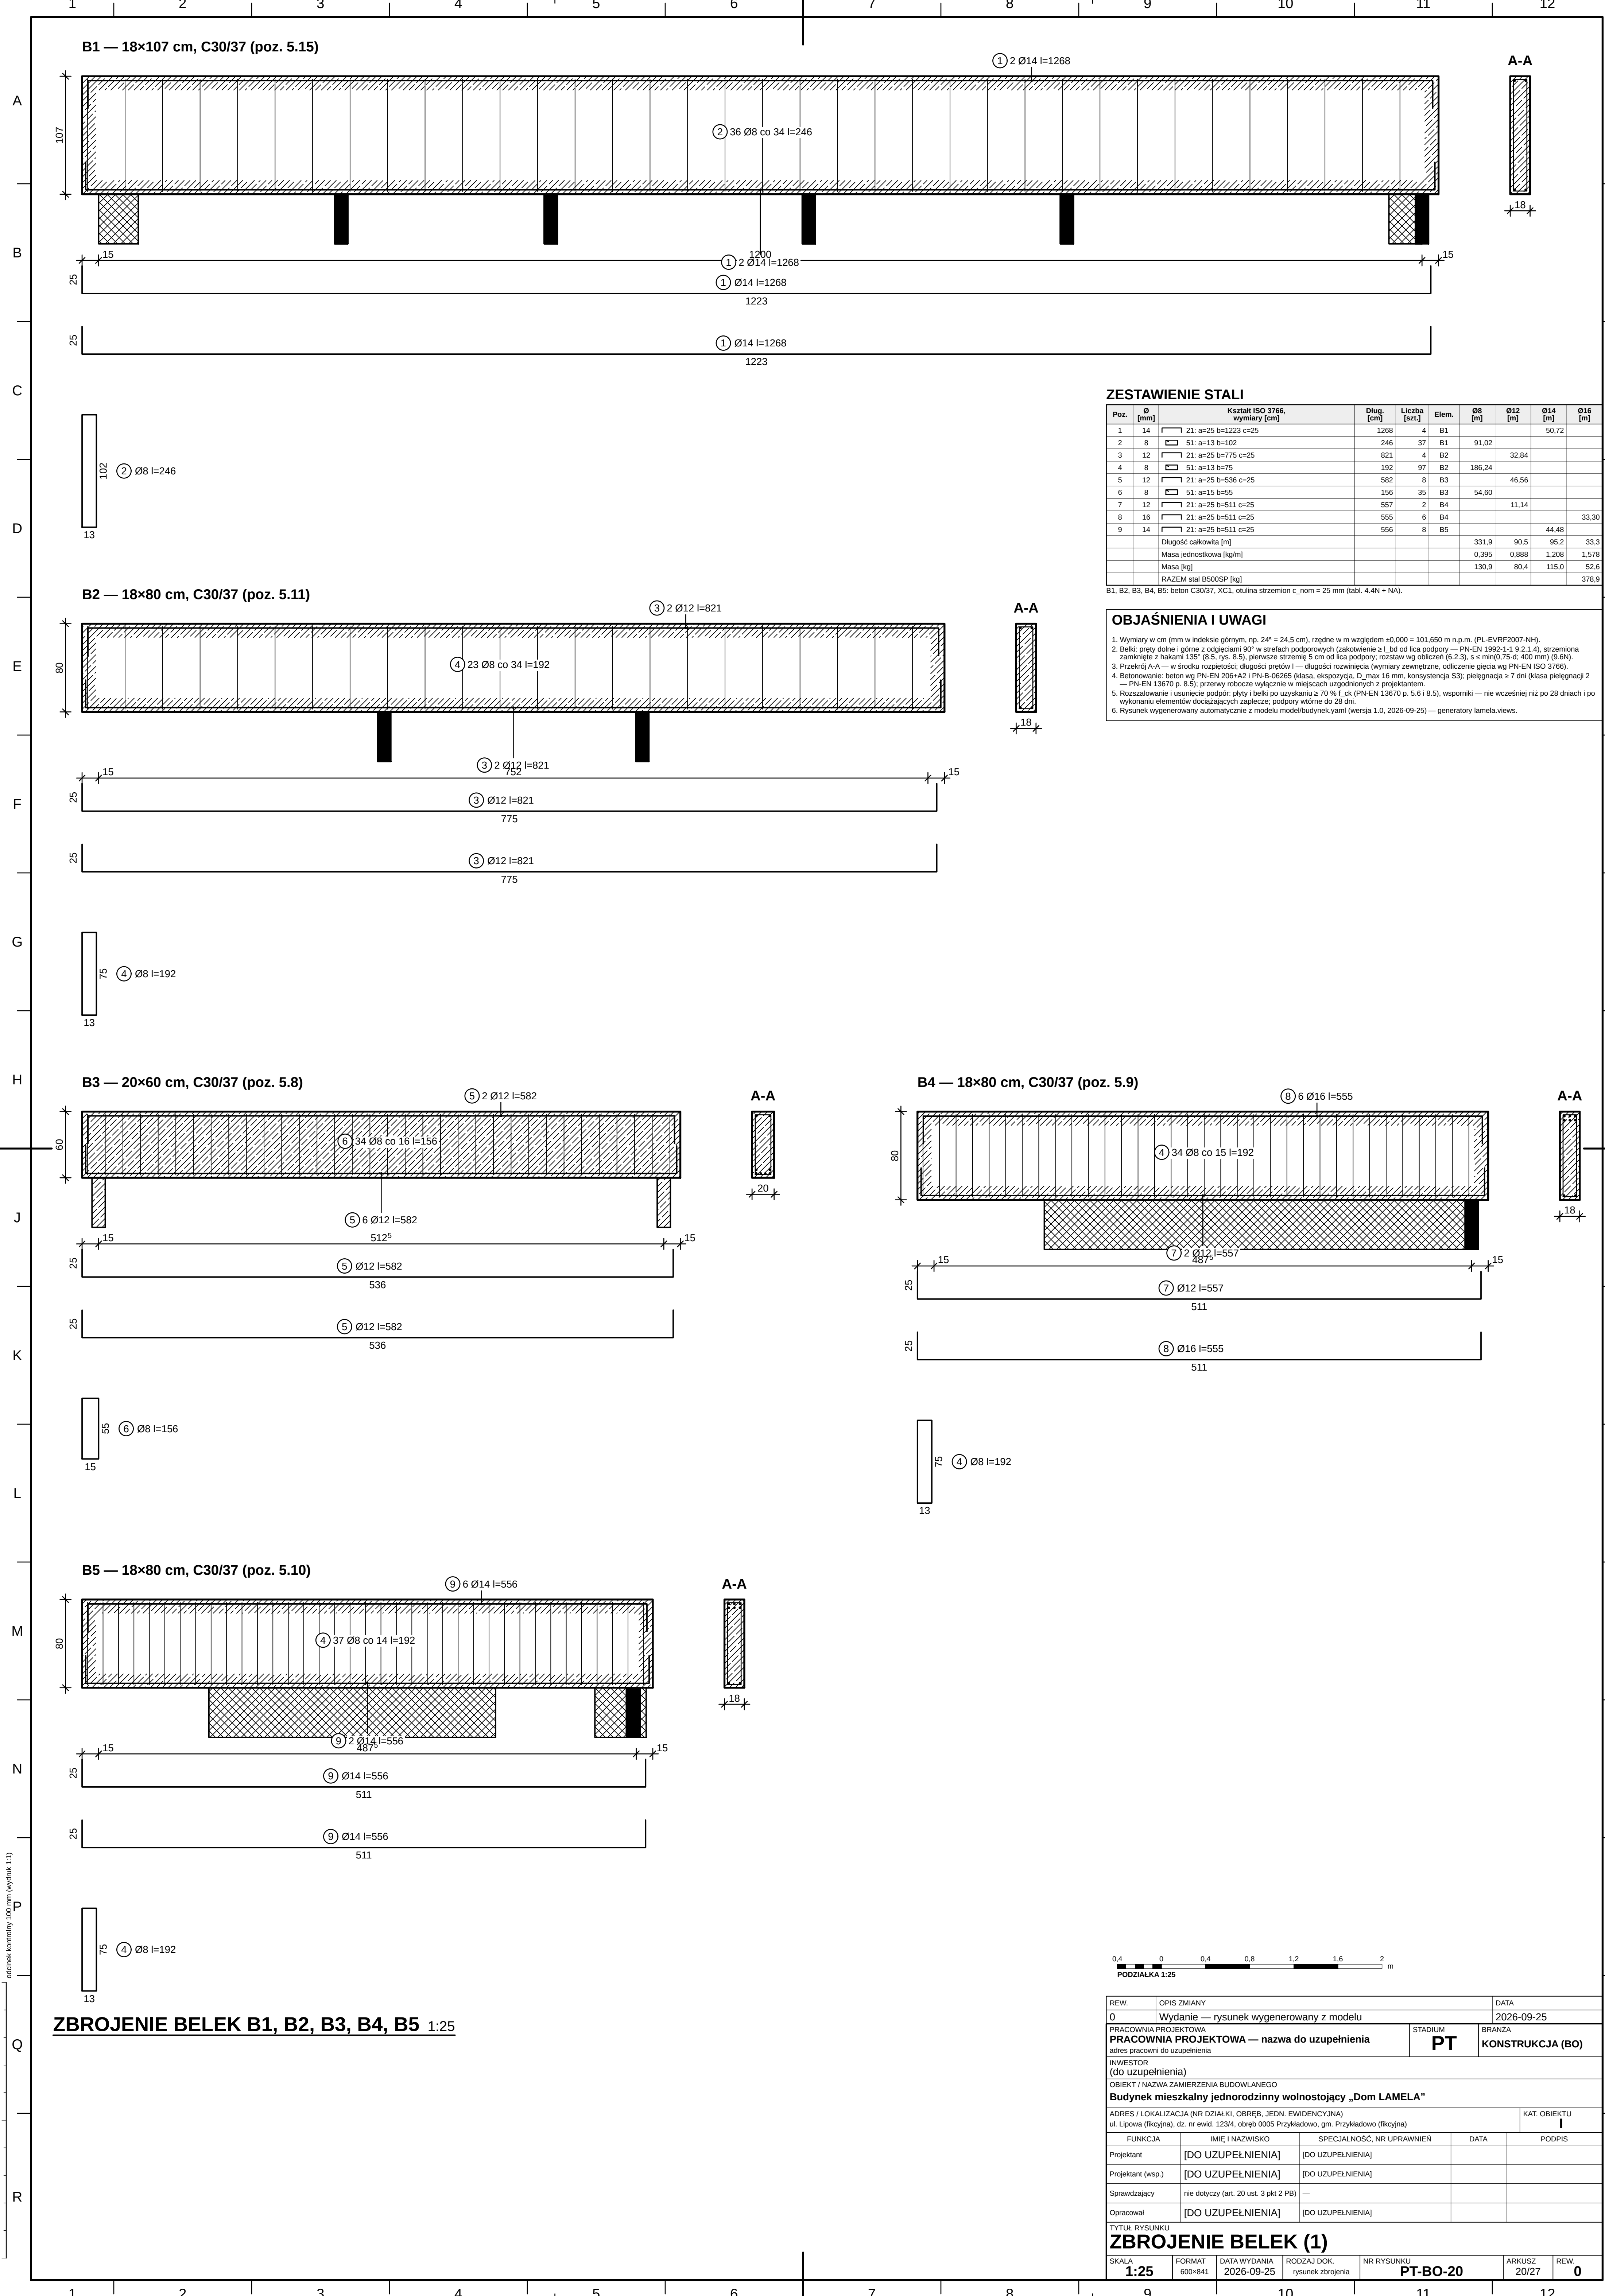

ZESTAWIENIE STALI											
Poz.	Ø [mm]	Kształt ISO 3766, wymiary [cm]	Dług. [cm]	Liczba [szt.]	Elem.	Ø8 [m]	Ø12 [m]	Ø14 [m]	Ø16 [m]		
1	14	21: a=25 b=1223 c=25	1268	4	B1			50,72			
2	8	51: a=13 b=102	246	37	B1	91,02					
3	12	21: a=25 b=775 c=25	821	4	B2		32,84				
4	8	51: a=13 b=75	192	97	B2	186,24					
5	12	21: a=25 b=536 c=25	582	8	B3		46,56				
6	8	51: a=15 b=55	156	35	B3	54,60					
7	12	21: a=25 b=511 c=25	557	2	B4		11,14				
8	16	21: a=25 b=511 c=25	555	6	B4						
9	14	21: a=25 b=511 c=25	556	8	B5			44,48			
Długość całkowita [m]						331,9	90,5	95,2	33,3		
Masa jednostkowa [kg/m]						0,395	0,888	1,208	1,578		
Masa [kg]						130,9	80,4	115,0	52,6		
RAZEM stal B500SP [kg]									378,9		

B1, B2, B3, B4, B5: beton C30/37, XC1, otulina strzemiem c_nom = 25 mm (tabl. 4.4N + NA).

OBJAŚNIENIA I UWAGI

1. Wymiary w cm (mm w indeksie górnym, np. 24^h = 24,5 cm), rzędne w m względem ±0,000 = 101,650 m n.p.m. (PL-EVRF2007-NH).


2. Belki: pręty dolne i górne z odjęciami 90° w strefach podporowych (zakotwienie ≥ 1,1d od łoża podpory — PN-EN 1992-1-1 § 2.1.4), strzemiona zamknięte z hakami 135° (8.5, rys. 8.5), pierwsze strzemie 5 cm od łoża podpory; rozstaw wg obliczeń (6.2.3), s ≤ min(0,75·d; 400 mm) (9.6N).

3. Przekrój A-A — w środku rozpiętości; długości prętów l — długości rozwinięcia (wymiary zewnętrzne, odliczenie gięcia wg PN-EN ISO 3766).

4. Betonowanie: beton wg PN-EN 206-V2 i PN-8-06265 (klasa, ekspozycja, D, max 18 mm, konsystencja S3); pielęgnacja z 7 dni (klasa pielęgnacji 2 — PN-EN 13670 p. 8.5); przewazy robocze wyłącznie w miejscach uzgodnionych z projektantem.

5. Rozszalowanie i usunięcie podpór: płyty i belki po uzyskaniu ≥ 70 % f_{ck} (PN-EN 13670 p. 5.6 i 8.5), wspomniki — nie wcześniej niż po 28 dniach i po wykonaniu elementów docończających zaplecze; podpory wtórne do 28 dni.

6. Rysunek wygenerowany automatycznie z modelu modelbudynek.yam (wersja 1.0, 2025-09-25) — generatory lamela.views.

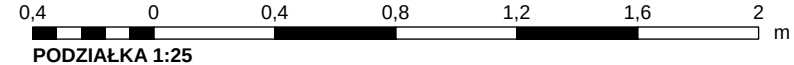

REW.	OPIS ZMIANY			DATA	
0	Wydanie — rysunek wygenerowany z modelu			2026-09-25	
PRACOWNIA PROJEKTOWA			STADIUM	BRANŻA	
PRACOWNIA PROJEKTOWA — nazwa do uzupełnienia			PT	KONSTRUKCJA (BO)	
adres pracowni do uzupełnienia					
INWESTOR (do uzupełnienia)					
OBIEKT / NAZWA ZAMIERZENIA BUDOWLANEGO					
Budynek mieszkalny jednorodzinny wolnostojący „Dom LAMELA”					
ADRES / LOKALIZACJA (NR DZIAŁKI, OBRĘB, JEDN. EWIDENCYJNA)				KAT. OBIEKTU	
ul. Lipowa (fikcyjna), dz. nr ewid. 123/4, obręb 0005 Przykładowo, gm. Przykładowo (fikcyjna)				I	
FUNKCJA		IMIĘ I NAZWISKO	SPECJALNOŚĆ, NR UPRAWNIEN	DATA	PODPIS
Projektant		[DO UZUPEŁNIENIA]	[DO UZUPEŁNIENIA]		
Projektant (wsp.)		[DO UZUPEŁNIENIA]	[DO UZUPEŁNIENIA]		
Sprawdzający		nie dotyczy (art. 20 ust. 3 pkt 2 PB)	—		
Opracował		[DO UZUPEŁNIENIA]	[DO UZUPEŁNIENIA]		
TYTUŁ RYSUNKU					
ZBROJENIE BELEK (1)					
SKALA	FORMAT	DATA WYDANIA	RODZAJ DOK.	NR RYSUNKU	ARKUSZ
1:25	600×841	2026-09-25	rysunek zbrojenia	PT-BO-20	20/27
					REW. 0

rodzinek kontroli 100 mm (wydruk 1:1)