

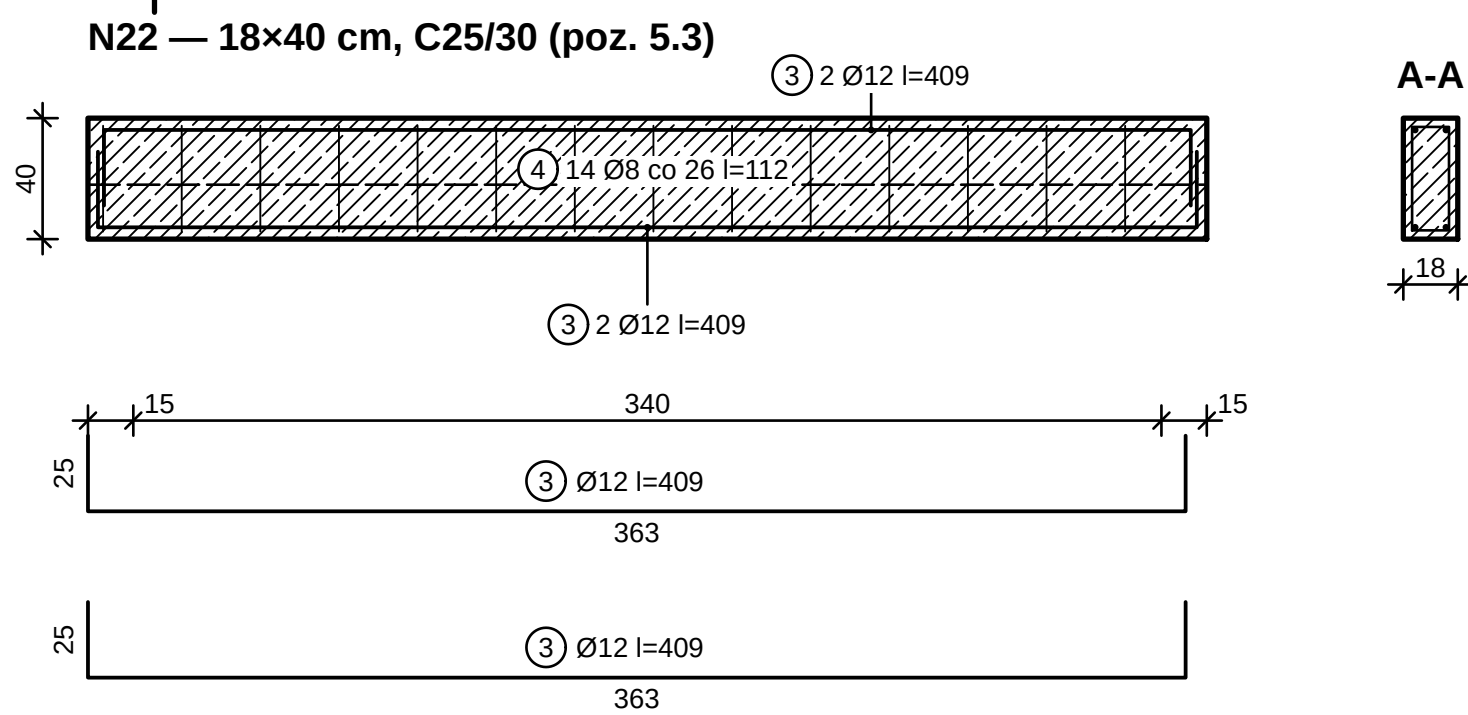
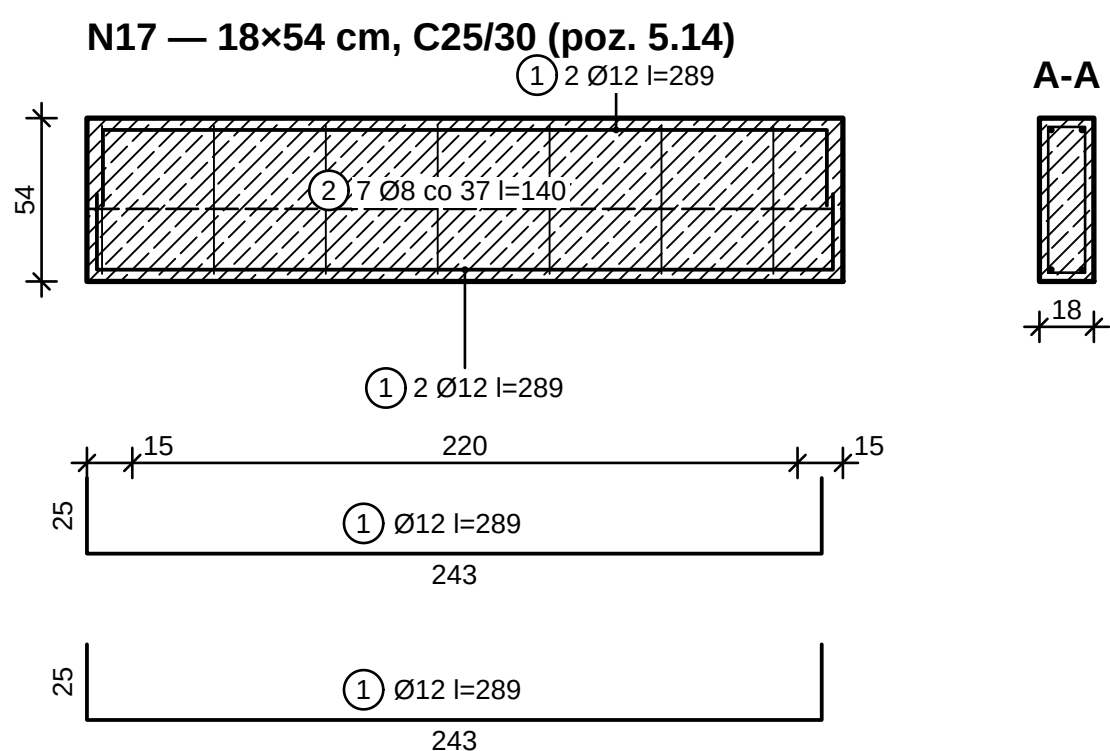
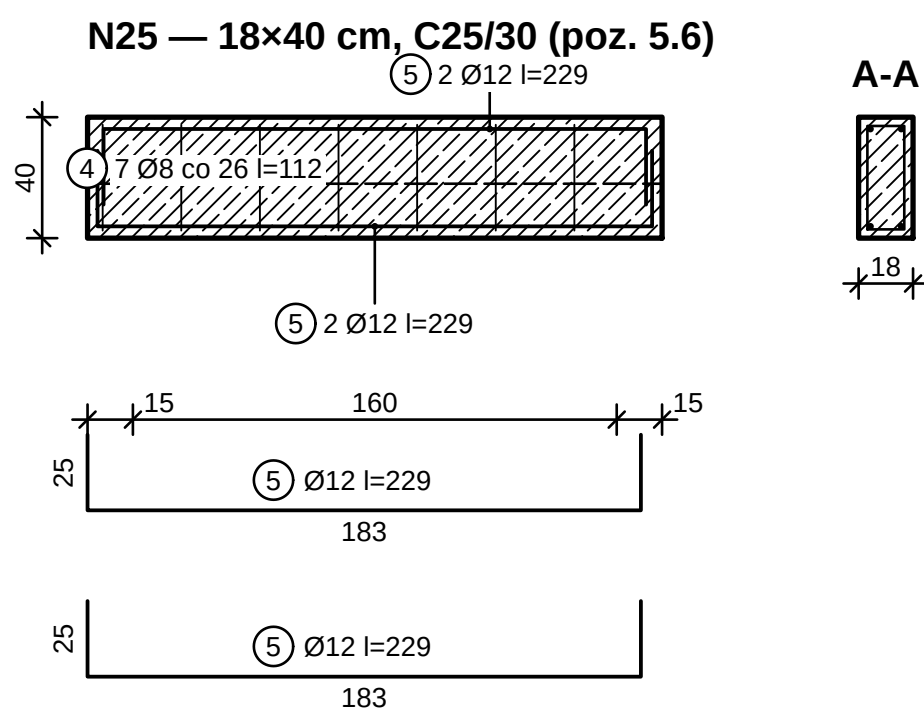
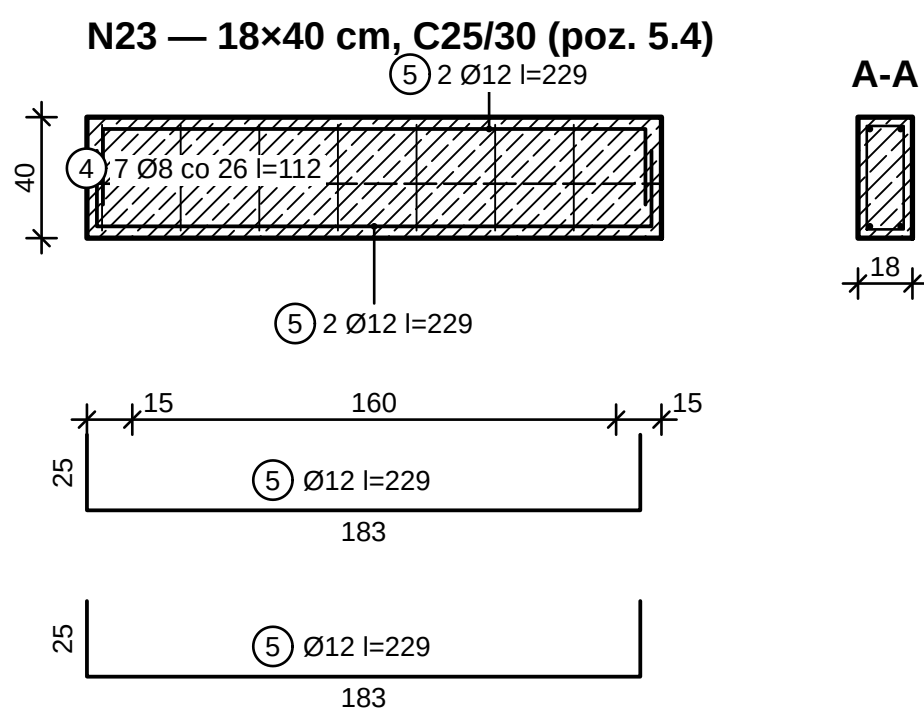


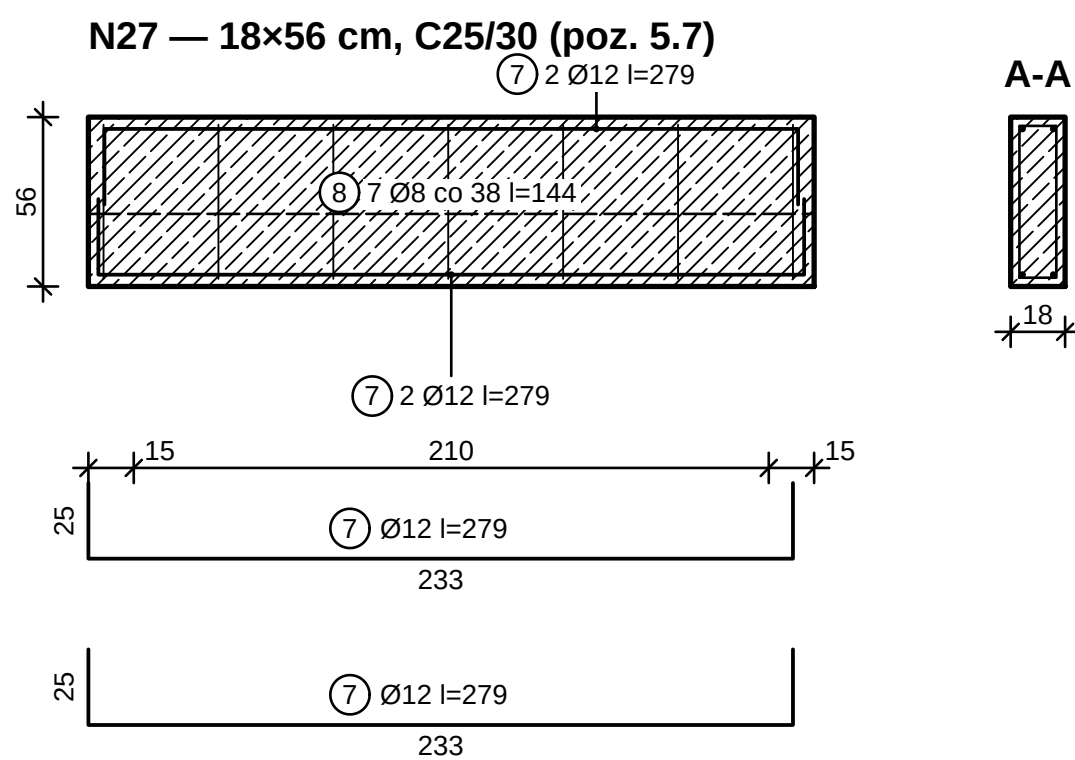

OBJAŚNIENIA I UWAGI

1. Wymiary w cm (mm w indeksie górnym, np. 24" = 24,5 cm), rzędne w m względem $\pm 0,000 \pm 101,650$ m n.p.m. (PL-EVPR2007-NH).
2. Belki: przędlone i górne z odciążeni ≥ 90 m strefach podporowych (zakotwienie ≥ 1 b.d na podporach – PN-EN 1992-1-1 9.2.1.4), strzemiona zamknięte z hakami 135° (8,5, rys. 8.5), pierwsze strzemie 5 cm od lica podpor; rozstaw wzdłuż belki (6.2.3), s $\leq \min(0,75; d)$ (400 mm) (3.6).
3. Przekrój A-A – w środku rozpiętości; długość przętów I – długość rozpięcia (wymiary zewnętrzne, odliczenie gęstości wg PN-EN ISO 9796).
4. Betonowanie: beton wg PN-EN 206-42 i PN-B-06265 (klasa, ekspozycja, $D_{\max}$ max 16 mm, konsystencja S3); pielęgnacja ≥ 7 dni (klasa pielęgnacji ≥ 1 – PN-EN 13670 p. 8.5); przewozy roboty wyłącznie w miejscach uzgodnionych z projektantem.

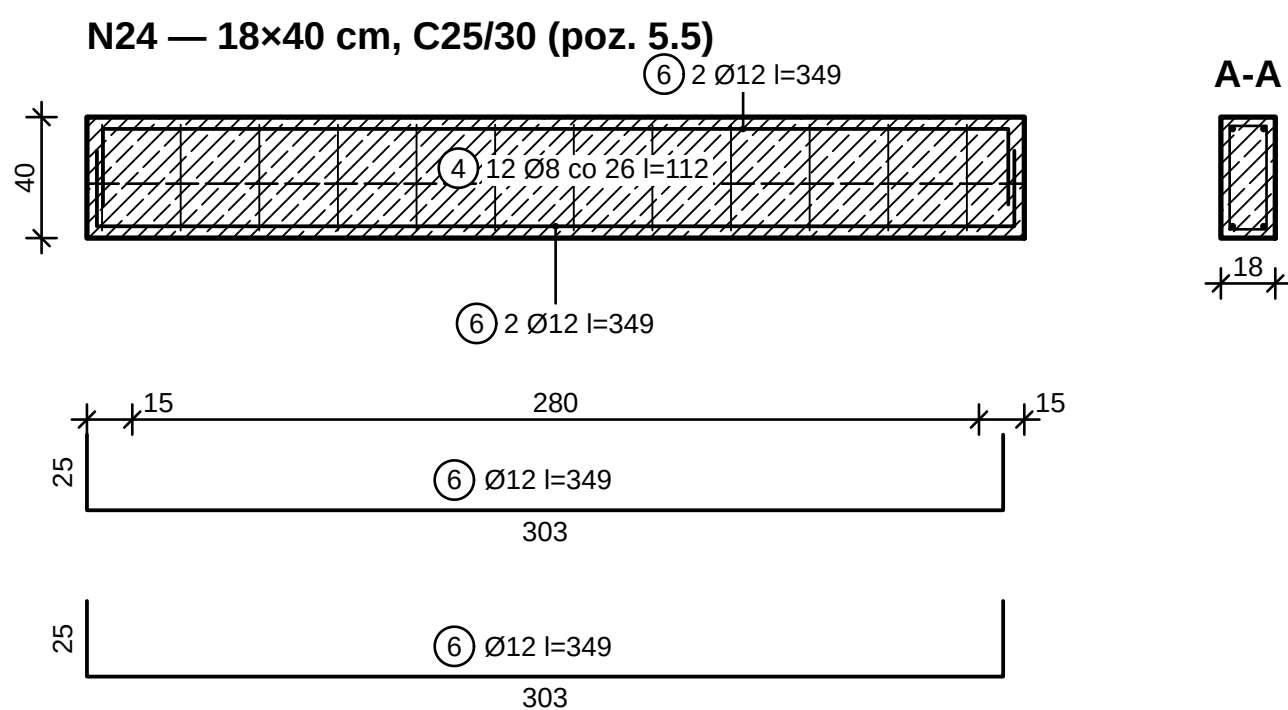

OBJAŚNIENIA I UWAGI (cd.)


5. Rozszalowanie i usunięcie podpór: płyty i belki po uzyskaniu $\geq 70\%$ f_{ck} (PN-EN 13670 p. 5.6 i 8.5), wsporniki — nie wcześniej niż po 28 dniach i po wykonaniu elementów dociągających zaplecze; podpory wtórne do 28 dni.
6. Rysunek wygenerowany automatycznie z modelu model/budynek.yaml (wersja 1.0, 2026-09-25) — generatory lamela.views.

ZBROJENIE BELEK N17, N22, N23, N24, N25, N27 1:25

ZESTAWIENIE STALI

Poz.	Ø [mm]	Kształt ISO 3766, wymiar [cm]	Dłg. [cm]	Liczba [szt.]	Elem.	Ø8 [m]	Ø12 [m]
1	12	 21: a=25 b=243 c=25	289	4	N17		11,56
2	8	 51: a=13 b=49	140	8	N17	11,20	
3	12	 21: a=25 b=363 c=25	409	4	N22		16,36
4	8	 51: a=13 b=35	112	44	N22	49,28	
5	12	 21: a=25 b=183 c=25	229	8	N23		18,32
6	12	 21: a=25 b=303 c=25	349	4	N24		13,96
7	12	 21: a=25 b=233 c=25	279	4	N27		11,16
8	8	 51: a=13 b=51	144	8	N27	11,52	
		Długość całkowita [m]				72,0	71,4
		Masa jednostkowa [kg/m]				0,395	0,888
		Masa [kg]				28,4	63,4
		RAZEM stal B500SP [kg]					91,8

N17, N22, N23, N24, N25, N27: beton C25/30, XC1, otulina strzemion c. nom = 25 mm (tabl. 4.4N + NA)

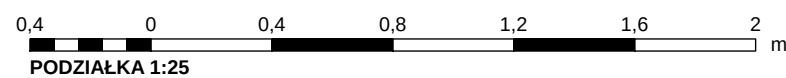

REW.	OPIS ZMIANY		DATA	
0	Wydanie — rysunek wygenerowany z modelu		2026-09-25	
PRACOWNIA PROJEKTOWA PRACOWNIA PROJEKTOWA — nazwa do uzupełnienia adres pracowni do uzupełnienia		STADIUM PT	BRANŻA KONSTRUKCJA (BO)	
INWESTOR (do uzupełnienia)				
OBIEKT / NAZWA ZAMIERZENIA BUDOWLANEGO Budynek mieszkalny jednorodzinny wolnostojący „Dom LAMELA”				
UL. / LOKALIZACJA (NR DZIAŁKI, OBRĘB, JEDN. EWIDENCYJNA) ad. Lipowa (fikcyjna), dz. nr ewid. 123/4, obręb 0005 Przykładowo, gm. Przykładowo (fikcyjna)			KAT. OBIEKTU I	
FUNKCJA	IMIĘ I NAZWISKO	SPECJALNOŚĆ, NR UPRAWNIENIEN	DATA	PODPIS
Projektant	[DO UZUPEŁNIENIA]	[DO UZUPEŁNIENIA]		
Projektant (wsp.)	[DO UZUPEŁNIENIA]	[DO UZUPEŁNIENIA]		
Sprawdzający	nie dotyczy (art. 20 ust. 3 pkt 2 PB)	—		
Opracował	[DO UZUPEŁNIENIA]	[DO UZUPEŁNIENIA]		
TYTUŁ RYSUNKU ZBROJENIE BELEK (3)				
SKALA 1:25	FORMAT 470×594	DATA WYDANIA 2026-09-25	RODZAJ DOK. rysunek zbrojenia	NR RYSUNKU PT-BO-22
ARKUSZ 22/27			REW. 0	