


NH — 18×25 cm, L = 1,50 m, C25/30

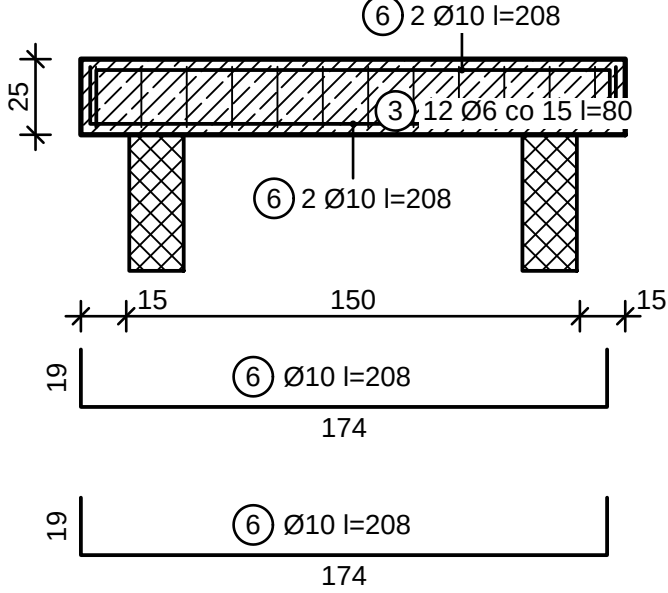


A-A



TYPY NADPROŻY — OTWORY I POZYCJE OBLICZEŃ

Typ	Otwory	Poz. obl.	Szt.
NE	O0-21	6.12	1
NF	O1-11	6.22	1
NG	O0-08	6.2	1
NH	O0-09	6.3	1

NG — 18×25 cm, L = 1,40 m, C25/30

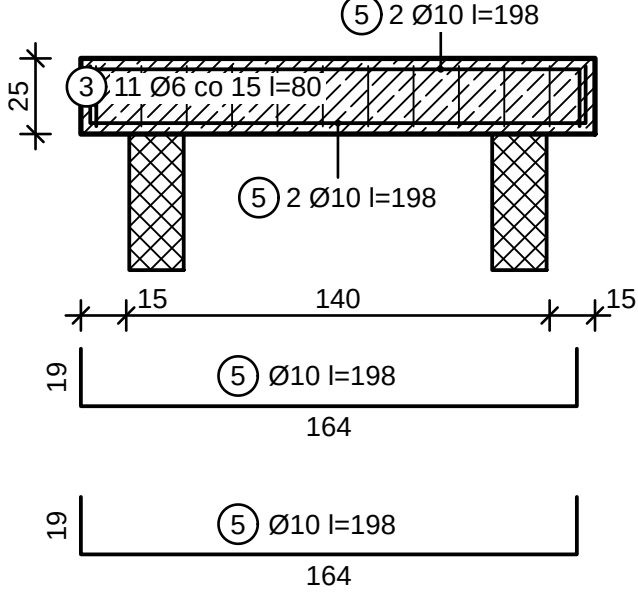

A-A




ZESTAWIENIE STALI

Poz.	Ø [mm]	Kształt ISO 3766, wymiary [cm]	Dług. [cm]	Liczba [szt.]	Elem.	Ø6 [m]	Ø10 [m]	Ø12 [m]	Ø14 [m]
1	12	21: a=19 b=154 c=19	188	2	N-O0-2			3,76	
2	10	21: a=19 b=154 c=19	188	4	N-O0-2		7,52		
3	6	51: a=13 b=20	80	48	N-O0-2	38,40			
4	14	21: a=19 b=154 c=19	187	2	N-O1-1				3,74
5	10	21: a=19 b=164 c=19	198	4	N-O0-0		7,92		
6	10	21: a=19 b=174 c=19	208	4	N-O0-0		8,32		
		Długość całkowita [m]				38,4	23,8	3,8	3,7
		Masa jednostkowa [kg/m]				0,222	0,617	0,888	1,208
		Masa [kg]				8,5	14,6	3,3	4,5
		RAZEM stal B500SP [kg]							31,0

O0-21, O1-11, O0-08, O0-09: beton C25/30, XC1, otulina strzemiem c_nom = 25 mm (tabl. 4.4N + NA).


NE — 18×25 cm, L = 1,30 m, C25/30

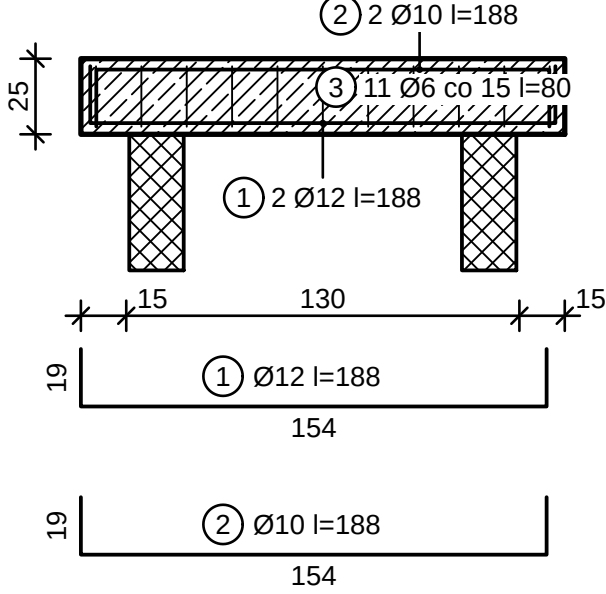



A-A



NF — 18×25 cm, L = 1,30 m, C25/30

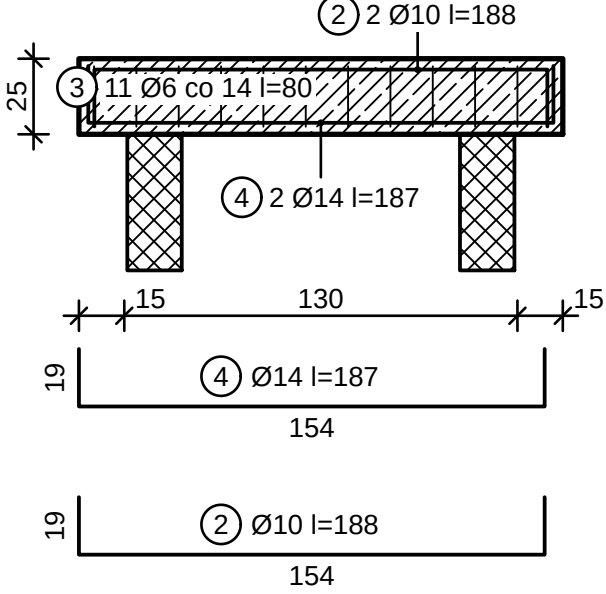


A-A

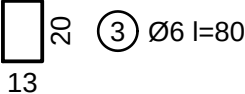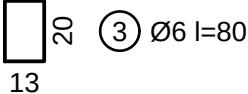

ZBROJENIE NADPROŻY NE, NF, NG, NH 1:25

OBJAŚNIENIA I UWAGI

- Wymiary w cm (mm w indeksie górnym, np. 24⁵ = 24,5 cm), rzędne w m względem ±0,000 = 101,650 m n.p.m. (PL-EVRF2007-NH).
- Belki: pręty dolne i górne z odgięciami 90° w strefach podporowych (zakotwienie ≥ l_{bd} od lica podpory — PN-EN 1992-1-1 9.2.1.4), strzemiona zamknięte z hakami 135° (8.5, rys. 8.5), pierwsze strzemie 5 cm od lica podpory; rozstaw wg obliczeń (6.2.3), s ≤ min(0,75·d; 400 mm) (9.6N).
- Przekrój A-A — w środku rozpiętości; długości prętów l — długości rozwinięcia (wymiary zewnętrzne, odliczenie gięcia wg PN-EN ISO 3766).
- Betonowanie: beton wg PN-EN 206+A2 i PN-B-06265 (klasa, ekspozycja, D_{max} 16 mm, konsystencja S3); pielęgnacja ≥ 7 dni (klasa pielęgnacji 2 — PN-EN 13670 p. 8.5); przerwy robocze wyłącznie w miejscach uzgodnionych z projektantem.
- Rozszalowanie i usunięcie podpór: płyty i belki po uzyskaniu ≥ 70 % f_{ck} (PN-EN 13670 p. 5.6 i 8.5), wsporniki — nie wcześniej niż po 28 dniach i po wykonaniu elementów dociążających zaplecze; podpory wtórne do 28 dni.
- Nadproża pogrupowano w typy (jednakowy przekrój, długość i zbrojenie z obliczeń); liczby sztuk w zestawieniu — łącznie dla wszystkich nadproży typu.
- Rysunek wygenerowany automatycznie z modelu model/budynek.yaml (wersja 1.0, 2026-09-25) — generatory lamela.views.

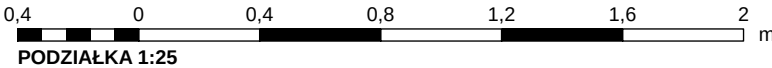

REW.	OPIS ZMIANY	DATA
0	Wydanie — rysunek wygenerowany z modelu	2026-09-25
PRACOWNIA PROJEKTOWA PRACOWNIA PROJEKTOWA — nazwa do uzupełnienia adres pracowni do uzupełnienia		STADIUM PT
INWESTOR (do uzupełnienia)		BRANŻA KONSTRUKCJA (BO)
OBIEKT / NAZWA ZAMIERZENIA BUDOWLANEGO Budynek mieszkalny jednorodzinny wolnostojący „Dom LAMELA”		
ADRES / LOKALIZACJA (NR DZIAŁKI, OBRĘB, JEDN. EWIDENCYJNA) ul. Lipowa (fikcyjna), dz. nr ewid. 123/4, obręb 0005 Przykładowo, gm. Przykładowo (fikcyjna)		KAT. OBIEKTU I
FUNKCJA	IMIĘ I NAZWISKO	SPECJALNOŚĆ, NR UPRAWNIENI
Projektant	[DO UZUPEŁNIENIA]	[DO UZUPEŁNIENIA]
Projektant (wsp.)	[DO UZUPEŁNIENIA]	[DO UZUPEŁNIENIA]
Sprawdzający	nie dotyczy (art. 20 ust. 3 pkt 2 PB)	—
Opracował	[DO UZUPEŁNIENIA]	[DO UZUPEŁNIENIA]
TYTUŁ RYSUNKU ZBROJENIE NADPROŻY (2)		
SKALA 1:25	FORMAT 330×594	DATA WYDANIA 2026-09-25
RODZAJ DOK. rysunek zbrojenia	NR RYSUNKU PT-BO-24	ARKUSZ 24/27
REW. 0		